
◆建築仕上表


室名	食堂　FL±0__CH=3000
床	ﾌﾛｰﾘﾝｸﾞ__構造用合板下地__一部ﾋﾞﾆﾙ床ﾀｲﾙ-B
巾木	H=40__木製小幅板
壁	せっこうﾎﾞｰﾄﾞ__ﾋﾞﾆﾙｸﾛｽ__軽量鉄骨下地
天井	ﾛｯｸｳｰﾙ化粧吸音板__天井用ﾒﾗﾐﾝ不燃化粧板
見切縁	ﾋﾞﾆﾙ製見切縁


《主な仕様・品番》

天板	杉積層(富山県産材)	[ｸﾘｱ]ﾛｰﾄｽ・ﾜﾝ(自然系撥水塗料)
ﾌﾞﾗｹｯﾄ	ｽﾁｰﾙFB_t9mm_錆止め塗装	仕上(SOP)は塗装工事
ﾌｯｸ	ｽﾃﾝﾚｽ　[LAMP]5HJU-60M	鏡面研磨

■ 全体はNo.02-1図・詳細はNo.02-3図・ﾍﾞﾝﾁはNo.03図参照
■ 天板連結部・見切り連結部はﾗﾐﾅ幅を揃える
■ 天板前端の傾斜角度はﾍﾞﾝﾁ背に合わせる
■ ﾍﾞﾝﾁ上のｶｳﾝﾀｰはﾍﾞﾝﾁと一体にして取付

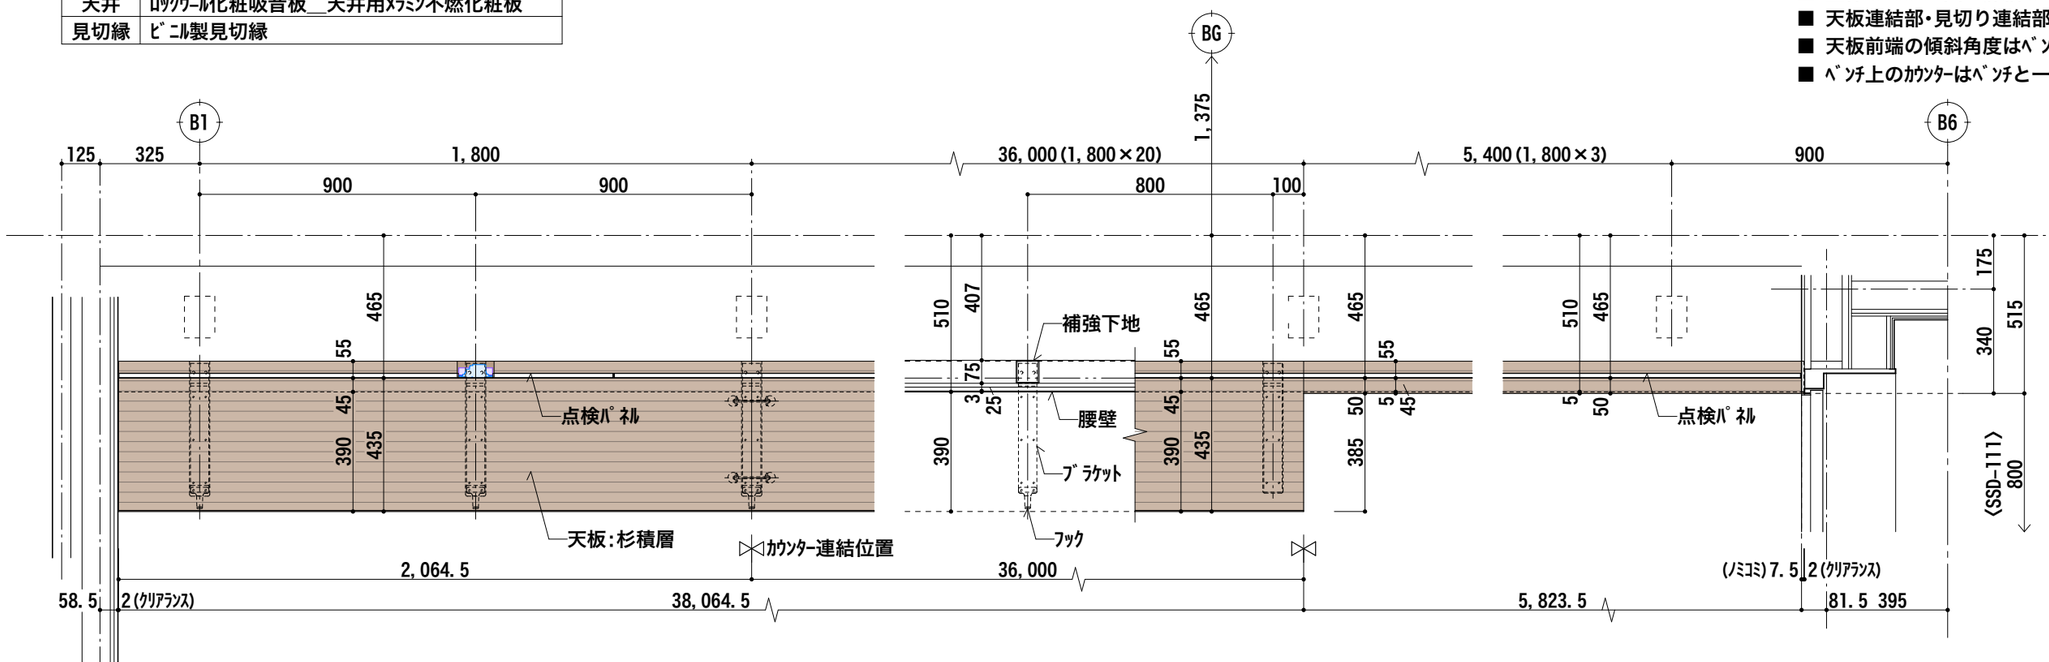


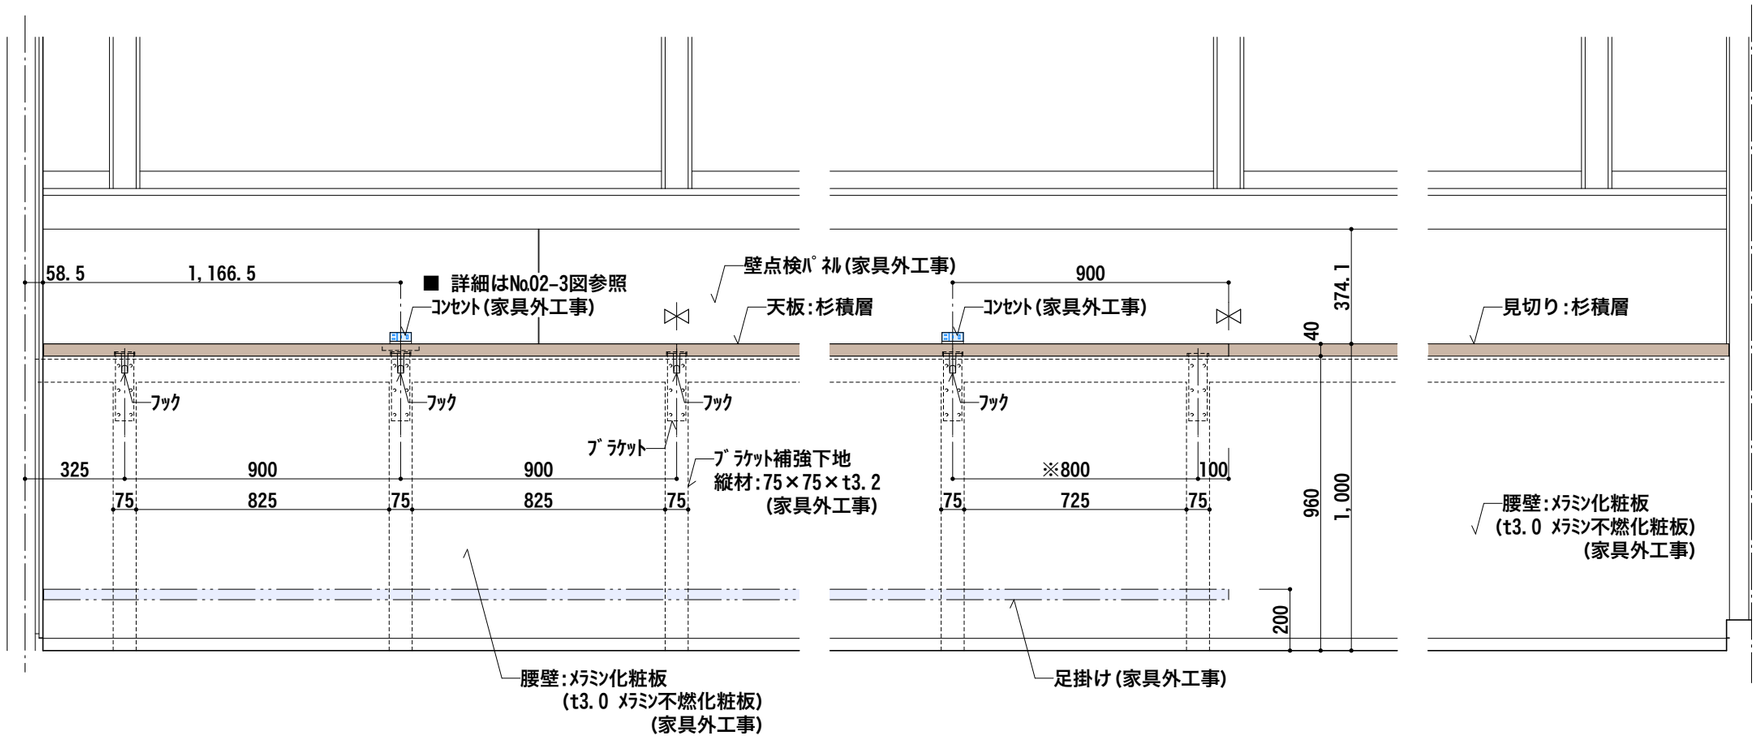

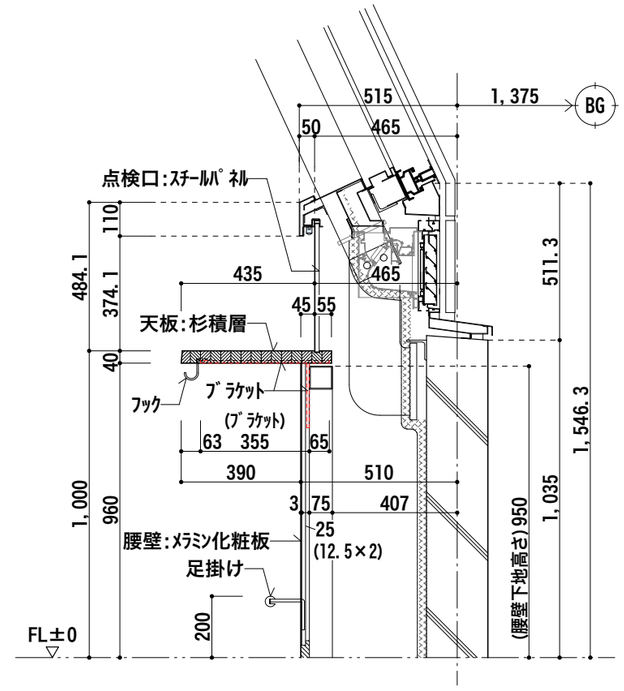


立断面図　1：20


作図	2025.09		夕カハタ工業株式会社 富山県南砺市坪野364　TEL 0763(82)0226(代)　FAX 0763(82)6627	担当	工事名称 北陸銀行 アルプスビル別館増築・アルプスビル電算棟改修工事	縮尺 1：20	承認	図面No. 02-2
訂正	2026.01.26	2026.03.30		作図	図面名称 3階 食堂　ｶｳﾝﾀｰ　【H-2】			
	2026.02.16	2026.04.28						
	2026.03.06							

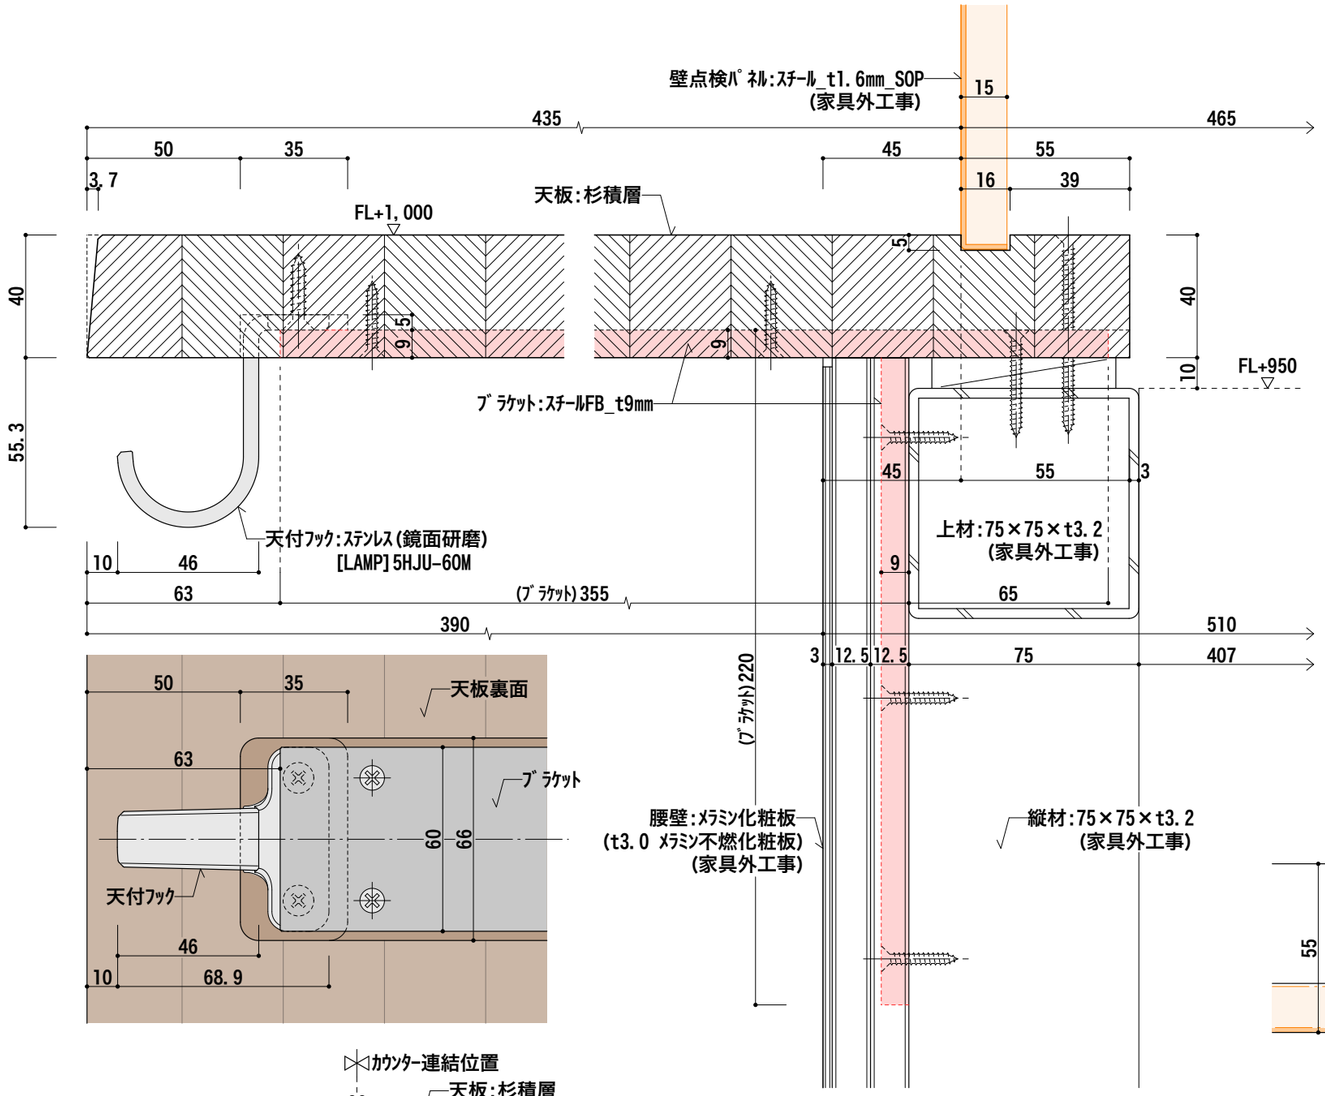

カウンター立断面詳細図　1：2

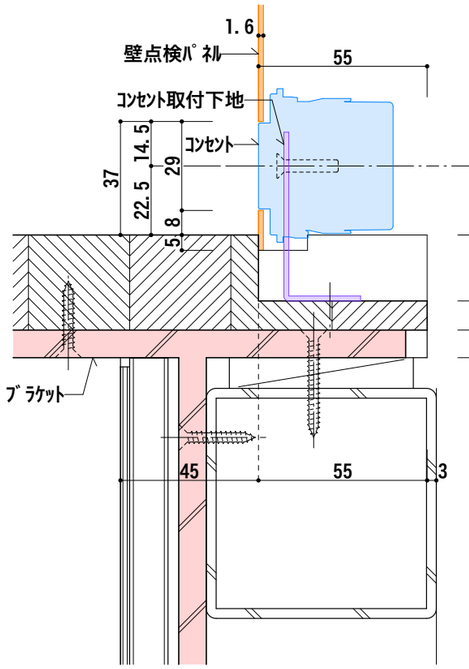


コンセント部立断面詳細図　1：2

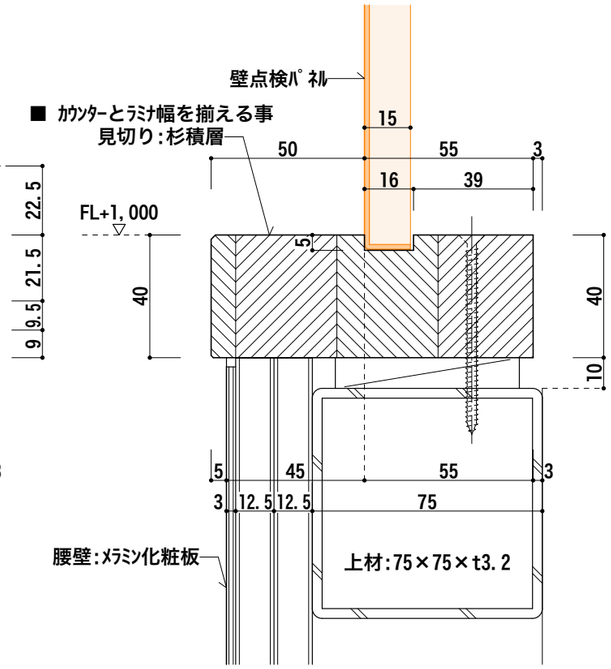


見切り立断面詳細図　1：2

カウンター連結部詳細図　1：2

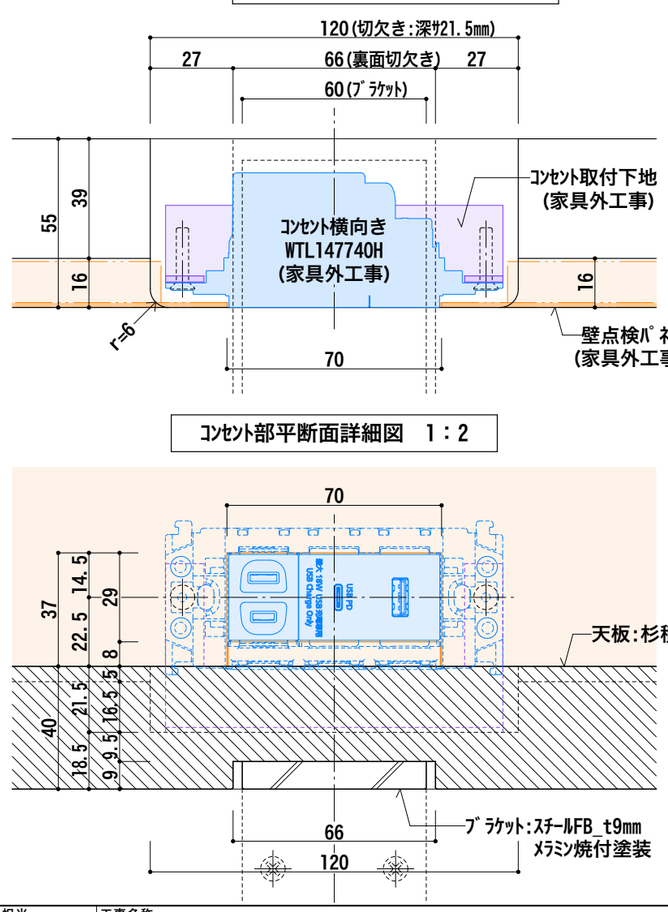

コンセント部平断面詳細図　1：2

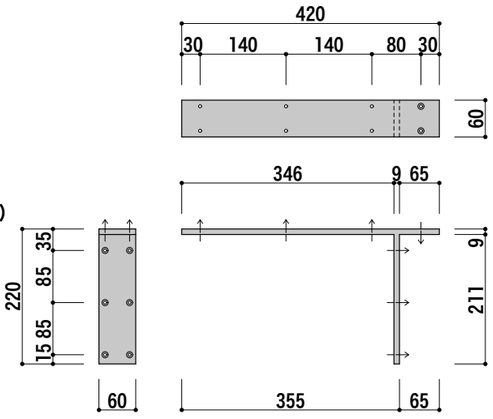

仕様:ｽﾁｰﾙFB_t9mm
仕上:SOP(塗装工事)

ﾌﾞﾗｹｯﾄ


作図	2025.09		タカハタ工業株式会社	担当	工事名称	北陸銀行 アルプスビル別館増築・アルプスビル電算棟改修工事	縮尺	承認	図面No.
訂正	2026.01.26	2026.03.30	富山県南砺市坪野364 TEL 0763(82)0226(代) FAX 0763(82)6627	作図	図面名称	3階 食堂　ｶｳﾝﾀｰ　【H-2】　詳細図	1：2 1：10		02-3
	2026.02.16	2026.04.28							
	2026.03.06								




《主な仕様・品番》

天板	杉積層(富山県産材)	[ｸﾘｱ]ﾛｰﾄｽ・ﾜﾝ(自然系撥水塗料)


■ 天板連結部はﾗﾐﾅ幅を揃える

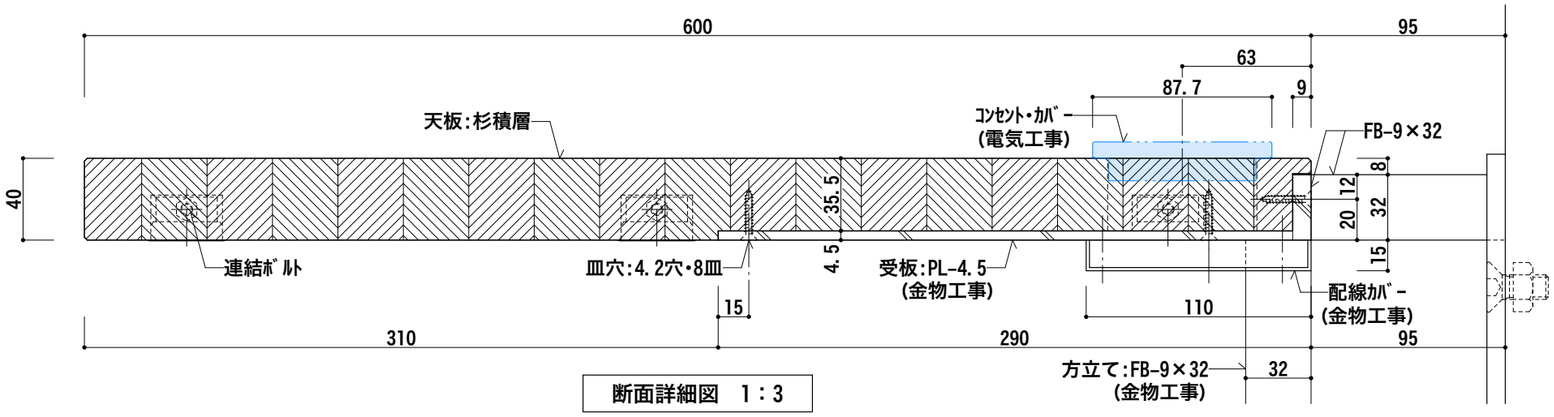

断面詳細図　1：3

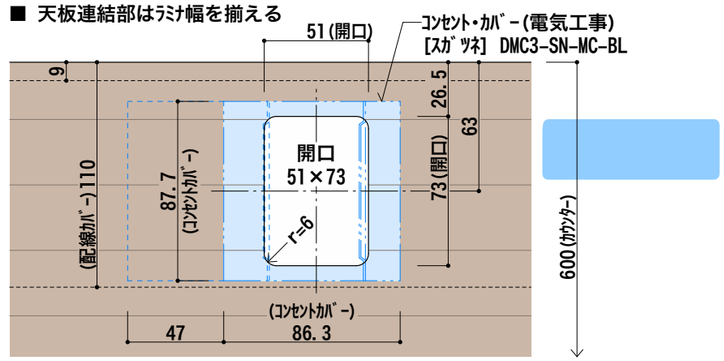


ｺﾝｾﾝﾄ開口

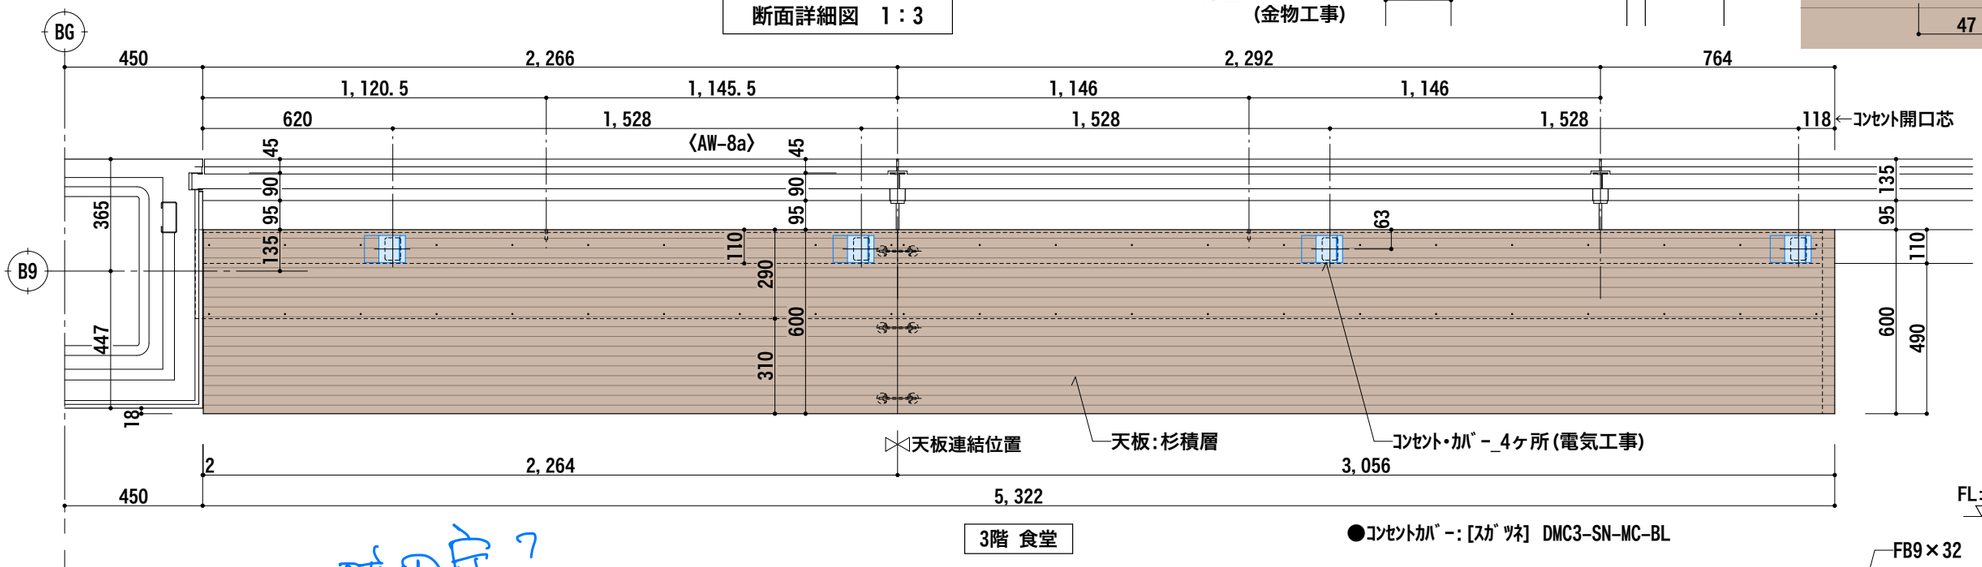


3階 食堂

●ｺﾝｾﾝﾄｶﾊﾞｰ:[ｽｶﾞﾂﾈ] DMC3-SN-MC-BL

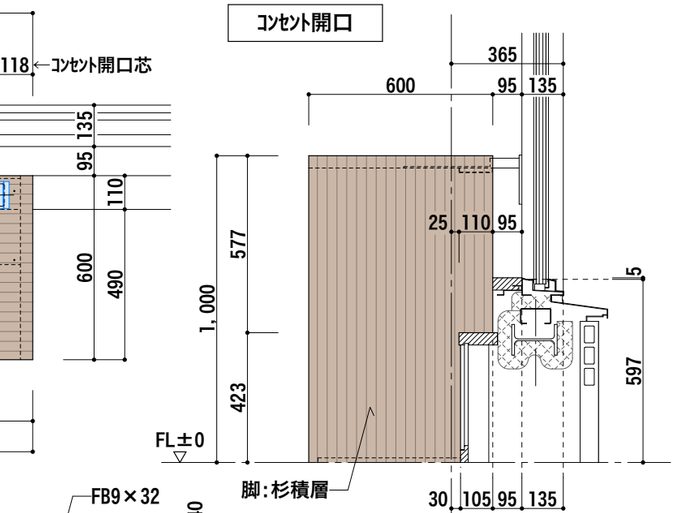

側面図　1：20

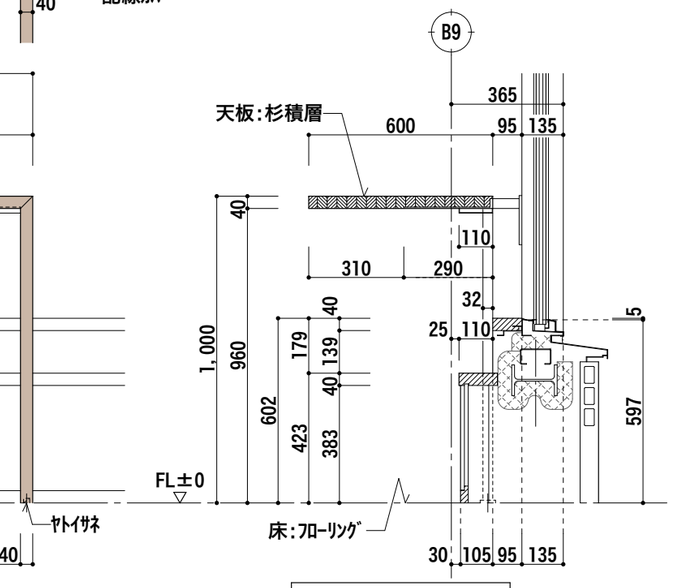

立断面図　1：20

作図	2026.04.23	タカハタ工業株式会社	担当	工事名称	北陸銀行 アルプスビル別館増築・アルプスビル電算棟改修工事	縮尺	承認
訂正	2026.04.30	富山県南砺市坪野364 TEL 0763(82)0226(代) FAX 0763(82)6627	作図	図面名称	3階 食堂　ﾊｲｶｳﾝﾀｰ (AW-8a前)	1：20 1：3	図面No. 29

