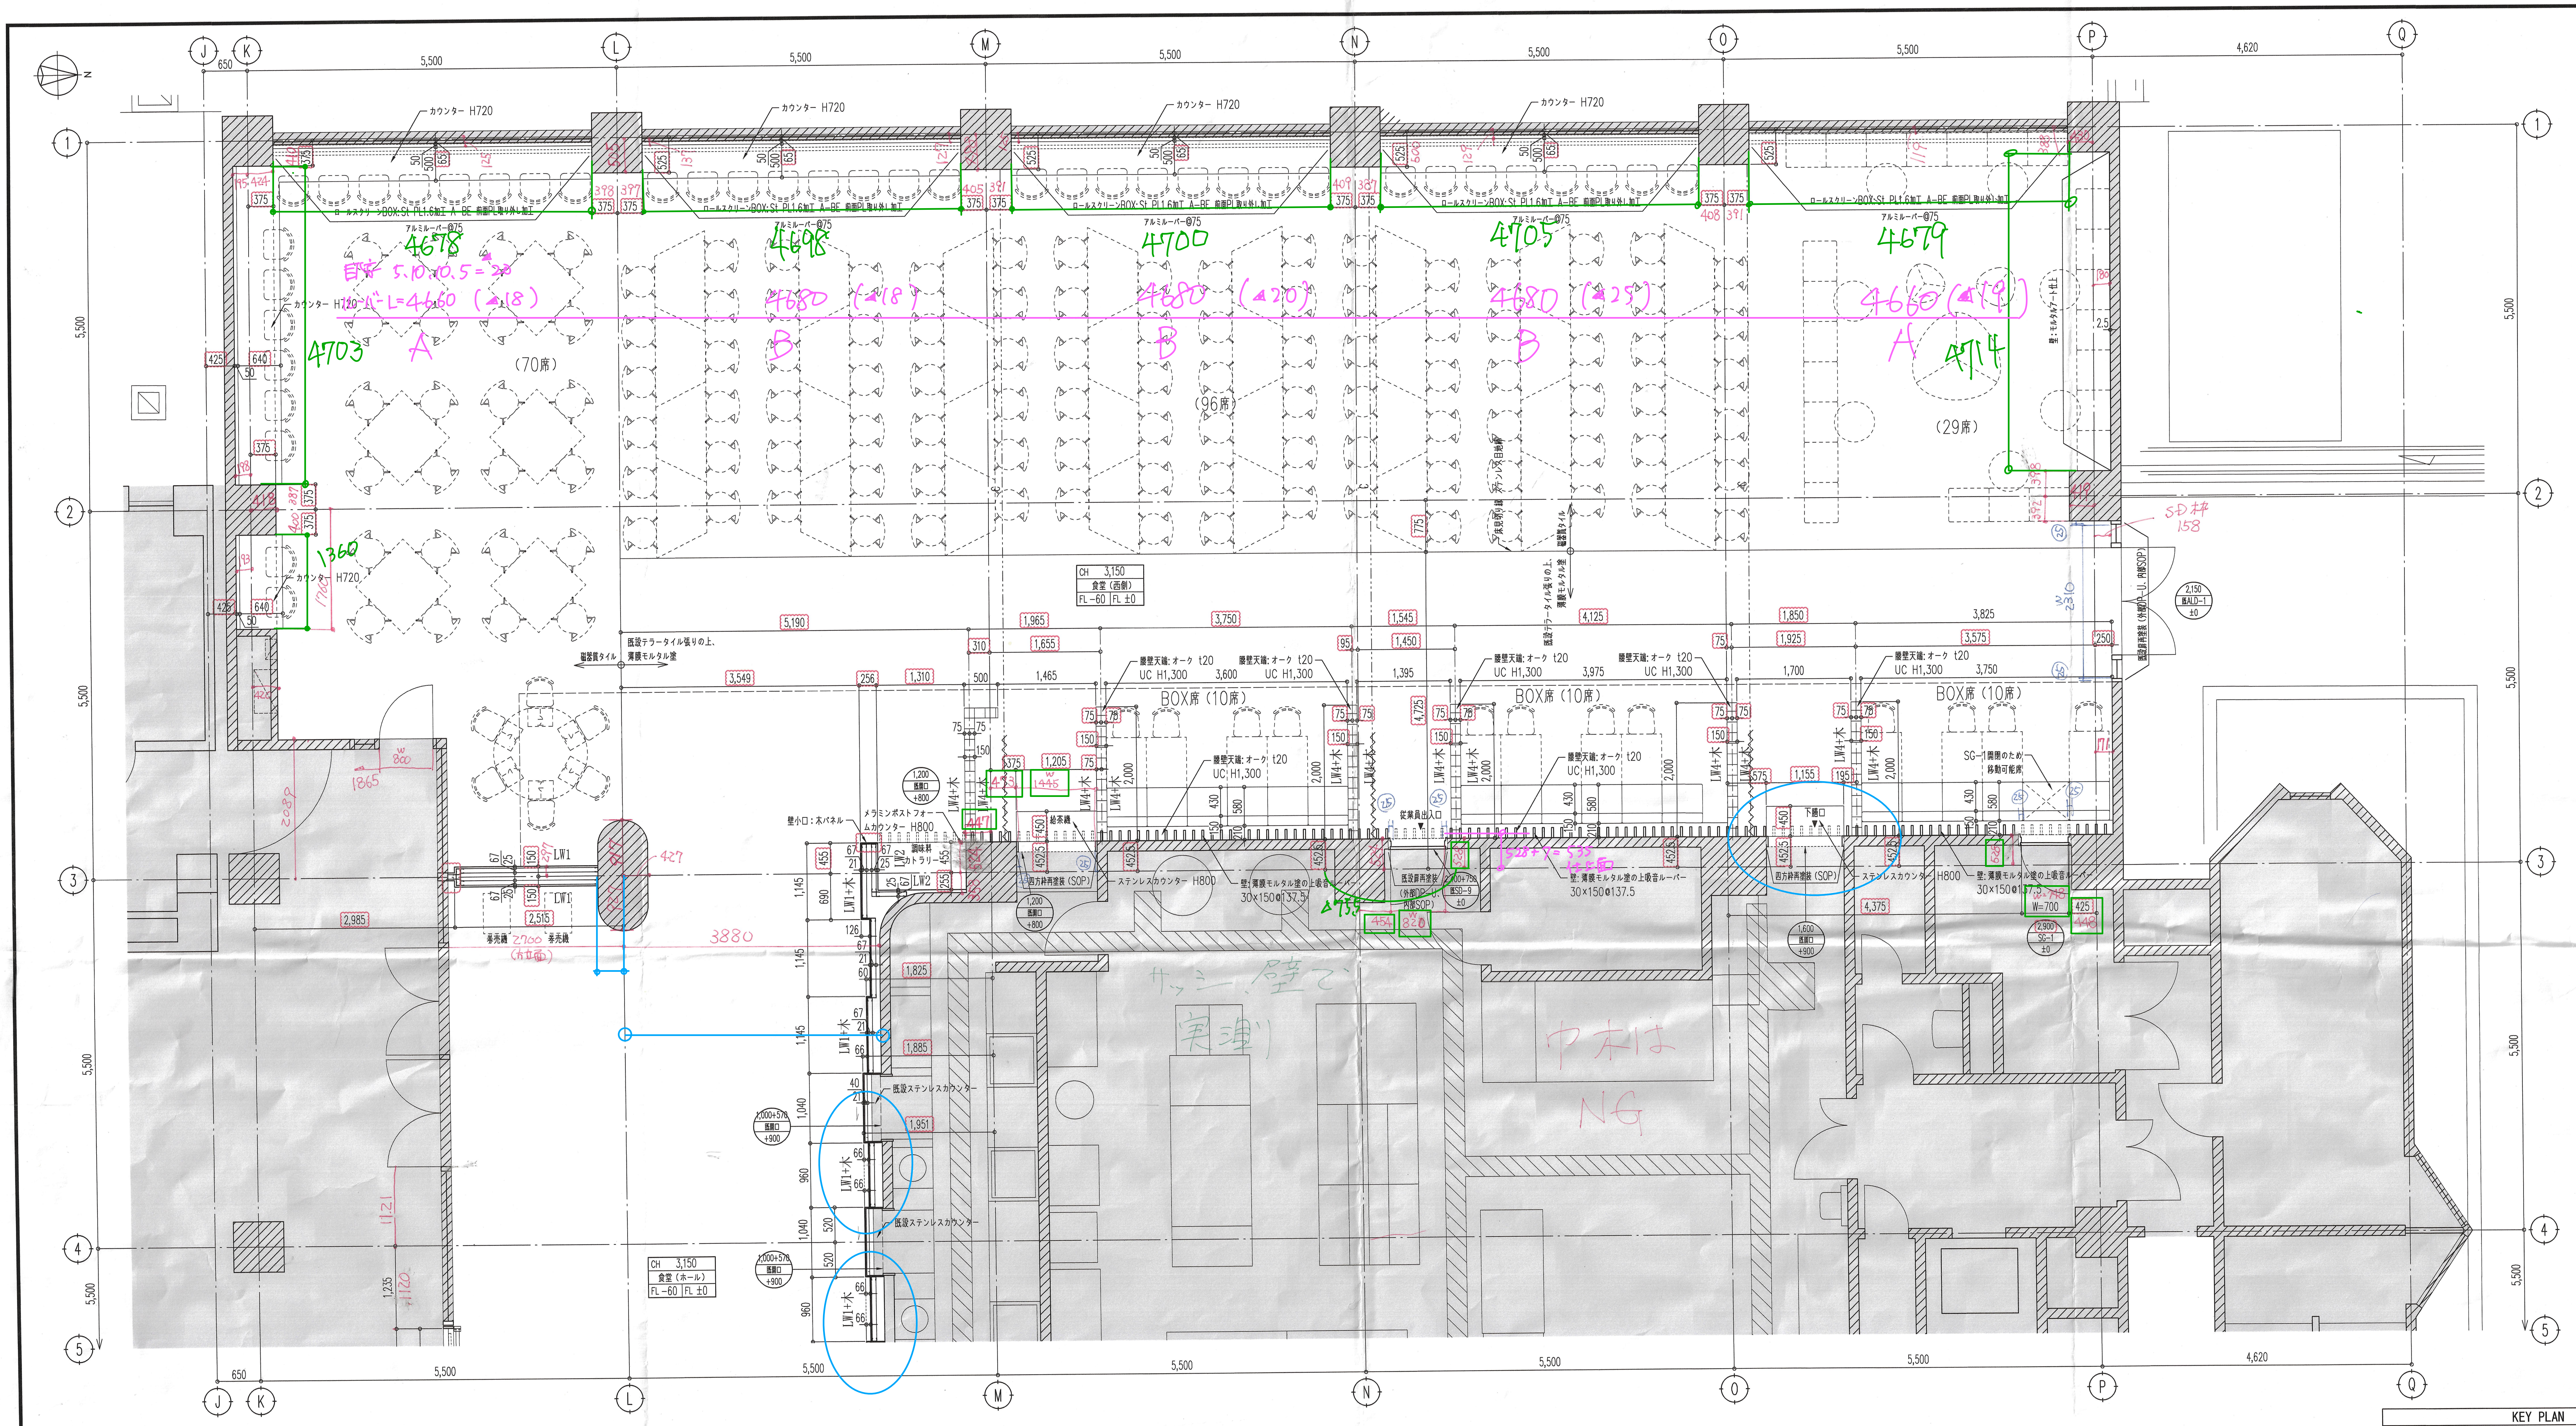
J
K
L
M
N
O
P
Q
1
2
3
4
5
650
5,500
4,620
カウンター H720
ロールスクリーンBOX:St PL1.6加工 A-BE 前面PL取り外し加工
アルミルーバー@75
375
425
640
50
（70席）
（96席）
（29席）
壁：モルタルアート仕上
CH 3,150
食堂（西側）
FL－60 FL ±0
既設テラータイル張りの上、薄膜モルタル塗
磁器質タイル
5,190
3,549
256
1,310
1,965
1,655
310
500
1,465
3,750
1,545
1,450
95
1,395
4,125
1,850
1,925
3,825
3,575
250
腰壁天端：オーク t20
UC H1,300
3,600
3,975
1,700
BOX席（10席）
LW4+木
2,000
430
580
150
210
75
1,205
1,155
195
575
4,725
775
ステンレス見切り線
SG−1開閉のため移動可能席
メラミンポストフォームカウンター H800
壁小口：木パネル
調味料カトラリー
LW1
LW2
LW1+木
給茶機
従業員出入口
下膳口
四方枠再塗装（SOP）
ステンレスカウンター H800
壁：薄膜モルタル塗の上吸音ルーバー 30×150@137.5
既設扉再塗装（外部DP−U、内部SOP）
2,100+750 既SD−9 ±0
1,200 既開口 +800
1,600 既開口 +900
2,900 SG−1 ±0
2,150 既ALD−1 ±0
W=700
425
4,375
既設扉再塗装（外部DP−U、内部SOP）
券売機
2,515
2,985
1,145
690
126
67
21
60
66
40
1,040
960
520
1,825
1,885
1,951
既設ステンレスカウンター
1,000+570 既開口 +900
CH 3,150
食堂（ホール）
FL－60 FL ±0
1,235
4678
4698
4700
4705
4679
目地 5.10.10.5＝20
ルーバーL＝4660（▲18）
4680（▲18）
4680（▲20）
4680（▲25）
4660（▲19）
A
B
B
B
A
4703
4714
1360
1760
195 424
398 397
405 391
409 387
408 391
388 430
418 387
400
198
193
420
w 800
1865
2089
427
3880
2700（右立面）
297
1121
1120
447
453
w 1445
▲735
454
w 820
528
528+7＝535 仕上面
626
w＝718
448
180
171
392
398
419
SD枠 158
w 2310
25
125
137
127
129
119
525
600
サッシ、壁で実測
中木は NG

壁記号凡例

L 床～天井
[L] スラブ～スラブ
[L] 天井内　増張り
[L][X][Y]+[Z]
MT：薄膜モルタル塗
木：木パネル t5・7・9

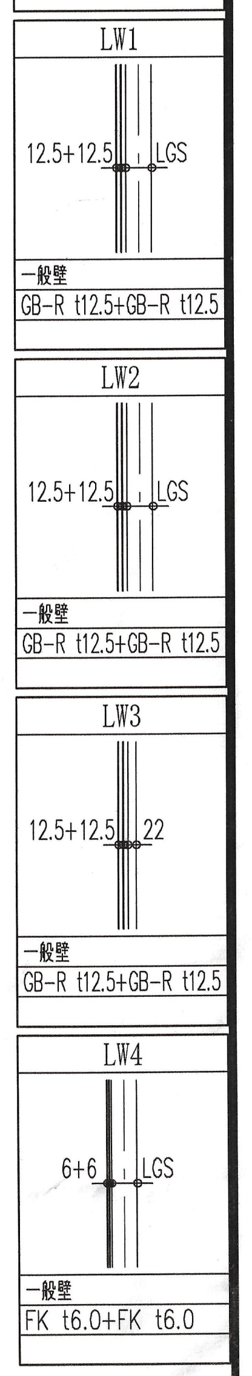
LW1
12.5+12.5
LGS
LW2
12.5+12.5
LGS
LW3
12.5+12.5
22
LW4
6+6
LGS

記号	種別	構成
LW1	一般壁	GB-R t12.5+GB-R t12.5
LW2	一般壁	GB-R t12.5+GB-R t12.5
LW3	一般壁	GB-R t12.5+GB-R t12.5
LW4	一般壁	FK t6.0+FK t6.0

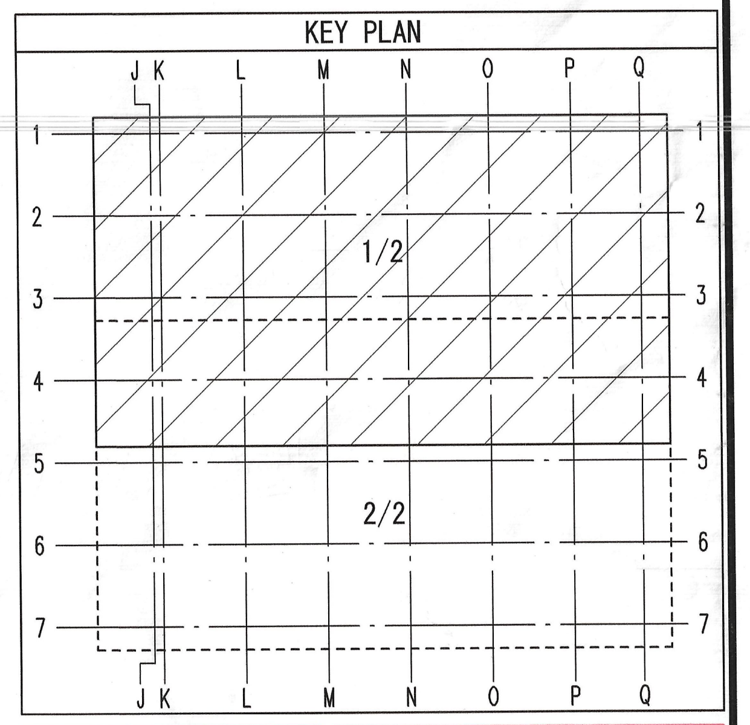
KEY PLAN
J K L M N O P Q
1
2
3
4
5
6
7
1/2
2/2

打合図
'26.10.08

設計図発行日
'26.03.27

76

71

ボード略号凡例

略号	内容
GB-R	石膏ボード
GB-R-H	普通硬質石膏ボード
GB-S	シージング石膏ボード
GB-F	強化石膏ボード
GB-L	石膏ラスボード
GB-D	化粧石膏ボード
GB-NC	不燃積層石膏ボード、不燃化粧石膏ボード
GB-P	吸音あなあき石膏ボード
GB-PD	化粧石膏吸音ボード
GB-R-Hc	吸放湿石膏ボード
K	けい酸カルシウム板
KB	化粧けい酸カルシウム板
RB	ロックウール吸音板

食堂（西側）	CH=3,150	躯体レベル FL-60 仕上レベル FL±0
床	仕上	既設テラータイル張りの上薄膜モルタル塗 レベル調整モルタルの上磁器質タイル
	下地	コンクリート
巾木		不陸調整の上 樹脂巾木 H40
壁	仕上	吸音ルーバー 既設GB-Rt12下地ラフトンジャンボ吹付一部50角タイル張りの上薄膜モルタル塗
	下地	軽量鉄骨
天井	仕上	DR t12 GB-Rt12.5下地EP+吸音ルーバー
	下地	軽量鉄骨
廻縁		塩ビ製
特記		カウンター、四方枠・三方枠再塗装、ストリングスカーテン＋埋込カーテンレール、アルミルーバー＋ロールスクリーン

食堂（ホール）	CH=3,150	躯体レベル FL-60 仕上レベル FL±0
床	仕上	既設テラータイル張りの上薄膜モルタル塗
	下地	コンクリート
巾木		不陸調整の上 樹脂巾木 H40
壁	仕上	木パネル 既設GB-Rt12下地ラフトンジャンボ吹付一部50角タイル張りの上薄膜モルタル塗
	下地	軽量鉄骨
天井	仕上	DR t12 GB-Rt12.5下地EP+吸音ルーバー
	下地	軽量鉄骨
廻縁		－
特記		手洗いカウンター（設備工事）・鏡

チェック項目	未	完	・	未	完
•FLの押えの統一			•巾木の逃げ		
•下げ梁 下げスラブ			•石、T、B（テラゾー B）の逃げ		
•フロアーヒンジ			•SW、AW、SDの差筋・箱入		
•インサート・ルーフドレーン（打込み金物）			•SSの溝ボックス差筋箱入		
•防水立上り			•手摺子金物、アンカー差筋・箱入		
•ELV関連、箱入（押ボタン、フイヤー穴）			•ブロック用差筋（床、天井、梁下、壁）		
•設備開口、及貫通孔			•断熱材の打込み		
•荷揚げ用仮穴、墨出し穴、足場用アンカー			•誘発目地・化粧目地		
•後打部（打継ぎ部）			•常備のSFD埋め込み（マグネット夫）		
•掃除口穴（打継ぎ部清掃）			•		
•打放しフカシ・増打			•		

凡例

<階高>
2FL
4,950
1FL

<室名 記号>
天井高さ
室名
躯体天端 床仕上天端
特記事項

<開口 記号>
H 開口寸法 高さ
符号 建具符号
h 基準高さから建具下枠の上端までの高さ
特記事項（電気錠等）

●●…扉の開き優先を示す。

記号	内容	C	ストリングスカーテン
⬭	保留を示す		
◠	床レベル（FL基準）		
∧	壁ボード目地		
▨	既存（壁・柱）を示す		
▩	既存 を示す		

改訂履歴	改訂日	改訂ヶ所	改訂理由
第１回改訂			
第２回改訂			
第３回改訂			
第４回改訂			
第５回改訂			

配布ルール
1 変更の場合はこの原図を変更し、改訂履歴を明記する。
2 原図に配布予定先を記入する。
3 変更の都度、全部の配布予定先にコピーを配布する。
4 変更図（コピー）を受領したら旧版は自主廃棄する。

配布予定業者

承認	審査	作成
現場管理責任者		担当者

受領日

椙山女学園星が丘キャンパス大学会館食堂リニューアル工事
1階平面詳細図-1/2
縮尺 A1:1/50 A3:1/100　'26.09.16
清水建設株式会社名古屋支店
仕上－０１