図面・計画書添付書

工事名

椙山女学園　星が丘キャンパス大学会館食堂リニューアル工事

図面名称	躯体	仕上	設備
アルミ自動ドア製作図	打合図	受領図	受領印用図
施工予定日 2027/01/15	発行日 2026/10/02	返却希望日	

	発注者			施工部署				生産技術部		設備部	
				現場管理責任者	工事長	主任	担当者	工事長	担当者	工事長	担当者
印				承認 2026/10/07 金子 冬平				承認 2026/10/01 小山 努			
日付				10,7							

	設計責任者	工事監理者	工事監理担当者									
			意匠		構造		機械		電気			
印		工藤	山上	緒垣								
日付		261016	261014	2026,10,8								

記　事（質疑応答・連絡事項・その他）

P2～案1）一般形状で方立MIN45

工事名	椙山女学園/星が丘キャンパス　大学会館食堂リニューアル工事		
設計監理	株式会社　日建設計　　殿	施工	清水建設　株式会社　　殿

受領印	
	年　月　日

改訂	No	改訂日	改定内容	担当	受領印	No	改訂日	改定内容	担当	受領印

出図	チェック図受取	出図	チェック図受取	出図	チェック図受取
出図 2026.10.1 昭和フロント					
出図	チェック図受取	出図	チェック図受取	出図	チェック図受取

受注番号	施工図番号	
支店	管理番号	
営業 岸	検図 吉田	図番 00

※施工図修正については、基本2回以内で御承諾頂きますようご協力お願い致します。

昭和フロント株式会社

仕 様 確 認 書

この仕様は，昭和フロント株式会社のアルミサッシ，ドアー等に適用する。ご確認願います。

（注1） チェックなき場合は※印仕様（当社標準仕様）と致します。

（注2） ※印以外の仕様を適用する場合は該当項目に，特記，もしくは〇印を付けて下さい。
（建具表にもご記入下さい）

（注3） 1項の特定建築工事仕様書がある場合は，1項に記入の上，その仕様に基づき
チェックして下さい。

1.仕様書

■ ※公共建築工事標準仕様書
□ 〔 〕仕様書

2. 材 料

(a)押出形材

■ ※JIS H 4100（アルミニウム及びアルミニウム合金押出形材）に
規定するA6063S－T5とする。

(b)板 材

□ ※JIS H 4000（アルミニウム及びアルミニウム合金の板及び条）に
規定するA1100P若しくはA1200Pとする。

□ その他

(c)補 助 材

イ）補強材：アンカー（絶縁処理は、6-(a)項参照）

■ ※JIS G 3141（冷間圧延鋼板及び鋼帯）に規定するものを使用する。
JIS H 8610……電気亜鉛めっき

□ ※JIS G 3131（熱間圧延軟鋼板及び鋼帯）に規定するものを使用する。
SPHC……黒皮鋼板

□ ※JIS G 3101（一般構造用圧延鋼材）に規定するものを使用する。
SS41……普通鋼材

ロ）気密材・水密材

■ ※合成ゴム（シリコーン、EPDM－S、EPDM、クロロプレン、ブチル等）及び、ポリエステル。
■ ※軟質塩化ビニル樹脂
□ その他

ハ）振れ止め、戸当り

□ ※ポリアミド及びポリアセタール樹脂 □ その他

ニ）クレセント

□ ※本体は亜鉛合金ダイカスト（ZDC－2）鎌部分SUS304
□ 亜鉛合金ダイカスト □ SUS304 □ その他

ホ）戸車（タイヤ）

□ ※ポリアセタール樹脂 □ その他

ヘ）ネジ類

□ ※JIS G 4315（冷間圧造用ステンレス鋼線）に規定するSUS XM7
□ その他

3.表 面 処 理

（色指定は，必ずご記入下さい）

	カラー区分	種 類	処理方法 被膜	処理方法 塗膜	JIS規格	名称
□	シルバー	A1	陽極酸化皮膜 平均厚さ5μm以上	アクリル樹脂系クリヤ電着塗装を塗布	H 8602-2010	F
□	ブロンズ	A2	陽極酸化皮膜 平均厚さ5μm以上	アクリル樹脂系クリヤ電着塗装を塗布	H 8602-2010	B
□	ブラック	A1	陽極酸化皮膜 平均厚さ5μm以上	アクリル樹脂系カラー電着塗装を塗布	H 8602-2010	K
□	ホワイト	A2	陽極酸化皮膜 平均厚さ5μm以上	アクリル樹脂系カラー電着塗装を塗布	H 8602-2010	W
■	ステンカラー	A1	陽極酸化皮膜 平均厚さ5μm以上	アクリル樹脂系クリヤ電着塗装を塗布	H 8602-2010	T
□	ダークブロンズ	A1	陽極酸化皮膜 平均厚さ5μm以上	アクリル樹脂系クリヤ電着塗装を塗布	H 8602-2010	D
□	TEN-写（水圧転写）	A1	陽極酸化皮膜 平均厚さ5μm以上	アクリル樹脂系クリヤ電着塗装を塗布	H 8602-2010 ＋ K 5600	
			上記の上に、{ベースカラー塗装（セラミック系塗装）＋転写フィルム＋トップコート（セラミック系塗装）}を施した処理			
□	アクリル樹脂焼付塗装		デュラクロンCW（大日本塗料） 平均厚さ40μm以上			

4.出入口の沓摺

□ ※アルミ押出形材（2－(a)項参照）
■ JIS G 4305に規定するSUS304とし，仕上げはヘアーライン仕上げとする。
□ その他

5.ガラス工事請負の有無

■ ※別途工事
□ 請負工事

6.ガラス押えの使用区分

□ ガスケット
■ 弾性シーラント（硝子請負業者） 防火設備には防火戸用指定シーリング材とする。

7.絶縁処理

(a)補強材，アンカー

□ ※電気亜鉛めっきJIS H 8610に規定する所定のめっき処理を施したもの。
□ その他
□ ※溶融亜鉛めっき又は電気亜鉛めっき鋼板に日本塗料工業会規格 JPMS28（一液形変性エポキシ樹脂さび止めペイント）

(b)その他

8.養生

■ ※普通養生（PVC）
□ ポリシート・クラフト紙・ポリチューブ等を使用 □ その他

付属金物

（指定品の場合メーカー名，品名を記入して下さい）

付属金物	当社標準品	指定品
ドアクローザ		
ピポットヒンジ・丁番		
フロアーヒンジ		
錠 前	美 和	
ドアハンドル		
エンジン装置	ナブコ	
オペレータ装置		
マスターキー 有り （MK本数： 本）		（無し）
その他		

その他の特記事項

溶接アンカーの取付ピッチ 400以内

アルミ製建具 2,000未満 3

◎サッシ（アルミフロント）の完成品に対する寸法公差（JIS A 4706）
（単位：mm）

対象部位	サッシ（フロント）の寸法	公差
幅及び高さ（W・H又はw・h）	2,000未満	3
	2,000未満 3,500未満	4
	3,500以上	5
幅及び高さ（W・H又はw・h）の相対する辺寸法の差	2,000未満	2
	2,000未満 3,500未満	3
	3,500以上	4
枠見込み(t)	120未満	2
	120以上 150未満	3
	150以上 200未満	4
	200以上	5

改訂 No	改訂日	改訂内容	担当	工事名	相山女学園/星が丘キャンパス 大学会館食堂リニューアル工事	設計監理	株式会社 日建設計 殿	受領	年 月 日	代理店		工番	差替	製図	藤木
				図面名	仕様確認書	施工	清水建設 株式会社 殿				昭和フロント株式会社	FDNO. DATE. 縮尺	□ A2-100% □ A3-71% 検図 吉田	図番	01

建具リスト表

製作工場名	確認欄

所長	担当者

参照図番	符　号	W	X	H	数　量	取付場所	特記金物	SFシール 工場チェック	製品寸法 工場チェック
04-09	AD-1	3098	X	3065	1	エントランス～食堂			
			X						
			X						
現場案内図

施工管理	清水建設　株式会社	担当
現場住所	愛知県名古屋市千種区星が丘元町17-3	
現場電話番号		


現場地図



特記事項			サッシ納期	2026年**月**日	取付日	2026年**月**日

改訂	No	改訂日	改訂内容	担当

工事名	椙山女学園/星が丘キャンパス 大学会館食堂リニューアル工事	設計監理	株式会社　日建設計	殿	受領		代理店		工番		差替		製図	藤木
									FDNO.		DATE.			
図面名	建具リスト	施工	清水建設　株式会社	殿		年　月　日		昭和フロント株式会社	縮尺	☐ A2-100% ☐ A3-71%		検図	吉田	図番	02

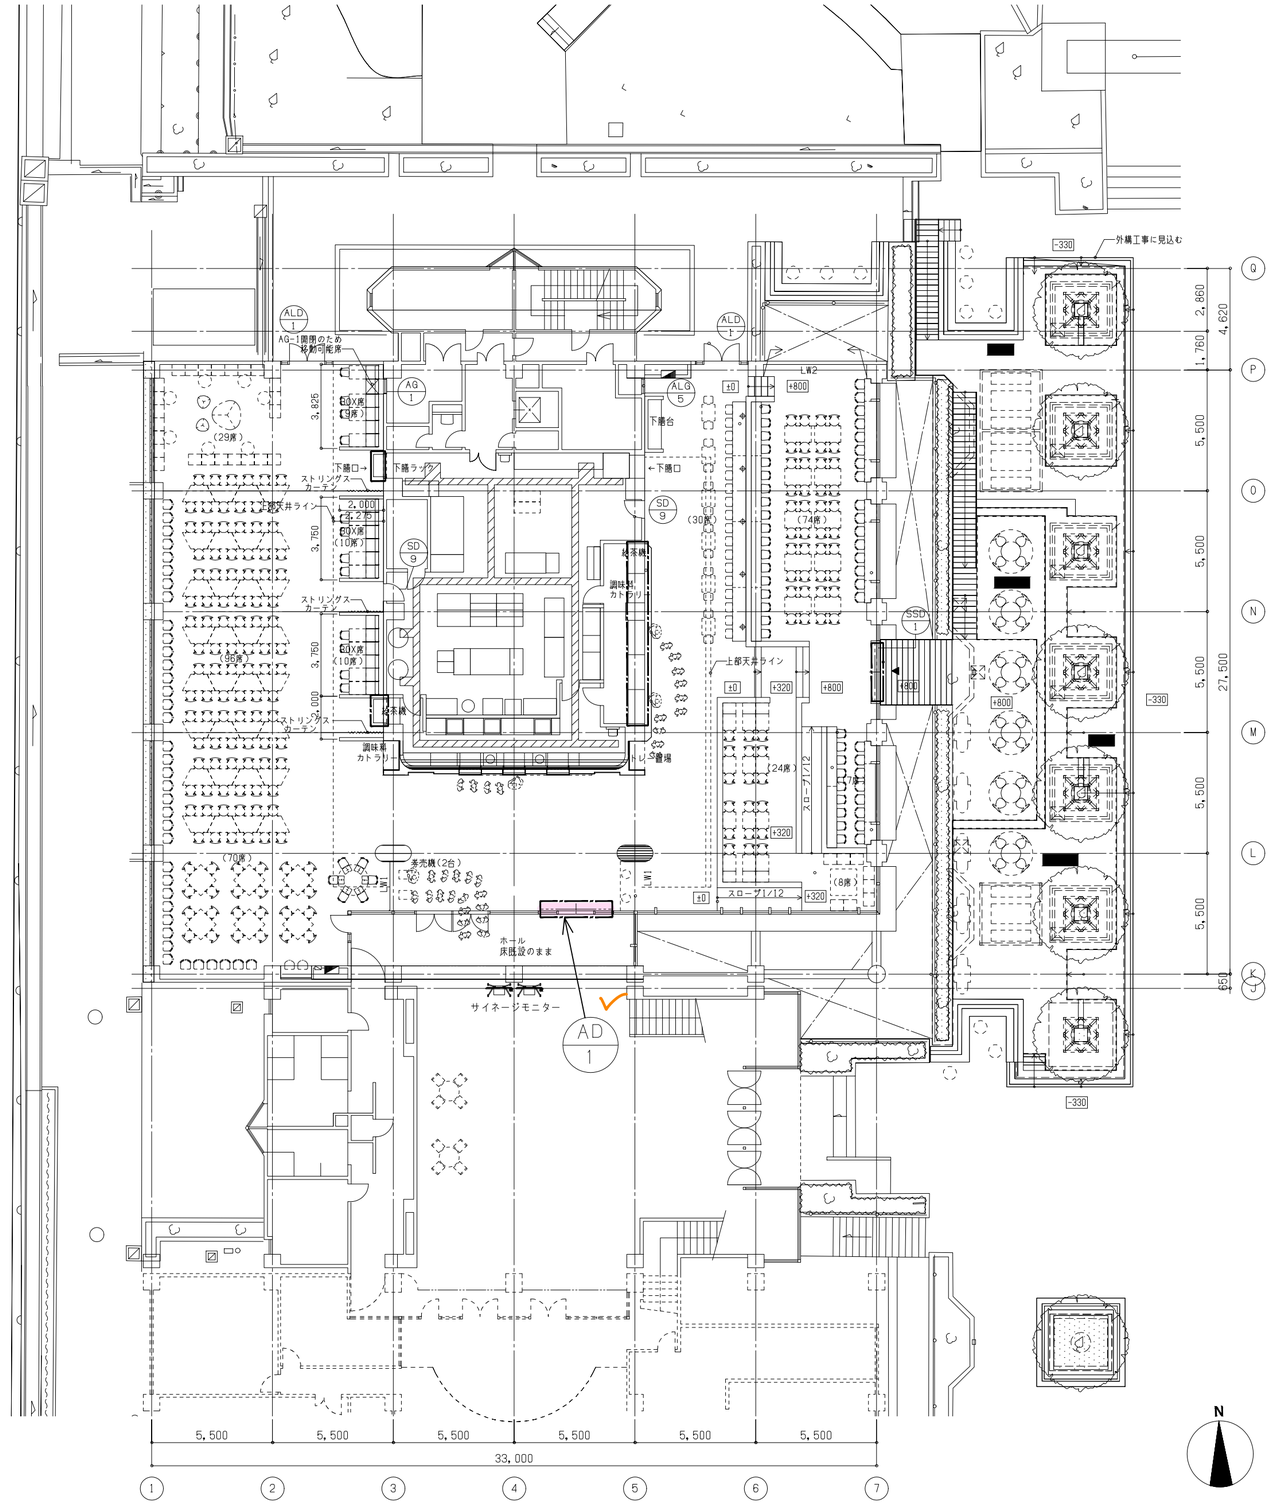

改訂	No	改訂日	改訂内容	担当


工事名	椙山女学園/星が丘キャンパス 大学会館食堂リニューアル工事	設計監理	株式会社　日建設計	殿	受領		代理店		工番		差替		製図	藤木
図面名	建具配置図	施工	清水建設　株式会社	殿		年　月　日		昭和フロント株式会社	FDNO.	DATE.	縮尺	□ A2-100% □ A3-71%	検図	吉田	図番	03

※アンカーピッチ：両端～100・@400以下


1
AD

新 設


時記 5.14.8.6
強くガラス4t全数ヒートソーク試験

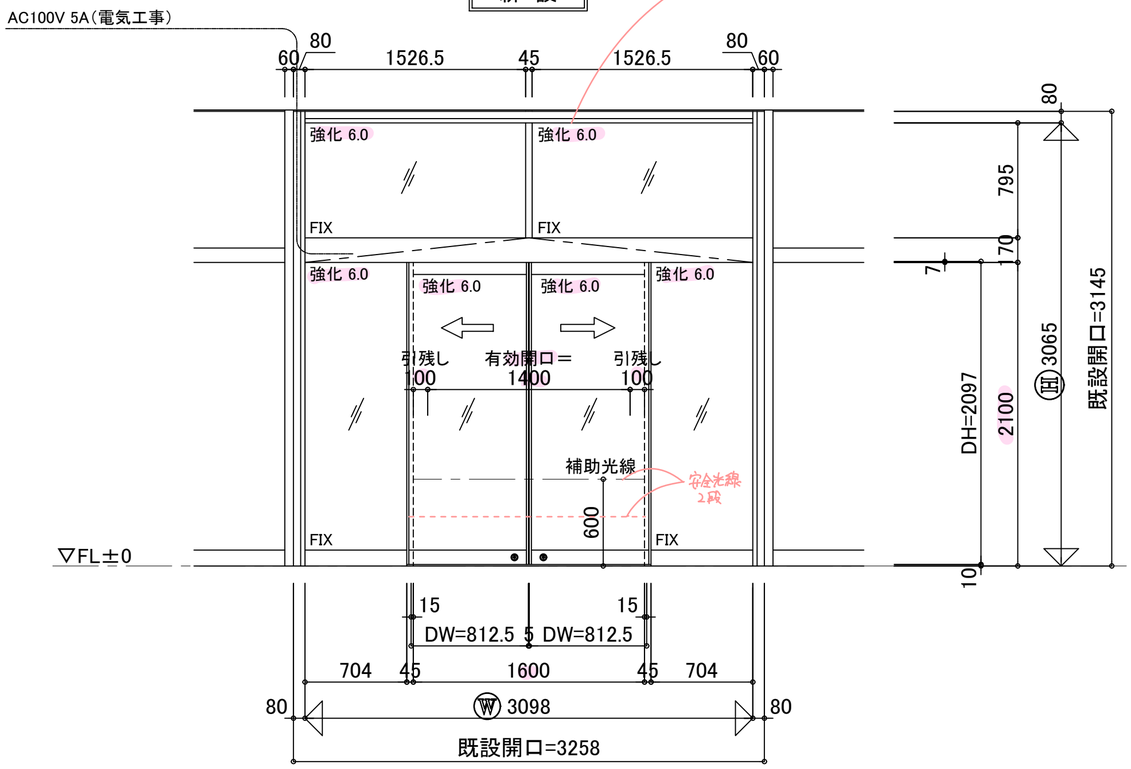

既 設

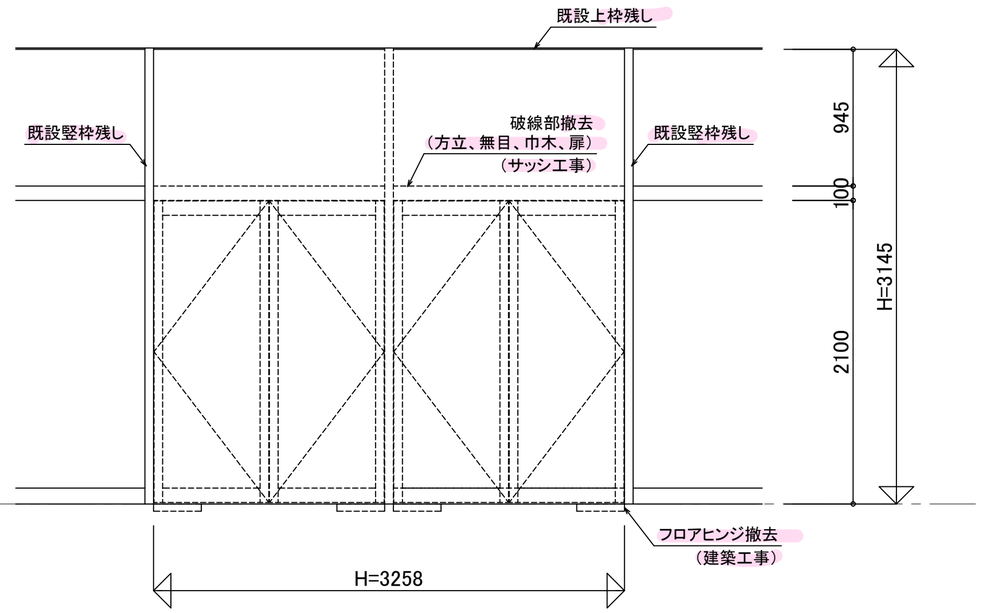

エントランス

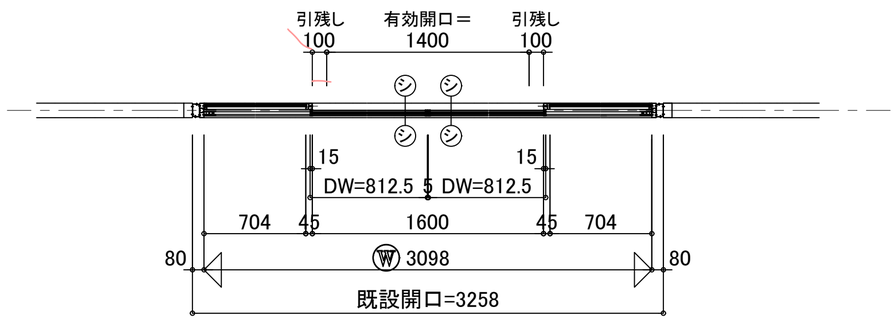

食 堂

ノックダウン納品

食堂側観図

符号	数量	取付場所
1/AD	1	エントランス～食堂
機種	NL400 引分け自動ドア（斜美）	
耐風圧性能		
仕上	ステンカラー	
水切出	㎡	アルミ額縁
硝子厚		網戸 可動・固定（　）
強化ガラス 6.0	㎡	硝子仕舞　ビード・シール

付属金物 1箇所当りの金物数を記入する

部品名	品番	数量	適要
エンジン装置	ナブコ	一式	
センサー	ナブコ NS-A02	2	内外取付
補助光線		1	H=600
錠 前	美和 DG2D-4	2	

※停電時及び火報発報時、連動解錠手動開閉可能


キープラレロ 引き調整するので
サムターンやシリンダーが設置できるようにしておく。

改訂 No	改訂日	改訂内容	担当

工事名	椙山女学園/星が丘キャンパス 大学会館食堂リニューアル工事	設計監理	株式会社　日建設計	殿	受領		代理店		工番		差替		製図	藤木
図面名	AD-1 姿図	施工	清水建設　株式会社	殿		年　月　日	昭和フロント株式会社		FDNO.	DATE.	縮尺	1/30	□ A2-100% □ A3-71%	検図	吉田	図番	04

1
AD


食 堂

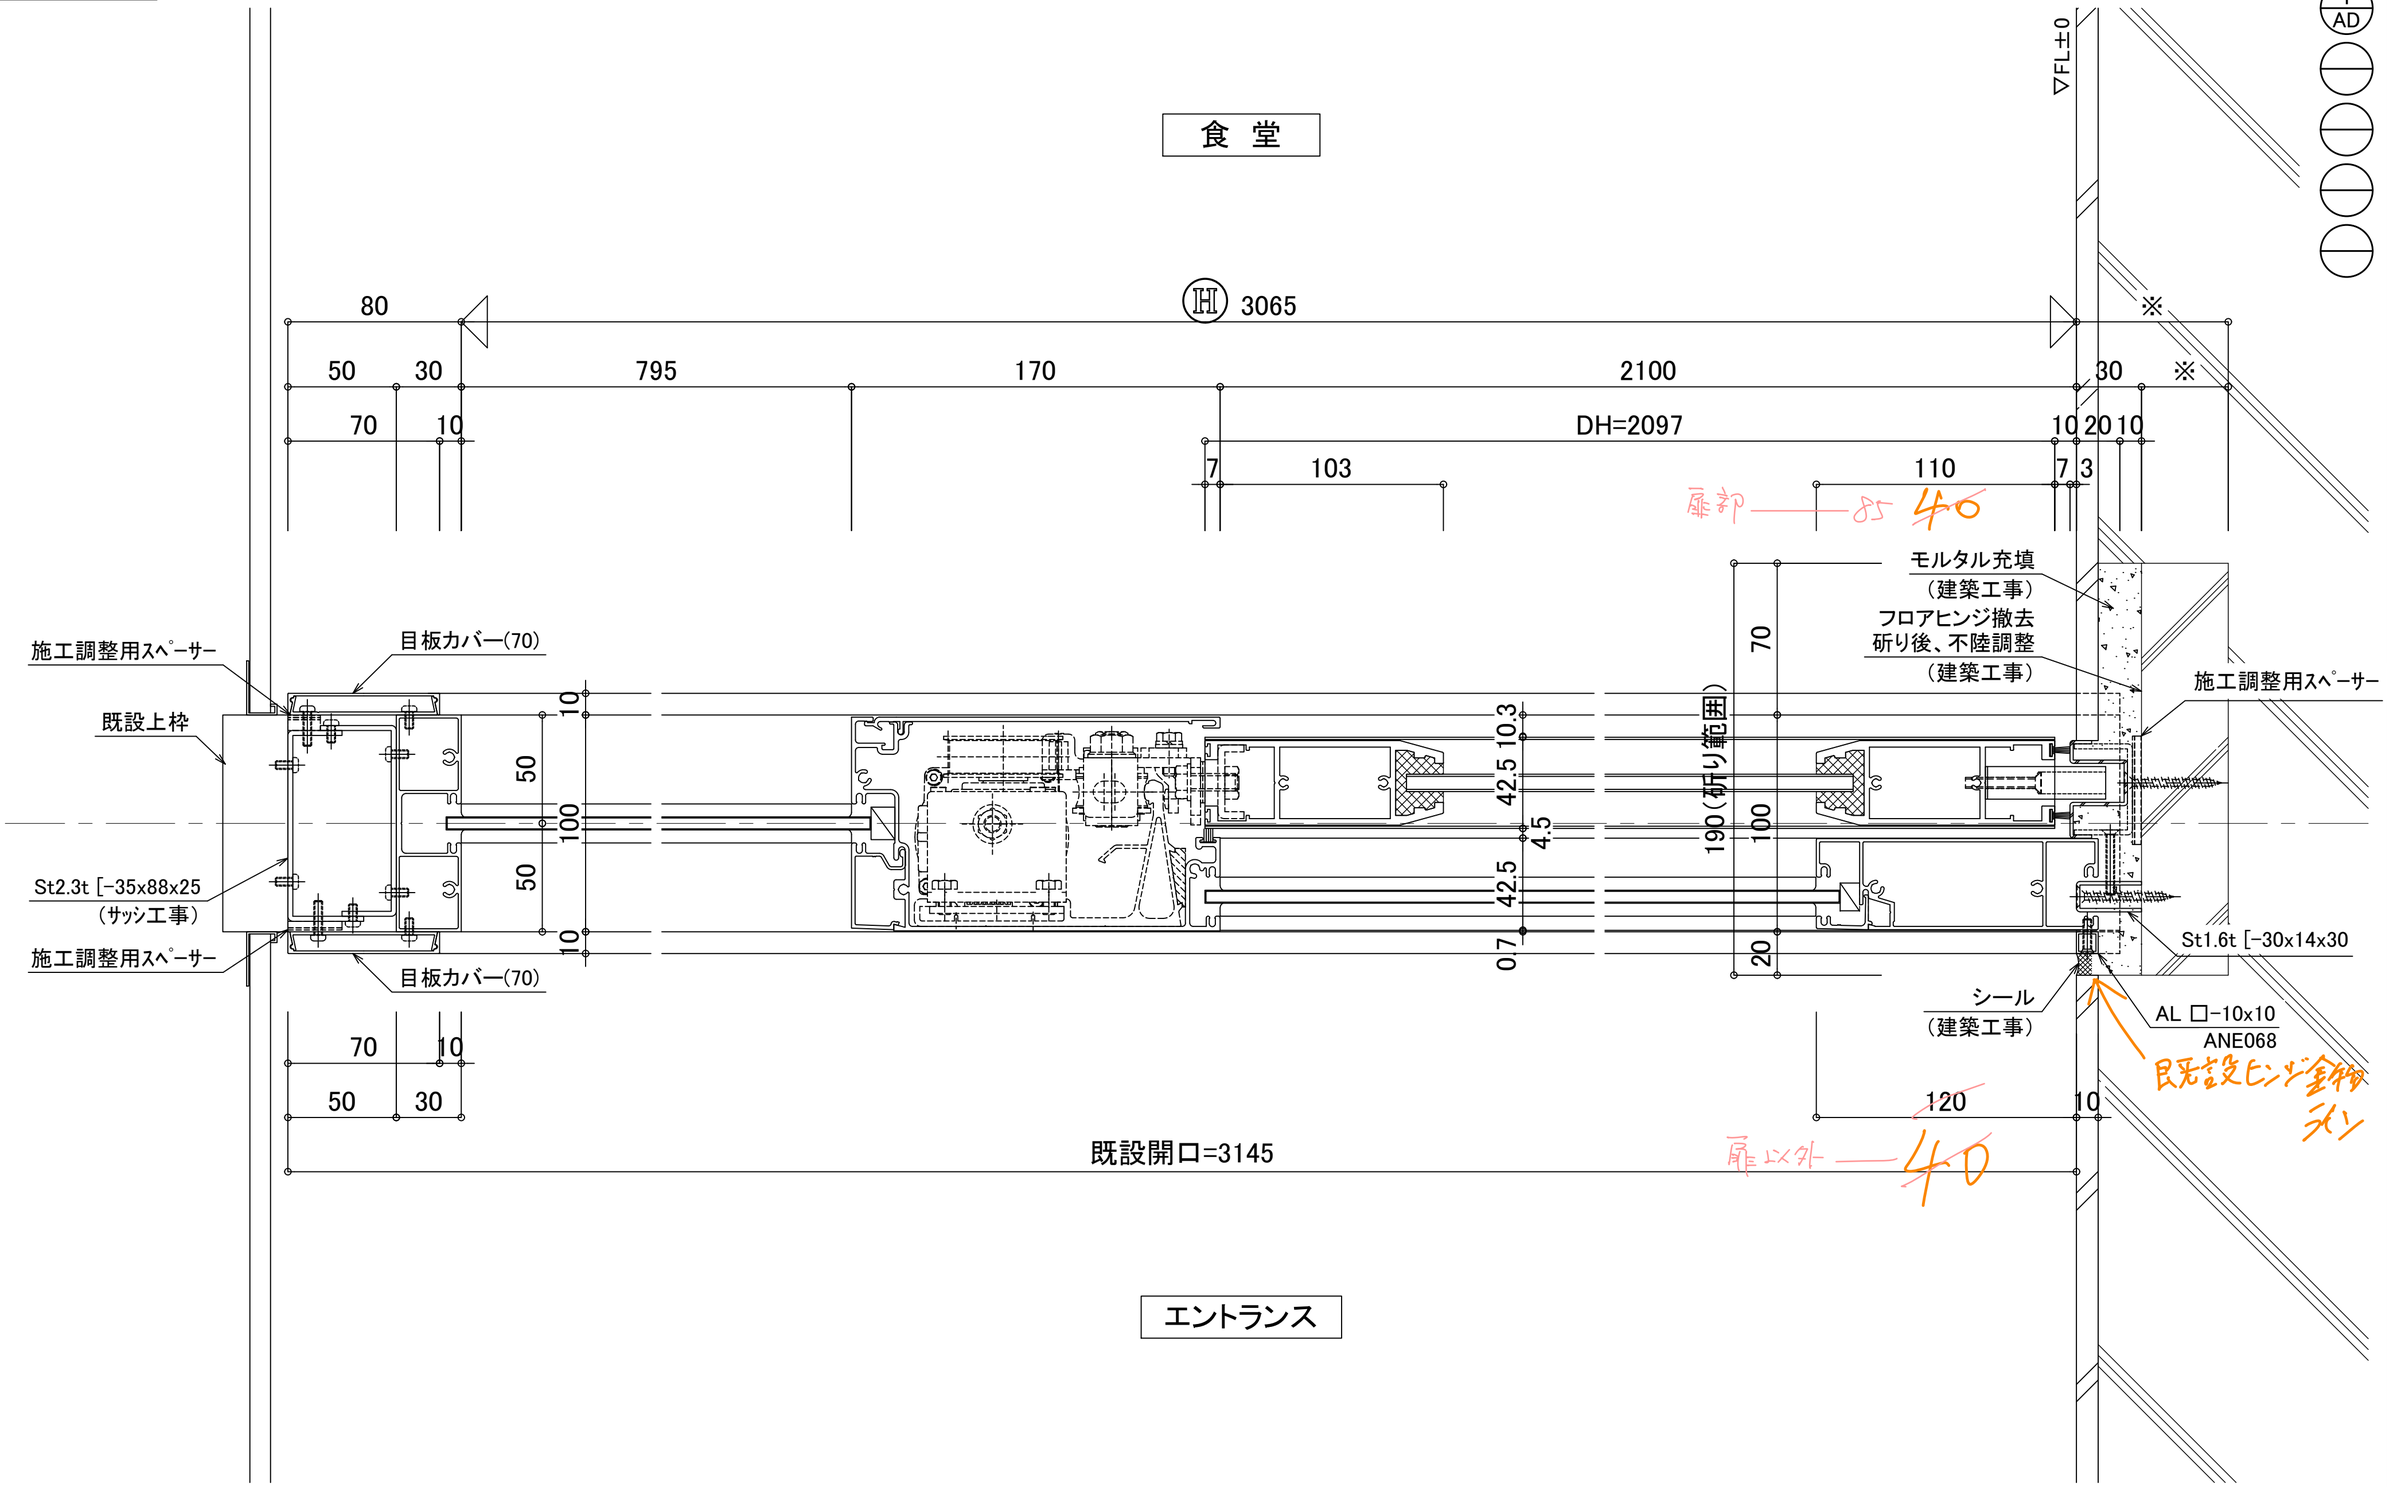

エントランス

改訂	No	改訂日	改訂内容	担当

工事名	椙山女学園/星が丘キャンパス 大学会館食堂リニューアル工事	設計監理	株式会社 日建設計	殿	受領		代理店		工番		差替	製図	藤木
図面名	AD-1 詳細図	施工	清水建設 株式会社	殿		年 月 日		昭和フロント株式会社	FDNO.	DATE.			
									縮尺	1/2	□ A2-100% □ A3-71%	検図	吉田	図番	05

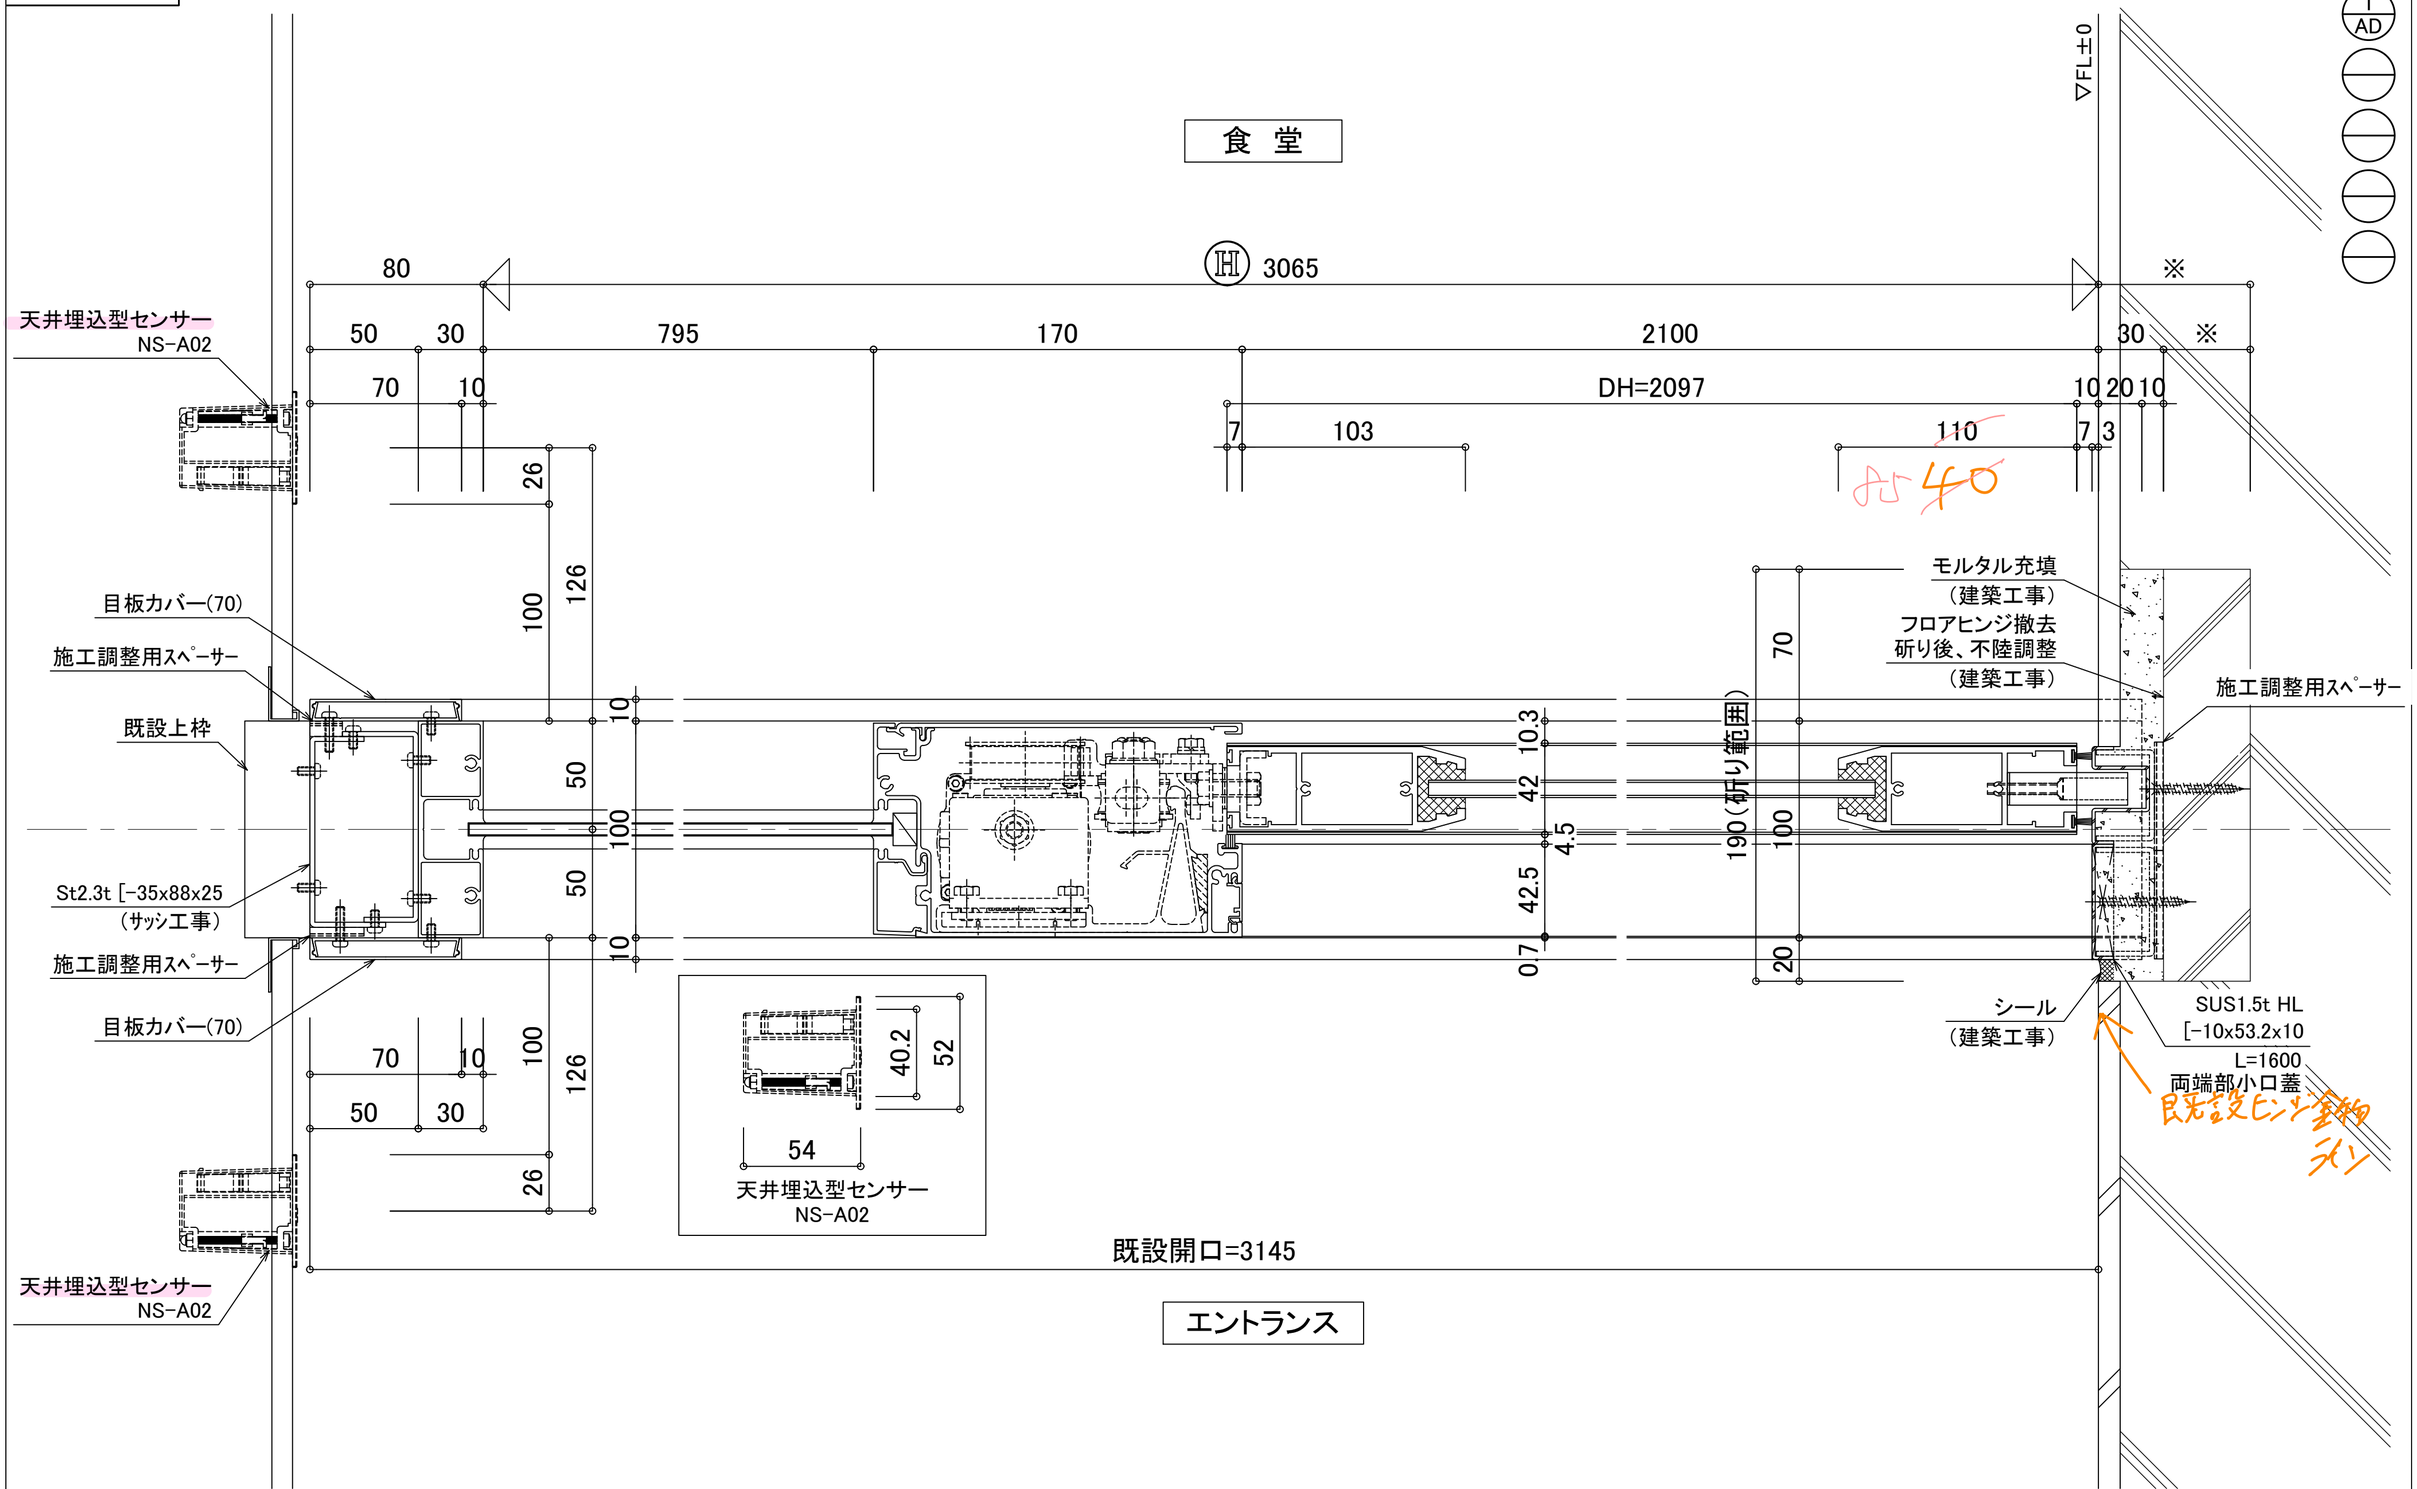


改訂	No	改訂日	改訂内容	担当

工事名	椙山女学園/星が丘キャンパス 大学会館食堂リニューアル工事	設計監理	株式会社 日建設計	殿	受領		代理店		工番		差替	製図	藤木
図面名	AD-1 詳細図	施工	清水建設 株式会社	殿		年 月 日		昭和フロント株式会社	FDNO.	DATE.		図番	06
									縮尺	1/2	□ A2-100% □ A3-71%	検図	吉田

1
AD

エントランス

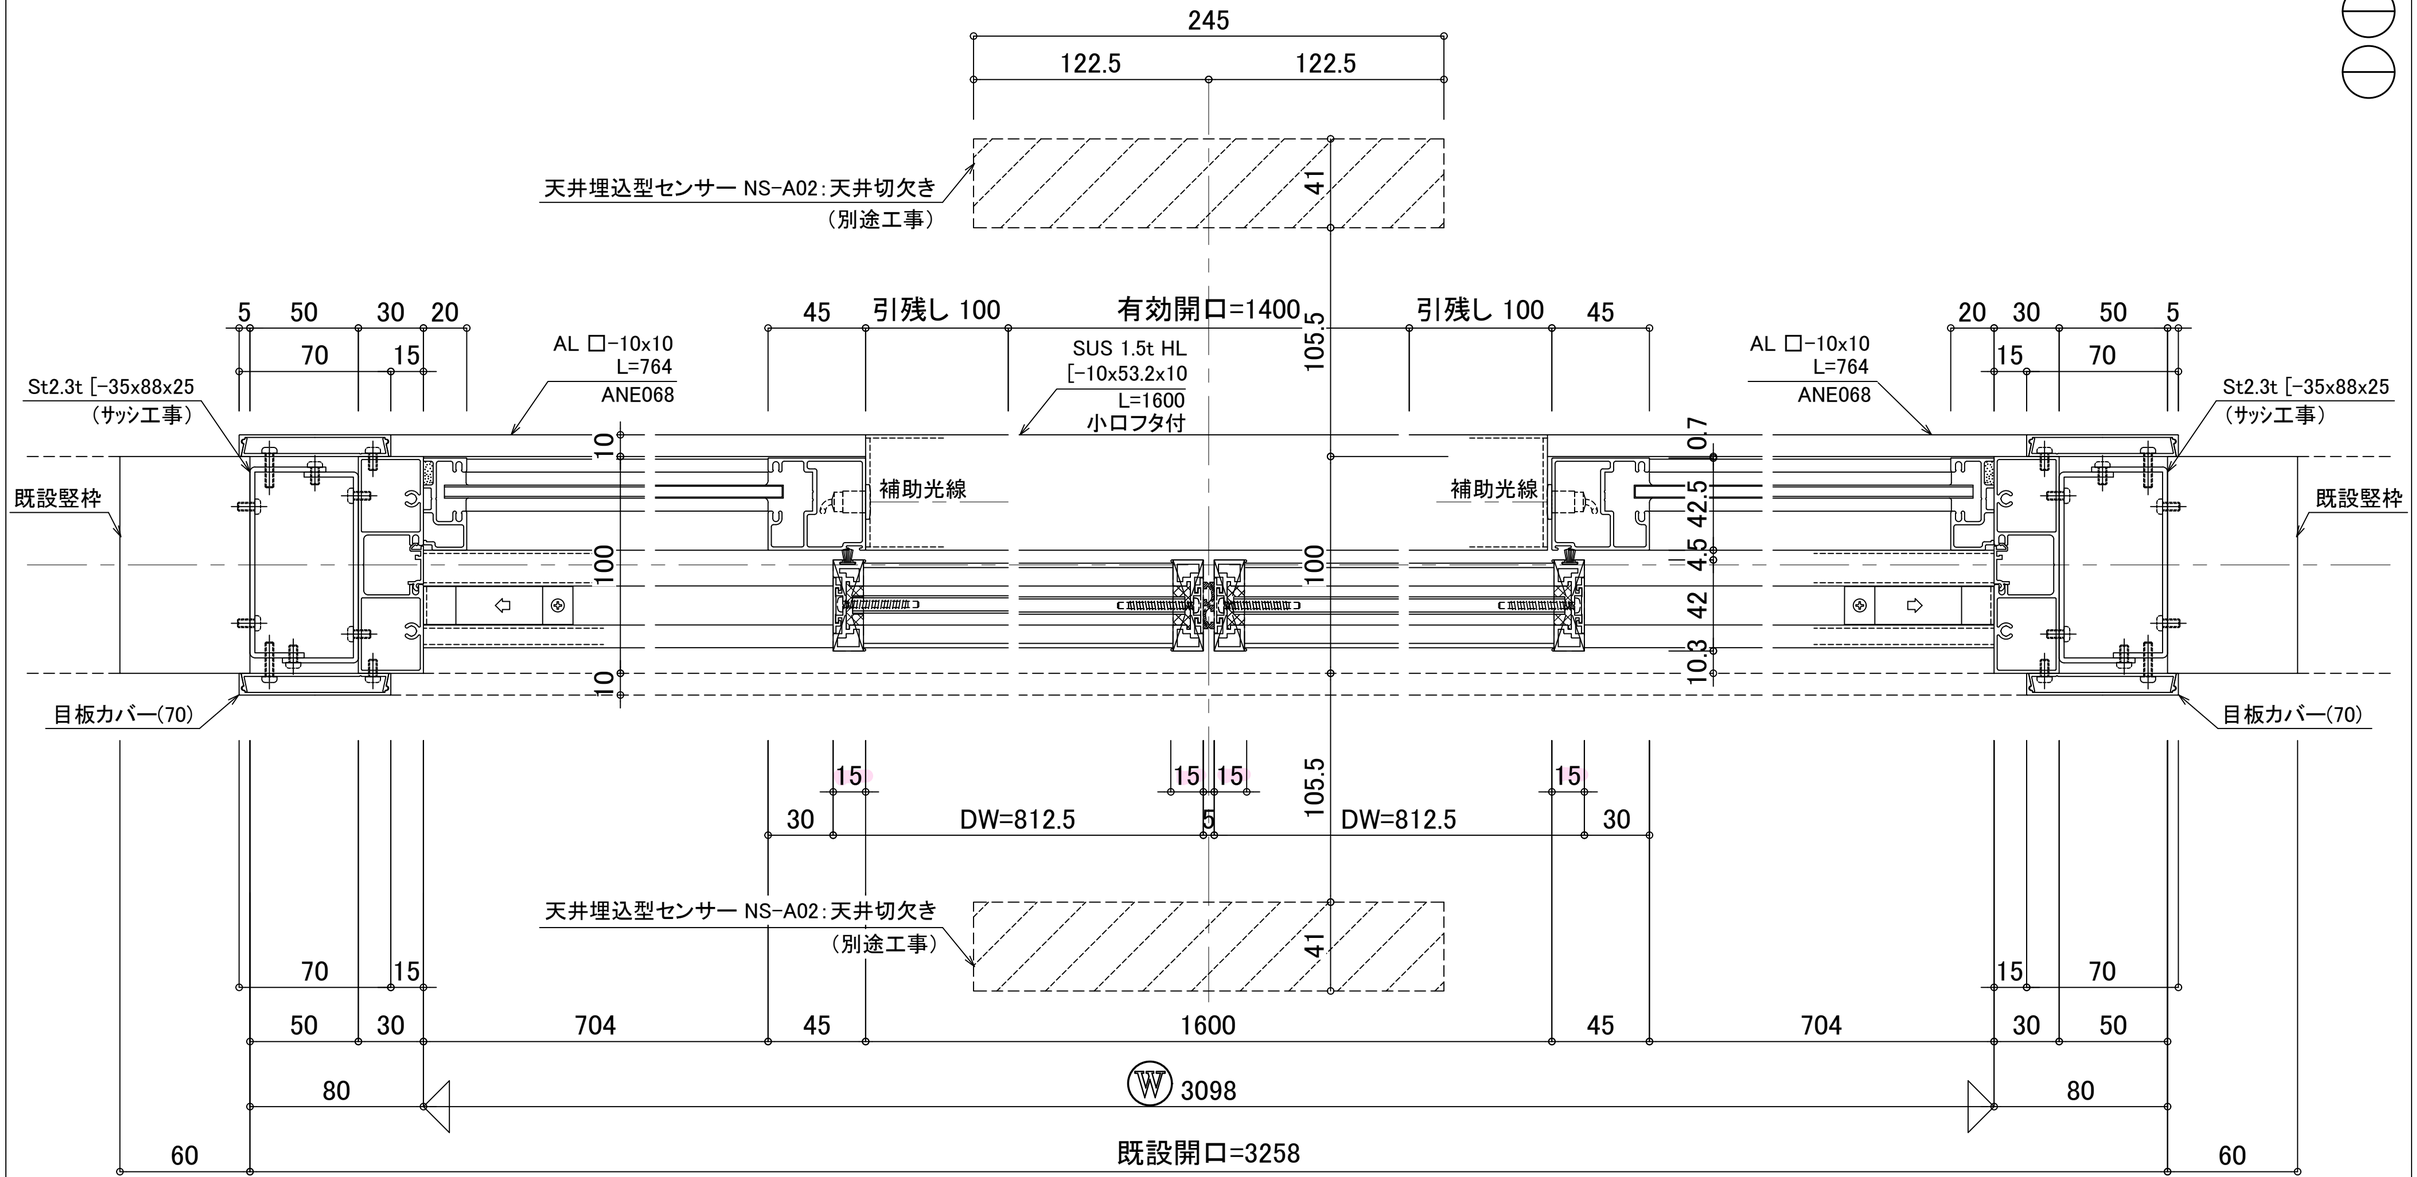


食 堂

改訂	No	改訂日	改訂内容	担当

工事名	相山女学園/星が丘キャンパス 大学会館食堂リニューアル工事	設計監理	株式会社　日建設計　殿	受領		代理店		工番		差替	製図	藤木
図面名	AD-1 詳細図	施工	清水建設　株式会社　殿		年　月　日		昭和フロント株式会社	FDNO.	DATE.		図番	07
								縮尺	1／2	□ A2-100% □ A3-71%	検図	吉田

1
AD

エントランス

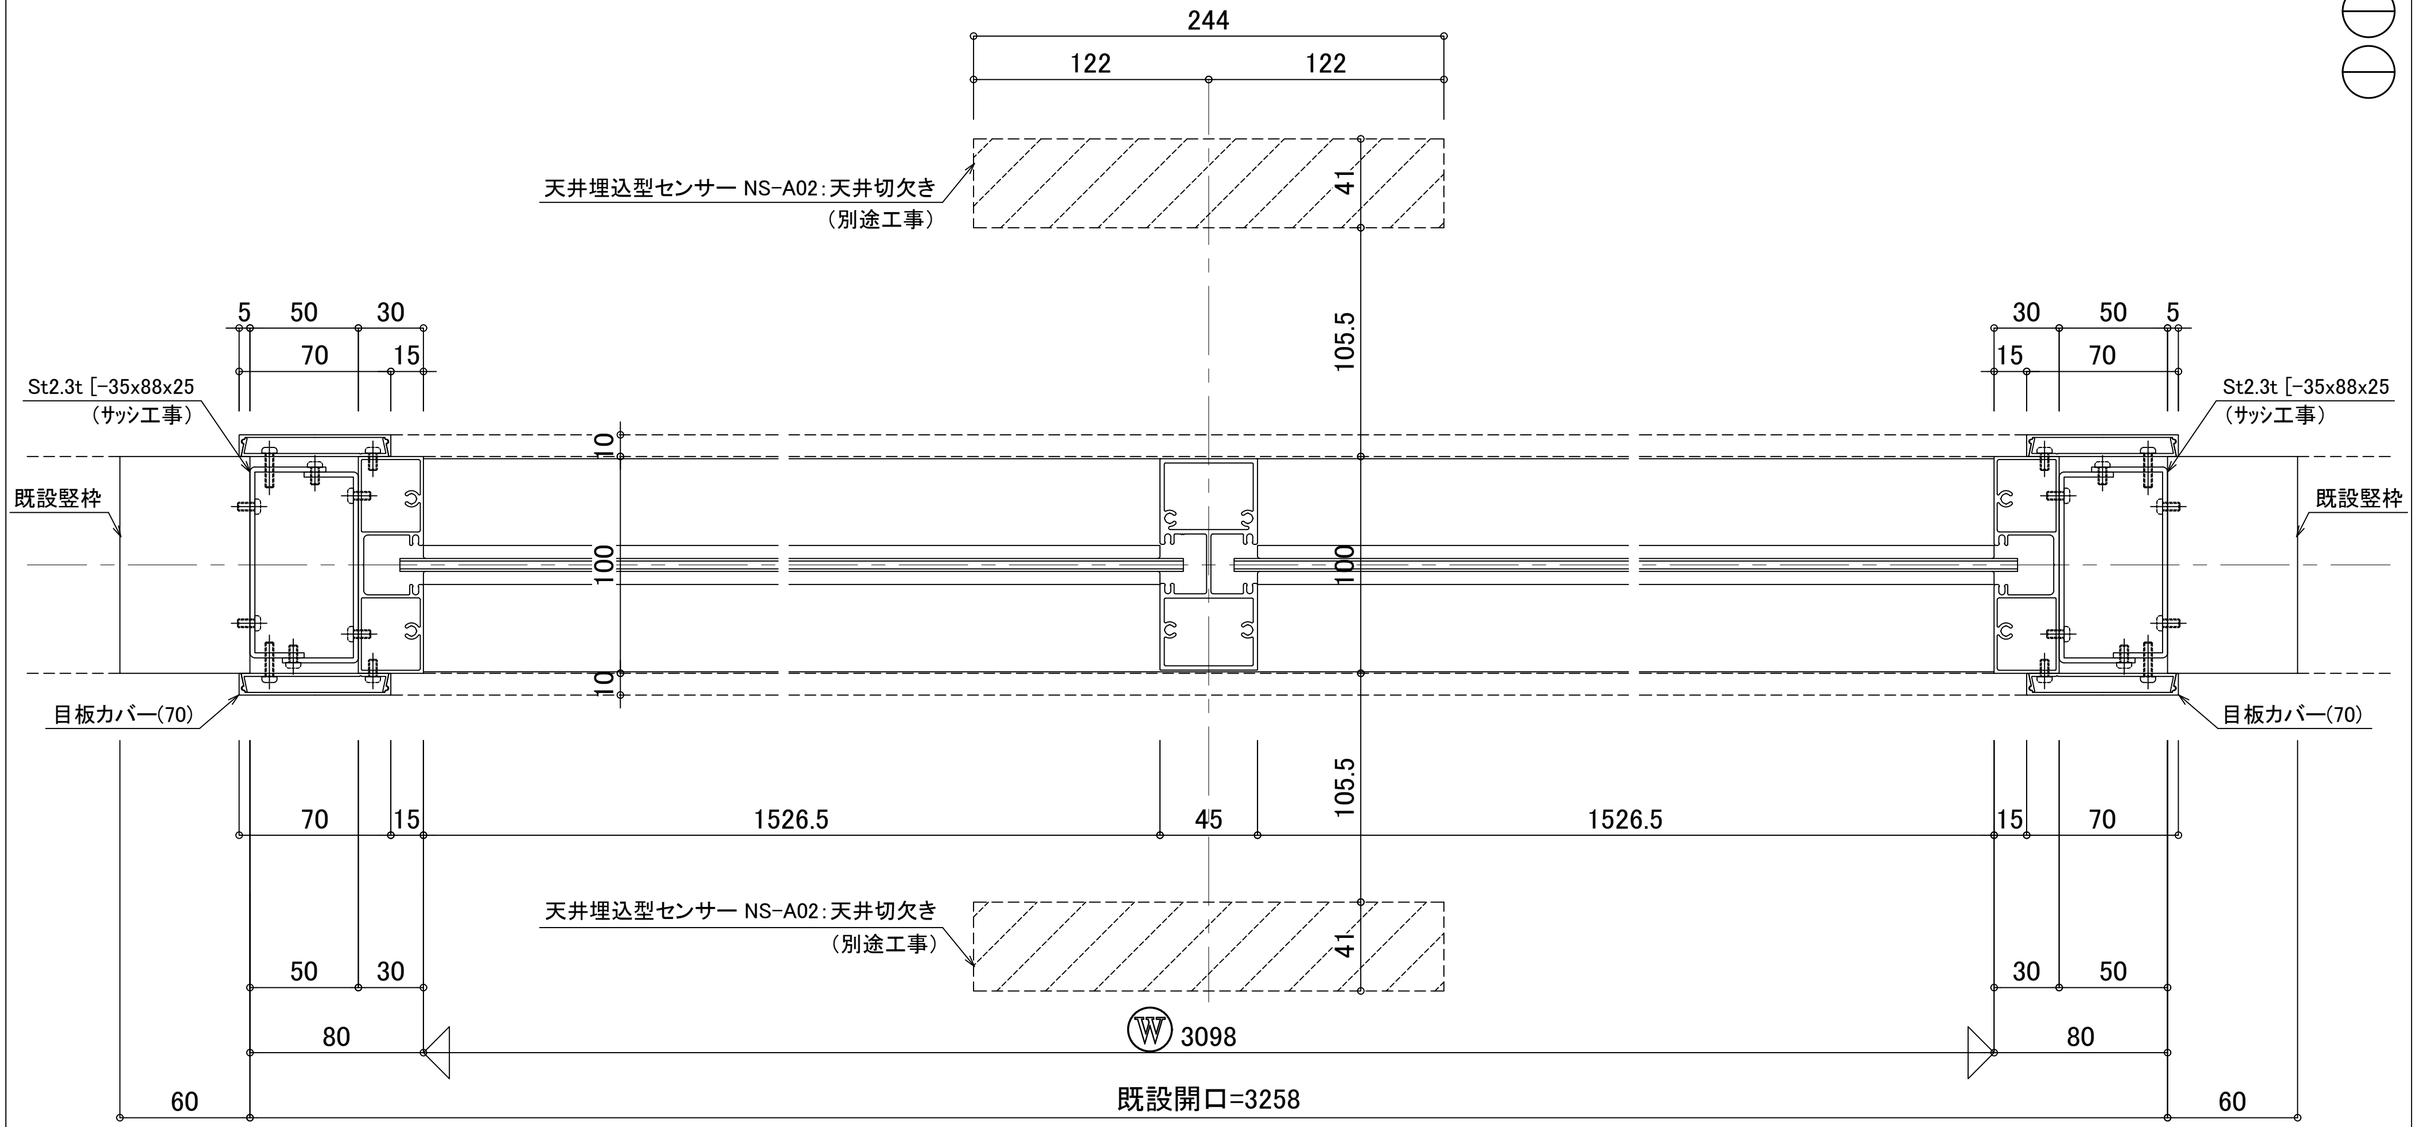

食　堂


欄間部

改訂	No	改訂日	改訂内容	担当

工事名	相山女学園/星が丘キャンパス 大学会館食堂リニューアル工事	設計監理	株式会社　日建設計　殿	受領		代理店		工番		差替	製図	藤木
図面名	AD-1 詳細図	施工	清水建設　株式会社　殿		年　月　日		昭和フロント株式会社	FDNO.	DATE.		図番	08
								縮尺	1／2	□ A2-100% □ A3-71%	検図	吉田

1
AD

エントランス

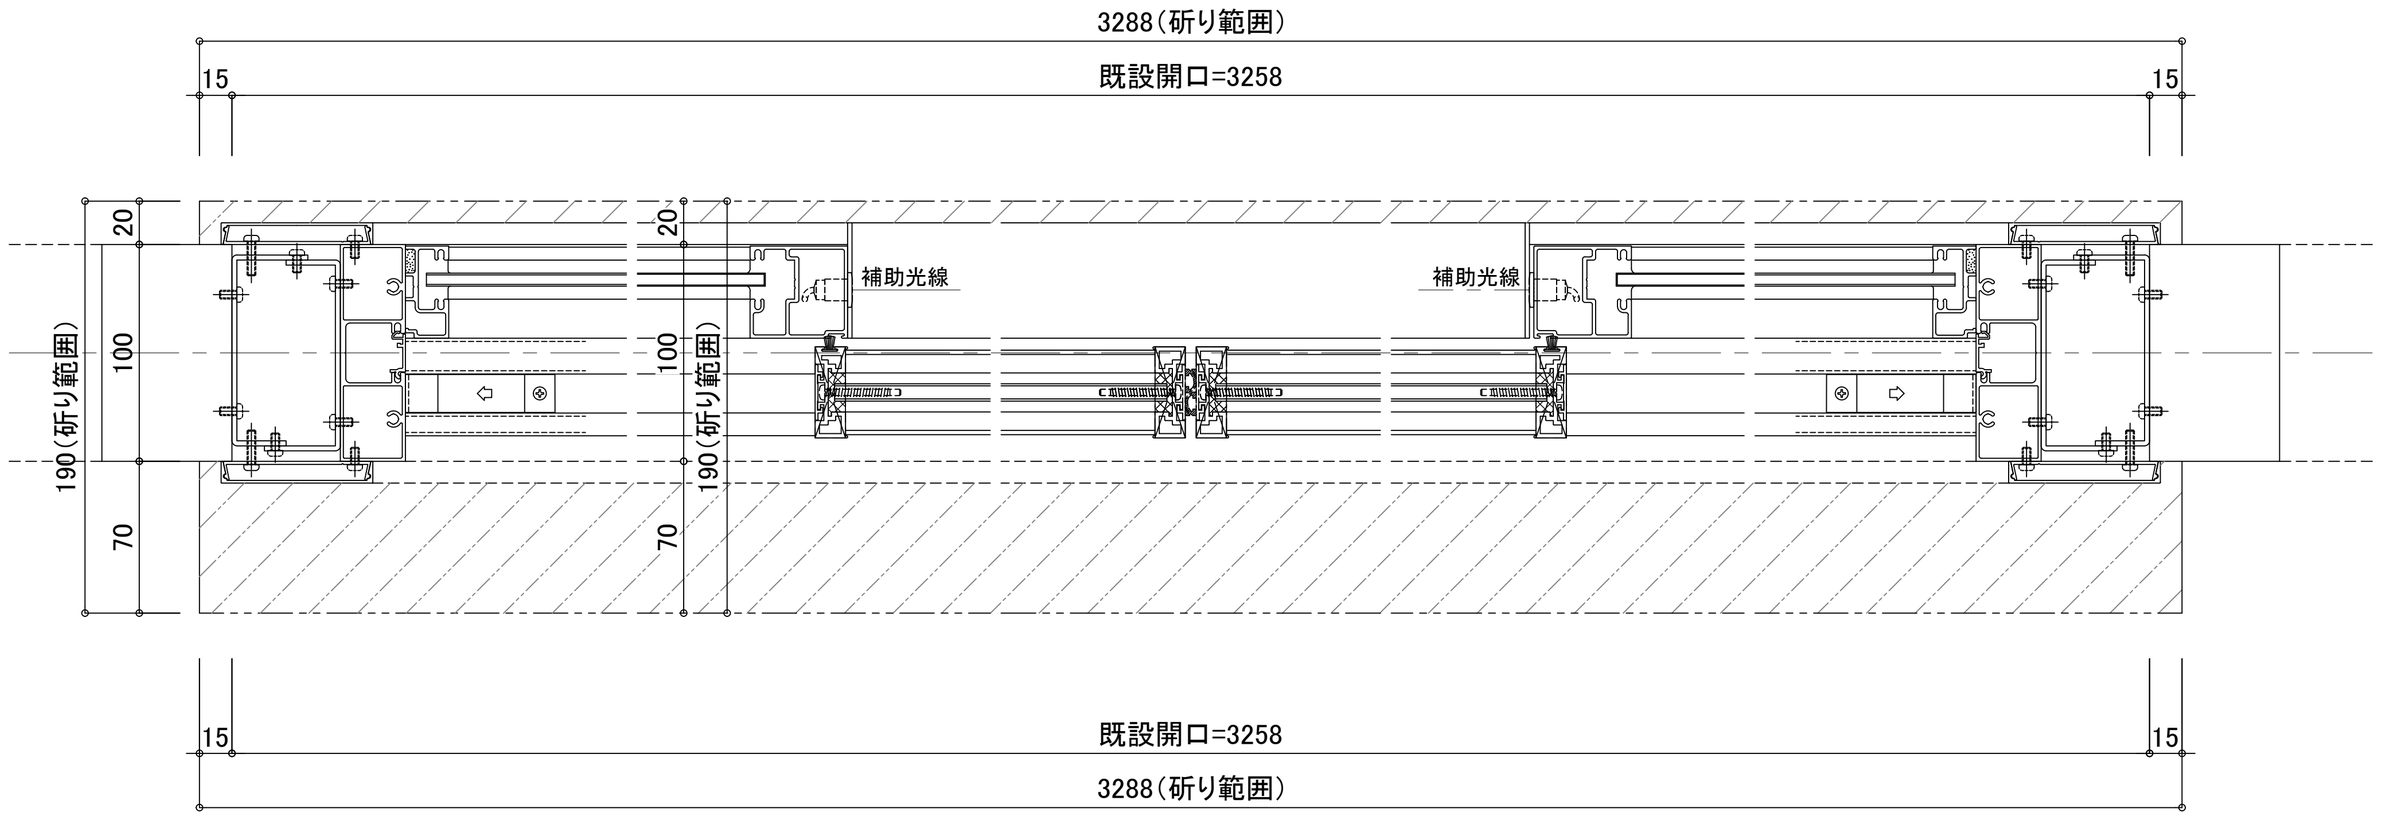

:斫り範囲(別途工事)

食 堂

改訂	No	改訂日	改訂内容	担当

工事名	椙山女学園/星が丘キャンパス 大学会館食堂リニューアル工事	設計監理	株式会社 日建設計	殿	受領		代理店		工番		差替		製図	藤木
図面名	AD-1 詳細図	施工	清水建設 株式会社	殿		年 月 日		昭和フロント株式会社	FDNO.	DATE.				
									縮尺	1/2	□ A2-100% □ A3-71%	検図	吉田	図番 09

センサーは天井埋込型です

NS-A01　N Search

露出型


～より使いやすい、高性能自動ドアセンサー～（NATRUS+e 対応）

型式・名称	NS-A01 N Search
検知特性	動体・静止体検知（近赤外線反射式）
取付高さ※	起動センサーとして使用時：2.0 ～ 4.0m 保護センサーとして使用時：2.0 ～ 3.5m
検知エリア	取付高さ 2.2m 時：幅 2.77m ×奥行 1.62m（参考値）
電源・消費電流	DC12V 120mA 以下
出力信号定格	NET 専用出力
備　考	72 スポット独立のエリア設定機能、1 開閉毎の安全テスト機能、機器トラブルお知らせサイン機能、ドアウェイ監視機能、フルカラー LED 表示、eco モード、雪虫モード、非接触タッチセンサー機能、異型ドア対応機能

※ 設置環境により取付高さが制限される場合があります。




外形図（mm）

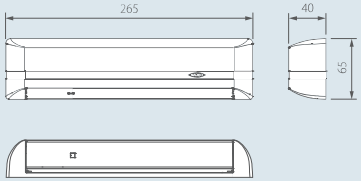

本体質量：300g

検知エリア図　※全72スポット個別に有効／無効設定可能

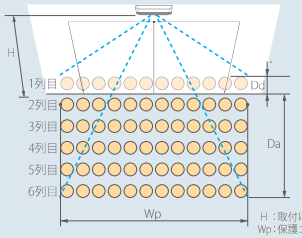

H：取付け高さ
Wp：保護エリア（2列目の）幅寸法
Da：起動エリアの奥行寸法
Dd：ドアエリアの奥行寸法

■検出範囲値表　（mm）

参考値（JIS A 4722に基づく調整実施時）			
H	Wp	Da	Dd
2000	2520	1480	175
2200	2770	1620	200
2500	3150	1830	240
3000	3780	2180	305
3500	4410	2530	365
4000	5040	2880	430

NS-A02　N Search

埋込型


～より使いやすい、高性能自動ドアセンサー～（NATRUS+e 対応）

型式・名称	NS-A02 N Search
検知特性	動体・静止体検知（近赤外線反射式）
取付高さ※	起動センサーとして使用時：2.0 ～ 4.0m 保護センサーとして使用時：2.0 ～ 3.5m
検知エリア	取付高さ 2.2m 時：幅 2.77m ×奥行 1.62m（参考値）
電源・消費電流	DC12V 120mA 以下
出力信号定格	NET 専用出力
備　考	72 スポット独立のエリア設定機能、1 開閉毎の安全テスト機能、機器トラブルお知らせサイン機能、ドアウェイ監視機能、フルカラー LED 表示、eco モード、雪虫モード、非接触タッチセンサー機能、異型ドア対応機能



※設置環境により取付高さが制限される場合があります。

外形図（mm）

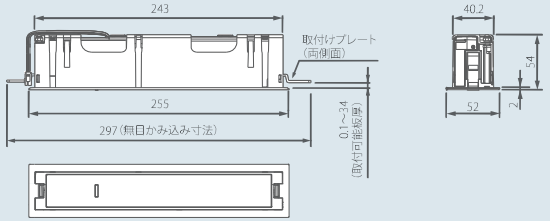

本体質量：300g

7. 検出範囲

7.1. 検出範囲サイズ

⚠注意		本装置は、近赤外線を照射し、検出範囲内床面から反射される近赤外線の光量の変化を検出しています。検出範囲サイズは、当社測定方法による参考検出範囲であり、人（物）の服装（外装）および、床面の色や材質により、近赤外線の反射量が異なるため、検出範囲内に進入しても検出しにくくなることがあります。検出感度などの設定によっても、検出範囲は変動しますので、調整後必ず検出範囲を確認してください。この際、リアルタイムモニタ（「5.4.テスト作動による検出範囲の確認（リアルタイムモニタ機能）」参照）または参照モードをご使用ください。

下表の代表値はドア表面からセンサー取付け面までの奥行距離を80㎜と仮定し、2列目を保護エリアとして調整した場合のドア表面を基準にした寸法を記載しています。ただし、大外調整時はセンサー取付け位置を基準にした寸法を記載しています。

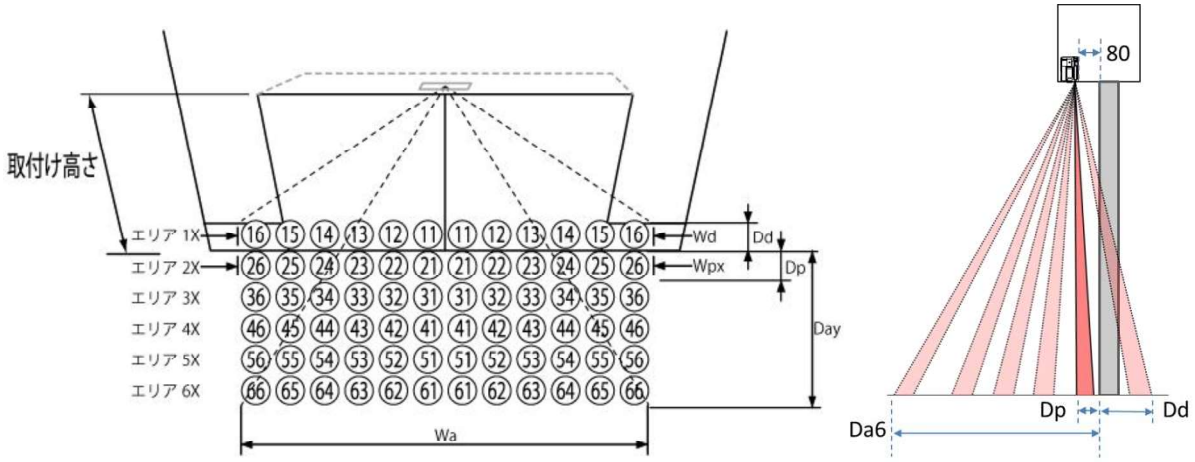


図 7-1 検出範囲

表 7-1 検出範囲値表[単位:mm]

	取付け高さ			2.0m	2.2m	2.5m	3.0m	3.5m	4.0m
代表値	起動エリア	奥行き	Da6	1480	1620	1830	2180	2530	2880
			Da5	1130	1235	1395	1655	1920	2180
			Da4	830	905	1015	1205	1390	1575
			Da3	535	585	650	765	880	995
		幅	Wa	2610	2875	3265	3920	4575	5225
	保護エリア	奥行き	Dp	270	290	320	370	415	465
		幅	Wp12	2520	2770	3150	3780	4410	5040
			Wp10	1995	2190	2490	2990	3490	3985
			Wp8	1600	1760	1995	2395	2795	3195
			Wp6	1135	1250	1420	1705	1990	2270
			Wp4	740	815	920	1110	1295	1480
	ドアウェイエリア	奥行き	Dd	175	200	240	305	365	430
		幅	Wd	2485	2735	3110	3730	4350	4975
大外調整時　センサー取付位置から起動エリア先端までの距離				1725	1895	2155	2585	3015	3445

(C) Nabtesco Corporation　All Rights Reserved.