図面・計画書添付書

工事名

椙山女学園　星が丘キャンパス大学会館食堂リニューアル工事

図面名称	躯体	仕上	設備
	打合図	受領図	受領印用図
ハンガードア製作図	発行日	返却希望日	
施工予定日 2027/02/01			

	発注者			施工部署				生産技術部		設備部	
				現場管理責任者	工事長	主任	担当者	工事長	担当者	工事長	担当者
印				✓ 承認 2026/10/07 金子 冬平				承認 2026/10/07 小山 努			
日付				10.7							

	設計責任者	工事監理者	工事監理担当者									
			意匠		構造		機械		電気			
印		工藤		椙垣								
日付		261016		2026,10,8								

記　事（質疑応答・連絡事項・その他）

椙山女学園星が丘キャンパス　大学会館食堂リニューアル工事

鋼製建具施工図

三和シヤッター工業　㈱

設計監理　：　株式会社　日建設計　殿

施　　工　：　清水建設(株)名古屋支店　殿

	承認期日：　11月　1日
製作納期　50日必要です。	初回納期：　12月　20日

注)製作納期60日(繁忙期)となります。承認期日の遅延が直接納期に影響しますので、お早目のご指示を何卒お願い致します。

出図	チェック図受領	出図	チェック図受領	出図	承諾
出図 26.10.6 設計課					
平 26.10.6 野 / 足 26.10.6 立					

※製作手配後の変更は有償・納期遅延となりますので、ご理解の程お願い致します。

※訂正回数は2回までを目標に図面チェックバック御協力お願い致します。


枠・扉　同時手配を原則としております。
製作にあたりましては、下記の項目の決定が必要となりますので、
受領までに御確認・御決定願います。

確認事項	回答

扉手配の為に、下記事項についてご指示下さい。	
	錠前シリンダーサイド(シ サ 空　　他)
	扉意匠(窓ガラリ形状・サイズ、ガラリ開口面積)
	マスターキープラン

※各建具個別の確認事項については、図面参照願います。


木のタテヨコ貼合寸、検討中。

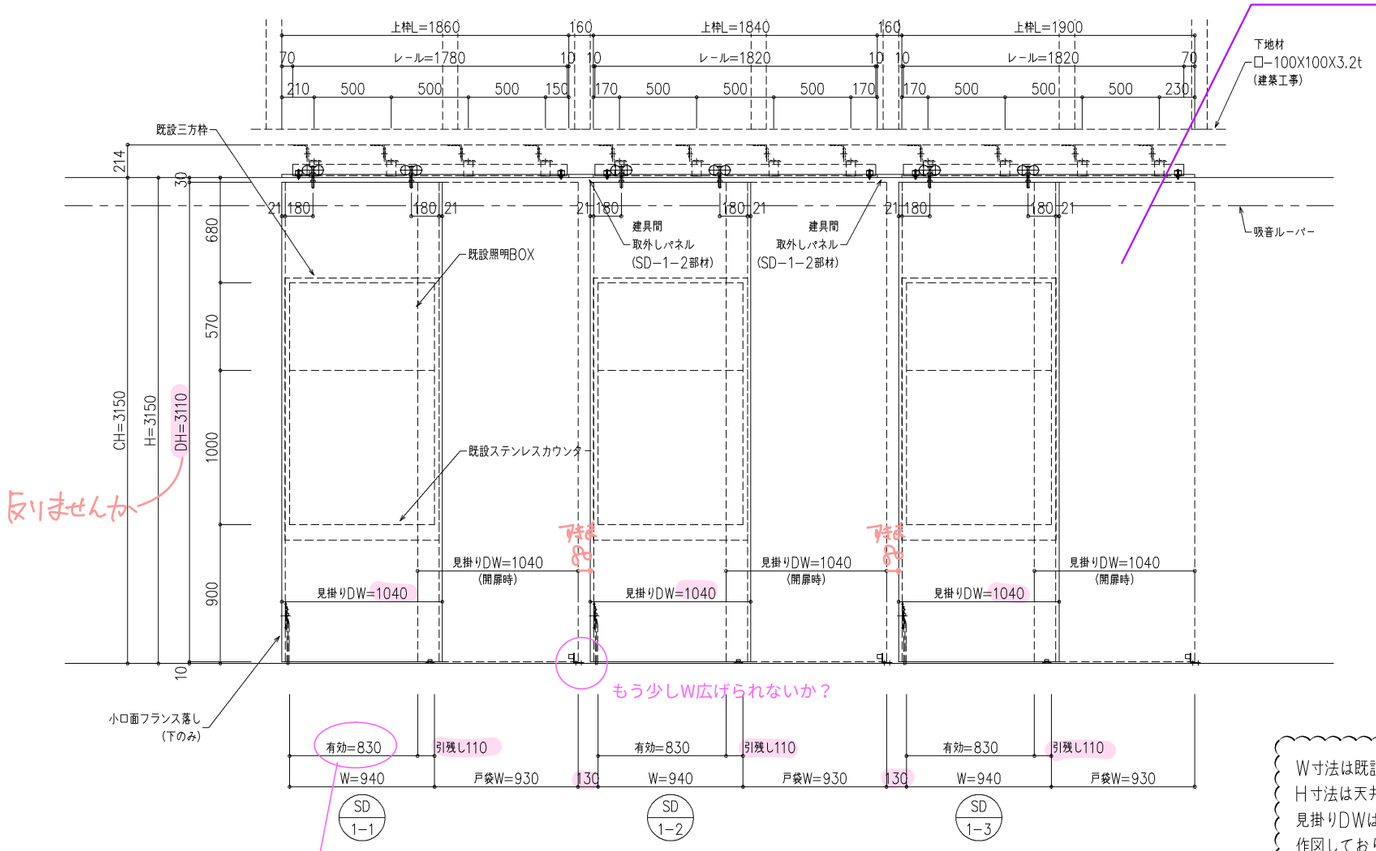

反りませんか

もう少しW広げられないか？

to NS
有効W物理的に限界です

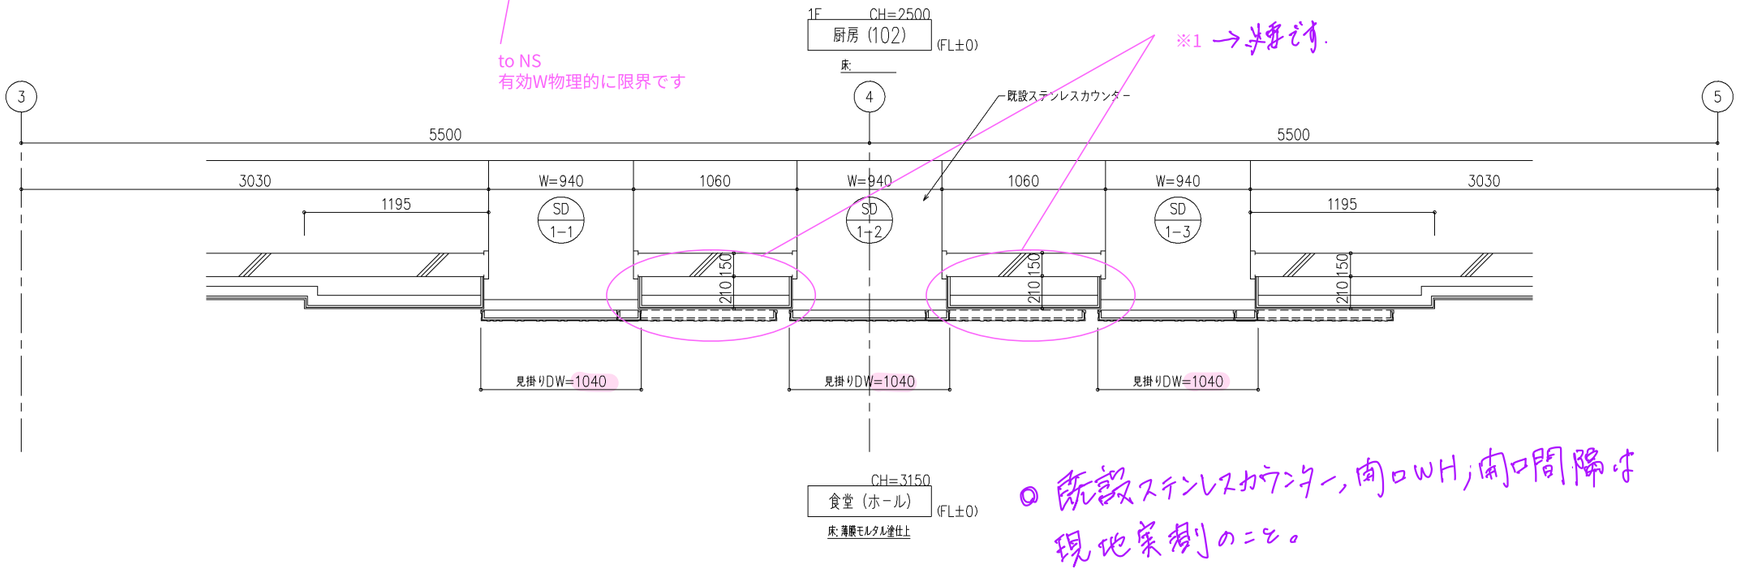

◎既設ステンレスカウンター、南口WH、南口間隔は現地実測のこと。

鋼製引戸（片引き）
枠：1.6t 錆止め (SOPは当社工事外)
扉：1.6t 錆止め (SOPは当社工事外)

符号	勝手	数量	枠性能	充填材	防火区分
SD 1-1	R 1 / L 0	1	ST		指定なし
SD 1-2	R 1 / L 0	1	ST		指定なし
SD 1-3	R 1 / L 0	1	ST		指定なし
ガラリ	-		ガラリタイプ		
ガラス	-		窓タイプ		

金具品名	メーカー・品番	1ヶ所数量	備考
ﾊﾝｶﾞｰﾚｰﾙ	ﾀﾞｲｹﾝ #4 HR	1	L=1820
複車	ﾀﾞｲｹﾝ #4 4WH-B	2	
天井受下	ﾀﾞｲｹﾝ #4 BOX	4	
ｶﾞｲﾄﾞﾛｰﾗｰ	NS GR-30Z	1	
戸当り	ﾀﾞｲｹﾝ #3 CS	2	上部
面付用戸当り(戸尻)	ﾘｮｰﾋﾞ SWTOA-L28N	1	
ﾌﾗｽ落し	ｼｱﾀﾞﾝ DE-5VN 下	1	下のみ
下ｶﾞﾏ	ｼｱﾀﾞﾝ DB-79	1	

製品コード：999999　　枠：ノックダウン

扉重量（1枚）
約180 kg/枚

手動で開放できますか？
吊り金物対応できますか？

W寸法は既設三方枠を基準
H寸法は天井高さを基準
見掛りDWは設計図部分詳細合わせて
作図しております。

貼物重量ご指示願います。
木パネルt12 ・・・9.6kg/m²
オーク材t9 ・・・6.8kg/m²
上記にて重量算出しております。

引手必要でしょうか。
部分詳細（設1－24）の小口手掛けより
引手なしとしております。


錠有無ご確認願います。
戸先フランス落しで作図しております。

錠、フランス落し共不要

製作手配後の変更は増額対象となり、更に製作日数が必要となります。

工事名 【R】椙山女学園星が丘キャンパス 大学会館食堂リニューアル工事		受領 年月日	設計 林 秀樹	営業 中部B営業一課 下賀 陸史	尺度 1/2, 1/20
設計監理 殿	施工 清水建設(株) 名古屋支店 殿		三和シヤッター工業株式会社 www.sanwa-ss.co.jp		図番 001
					設計番号 WND-0070375401-01

SD 1-3
SD 1-2
SD 1-1

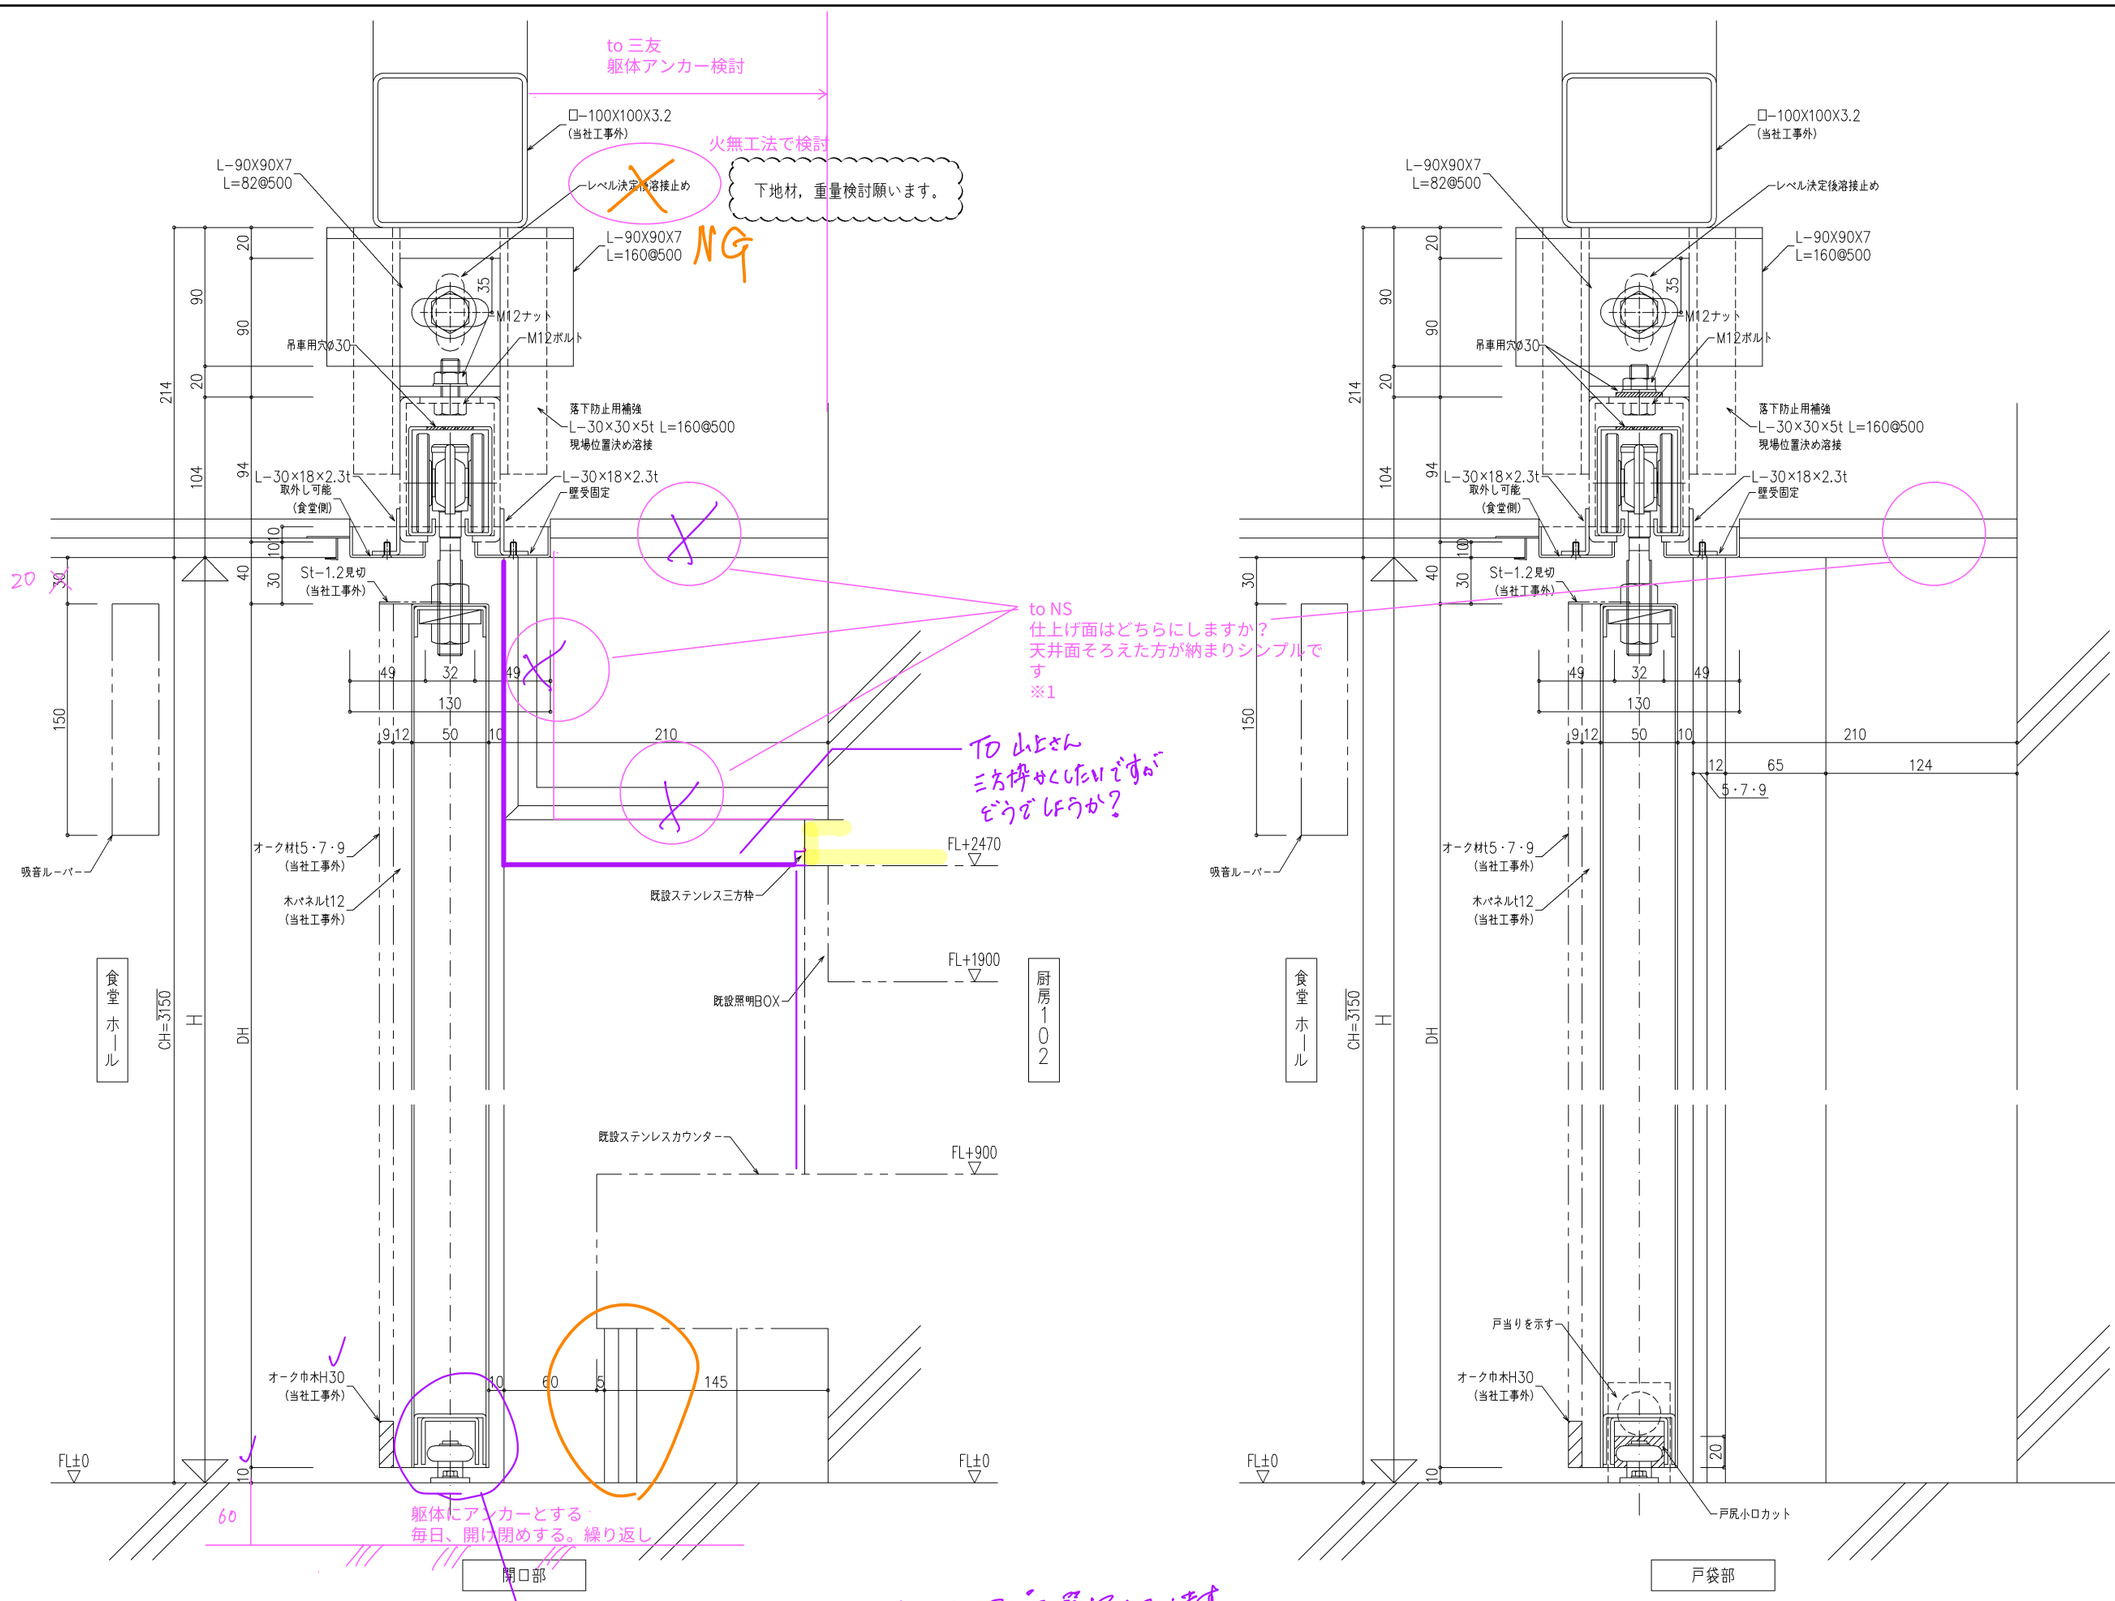

製作手配後の変更は増額対象となり、
更に製作日数が必要となります。

工事名 【R】椙山女学園星が丘キャンパス　大学会館食堂リニューアル工事		受領　年　月　日	設計 林　秀樹	営業 中部B営業一課 下賀　隆史	尺度 1/2, 1/20
設計監理　殿	施工 清水建設(株)　名古屋支店　殿		三和シヤッター工業株式会社 www.sanwa-ss.co.jp		図番 002 / 設計番号 WND-0070375401-01

SD 1-3
SD 1-2
SD 1-1

厨房（102）

実測

940　1060

30　30　30

既設ステンレス三方枠

15　150　180

65　12　9　30　65　12　9　30

側板 オークUCt9

210　124　195

65

5・7・9　12　10　10

100　71　50　12　19

5・7・9

端部固定パネルを示す

上枠ラインを示す

上部壁受固定パネル
（SD−1−2部材）

上部取外しパネル
（SD−1−2部材）

30

21　DW　21

見掛りDW

5・7・9　12　DW　12　5・7・9

50　有効開口　引残し 110　50

見掛りDW

50　W　戸袋W　130　W

SD 1−1　SD 1−2

60　80　20　30

160

上枠 L　上枠 L

食堂（ホール）

to NS
中間のこの出っ張りは必要でしょうか？
※1
↳ 必要です。
扉を閉めた時は
木の壁になる様にしたいです。

引残しを極力小さくできないか相談
（めん類カウンター利用時、じゃまにならない様）

扉を閉めても金物が
見えない仕様、スガツネ
フロアレール
参1−24参照

フランス落し部切欠

90　90　298

5・7・9　12　18.5

50　W

共通 フランス落し納まり

フランス落し部切欠

フランス落し

40　25　25　12

5・7・9

戸当り部切欠

50　45　12

5・7・9

5・7・9　12　17.5　35　12.5

30　65

共通 戸当り納まり

5・7・9

12　80

30　65　6

17.5　35　12.5

戸当り部切欠

70　65

10

扉吊込用小ロカット
h20


SD 1−2

SD 1−1

製作手配後の変更は増額対象となり、更に製作日数が必要となります。

工事名 【R】椙山女学園星が丘キャンパス　大学会館食堂リニューアル工事		受領　年　月　日	設計 林　秀樹	営業 中部B営業一課 下賀　隆史	尺度 1/2, 1/20
設計監理　殿	施工 清水建設（株）　名古屋支店　殿		三和シヤッター工業株式会社 www.sanwa-ss.co.jp		図番 003
					設計番号 WND-0070375401-01

厨房（102）

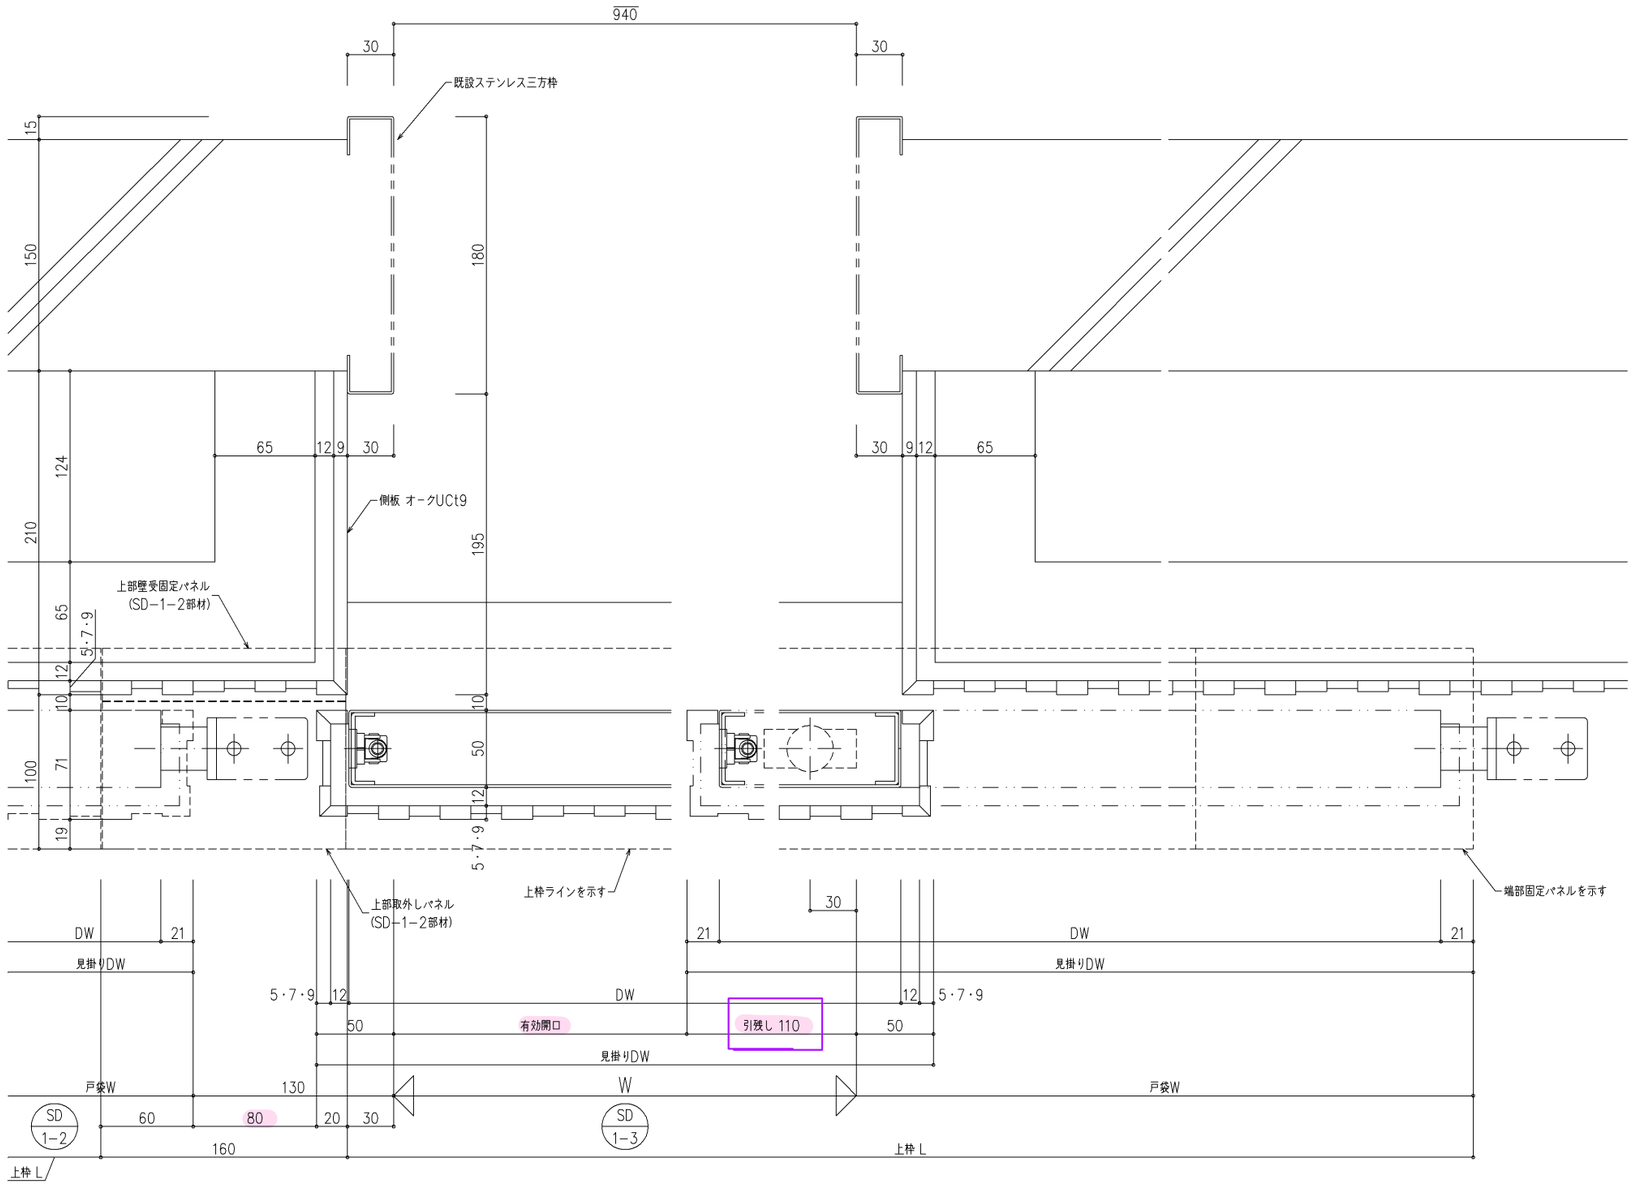


食堂（ホール）


製作手配後の変更は増額対象となり、
更に製作日数が必要となります。


工事名 【R】椙山女学園星が丘キャンパス　大学会館食堂リニューアル工事		受領　年　月　日	設計 林　秀樹	営業 中部B営業一課 下賀　隆史	尺度 1/2, 1/20
設計監理 殿	施工 清水建設（株）　名古屋支店 殿		三和シヤッター工業株式会社 www.sanwa-ss.co.jp		図番 004
					設計番号 WND-0070375401-01


SD 1−3
SD 1−2

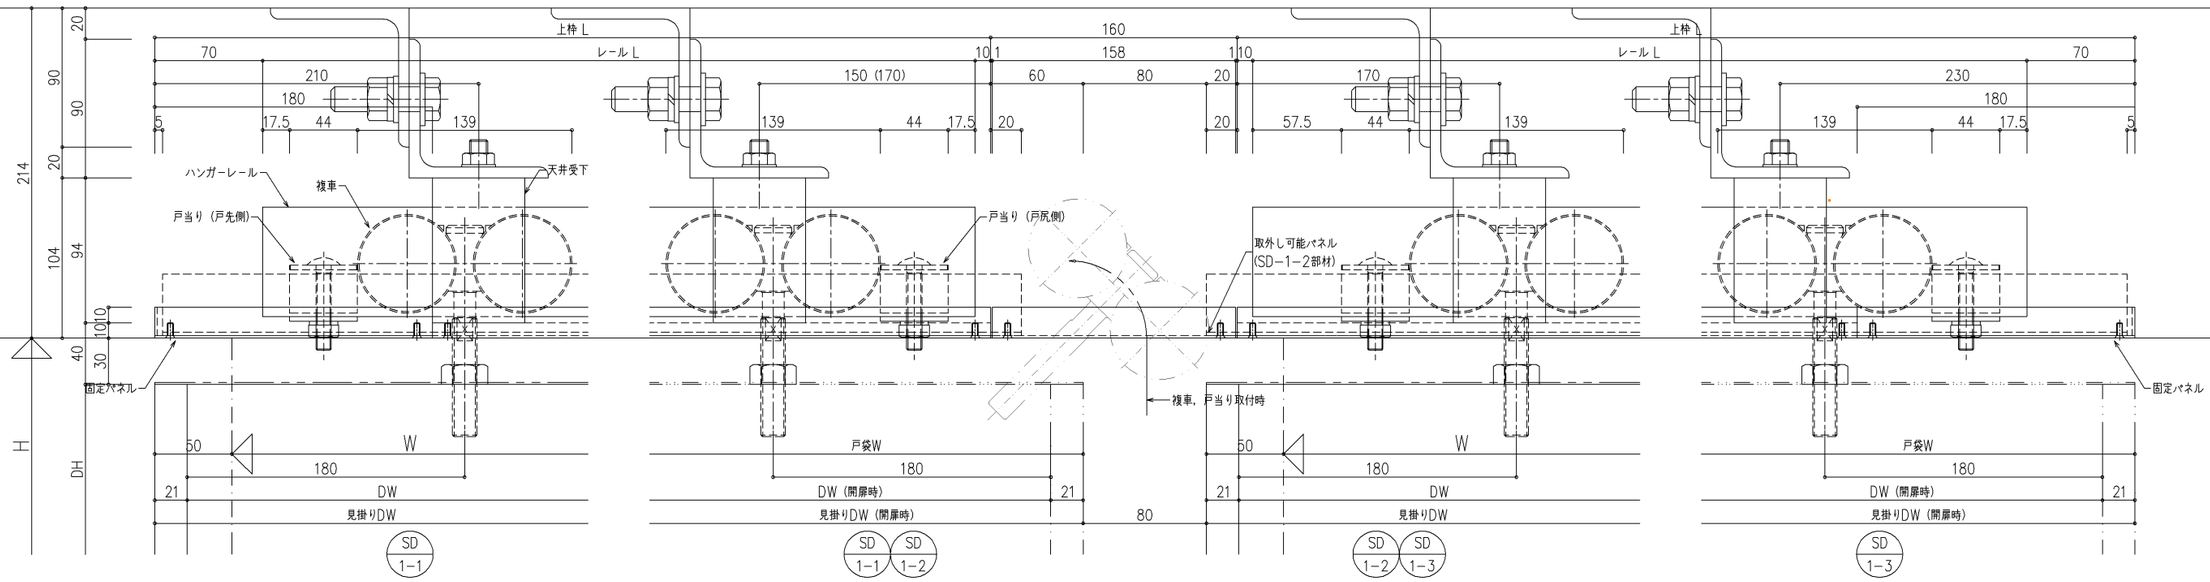



（ ）内寸法はSD−1−2を示す

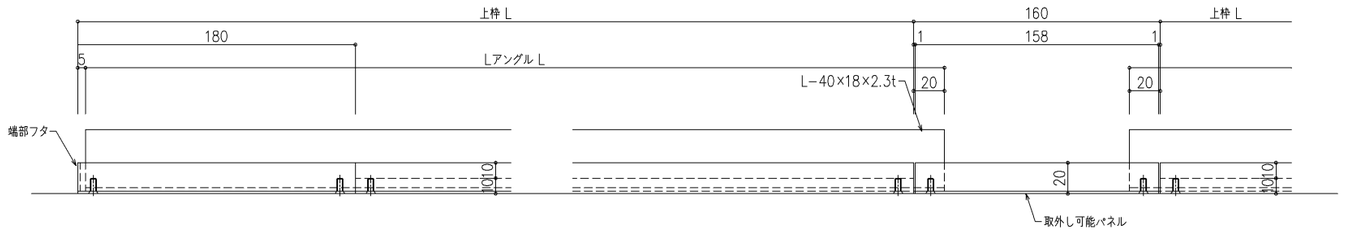

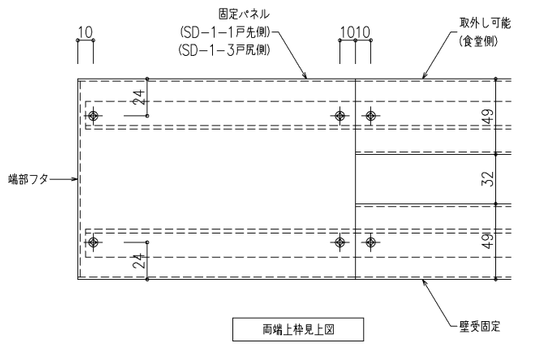

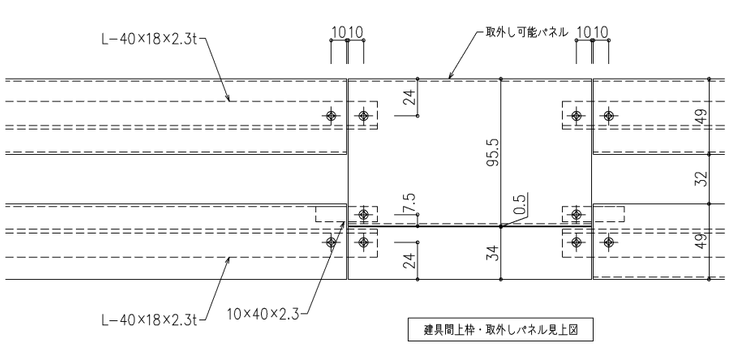

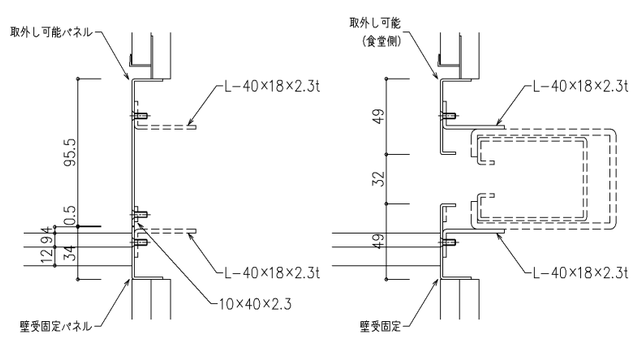

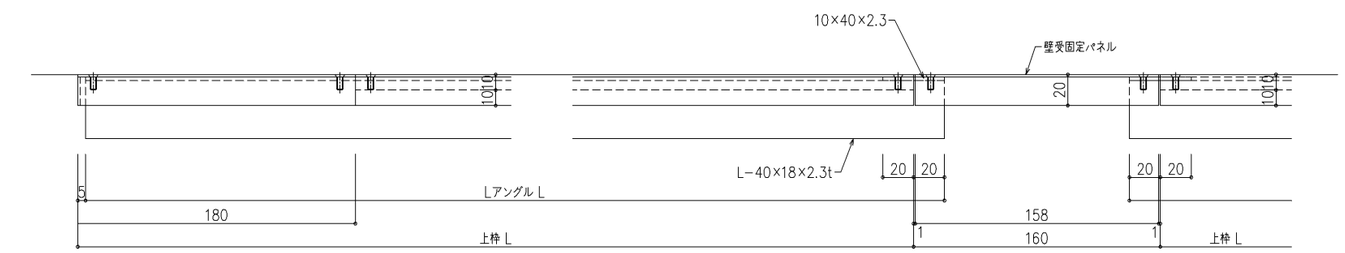

製作手配後の変更は増額対象となり、更に製作日数が必要となります。

工事名 【R】椙山女学園星が丘キャンパス　大学会館食堂リニューアル工事		受領　年　月　日	設計 林　秀樹	営業 中部B営業一課 下賀　隆史	尺度 1/2, 1/20
設計監理 殿	施工 清水建設（株）　名古屋支店 殿		三和シヤッター工業株式会社 www.sanwa-ss.co.jp		図番 005
					設計番号 WND-0070375401-01

SD 1−3
SD 1−2
SD 1−1

壁記号凡例
L 床～天井
L スラブへスラブ
天井内 間仕切
MT：薄塗モルタル塗
木 ：木パネル t5・7・9
LW1 12.5+12.5 LGS 一般壁 GB-R t12.5+GB-R t12.5
LW2 12.5+12.5 LGS 一般壁 GB-R t12.5+GB-R t12.5
LW3 12.5+12.5 22 一般壁 GB-R t12.5+GB-R t12.5
LW4 6+6 LGS 一般壁 FK t6.0+FK t6.0

全体を右に
←
M通りとO通りのカーテンは什器移動無で閉められるように

toNS 壁字からL字へ変更の壁位置ご指示ください

to NS 柱前面は実同様カウンター縁切りで宜しいですか？ to 現場 仕上げ代確認

to 現場、サッシ枠にかぶる？

to 現場、サッシ方立ピッチ確認

腰壁H不明

カウンター H720

ロールスクリーンBOX:St PL1.6加工 A-BE 板面PL取り外し加工

アルミルーバー@75

to NS 現場運用図の文字は23角、絵は27角です

to PDS 座席番号ふる 各エリア毎の席数も 厨房側開口用途記入 壁モルタルアートの仕上げ厚記入

to NS タイル割の基準でいいですか？

to NS カーテンの運用確認願います 吸音ルーバーの範囲も？ 後日に干渉します

to NS この通路だけ狭い box床→300移動しませんか？ 他エリアカーテン

to 現場 基本、ルーバー直張り、壁面凸凹調査、ずりも

to NS ガラリ開閉とは？

既存ガラリ片開戸が開くように

医設テラゾータイル張りの上、薄塗モルタル塗

to NS 袖前に出してルーバーとそろえますか？

500開口変更

メラミンポストフォーム カウンター H800

壁小口：木パネル

to NS ガラリ交換する必要ありますか？ または、ルーバーが取付け可能 納まりとすることが目的です か？ 開口率は？

toNS 分離会で質疑した通り既存塗装 造作家具にてメンテナンスできるようにします

よろしくお願いします

to 現場 扉残存か確認

to NS 仕上げできない 金物としますか？

券売機

現地確認の上、調整します。

to NS現状は鉄板にて塞がれています いかがしましょうか

さや管を取り外して下膳台新設ください

屋内（377席）
屋外（ 69席）
合計（446席）
手洗（ ）

223+123=376(▲1)…ok
+30 ~~346(▲31)~~

to NS 座席数チェックお願いします

薄塗り12.5としてもレベル調整必要、特に既存建具廻り

KEY PLAN

打合図 '26.09.18

設計図発行日 '26.03.27

ボード略号凡例

略号	内容
GB-R	石膏ボード
GB-R-H	普通硬質石膏ボード
GB-S	シージング石膏ボード
GB-F	強化石膏ボード
GB-L	石膏ラスボード
GB-D	化粧石膏ボード
GB-NC	不燃規格石膏ボード、不燃化粧石膏ボード
GB-P	吸音あなあき石膏ボード
GB-PD	化粧石膏吸音ボード
GB-R-Hc	吸放湿石膏ボード
K	けい酸カルシウム板
KB	化粧けい酸カルシウム板
RB	ロックウール吸音板

		食堂（西側） CH=3,150 FL-60	食堂（ホール） CH=3,150 FL-60
床	仕上	既設テラータイル張りの上薄塗モルタル塗 レベル調整モルタルの上磁器質タイル張 FL±0	床 仕上 M仕 FL±0
	下地	コンクリート	下地 コンクリート
巾木		不燃調整の上 厳制巾木 H40	巾木 不燃調整の上 厳制巾木 H40
壁	仕上	吸音ルーバー 金PL-BOT(下地クリフランチ)不燃壁一重GL張 future壁	壁 仕上 木パネル 金PL-BOT(下地クリフランチ)不燃壁一重GL張ふかし壁
	下地	軽量鉄骨	下地 軽量鉄骨
天井	仕上	CW-H17	天井 仕上 CW-H17
	下地	GB-R(12.5下地)PP+吸音ルーバー	下地 GB-R(12.5下地)PP+吸音ルーバー
廻縁		型記載	廻縁 —
特記		カウンター、西方枠・三方枠共塗装、ストリングスカーテン＋横払カーテンレール、アルミルーバー＋ロールスクリーン	特記 手洗いカウンター（設備工事）・鏡

記号	内容	C	ストリングスカーテン
	保留を示す		
	床レベル（FL基準）		
	壁ボード目地		
	既存（壁・柱）を示す		
	既存 を示す		

改訂履歴		改訂日	改訂ヶ所	改訂理由
	第1回改訂			
	第2回改訂			
	第3回改訂			
	第4回改訂			
	第5回改訂			

配布ルール
1 変更の場合はこの原図を変更し、改訂履歴を明記する。
2 原図に配布予定先を記入する。
3 変更の都度、全部の配布予定先にコピーを配布する。
4 変更図（コピー）を受領したら旧版は自主廃棄する。

配布予定業者			

壁記号凡例
L 床～天井
L スラブ～スラブ
天井内 懐寸
MT：薄膜モルタル塗
木 ：木パネル t5・7・9
LW1
12.5+12.5 LGS
一般壁
GB-R t12.5+GB-R t12.5
LW2
12.5+12.5 LGS
一般壁
GB-R t12.5+GB-R t12.5
CH 3,150
食堂（ホール）
FL-60 FL ±0
西と同様
to NS
仕上げできない金物ありますか？
to NS
建物、スロープ共通
勾配チェックお願いします
to NS
壁取合いの巾木が見切り不要ですか？
方針とタイル割とご相談の上、
ビニル巾木ありでお願いします。
Start
Last
to NS
デッドスペースで宜しいですか？
階段横だけふかせば広く使えます
既存壁面・赤タイル
↳ふかし壁OK
to NS
壁取合いの巾木が見切り不要ですか？
日地棒（意1-20）参照
プロジェクターで投影する際に段差が邪魔になるので、ふかし壁ありのままで。
床下パッケージ空冷機 PAC-1α-1 立梅のため目立たない様、机下に配置、入れないか？
食堂トレー（おぼん）サイズが置ける様、275以上確保。トレー W370×D270
コナー金物 19ミリ下がりを内容反映のこと
KEY PLAN
1/2
2/2
打合図 '26. 09. 18
設計図発行日 '26. 03. 27

ボード略号凡例

略号	内容
GB-R	石膏ボード
GB-R-H	普通硬質石膏ボード
GB-S	シージングGL石膏ボード
GB-F	強化石膏ボード
GB-L	石膏ラスボード
GB-D	化粧石膏ボード
GB-NC	不燃積層石膏ボード、不燃化粧石膏ボード
GB-P	吸音あなあき石膏ボード
GB-PD	化粧石膏吸音ボード
GB-R-Hc	吸湿湿石膏ボード
K	けい酸カルシウム板
KB	化粧けい酸カルシウム板
RB	ロックウール吸音板

		食堂（東側） CH=3,150 / CH=7,700	基準レベル FL-60 / 仕上レベル FL+10 / +320 / +800
床	仕上	敷張りL.A.	
	下地	既設テラゾータイル張りの上薄膜モルタル塗	
巾木		既設躯体の上 敷張巾木 H40	
壁	仕上	GB-R(17.5下地)PEP+塗装ミルーバー	
	下地	既設躯体の上 敷張巾木 H40	
天井	仕上	GB-R(17.5下地)PEP+塗装ミルーバー	
	下地	GB-R(12.5下地)+T-25@ 415, 910 張り	
廻縁		既存躯体	
特記		-	

		食堂（ホール） CH=3,150	基準レベル FL-60 / 仕上レベル FL±0
床	仕上	M1	
	下地	コンクリート	
巾木		不燃調整の上 敷張巾木 H40	
壁	仕上	木パネル	
	下地	既設GB-R(12下地)ファンファン用壁一部GB張りボード張り	
天井	仕上	既設GB-R(12下地)ファンファン用壁一部GB張りボード張り	
	下地	既存躯体	
廻縁		DR 117	
特記		GB-R(12.5下地)PEP+塗装ミルーバー	
		手元リカウンター（設備工事）・蔵	

チェック項目	済	他
• FLLの埋め込み		• ガス、ヨ（ドラフター、ロ）の為が
• 方向、ゴボラフ		• ①N、A字、②GL金属板（個人
• フロアーリング		• ①GL金属ボックス金属個人
• インサート・ルーフドレーン（打込み金物）		• 引張り金物、アンカー金物・個人
• 断熱工事		• プロットの位置（点、天井、壁下、壁）
• ビニール幅金、個人（押ボタン、ライマ、ガ）		• 断熱材の打込み
• 排煙窓に、注意書き		• 防犯設備・仕様目標
• 設備の指定方、金ぬり方、足場用アンカー		• 有害のSFD埋め込み（マグネット入）
• 海打用（打設不可）		•
• 断熱工法（打設不可箇所）		•
• 打合いスカン・報打		•

凡例
<階高> 2FL 4,950 1FL
<室名 記号> 天井高さ / 室名 / 敷仕上幅 / 床仕上幅 / 特記事項
<開口 記号> H 開口寸法 高さ / 符号 建具符号 / h 基準面より建具下端の上端までの高さ
●●…扉の開き優先を示す。

記号	内容	C	ストリングスカーテン
	保留を示す		
	床レベル（FL基準）		
	壁ボード目地		
	既存（壁・柱）を示す		
	既存 を示す		

改訂履歴	改訂日	改訂ケ所	改訂理由
第1回改訂			
第2回改訂			
第3回改訂			
第4回改訂			
第5回改訂			

配布ルール
1 変更の場合はこの原図を変更し、改訂履歴を明記する。
2 原図に配布予定先を記入する。
3 変更の都度、全部の配布予定先にコピーを配布する。
4 変更図（コピー）を受領したら旧版は自主廃棄する。

配布予定業者				承認	審査	作成
				現場管理責任者		担当者
				受領日		

梢山女学園星が丘キャンパス大学会館食堂リニューアル工事
1階平面詳細図-2/2
縮尺 A1：1/50 A3：1/100 '26. 09. 16
清水建設株式会社名古屋支店
仕上－02




Noodle