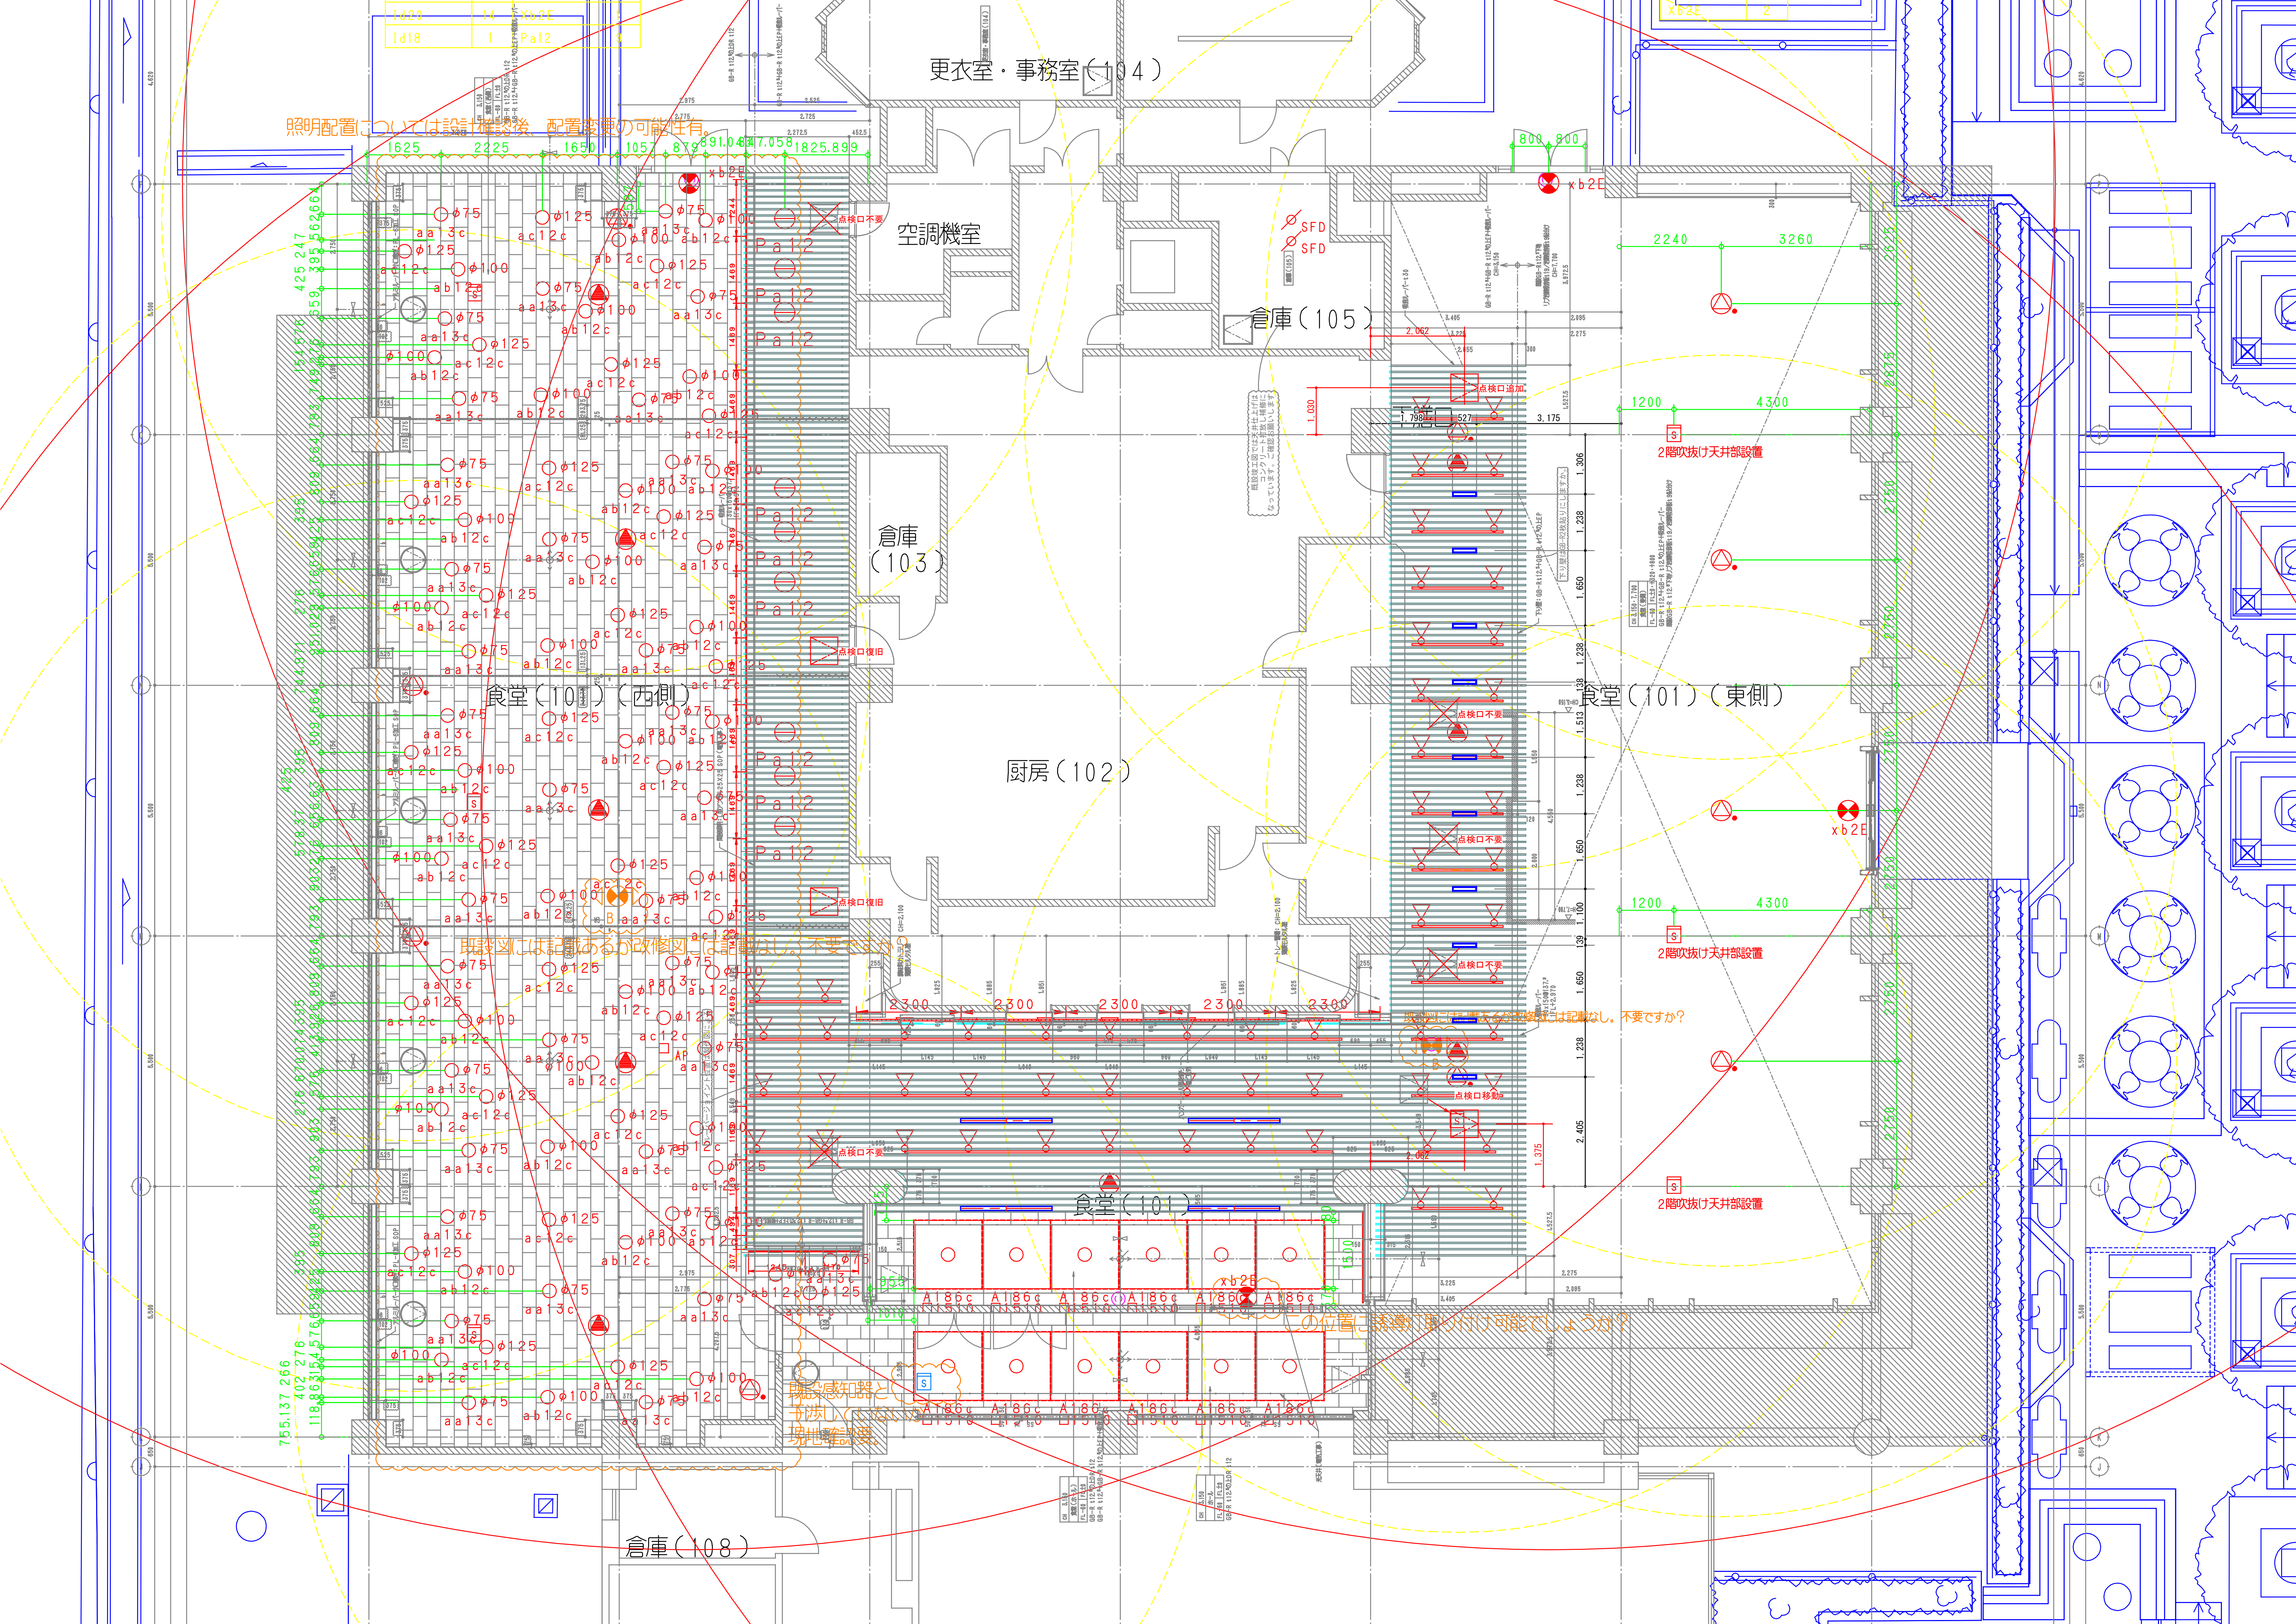
更衣室・事務室（104）
空調機室
倉庫（105）
倉庫（103）
食堂（101）（西側）
厨房（102）
食堂（101）（東側）
食堂（101）
倉庫（108）
点検口不要
点検口追加
点検口復旧
点検口移動
2階吹抜け天井部設置
SFD
xb2E
Pa12
aa13c
ab12c
ac12c
A186c
φ75
φ100
φ125
1625
2225
1650
1057
879
2240
3260
1200
4300
2300
1010
1500

照明配置については設計確認後、配置変更の可能性有。

既設図には記載あるが改修図には記載なし。不要ですか？

既設図には記載あるが改修図には記載なし。不要ですか？

この位置に誘導灯取り付け可能でしょうか？

既設感知器と干渉していないか現地確認要。