図面・計画書添付書

工事名

椙山女学園　星が丘キャンパス大学会館食堂リニューアル工事

図面名称

食堂床タイル割付図

施工予定日　2027/02/02

躯　体	[✓ 仕　上]	設　備
[✓ 打合図]	受領図	受領印用図

発行日

返却希望日

	発 注 者			施工部署				生産技術部		設備部	
				現場管理責任者	工事長	主任	担当者	工事長	担当者	工事長	担当者
印				✓ 承認 2026/10/29 金子　冬平				承認 2026/10/29 小山　努			
日付				10.29							

	設　計 責任者	工　事 監理者		工事監理担当者							
				意匠		構造		機械		電気	
印											
日付											

記　事（質疑応答・連絡事項・その他）

P2 家具有り

P4 修正箇所

P5 タイル業者調整事項

261030

~~2026/10/29~~

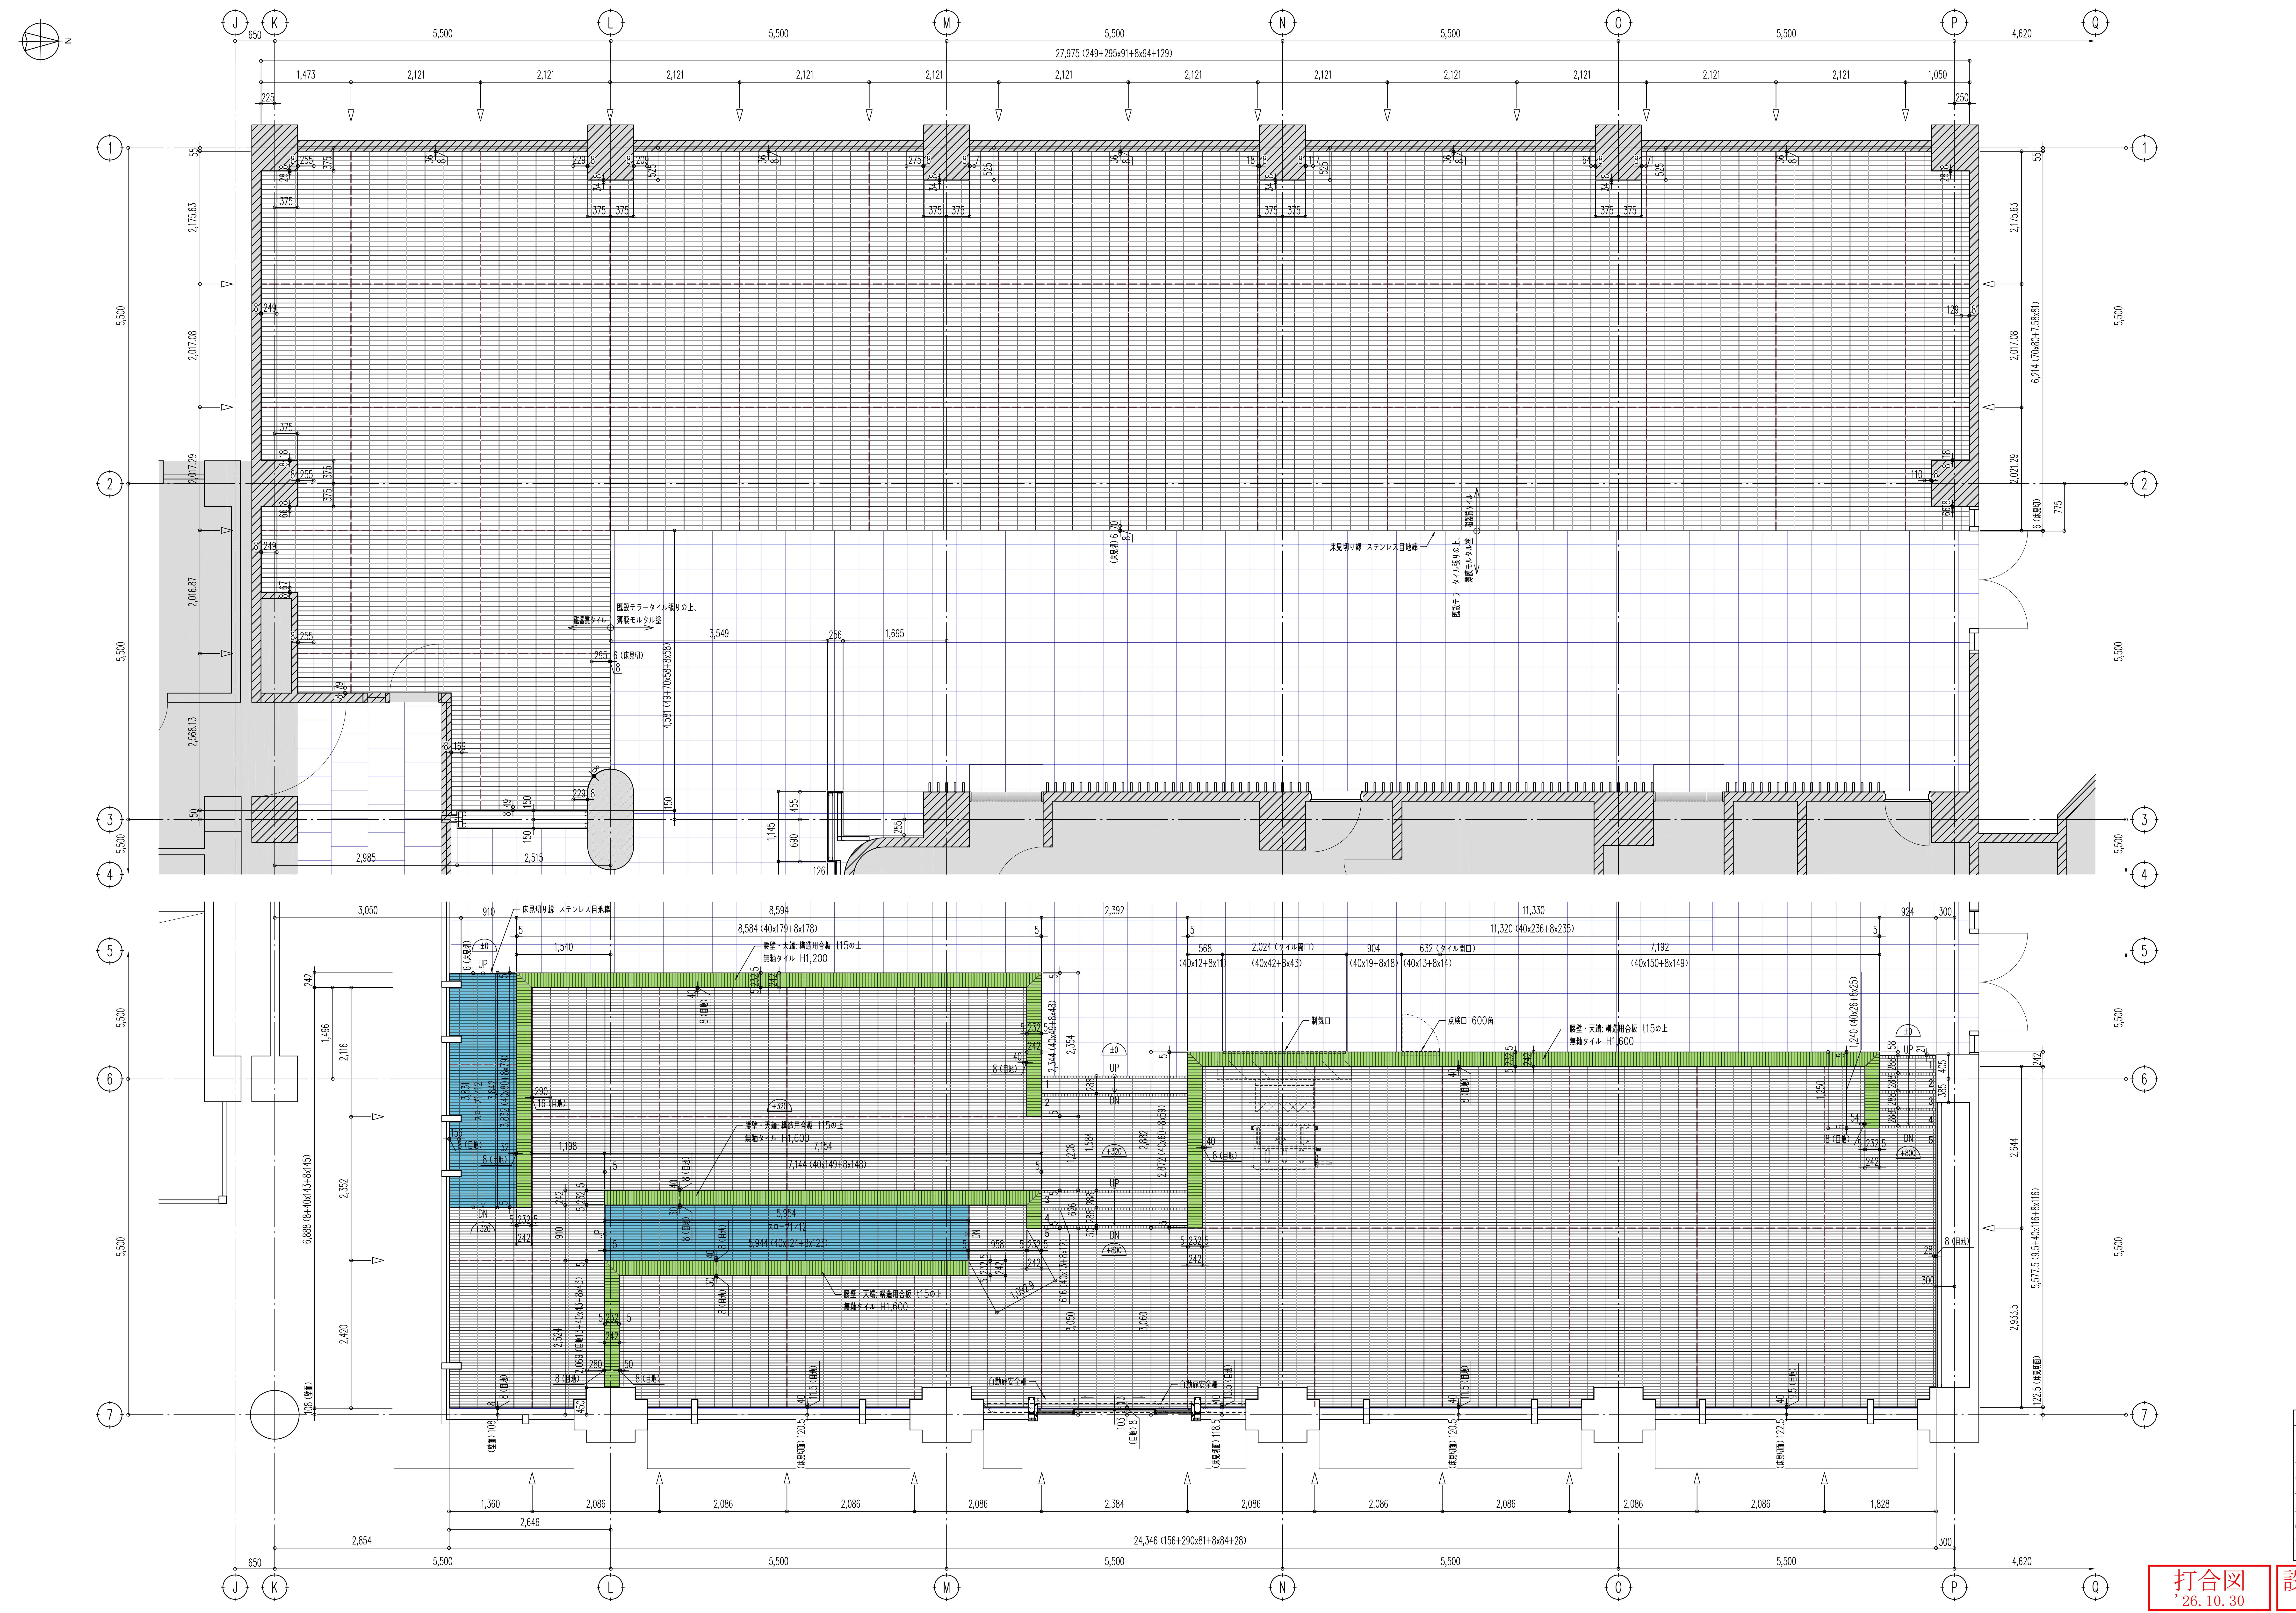

凡例

▷ - - -	伸縮目地を示す
🟦	スロープを示す
🟩	腰壁を示す
┼┼┼	既存タイルを示す

KEY PLAN

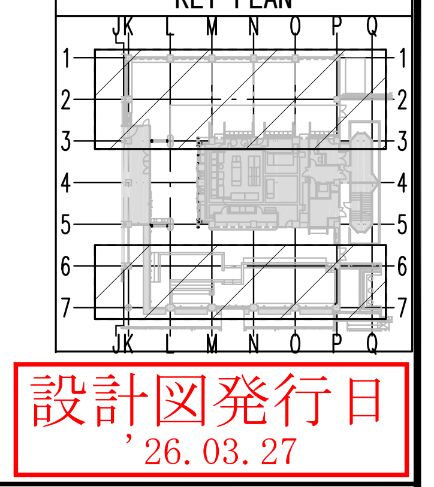

打合図
'26.10.30

設計図発行日
'26.03.27

チェック項目	未	完	• 巾木の逃げ		
• FLの押えの統一			• 石、T、B（テラゾー B）の逃げ		
• 下げ梁 下げスラブ			• SW、AW、SDの差筋・箱入		
• フロアーヒンジ			• SSの溝ボックス差筋箱入		
• インサート・ルーフドレーン（打込み金物）			• 手摺子金物、アンカー差筋・箱入		
• 防水立上り			• ブロック用差筋（床、天井、梁下、壁）		
• ELV関連、箱入（押ボタン、ワイヤー穴）			• 断熱材の打込み		
• 設備開口、及貫通孔			• 誘発目地・化粧目地		
• 荷揚げ用仮穴、墨出し穴、足場用アンカー			• 常開のSFD埋め込み（マグネット共）		
• 後打部（打継ぎ部）			•		
• 掃除口穴（打継ぎ部梁底）			•		
• 打放しフカシ・増打			•		

凡　例

<階高>
2FL
4,950
1FL

<室名 記号>
天井高さ
室名
躯体天端 | 床仕上天端
特記事項

<開口 記号>
H — 開口寸法 高さ
符号 — 建具符号
h — 基準高さから建具下枠の上端までの高さ
特記事項（電気錠等）

●●・・・扉の開き優先を示す。

記号	内　容	C	ストリングスカーテン		
⬭	保留を示す				
⌓	床レベル（FL基準）				
∧	壁ボード目地				

改訂履歴	改訂日	改訂ヶ所	改訂理由
第１回改訂			
第２回改訂			
第３回改訂			
第４回改訂			
第５回改訂			

配布ルール
1 変更の場合はこの原図を変更し、改訂履歴を明記する。
2 原図に配布予定先を記入する。
3 変更の都度、全部の配布予定先にコピーを配布する。
4 変更図（コピー）を受領したら旧版は自主廃棄する。

配布予定業者

承認	審査	作成
現場管理責任者		担当者

受領日

椙山女学園星が丘キャンパス大学会館食堂リニューアル工事

食堂床タイル割付図-1/2

縮尺 A1:1/50 A3:1/100　'26.10.23

清水建設株式会社名古屋支店

仕上－０８

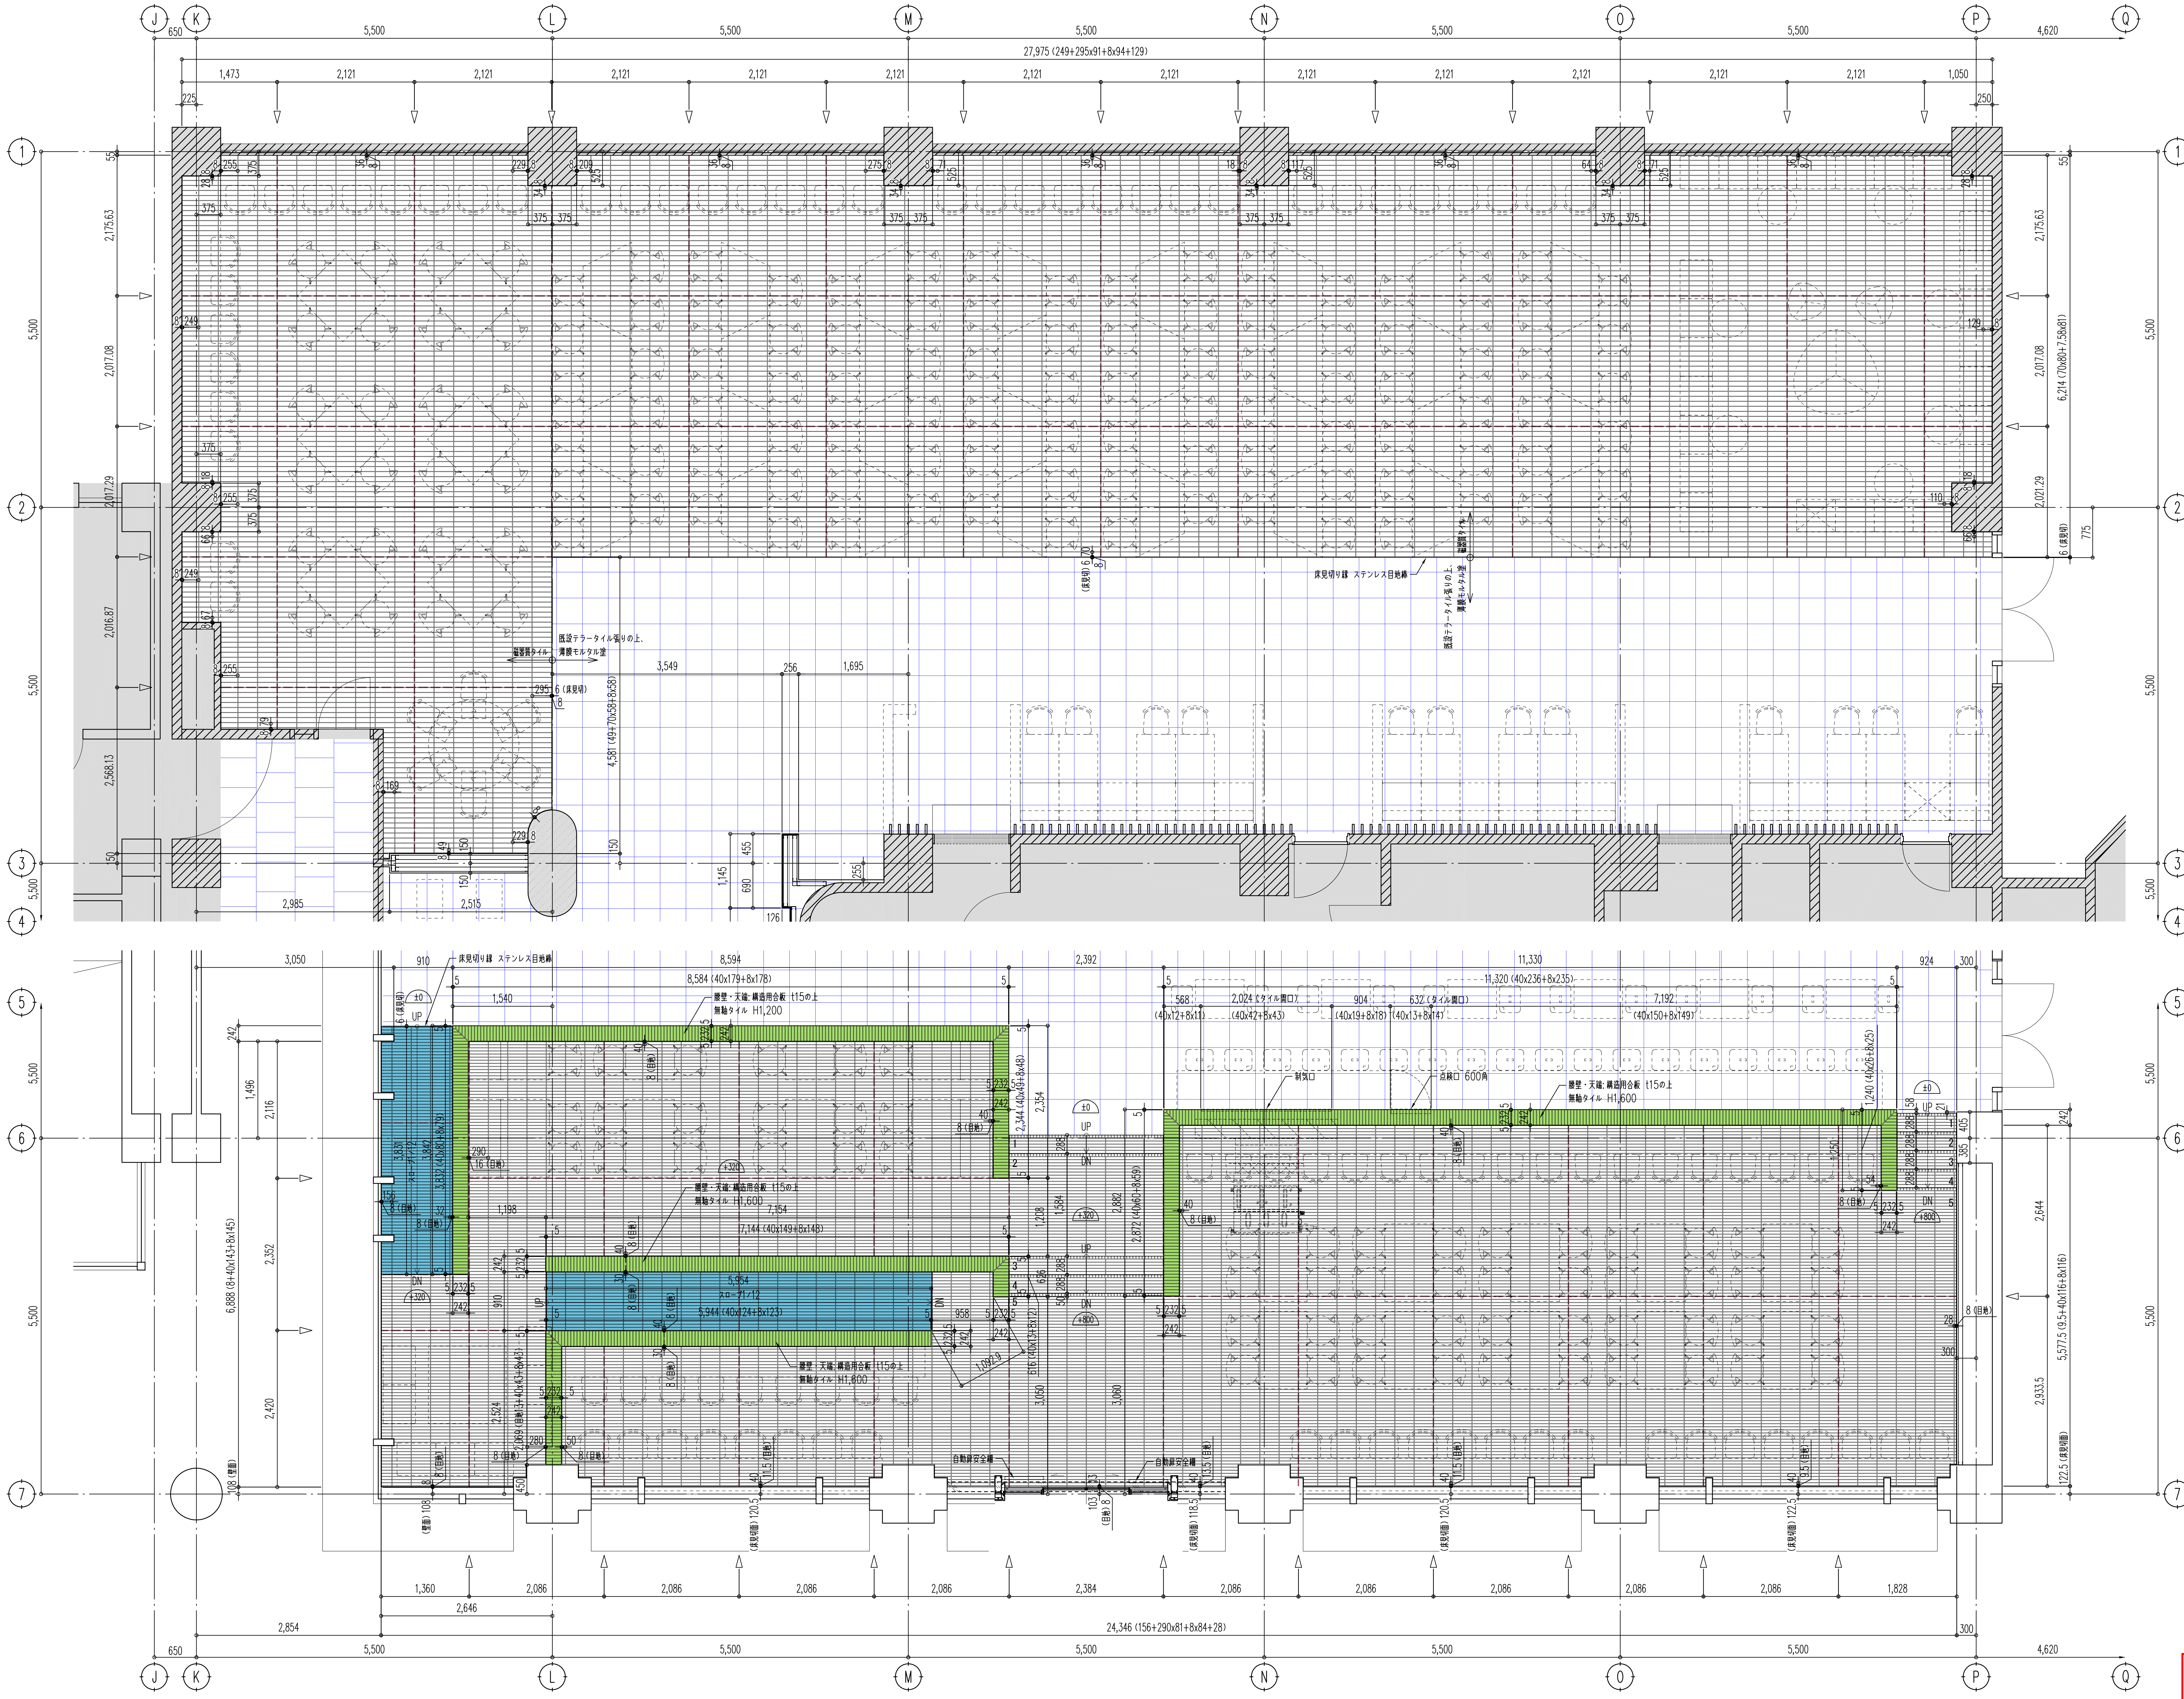

凡例	
▷ - - -	伸縮目地を示す
🟦	スロープを示す
🟩	腰壁を示す
╪╪╪	既存タイルを示す

KEY PLAN

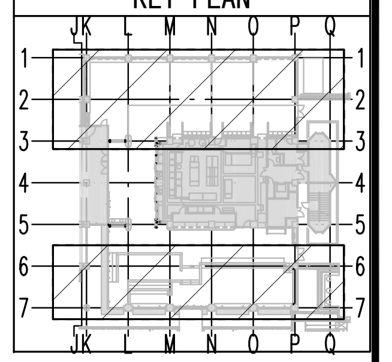

打合図
'26.10.30

設計図発行日
'26.03.27

チェック項目	未	完			
●FLの押えの統一			●巾木の逃げ		
●下げ梁　下げスラブ			●石、T、B（テラゾー　B）の逃げ		
●フロアーヒンジ			●SW、AW、SDの差筋・箱入		
●インサート・ルーフドレーン（打込み金物）			●SSの溝ボックス差筋箱入		
●防水立上り			●手摺子金物、アンカー差筋・箱入		
●ELV関連、箱入（押ボタン、ワイヤー穴）			●ブロック用差筋（床、天井、梁下、壁）		
●設備開口、及貫通孔			●断熱材の打込み		
●荷揚げ用仮穴、墨出し穴、足場用アンカー			●誘発目地・化粧目地		
●後打部（打継ぎ部）			●常開のSFD埋め込み（マグネット共）		
●掃除口穴（打継ぎ部梁底）			●		
●打放しフカシ・増打			●		

凡　　例

<階高>

2FL
4,950
1FL

<室名 記号>

天井高さ	
室名	
躯体天端	床仕上天端

特記事項

<開口 記号>

H — 開口寸法　高さ
符号 — 建具符号
h — 基準高さから建具下枠の上端までの高さ

特記事項（電気錠等）

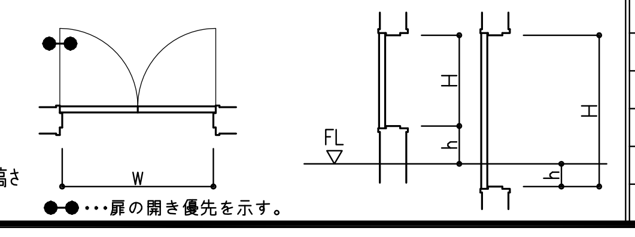

●-●・・・扉の開き優先を示す。

記号	内　容	C	ストリングスカーテン		
☁	保留を示す				
⌓	床レベル（FL基準）				
∧	壁ボード目地				

改訂履歴	改訂日	改訂ヶ所	改訂理由
第１回改訂			
第２回改訂			
第３回改訂			
第４回改訂			
第５回改訂			

配布ルール

1 変更の場合はこの原図を変更し、改訂履歴を明記する。
2 原図に配布予定先を記入する。
3 変更の都度、全部の配布予定先にコピーを配布する。
4 変更図（コピー）を受領したら旧版は自主廃棄する。

配布予定業者

承　認	審　査	作　成
現場管理責任者		担当者

受領日

椙山女学園星が丘キャンパス大学会館食堂リニューアル工事

食堂床タイル割付図-1/2(家具あり)

縮尺　A1:1/50　A3:1/100　'26.10.23

清水建設株式会社名古屋支店

仕上－０８

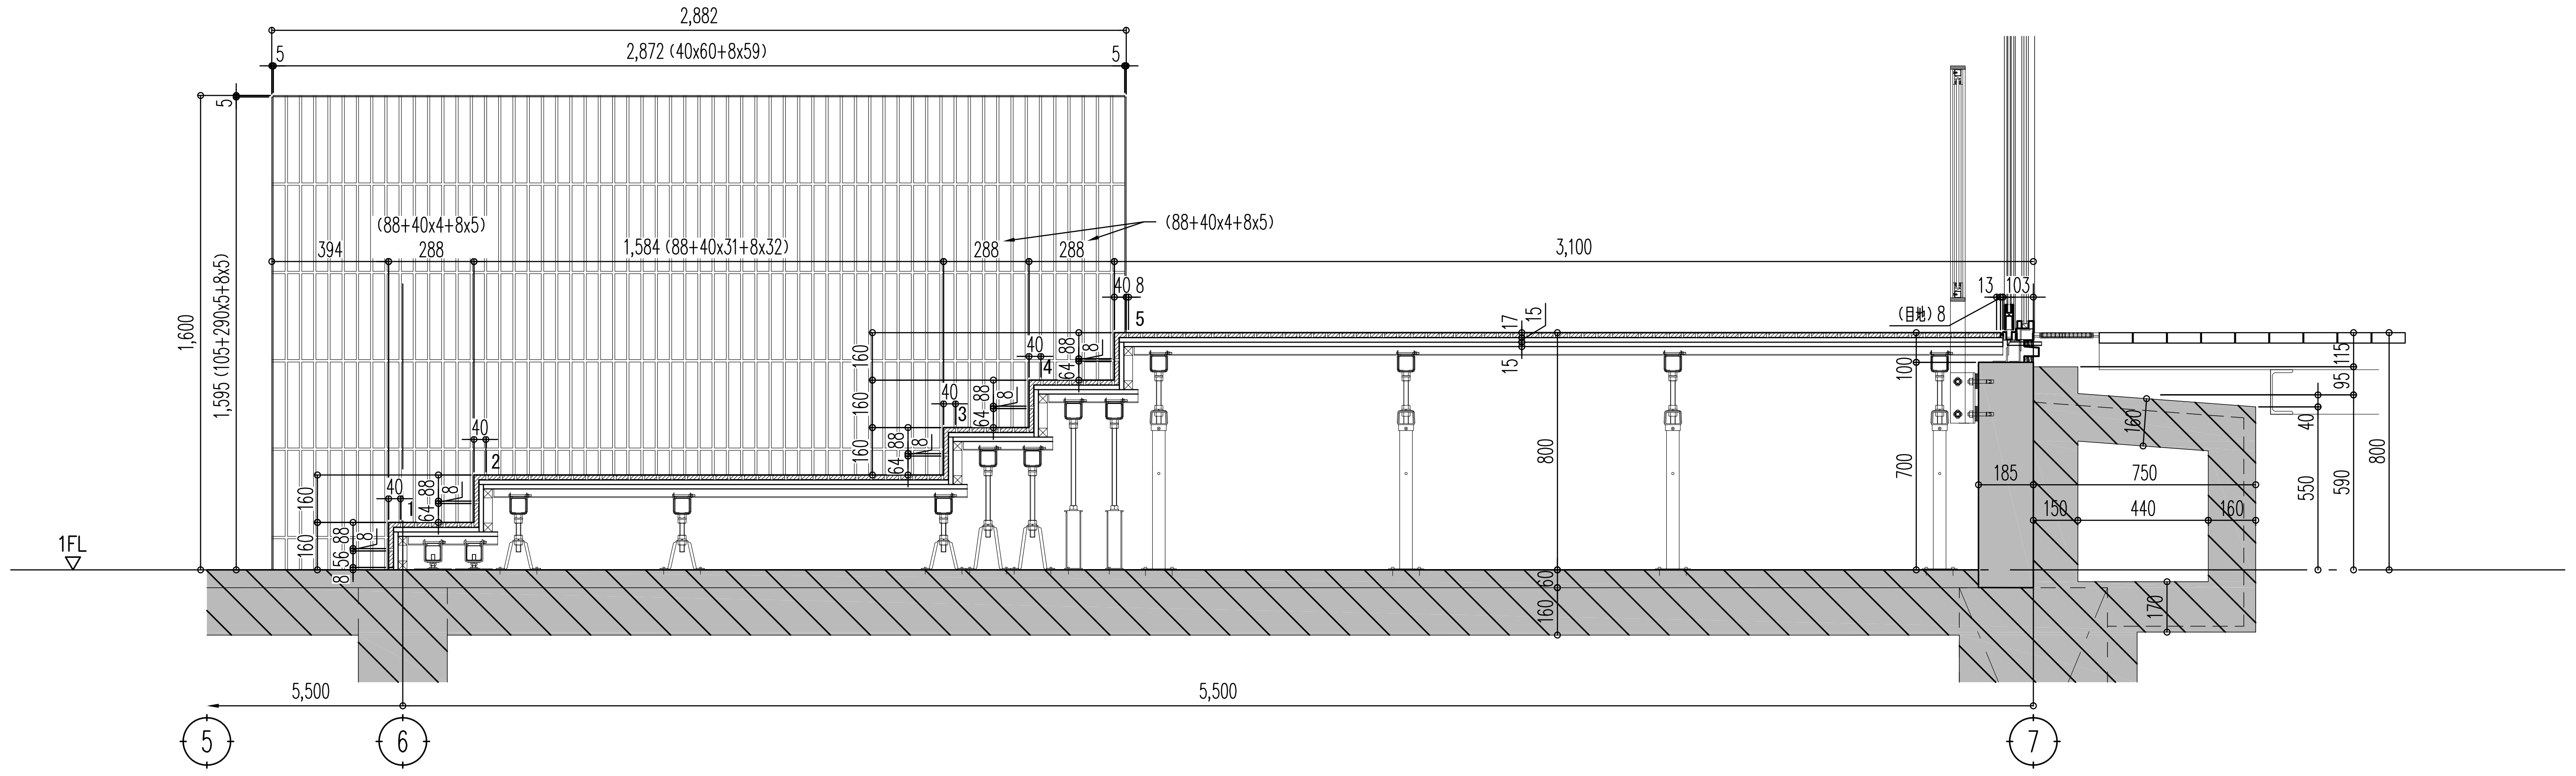

Ⓐ－Ⓐ断面図 S=1／20

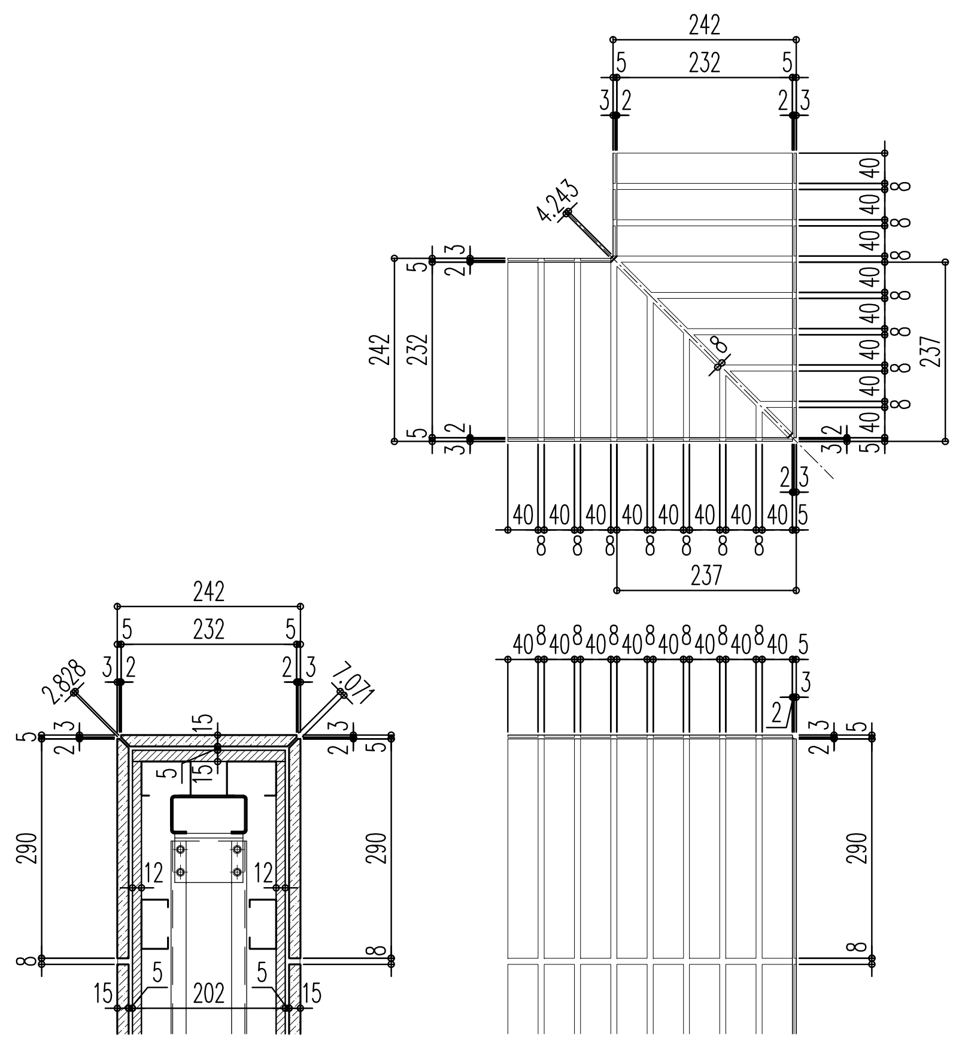

腰壁タイル割付詳細図 S=1／10

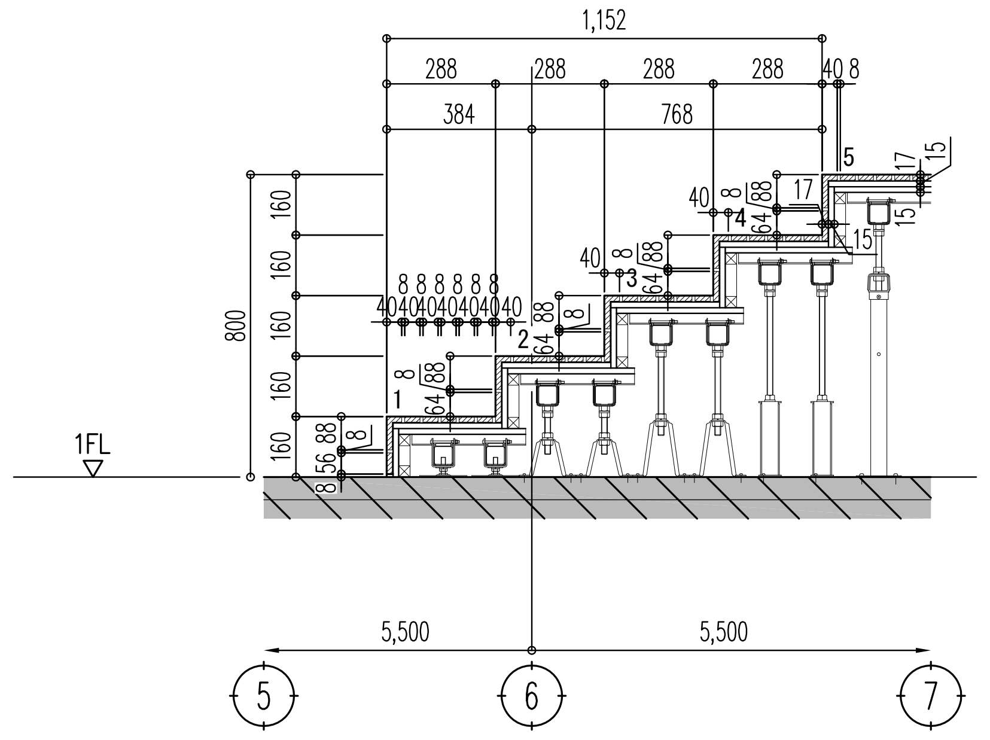

Ⓑ－Ⓑ断面図 S=1／20

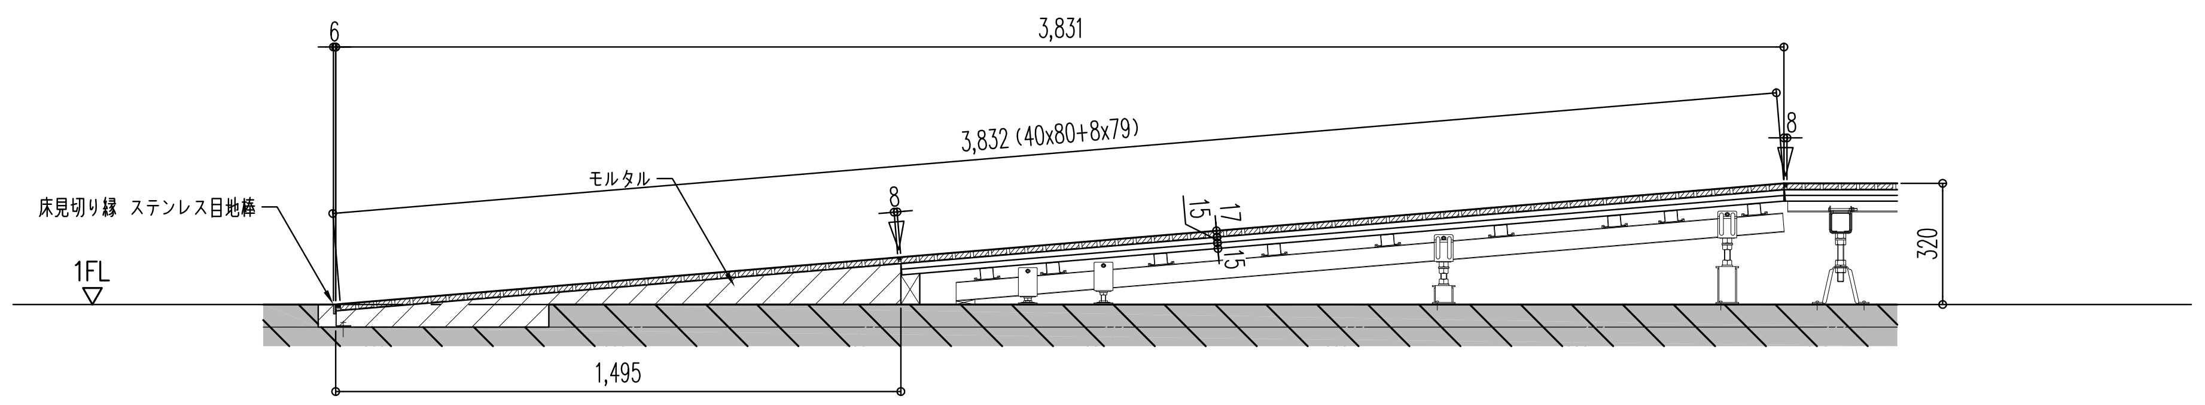

Ⓒ－Ⓒ断面図 S=1／20

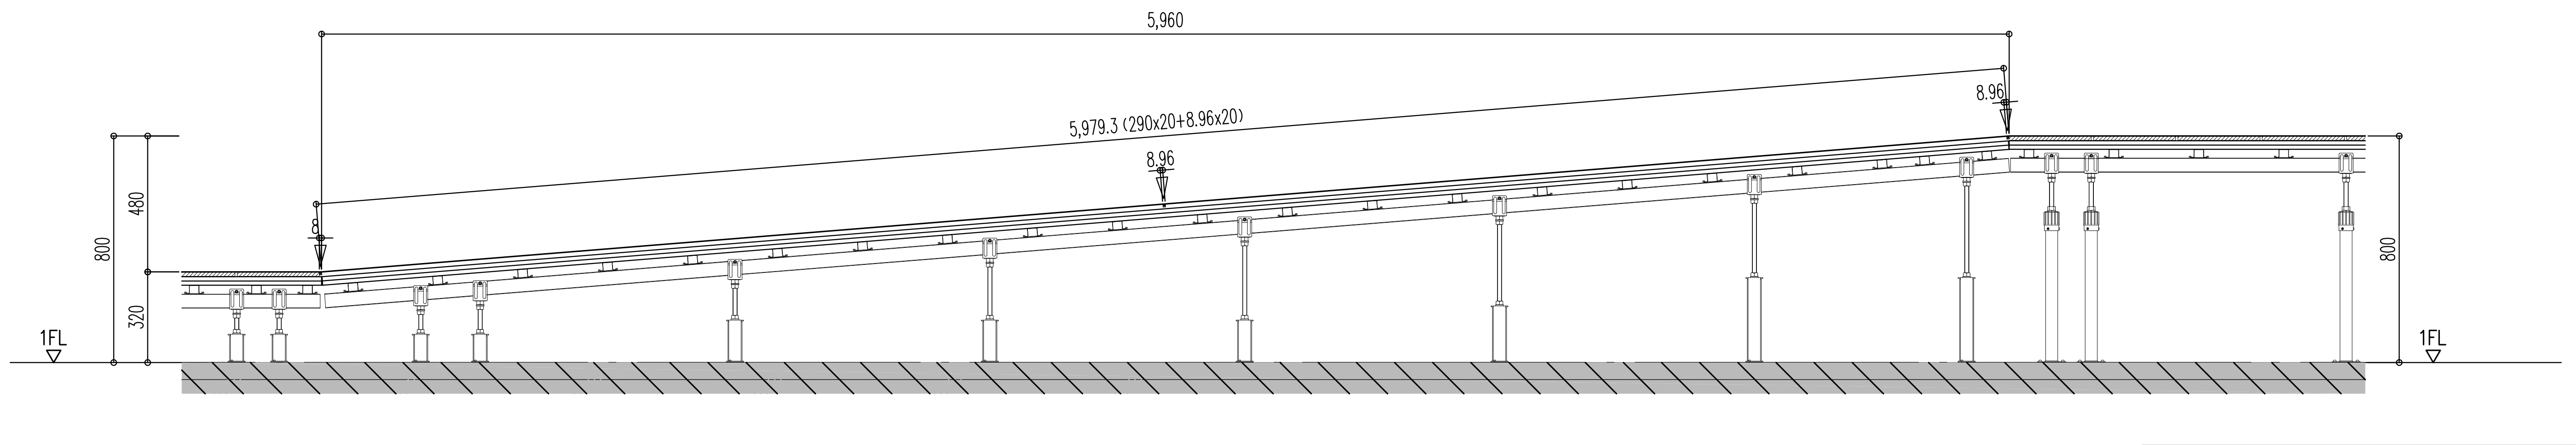

Ⓓ－Ⓓ断面図 S=1／20

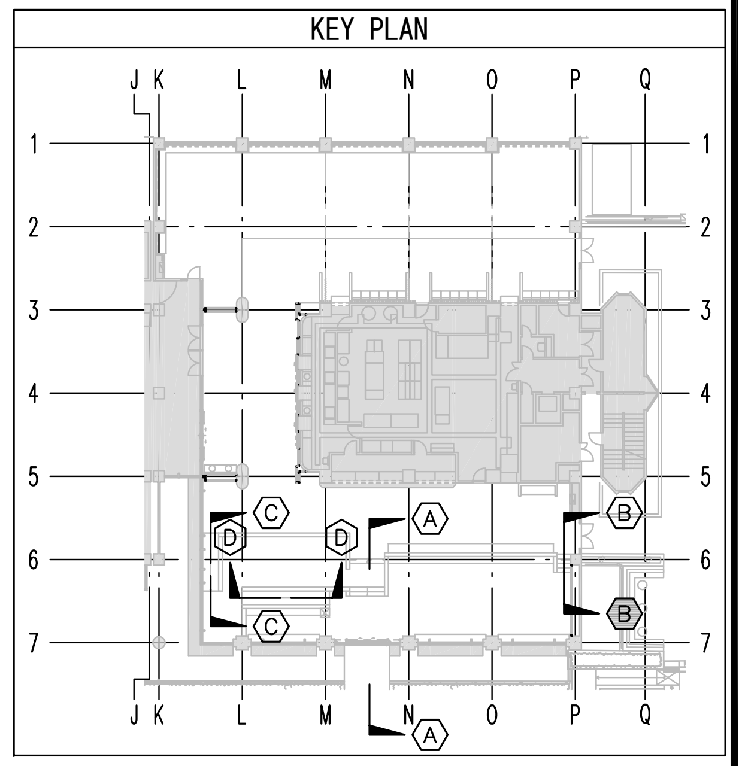

打合図
'26.10.30

設計図発行日
'26.03.27

チェック項目	未	完			
• FLの押えの統一			• 巾木の逃げ		
• 下げ梁 下げスラブ			• 石、T、B（テラゾー B）の逃げ		
• フロアーヒンジ			• SW、AW、SDの差筋・箱入		
• インサート・ルーフドレーン（打込み金物）			• SSの溝ボックス差筋箱入		
• 防水立上り			• 手摺子金物、アンカー差筋・箱入		
• ELV関連、箱入（押ボタン、ワイヤー穴）			• ブロック用差筋（床、天井、梁下、壁）		
• 設備開口、及貫通孔			• 断熱材の打込み		
• 荷揚げ用仮穴、墨出し穴、足場用アンカー			• 誘発目地・化粧目地		
• 後打部（打継ぎ部）			• 常開のSFD埋め込み（マグネット共）		
• 掃除口穴（打継ぎ部梁底）			•		
• 打放しフカシ・増打			•		

凡　例

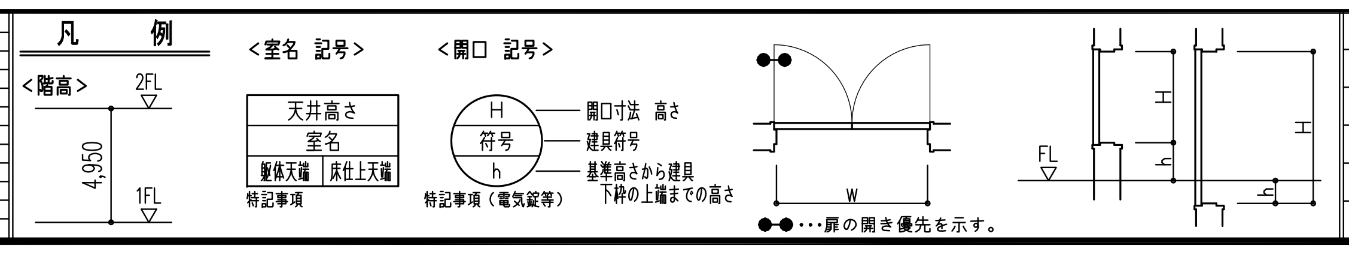

●●・・・扉の開き優先を示す。

記号	内　容	C	ストリングスカーテン		
⬭	保留を示す				
⌓	床レベル（FL基準）				
∧	壁ボード目地				

改訂履歴	改訂日	改訂ヶ所	改訂理由
第１回改訂			
第２回改訂			
第３回改訂			
第４回改訂			
第５回改訂			

配布ルール
1 変更の場合はこの原図を変更し、改訂履歴を明記する。
2 原図に配布予定先を記入する。
3 変更の都度、全部の配布予定先にコピーを配布する。
4 変更図（コピー）を受領したら旧版は自主廃棄する。

配布予定業者

承認	審査	作成
現場管理責任者		担当者

受領日

椙山女学園星が丘キャンパス大学会館食堂リニューアル工事
食堂床タイル割付図-2/2
縮尺 A1:1/50 A3:1/100 '26.10.23
清水建設株式会社名古屋支店
仕上－０９

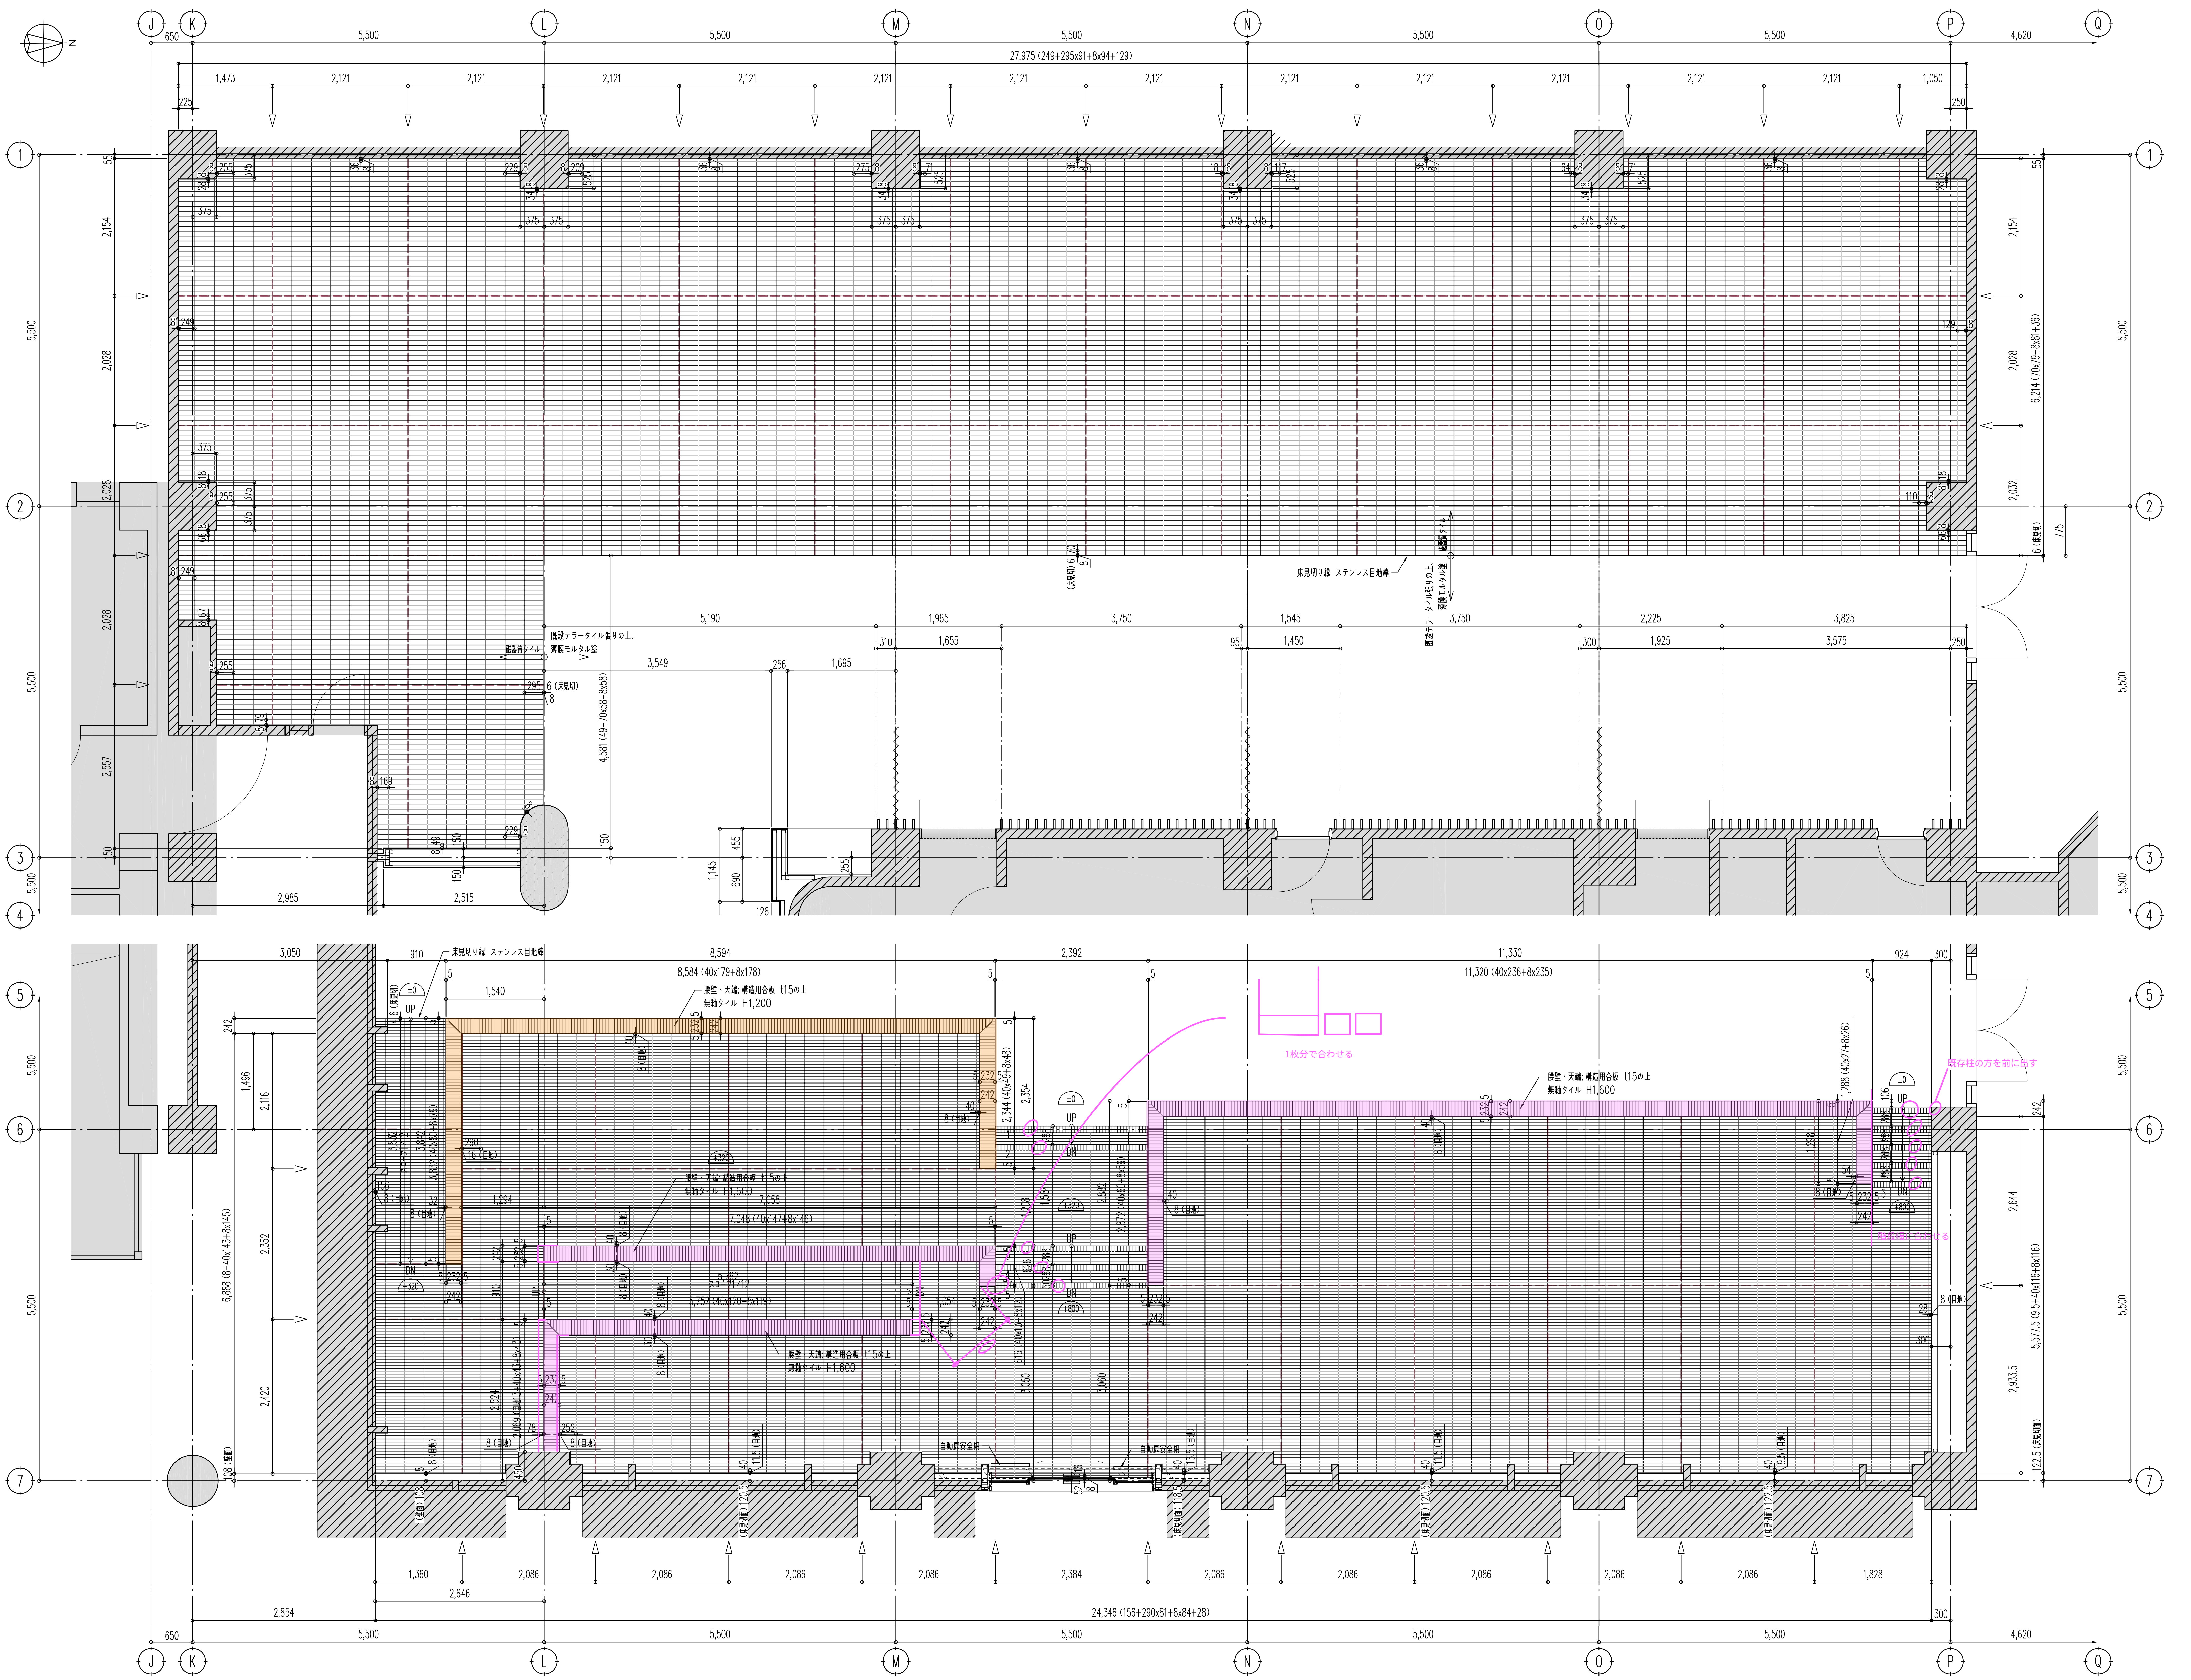

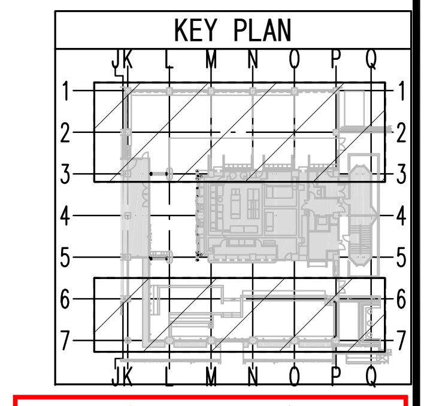

打合図
'26.10.27

設計図発行日
'26.03.27

チェック項目	未	完			
• FLの押えの統一			• 巾木の逃げ		
• 下げ梁 下げスラブ			• 石. T. B (テラゾー B) の逃げ		
• フロアーヒンジ			• SW. AW. SDの差筋・箱入		
• インサート・ルーフドレーン (打込み金物)			• SSの溝ボックス差筋箱入		
• 防水立上り			• 手摺子金物. アンカー差筋・箱入		
• ELV関連. 箱入 (押ボタン. ワイヤー穴)			• ブロック用差筋 (床. 天井. 梁下. 壁)		
• 設備開口. 及貫通孔			• 断熱材の打込み		
• 荷揚げ用仮穴. 墨出し穴. 足場用アンカー			• 誘発目地・化粧目地		
• 後打部 (打継ぎ部)			• 常開のSFD埋め込み (マグネット共)		
• 掃除口穴 (打継ぎ部梁底)			•		
• 打放しフカシ・増打			•		
			•		

凡 例

<階高> 2FL 4,950 1FL

<室名 記号>
天井高さ
室名
躯体天端 | 床仕上天端
特記事項

<開口 記号>
H — 開口寸法 高さ
符号 — 建具符号
h — 基準高さから建具下枠の上端までの高さ
特記事項 (電気錠等)

●● ・・・扉の開き優先を示す。

記号	内 容	C	ストリングスカーテン
⬭	保留を示す		
⌓	床レベル (FL基準)		
∧	壁ボード目地		

改訂履歴	改訂日	改訂ヶ所	改訂理由
第1回改訂			
第2回改訂			
第3回改訂			
第4回改訂			
第5回改訂			

配布ルール
1 変更の場合はこの原図を変更し、改訂履歴を明記する。
2 原図に配布予定先を記入する。
3 変更の都度、全部の配布予定先にコピーを配布する。
4 変更図 (コピー) を受領したら旧版は自主廃棄する。

配布予定業者

承 認	審 査	作 成
現場管理責任者		担当者
受領日		

椙山女学園星が丘キャンパス大学会館食堂リニューアル工事
食堂床タイル割付図-1/2
縮尺 A1:1/50 A3:1/100 '26.10.23
清水建設株式会社名古屋支店
仕上ー08

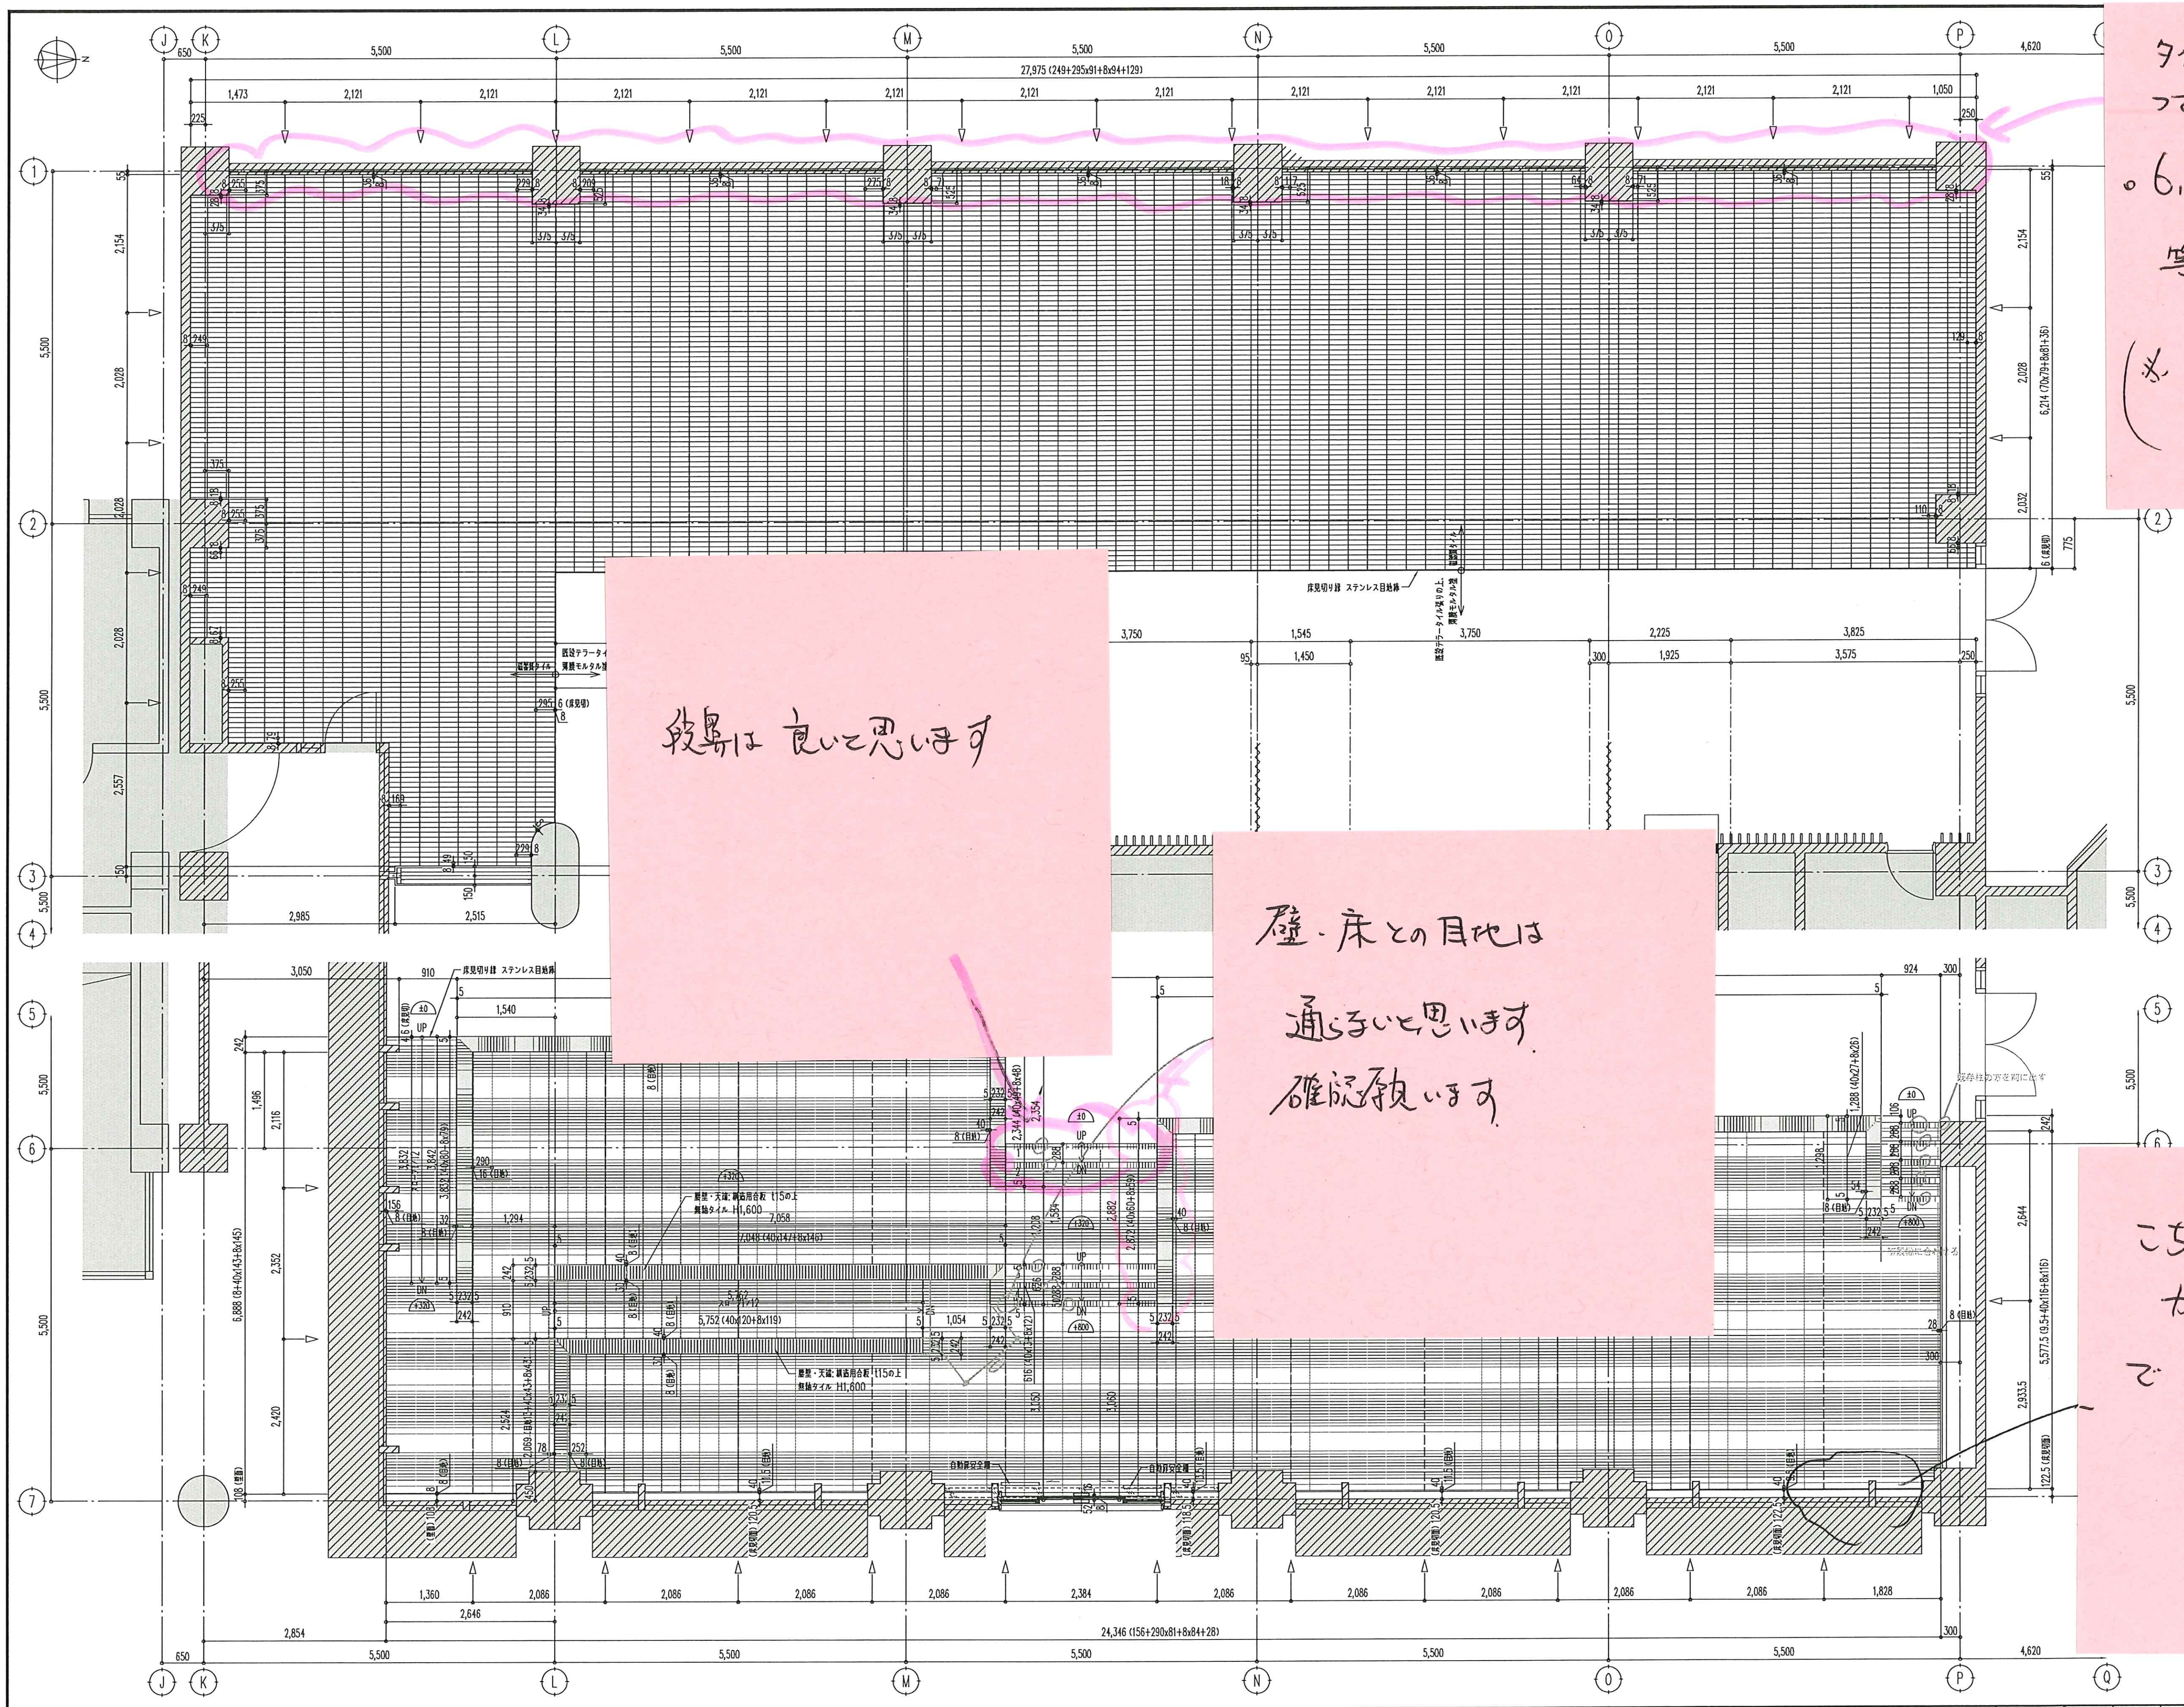
J
K
L
M
N
O
P
Q
1
2
3
4
5
6
7
5,500
650
4,620
27,975 (249+295x91+8x94+129)
6,214 (70x79+8x81+36)
24,346 (156+290x81+8x84+28)
床見切り目 ステンレス目地棒
既設テラゾータイル
自動扉安全器

タイルの長辺が、カット物になっております。

・6,214 = (70×80 + 7.58×81)

等に変更お願いします。

（※ バラで張るので、目地巾は自由です。）

段差は良いと思います

壁・床との目地は通らないと思います。確認願います。

こちらの端部は、カット無しで割れているでよかったでしょうか？

チェック項目	未	完	・巾木の逃げ		
・FLの押えの統一			・石、T、B（テラゾー B）の逃げ		
・下げ梁 下げスラブ			・SW、AW、SDの差筋・箱入		
・フロアーヒンジ			・SSの縦ボックス差筋箱入		
・インサート・ルーフドレーン（打込み金物）			・手摺子金物、アンカー差筋・箱入		
・防水立上り			・ブロック用差筋（床、天井、梁下、壁）		
・ELV開口、箱入（押ボタン、ワイヤー穴）			・断熱材の打込み		
・設備開口、及箱入			・誘発目地・化粧目地		
・荷揚げ用仮穴、墨出し穴、足場用アンカー			・常閉のSFD組込み（マグネット共）		
・後打部（打残し部）			・		
・掃除口穴（打継ぎ部清掃）			・		
・打増しフカシ・増打			・		

凡　例

<階高> 2FL 4,950 1FL

<室名 記号>

天井高さ
室名
躯体天端 | 床仕上天端
特記事項

<開口 記号>

H — 開口寸法 高さ
符号 — 建具符号
h — 基準高さから建具下枠の上端までの高さ
特記事項（電気錠等）

W

●-●…扉の開き優先を示す。

FL H h

記号	内　容	C	ストリングスカーテン		
⬚	保留を示す				
◠	床レベル（FL基準）				
∧	壁ボード目地				

改訂履歴	改訂日	改訂ヶ所	改訂理由
第1回改訂			
第2回改訂			
第3回改訂			
第4回改訂			
第5回改訂			

配布ルール

1 変更の場合はこの原図を変更し、改訂履歴を明記する。
2 原図に配布予定先を記入する。
3 変更の都度、全部の配布予定先にコピーを配布する。
4 変更図（コピー）を受領したら旧版は自主廃棄する。

配布予定業者

承認	審査	作成
現場管理責任者		担当者

受領日

打合図 '26. 10. 27

設計図発行日 '26. 03. 27

椙山女学園星が丘キャンパス大学会館食堂リニューアル工事

食堂床タイル割付図-1/2

縮尺 A1:1/50 A3:1/100 '26. 10. 23

清水建設株式会社名古屋支店

仕上－０８