図面・計画書添付書

工事名

椙山女学園　星が丘キャンパス大学会館食堂リニューアル工事

図面名称 1階・2階床伏図	[✓ 躯 体]	仕 上	設 備
	[✓ 打合図]	受領図	受領印用図
施工予定日 2026/12/07	発行日		返却希望日

	発 注 者			施工部署				生産技術部		設備部	
				現場管理責任者	工事長	主任	担当者	工事長	**担当者**	工事長	担当者
印				✓ 承認 2026/10/07 金子　冬平				承認 2026/10/07 小山　努			
日付				10.7							

	設 計 責任者	工 事 監理者	工事監理担当者								
			意匠		構造		機械		電気		
印		工藤	山上	稲垣							
日付		261016	261014	10.9							

記　事（質疑応答・連絡事項・その他）

1006

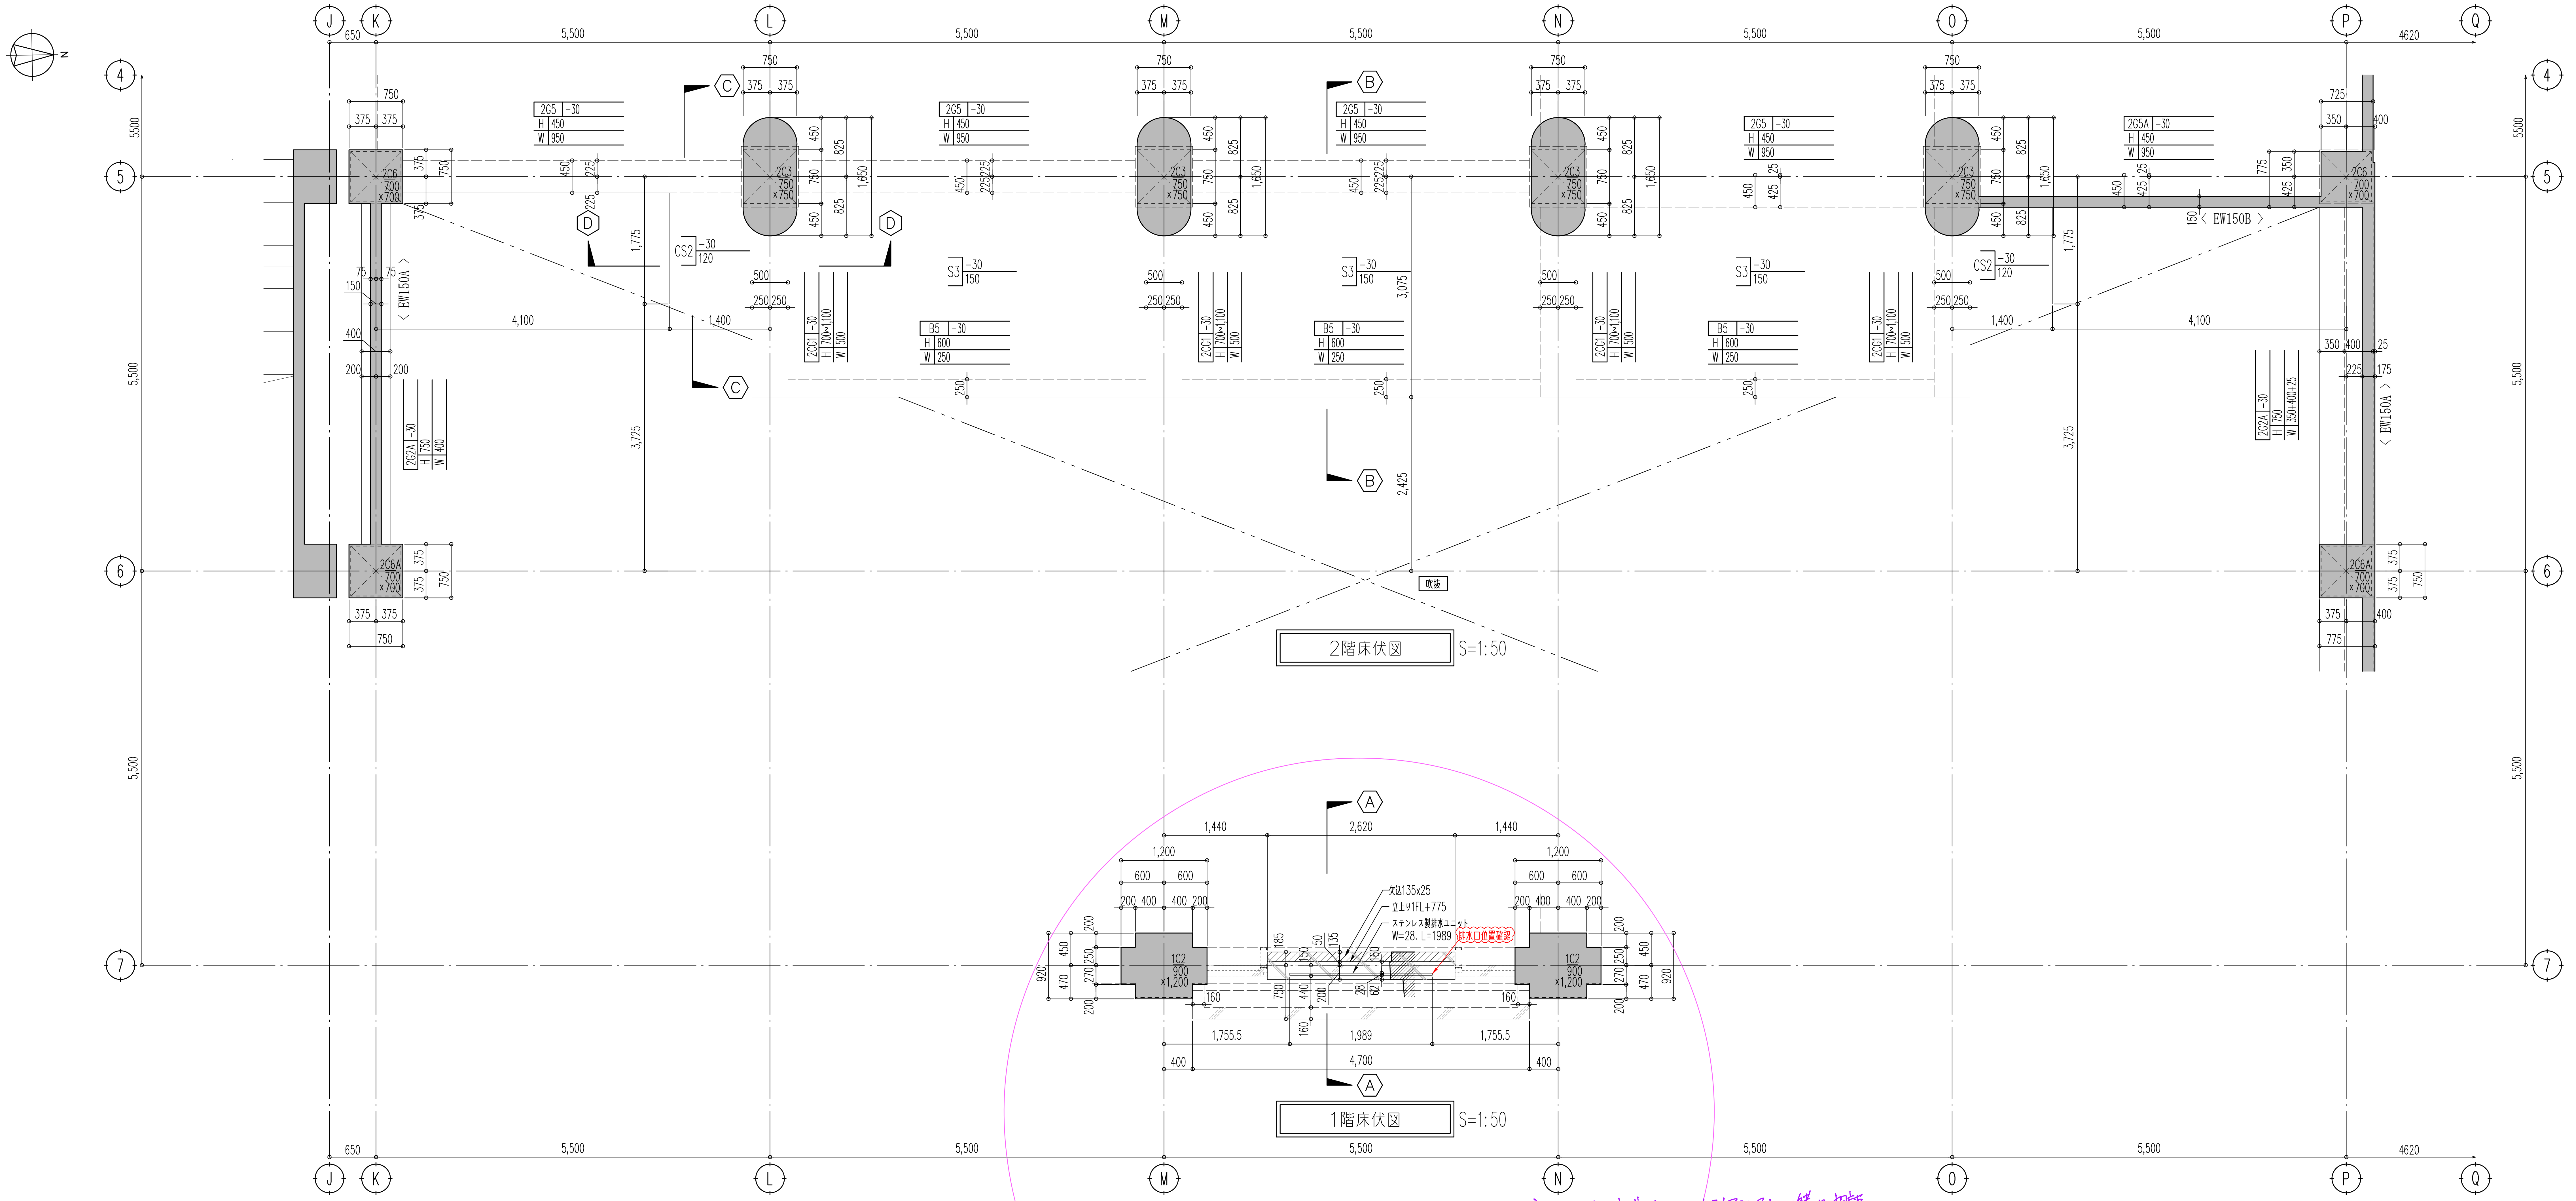

2階床伏図 S=1:50

1階床伏図 S=1:50

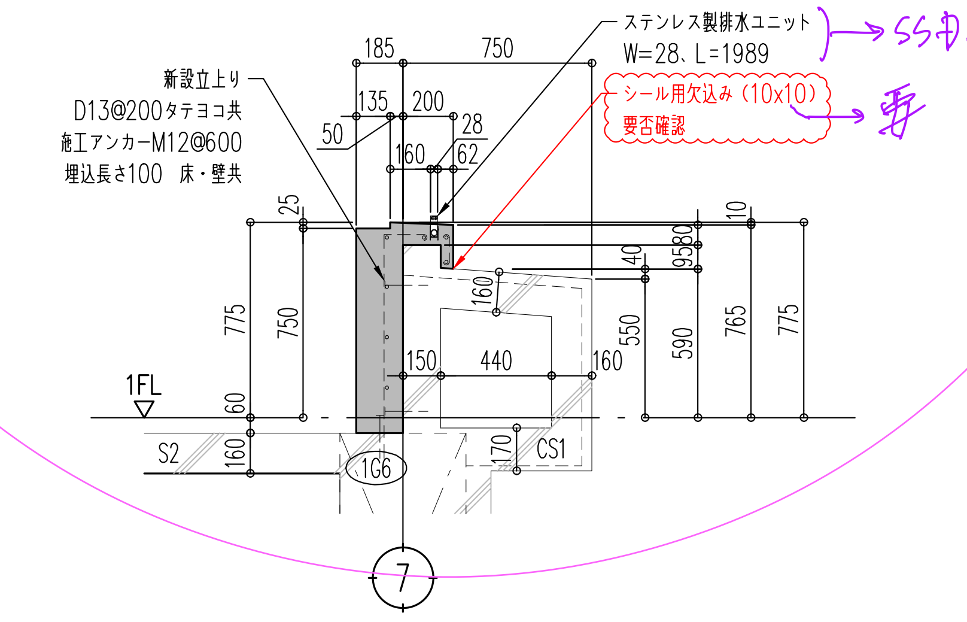

ステンレス製排水ユニット W=28、L=1989
シール用欠込み（10x10） 要否確認
断面立上り D13@200タテヨコ共
後施工アンカーM12@600 埋込長さ100 床・壁共
1FL
S2
CS1

A－A 断面図 S=1:30

→ SS巾、木デッキ、20ミリクリアランスと一緒に相談

→ 要

∠20mm クリアランスはヒールがはまり危険。細目グレーチングで水を切るのが確実

SSD納まりにより躯体形状検討中

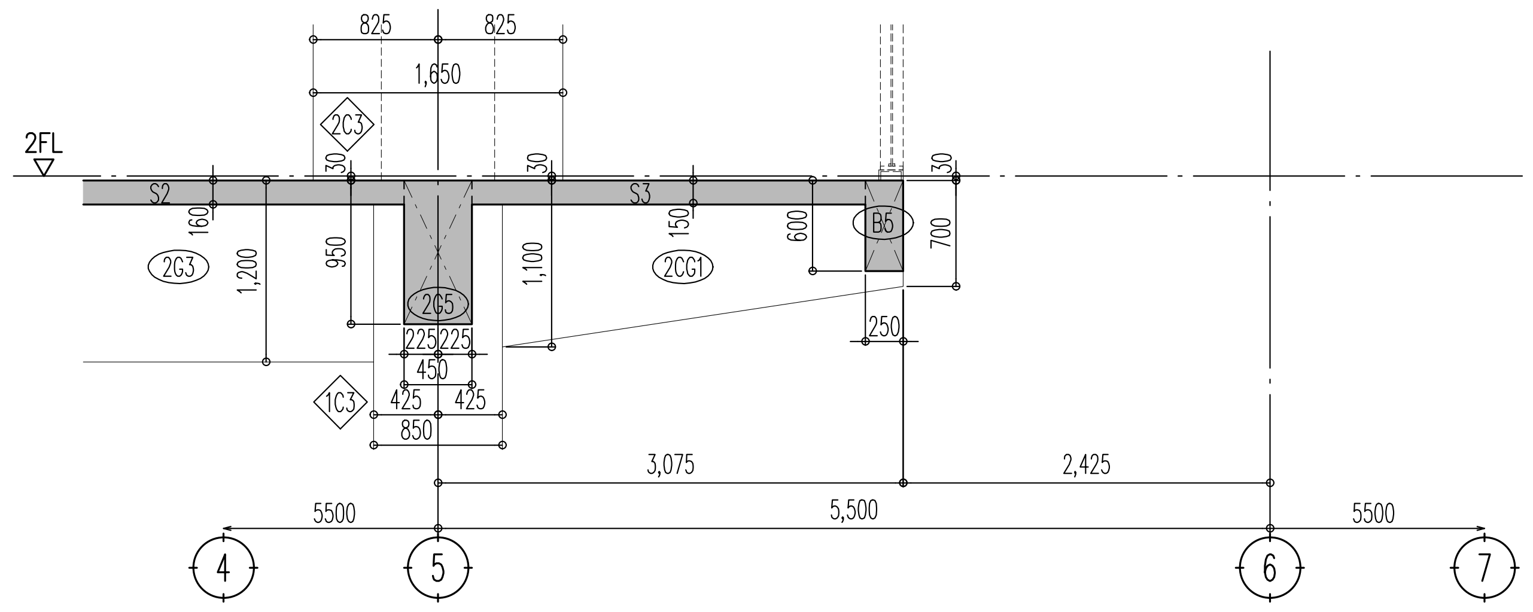

B－B 断面図 S=1:50

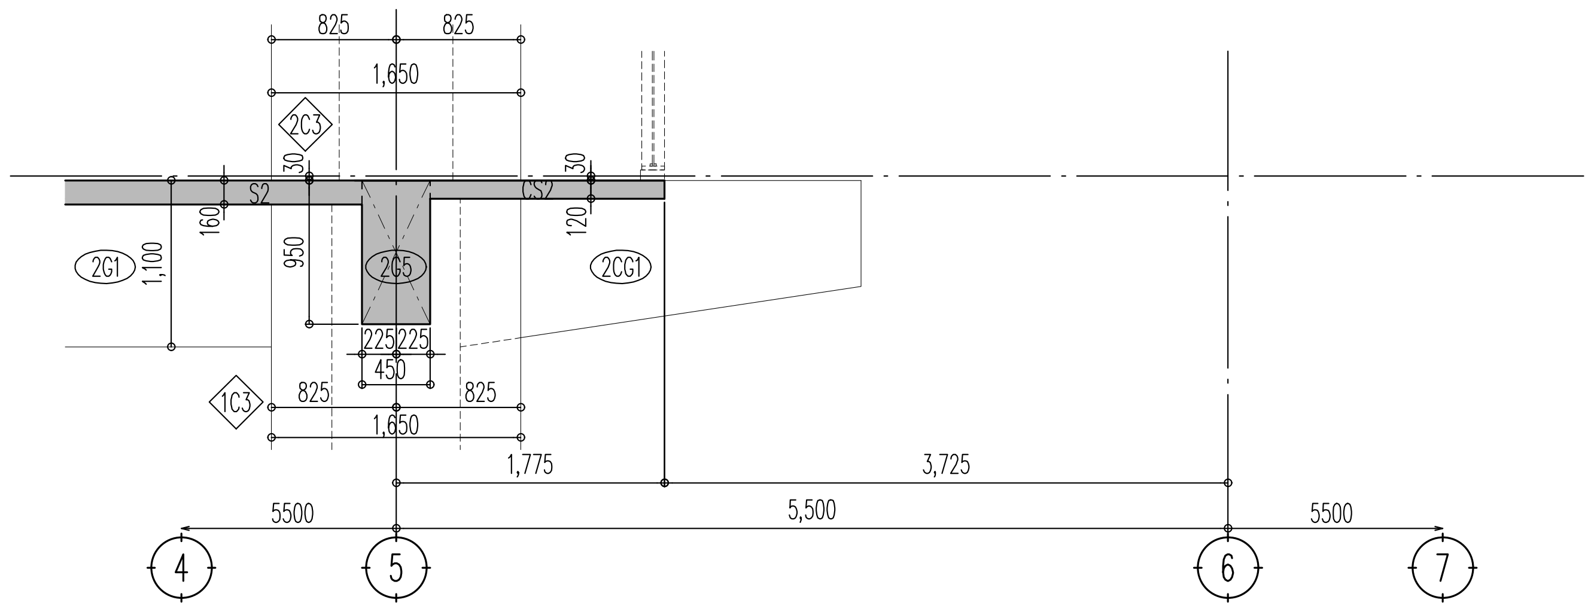

C－C 断面図 S=1:50

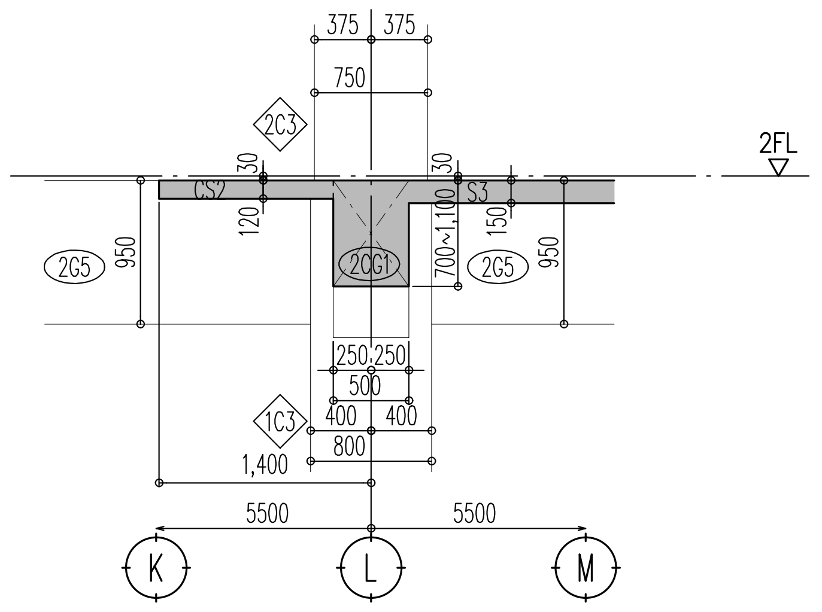

D－D 断面図 S=1:50

KEY PLAN

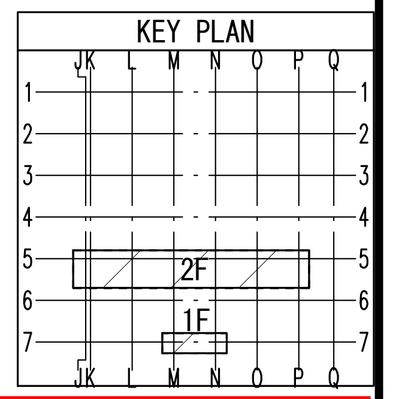

打合図 '26.10.06

設計図発行日 '26.03.27

チェック項目	未	完	・巾木の逃げ		
・FLの押えの統一			・石．T．B（テラゾー B）の逃げ		
・下げ梁 下げスラブ			・SW．AW．SDの差筋・箱入		
・フロアーヒンジ			・SSの溝ボックス差筋箱入		
・インサート・ルーフドレーン（打込み金物）			・手摺子金物．アンカー差筋・箱入		
・防水立上り			・ブロック用差筋（床．天井．梁下．壁）		
・ELV関連．箱入（押ボタン．ワイヤー穴）			・断熱材の打込み		
・設備開口．及貫通孔			・誘発目地・化粧目地		
・荷揚げ用仮穴．墨出し穴．足場用アンカー			・常開のSFD埋め込み（マグネット共）		
・後打部（打継ぎ部）			・		
・掃除口穴（打継ぎ部梁底）			・		
・打放しフカシ・増打			・		

凡 例

<階高> 2FL 4,950 1FL

<杭 記号>

杭符号	φ	杭径
	h	基準高さからの杭天端高さ
	L	杭長さ

<基礎 記号>

基礎符号	T	基礎下端レベル
	H	基礎高さ

<柱 記号>
柱符号
柱幅－X軸
柱幅－Y軸
構造天端
※特記なき柱構造天端：FL－000

<梁 記号>

梁符号	基準高さからのCon天端レベル（構造天端）
H	上増打＋梁成＋下増打
W	左側増打＋梁巾＋右側増打

（特記事項：部分打ち増し等）

<耐圧盤 記号>
耐圧盤符号 基準高さからのCon天端レベル（構造天端） / 天端フカシ厚さ＋版厚

<スラブ 記号>
スラブ符号 基準高さからのCon天端レベル（構造天端） / 上増打＋スラブ厚＋下増打
（特記事項：断熱材等）

<壁 記号>
一般 W15
垂壁 壁符号 直上階基準高さからの垂壁下端高さ
腰壁 壁符号 基準高さからの腰壁天端高さ

<開口 記号>
H 開口寸法 高さ
符号 開口符号
h 基準高さから開口下端までの高さ
（特記事項）

※アンカー＠５００以内

改訂履歴	改訂日	改訂ヶ所	改訂理由
第１回改訂			
第２回改訂			
第３回改訂			
第４回改訂			
第５回改訂			

配布ルール
1 変更の場合はこの原図を変更し、改訂履歴を明記する。
2 原図に配布予定先を記入する。
3 変更の都度、全部の配布予定先にコピーを配布する。
4 変更図（コピー）を受領したら旧版は自主廃棄する。

配布予定業者

承 認	審 査	作 成
現場管理責任者		担当者

受領日

椙山女学園星が丘キャンパス大学会館食堂リニューアル工事

1階・2階床伏図

縮尺 A1:1/50 A3:1/100 '26.10.06

清水建設株式会社名古屋支店

躯体－０１

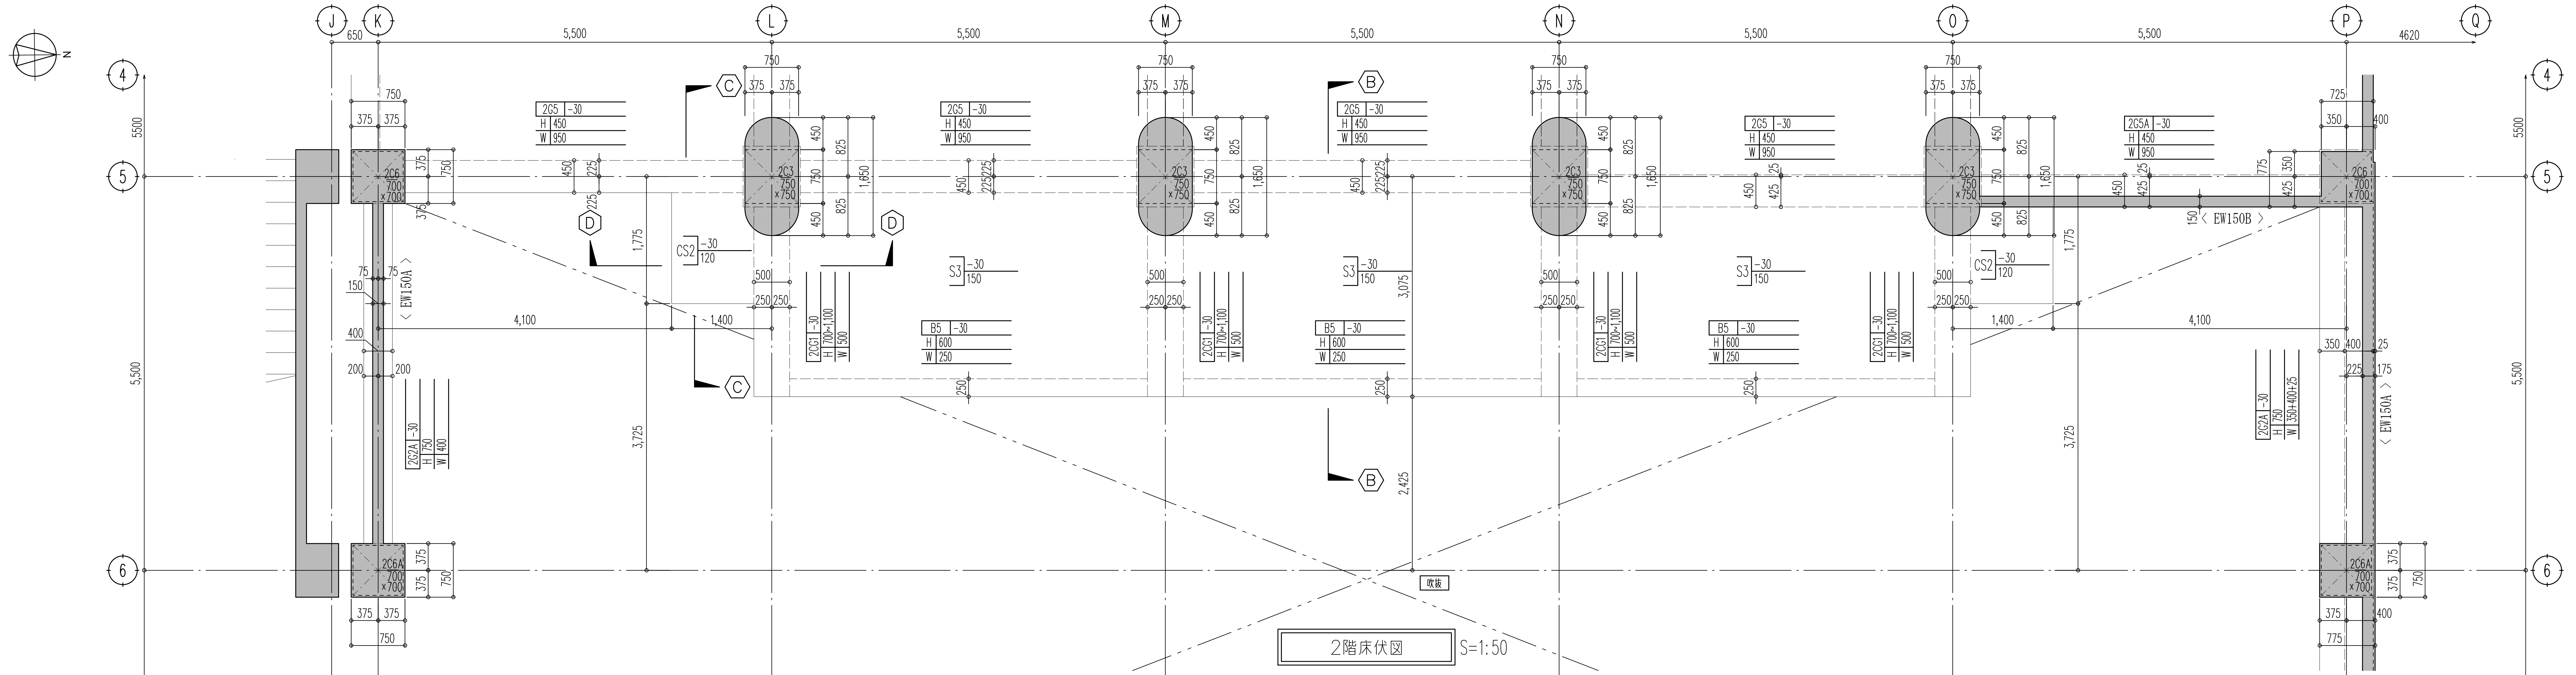

2階床伏図 S=1:50

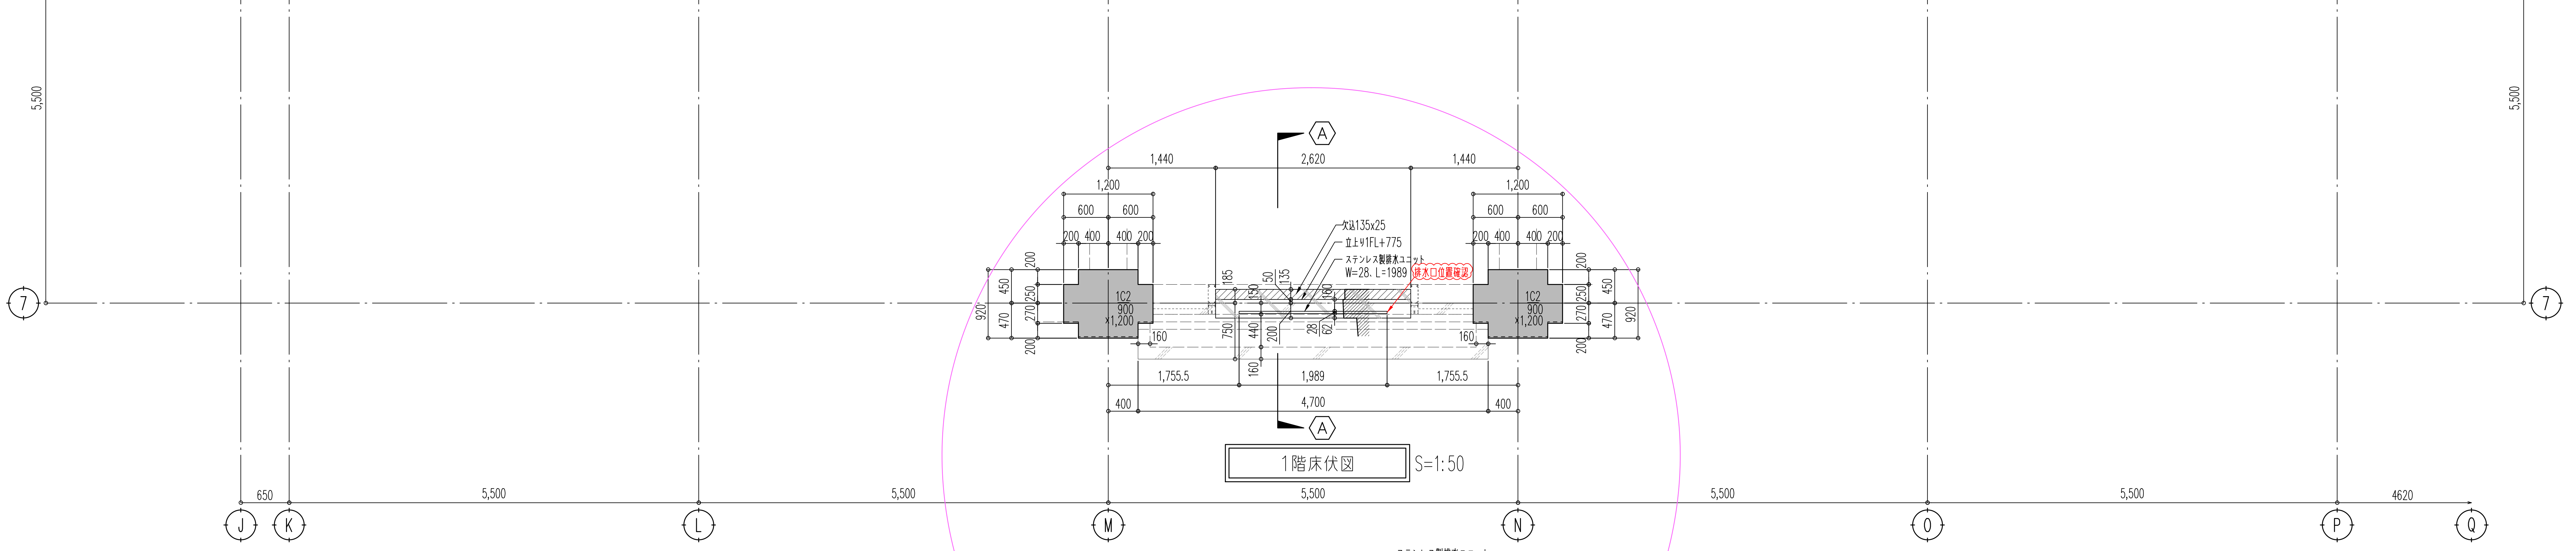

1階床伏図 S=1:50

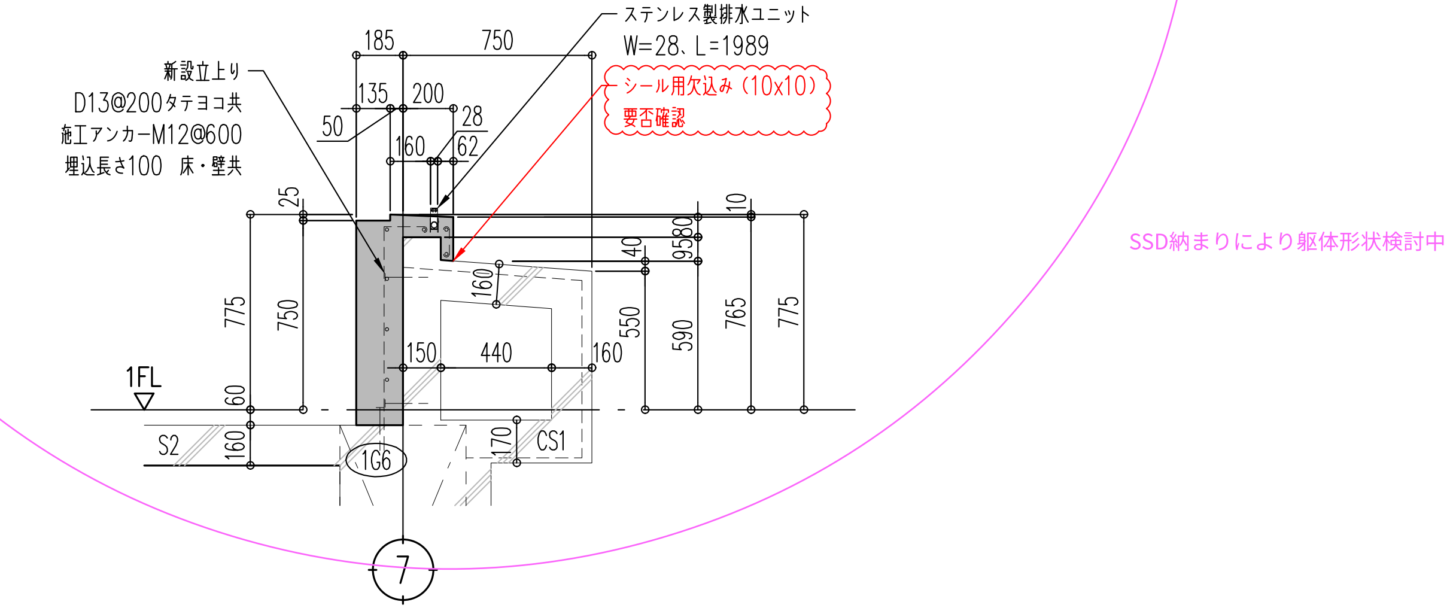

A－A 断面図 S=1:30

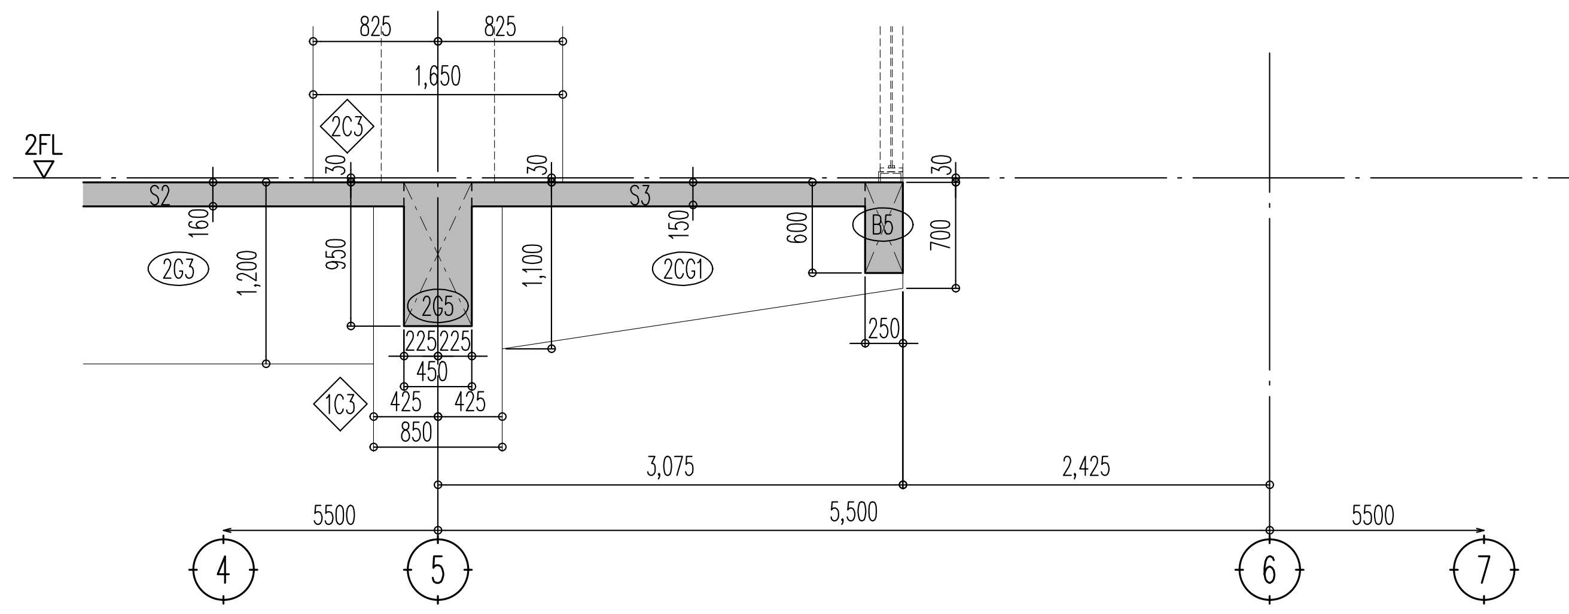

B－B 断面図 S=1:50

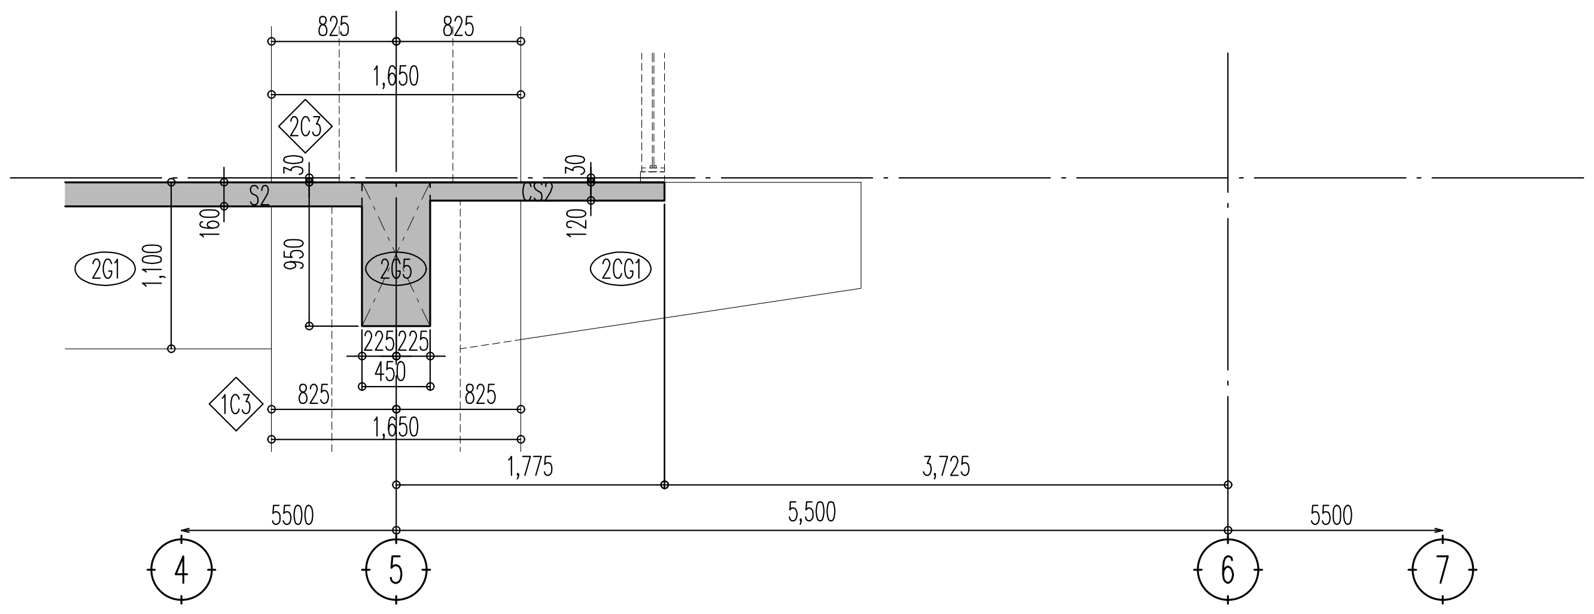

C－C 断面図 S=1:50

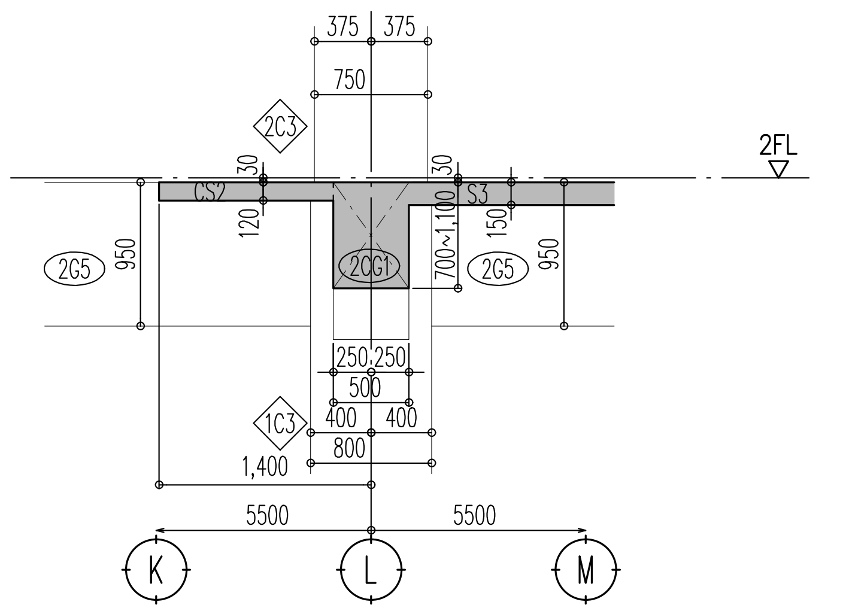

D－D 断面図 S=1:50

KEY PLAN

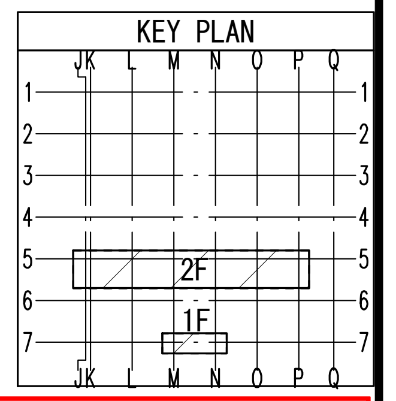

打合図 '26. 10. 06

設計図発行日 '26. 03. 27

チェック項目	未	完			
•FLの押えの統一			•巾木の逃げ		
•下げ梁　下げスラブ			•石．T．B（テラゾー　B）の逃げ		
•フロアーヒンジ			•SW．AW．SDの差筋・箱入		
•インサート・ルーフドレーン（打込み金物）			•SSの溝ボックス差筋箱入		
•防水立上り			•手摺子金物．アンカー差筋・箱入		
•ELV関連．箱入（押ボタン．ワイヤー穴）			•ブロック用差筋（床．天井．梁下．壁）		
•設備開口．及貫通孔			•断熱材の打込み		
•荷揚げ用仮穴．墨出し穴．足場用アンカー			•誘発目地・化粧目地		
•後打部（打継ぎ部）			•常開のSFD埋め込み（マグネット共）		
•掃除口穴（打継ぎ部梁底）			•		
•打放しフカシ・増打			•		

凡　例

<階高>
2FL
4,950
1FL

<杭 記号>

杭符号	φ	杭径
	h	基準高さからの杭天端高さ
	L	杭長さ

<基礎 記号>

基礎符号	T	基礎下端レベル
	H	基礎高さ

<柱 記号>
柱符号
柱幅－X軸
柱幅－Y軸
構造天端
※特記なき柱構造天端：FL－000

<梁 記号>

梁符号	基準高さからのCon天端レベル（構造天端）
H	上増打＋梁成＋下増打
W	左側増打＋梁巾＋右側増打

（特記事項：部分打ち増し等）

<耐圧盤 記号>
耐圧盤符号
基準高さからのCon天端レベル（構造天端）
天端フカシ厚さ＋版厚

<スラブ 記号>
スラブ符号
基準高さからのCon天端レベル（構造天端）
上増打＋スラブ厚＋下増打
（特記事項：断熱材等）

<壁 記号>
一般　W15
垂壁　壁符号　直上階基準高さからの垂壁下端高さ
腰壁　壁符号　基準高さからの腰壁天端高さ

<開口 記号>
H — 開口寸法　高さ
符号 — 開口符号
h — 基準高さから開口下端までの高さ
（特記事項）

FL
H
h
※アンカー＠５００以内

改訂履歴	改訂日	改訂ヶ所	改訂理由
第１回改訂			
第２回改訂			
第３回改訂			
第４回改訂			
第５回改訂			

配布ルール

1 変更の場合はこの原図を変更し、改訂履歴を明記する。
2 原図に配布予定先を記入する。
3 変更の都度、全部の配布予定先にコピーを配布する。
4 変更図（コピー）を受領したら旧版は自主廃棄する。

配布予定業者

承　認	審　査	作　成
現場管理責任者		担当者
受領日		

椙山女学園星が丘キャンパス大学会館食堂リニューアル工事

1階・2階床伏図

縮尺　A1:1/50　A3:1/100　'26. 10. 06

清水建設株式会社名古屋支店

躯体－０１