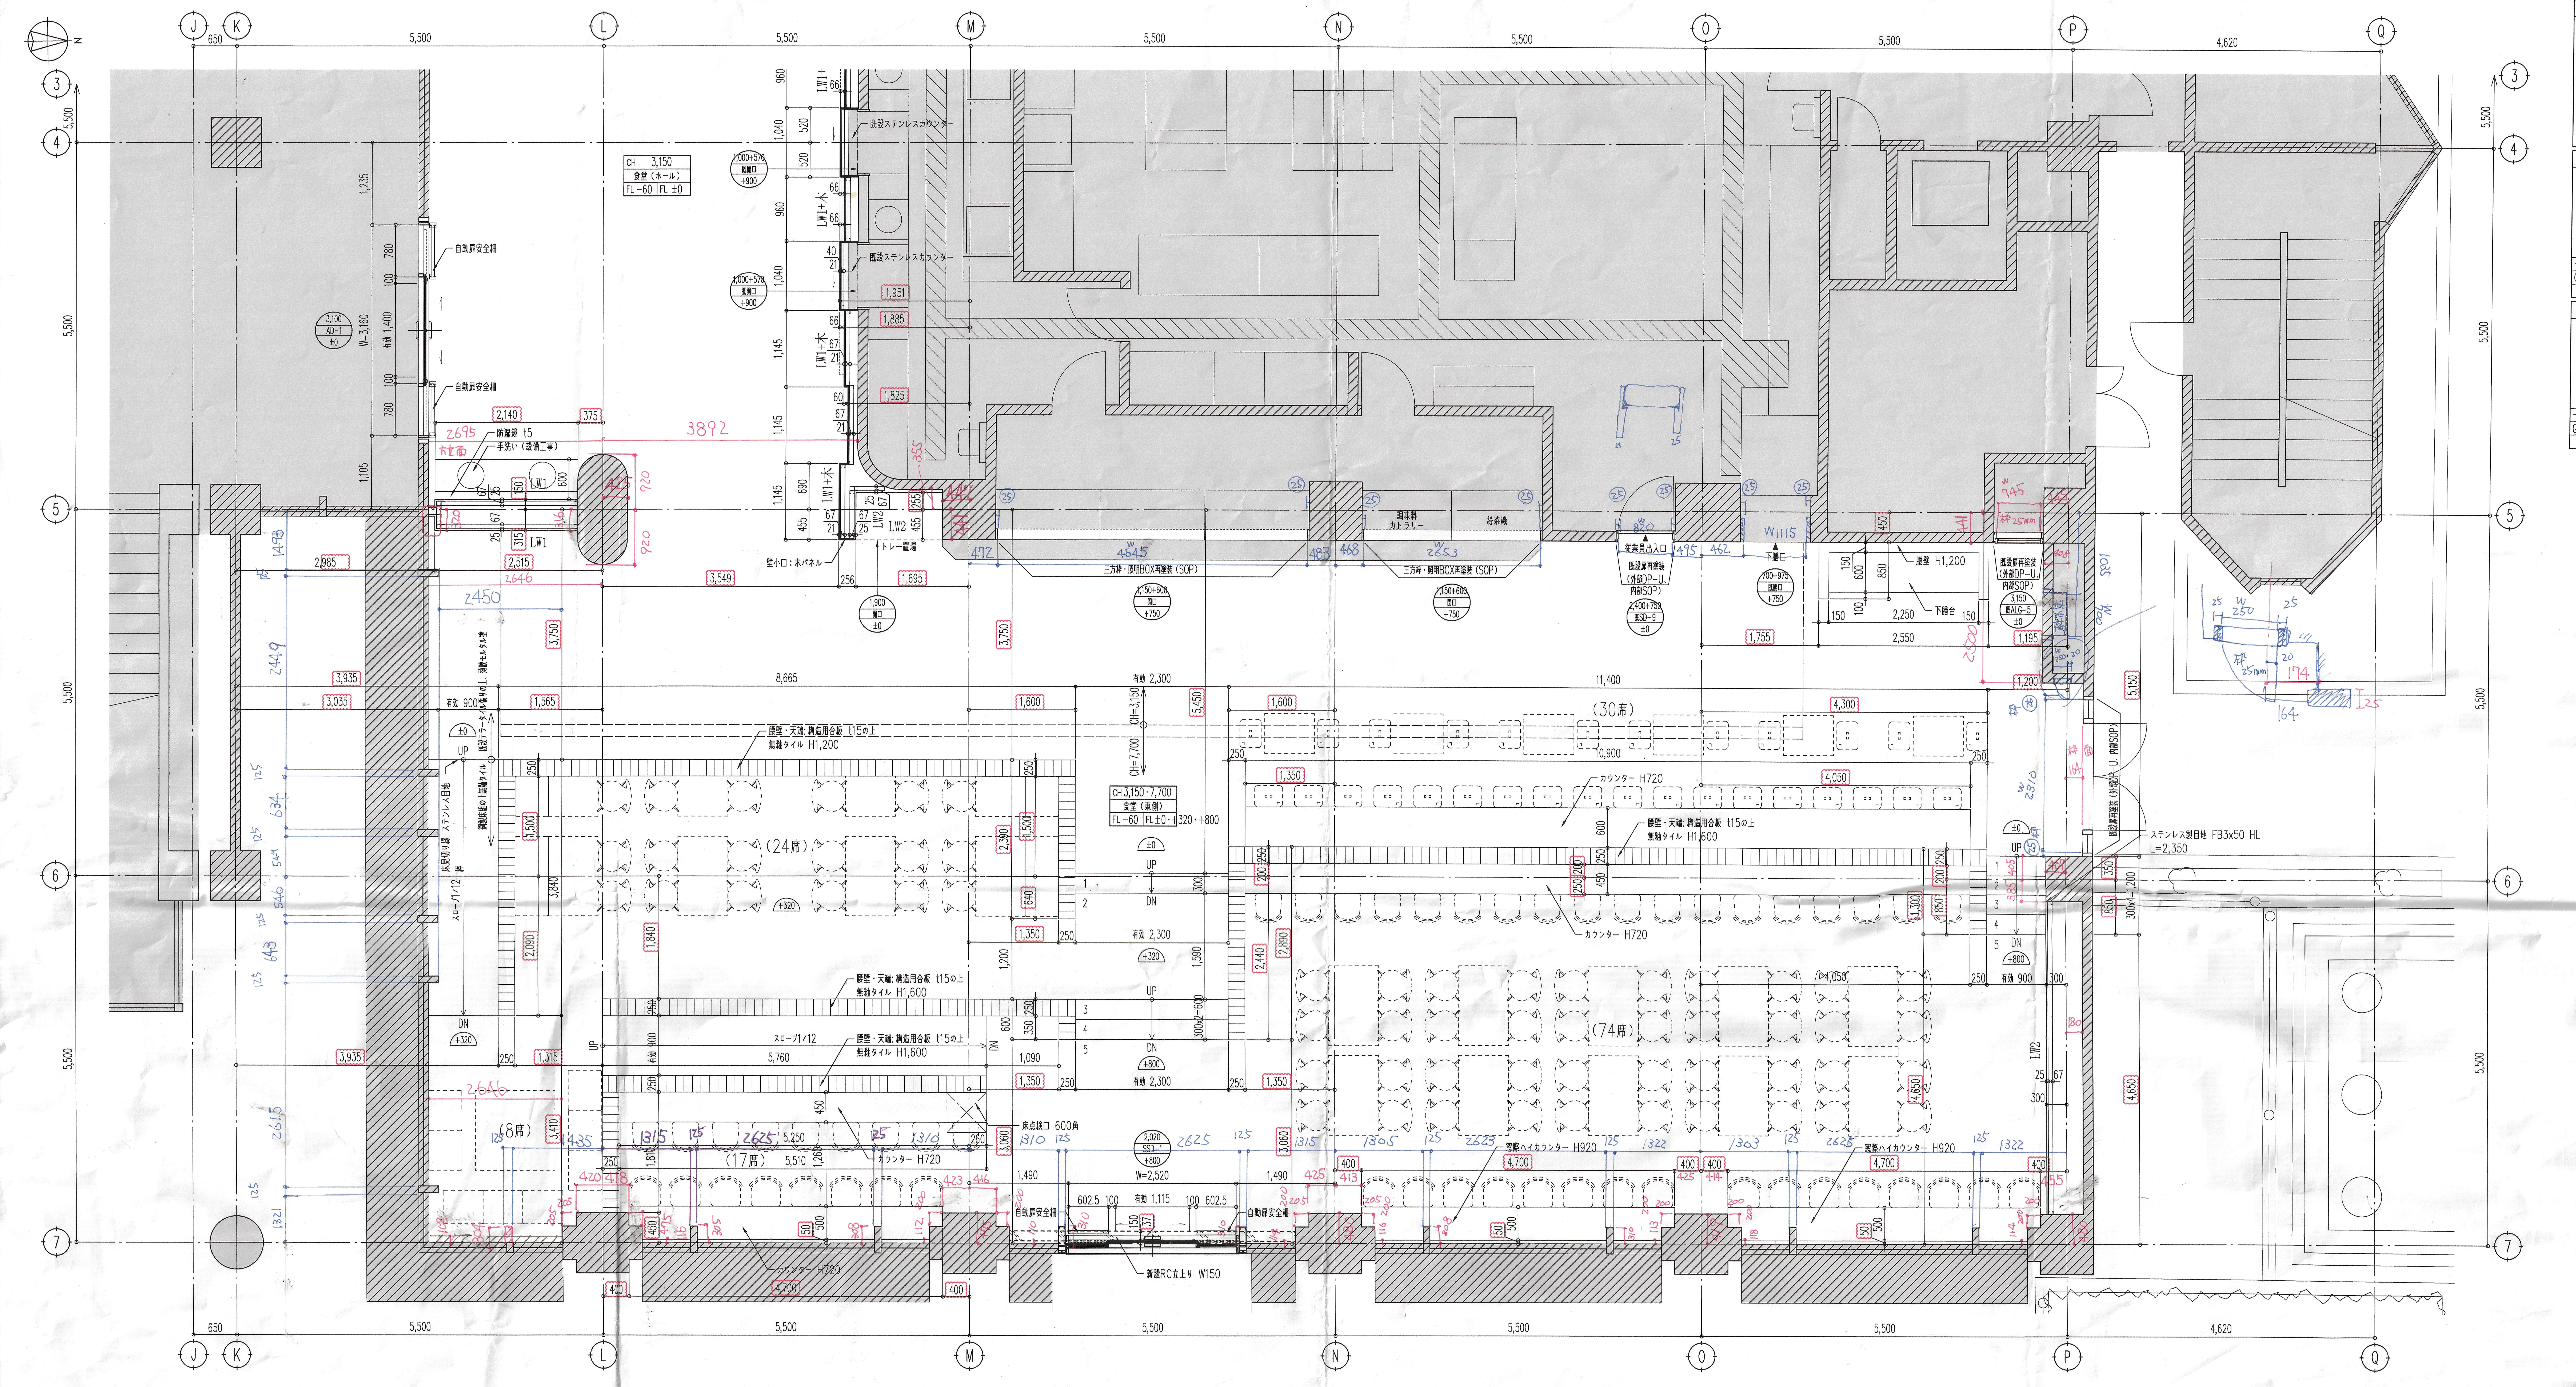
J
K
L
M
N
O
P
Q
3
4
5
6
7
650
5,500
4,620
既設ステンレスカウンター
自動扉安全柵
防湿鏡 t5
手洗い（設備工事）
CH 3,150
食堂（ホール）
FL −60 FL ±0
LW1
LW1+木
LW2
トレー置場
壁小口：木パネル
三方枠・照明BOX再塗装（SOP）
調味料
カトラリー
給茶機
従業員出入口
既設扉再塗装（外部DP−U、内部SOP）
下膳口
腰壁 H1,200
下膳台
(30席)
(24席)
(74席)
(17席)
(8席)
カウンター H720
腰壁・天端：構造用合板 t15の上 無釉タイル H1,200
腰壁・天端：構造用合板 t15の上 無釉タイル H1,600
CH 3,150・7,700
食堂（東側）
FL −60 FL ±0・+320・+800
スロープ1/12
床見切り縁 ステンレス目地
既設テラータイル張りの上 薄膜モルタル塗
鋼製床組の上無釉タイル
UP
DN
有効 900
有効 2,300
床点検口 600角
窓際ハイカウンター H920
新設RC立上り W150
ステンレス製目地 FB3x50 HL L=2,350
既設扉再塗装（外部DP−U、内部SOP）
2,020 SSD−1 +800
W=2,520
3,100 AD−1 ±0
W=3,160
有効 1,400
3892
2695
2646
2450
2449
2615
4545
2653
W1115
2625

壁記号凡例

- L 床～天井
- L スラブ～スラブ
- L 天井内 増張り
- L XX Y + Z
- MT：薄膜モルタル塗
- 木：木パネル t5・7・9

LW1

12.5+12.5 LGS

一般壁

GB−R t12.5+GB−R t12.5

LW2

12.5+12.5 LGS

一般壁

GB−R t12.5+GB−R t12.5

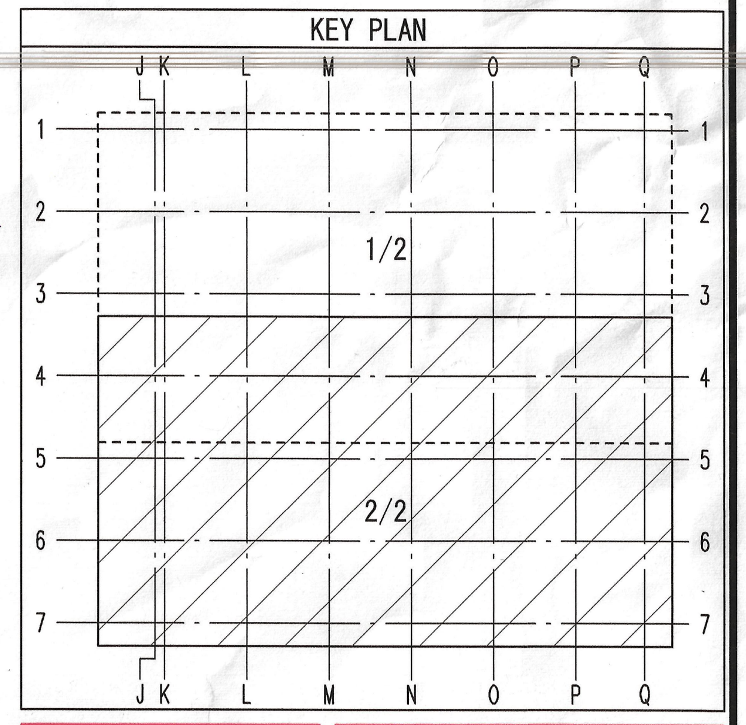
KEY PLAN
J K L M N O P Q
1
2
3
4
5
6
7
1/2
2/2

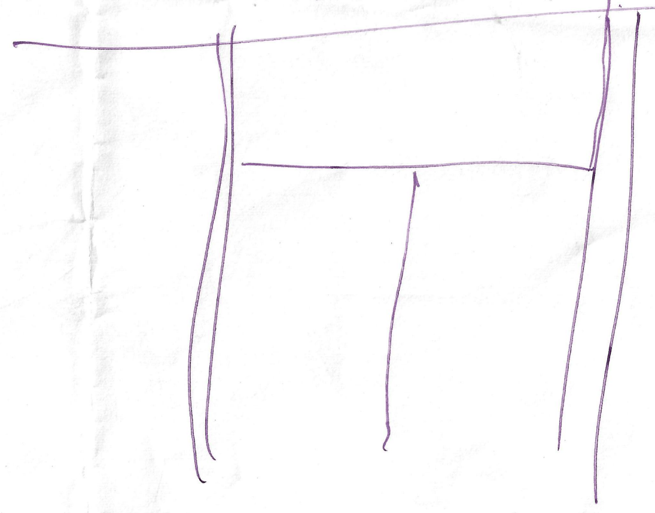

打合図	設計図発行日
'26. 10. 08	'26. 03. 27

ボード略号凡例

略号	内容
GB−R	石膏ボード
GB−R−H	普通硬質石膏ボード
GB−S	シージング石膏ボード
GB−F	強化石膏ボード
GB−L	石膏ラスボード
GB−D	化粧石膏ボード
GB−NC	不燃積層石膏ボード、不燃化粧石膏ボード
GB−P	吸音あなあき石膏ボード
GB−PD	化粧石膏吸音ボード
GB−R−Hc	吸放湿石膏ボード
K	けい酸カルシウム板
KB	化粧けい酸カルシウム板
RB	ロックウール吸音板

食堂（東側）	CH=3,150 CH=7,700	躯体レベル FL−60 仕上レベル FL±0・+320・+800
床	仕上	無釉タイル 既設テラータイル張りの上薄膜モルタル塗
	下地	鋼製床組+構造用合板 t15、コンクリート
巾木		不陸調整の上 樹脂巾木 H40
壁	仕上	GB−Rt12.5下地EP+吸音ルーバー 既設GB−Rt12下地ラフトンジャンボ吹付一部50角タイル張り
	下地	軽量鉄骨 の上薄膜モルタル塗
天井	仕上	GB−Rt12.5下地EP+吸音ルーバー GB−Rt12.5下地+リブDR t19、DR t9.0貼分け
	下地	軽量鉄骨
廻縁		塩ビ製
特記		−

食堂（ホール）	CH=3,150	躯体レベル FL−60 仕上レベル FL±0
床	仕上	既設テラータイル張りの上薄膜モルタル塗
	下地	コンクリート
巾木		不陸調整の上 樹脂巾木 H40
壁	仕上	木パネル 既設GB−Rt12下地ラフトンジャンボ吹付一部50角タイル張り
	下地	軽量鉄骨 の上薄膜モルタル塗
天井	仕上	DR t12 GB−Rt12.5下地EP+吸音ルーバー
	下地	軽量鉄骨
廻縁		−
特記		手洗いカウンター（設備工事）・鏡

チェック項目	未	完	・巾木の逃げ		
・FLの押えの統一			・石、T、B（テラゾー B）の逃げ		
・下げ梁 下げスラブ			・SW、AW、SDの差筋・箱入		
・フロアーヒンジ			・SSの溝ボックス差筋箱入		
・インサート・ルーフドレーン（打込み金物）			・手摺子金物、アンカー差筋・箱入		
・防水立上り			・ブロック用差筋（床、天井、梁下、壁）		
・ELV関連、箱入（押ボタン、ワイヤー穴）			・断熱材の打込み		
・設備開口、及貫通孔			・誘発目地・化粧目地		
・荷揚げ用仮穴、墨出し穴、足場用アンカー			・常開のSFD埋め込み（マグネット共）		
・後打部（打継ぎ部）			・		
・掃除口穴（打継ぎ部梁底）			・		
・打放しフカシ・増打			・		

凡例

<階高> 2FL 4,950 1FL

<室名 記号>

天井高さ	
室名	
躯体天端	床仕上天端

特記事項

<開口 記号>

H — 開口寸法 高さ
符号 — 建具符号
h — 基準高さから建具下枠の上端までの高さ

特記事項（電気錠等）

●● …扉の開き優先を示す。

記号	内容	C	ストリングスカーテン
⬭	保留を示す		
◠	床レベル（FL基準）		
∧	壁ボード目地		
▨	既存（壁・柱）を示す		
■	既存 を示す		

改訂履歴	改訂日	改訂ヶ所	改訂理由
第1回改訂			
第2回改訂			
第3回改訂			
第4回改訂			
第5回改訂			

配布ルール

1 変更の場合はこの原図を変更し、改訂履歴を明記する。
2 原図に配布予定先を記入する。
3 変更の都度、全部の配布予定先にコピーを配布する。
4 変更図（コピー）を受領したら旧版は自主廃棄する。

配布予定業者

承認	審査	作成
現場管理責任者		担当者

受領日

椙山女学園星が丘キャンパス大学会館食堂リニューアル工事

1階平面詳細図−2/2

縮尺 A1:1/50 A3:1/100 '26.09.16

清水建設株式会社名古屋支店

仕上−02

647
650