# 図面・計画書添付書

工事名

椙山女学園　星が丘キャンパス大学会館食堂リニューアル工事

| 図面名称 | | 躯体 | 仕上 | 設備 |
|---|---|---|---|---|
| | | 打合図 | 受領図 | 受領印用図 |
| サイン製作図 | | 発行日 | 返却希望日 | |
| 施工予定日 | 2027/03/01 | 2026/10/02 | 2026/10/09 | |

| | 発注者 | | | 施工部署 | | | | 生産技術部 | | 設備部 | |
|---|---|---|---|---|---|---|---|---|---|---|---|
| | | | | 現場管理責任者 | 工事長 | 主任 | 担当者 | 工事長 | 担当者 | 工事長 | 担当者 |
| 印 | | | | 承認 2026/10/07 金子　冬平 | | | | 承認 2026/10/01 小山　努 | | | |
| 日付 | | | | 10.7 | | | | | | | |

| | 設計責任者 | 工事監理者 | 工事監理担当者 | | | | | | | | | |
|---|---|---|---|---|---|---|---|---|---|---|---|---|
| | | | 意匠 | | 構造 | | 機械 | | 電気 | | | |
| 印 | | | | | | | | | | | | |
| 日付 | | | | | | | | | | | | |

記　事（質疑応答・連絡事項・その他）

0928

| S-15 | サイン［アクリル切り文字］ |
|---|---|
| H300 / 平付 | 30文字程度 |

和文：新ゴ R
英数：Rotis semi sons 55

文字ご指示下さい




アクリル切り文字［5.0t］
指定色塗装 3分ツヤ

■ 意匠図　S=1/3［A3］

| S-16 | サイン［塩ビシート］ |
|---|---|
| H100 / 壁直貼 | 20文字程度 |

和文：新ゴ R
英数：Rotis semi sons 55

文字ご指示下さい



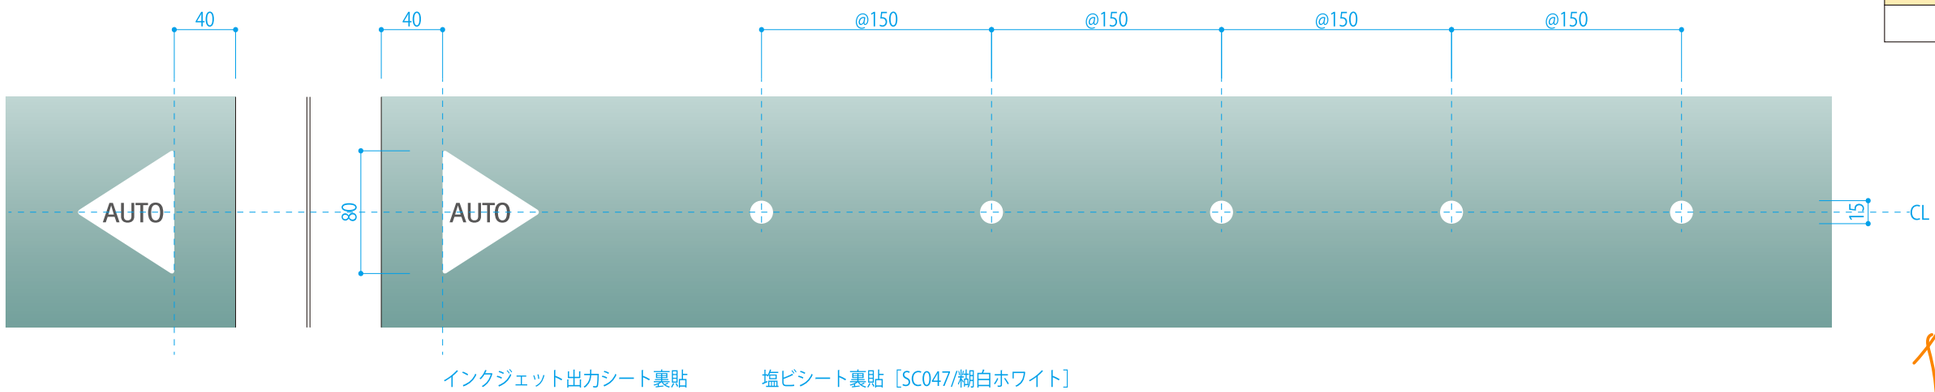

塩ビシート切り文字貼
［SC　　］

■ 意匠図　S=1/3［A3］


| 使用Font | | 設計 角田祐士 | Date 2026.09.18 | 工事名 椙山女学園大学 星ヶ丘キャンパス 食堂リニューアル工事に伴うサイン工事 | |
|---|---|---|---|---|---|
| | あなたが見上げる、その先に。 株式会社アイセイ社 | 営業 峯浦 | | 図名 サインアイテム図 | Scale S=1/　［A3］ | No. 01-01 |

| S-17 | 衝突防止サイン［塩ビシート］ | |
|---|---|---|
| | Φ15 @150 / ガラス裏貼 | 20 m |
| S-18 | 自動ドア表示止［インクジェットシート］ | |
| | H80 / ガラス裏貼 | 2ヶ所 |

和文：新ゴ R
英数：Rotis semi sons 55




■ 意匠図　S=1/4［A3］

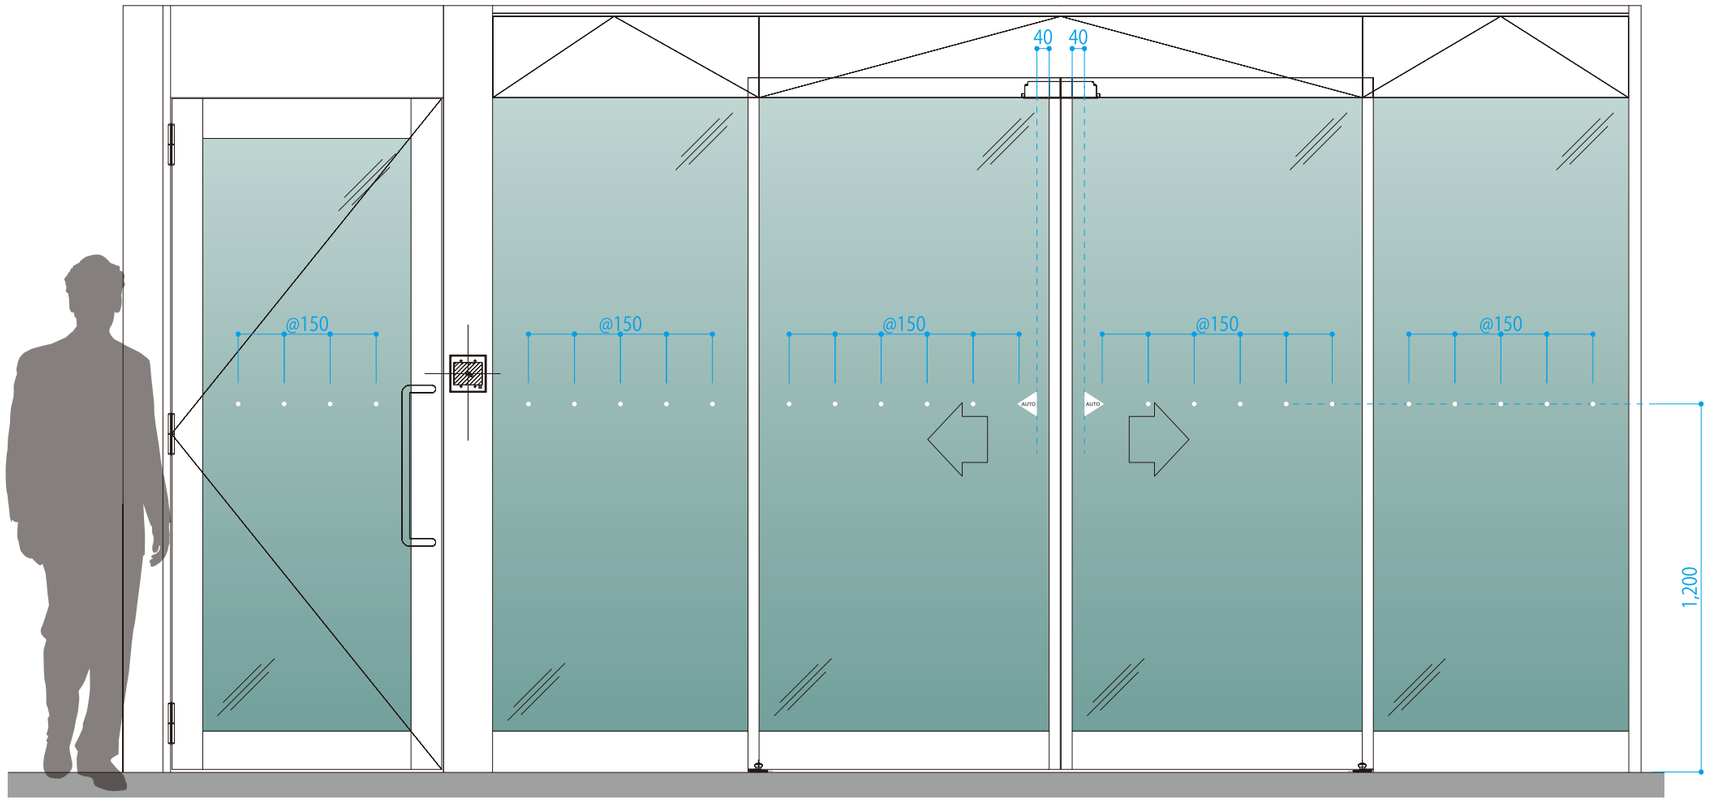


■ 意匠図　S=1/20［A3］

イメージよければ
ADとSSDの受領図に
作図して
受領図
提出します

| 使用Font | | 設計 角田祐士 | Date 2026.09.18 | 工事名 椙山女学園大学 星ヶ丘キャンパス 食堂リニューアル工事に伴うサイン工事 | | |
|---|---|---|---|---|---|---|
| | あなたが見上げる、その先に。 株式会社アイセイ社 | 営業 峯浦 | | 図名 サインアイテム図 | Scale S=1/　［A3］ | No. 01-01 |