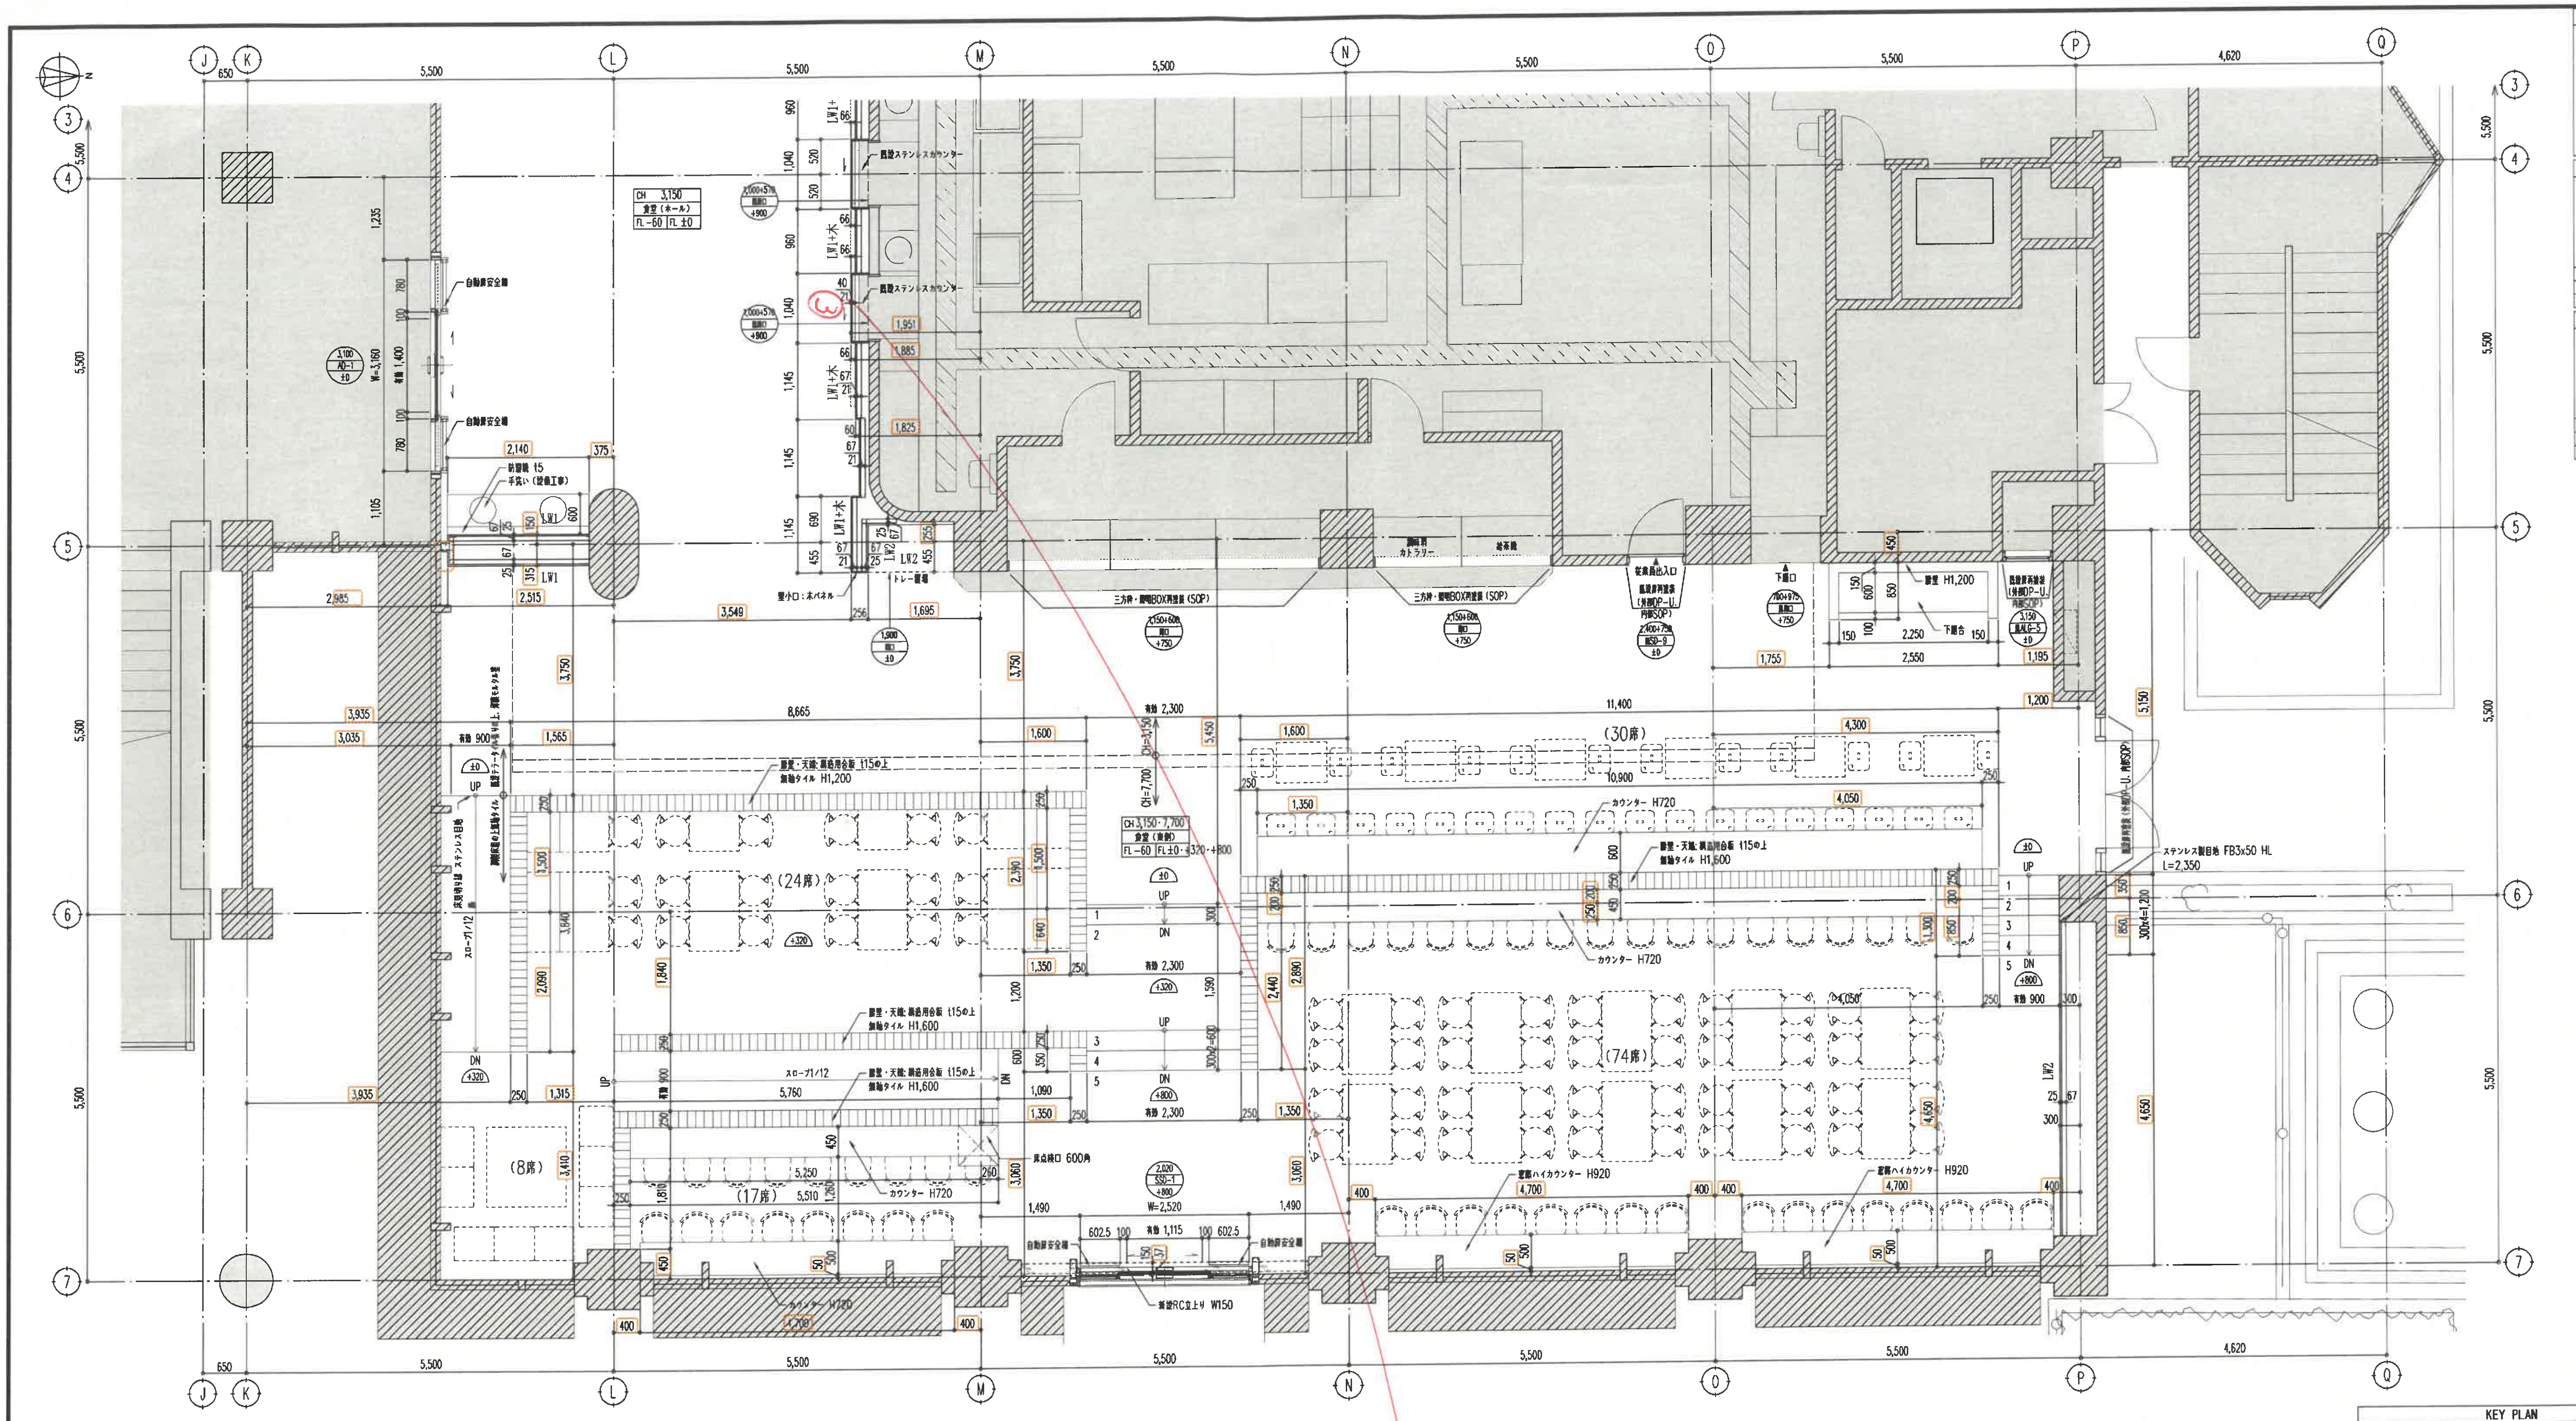
J
K
L
M
N
O
P
Q
3
4
5
6
7
650
5,500
4,620
CH 3,150
食堂（ホール）
FL-60 FL±0
既設ステンレスカウンター
自動扉安全機
3,100
AD-1
±0
W=3,160
三方枠・腰板BOX内部塗装（SOP）
トレー置場
(30席)
(24席)
(74席)
(8席)
(17席)
カウンター H720
壁面ハイカウンター H920
床置・天端：御影石本磨き t15の上
御影タイル H1,200
御影タイル H1,600
スロープ1/12
UP
DN
CH 3,150~7,700
食堂（東側）
FL-60 FL±0~+320~+800
ステンレス製目地 FB3x50 HL L=2,350
返却口 600角
W=2,520
既存RC立上り W150
11,400
8,665
5,760

壁記号凡例

- L 床～天井
- [L] スラブ～スラブ
- [L] 天井内
- [L][XX][Y]+[Z] 増張り
- MT：薄層モルタル塗
- 木 ：木パネル t5・7・9

LW1
12.5+12.5 LGS
一般壁
GB-R t12.5+GB-R t12.5

LW2
12.5+12.5 LGS
一般壁
GB-R t12.5+GB-R t12.5

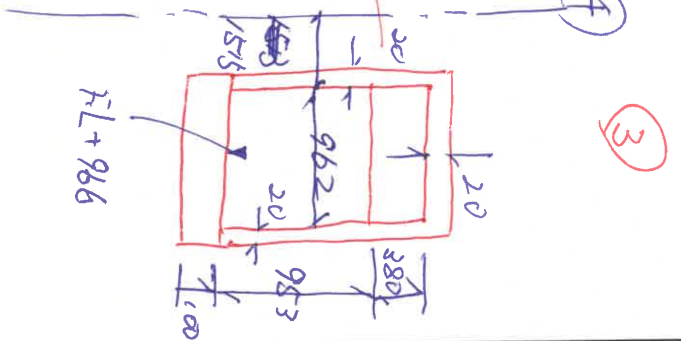
④
③
FL+966
1575
962
20
20
20
963
380
180

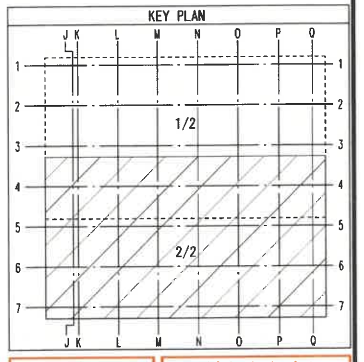
KEY PLAN
J K L M N O P Q
1
2
3
4
5
6
7
1/2
2/2

打合図
'26.10.08

設計図発行日
'26.03.27

ボード略号凡例

略号	内容
GB-R	石膏ボード
GB-R-H	普通硬質石膏ボード
GB-S	シージング石膏ボード
GB-F	強化石膏ボード
GB-L	石膏ラスボード
GB-D	化粧石膏ボード
GB-NC	不燃積層石膏ボード、不燃化粧石膏ボード
GB-P	吸音あなあき石膏ボード
GB-PD	化粧石膏吸音ボード
GB-R-Hc	耐水用石膏ボード
K	けい酸カルシウム板
KB	化粧けい酸カルシウム板
RB	ロックウール吸音板

食堂（東側）	CH=3,150 CH=7,700		FL-60 FL±0~+320~+800
床	仕上	磁器タイル 既設テラータイル張りの上薄層モルタル塗	
	下地	[illegible] t15、コンクリート	
巾木	不陸調整の上 [illegible]巾木 H40		
壁	仕上	GB-R t12.5下地EP+吸音ルーバー [illegible]	
	下地	軽量鉄骨	の上薄層モルタル塗
天井	仕上	GB-R t12.5下地EP+吸音ルーバー GB-R t12.5下地+リブDR t19、DR t19.0[illegible]	
	下地	軽量鉄骨	
廻縁	[illegible]		
特記	―		

食堂（ホール）	CH=3,150		FL-60 FL±0
床	仕上	既設テラータイル張りの上薄層モルタル塗	
	下地	コンクリート	
巾木	不陸調整の上 [illegible]巾木 H40		
壁	仕上	木パネル [illegible]	
	下地	軽量鉄骨	の上薄層モルタル塗
天井	仕上	DR t12 GB-R t12.5下地EP+吸音ルーバー	
	下地	軽量鉄骨	
廻縁	―		
特記	手洗いカウンター（設備工事）・鏡		

凡例

<階高> 2FL 4,950 1FL

<室名 記号> 天井高さ / 室名 / 躯体天端 床仕上天端 / 特記事項

<開口 記号> H 開口寸法 高さ / 符号 建具符号 / h 基準高さから建具下枠の上端までの高さ / 特記事項（電気設備）

記号	内容	C	ストリングスカーテン
⬚	保留を示す		
◠	床レベル（FL基準）		
∧	壁ボード目地		
▨	既存（壁・柱）を示す		
▭	既存 を示す		

改訂履歴	改訂日	改訂ヶ所	改訂理由
第1回改訂			
第2回改訂			
第3回改訂			
第4回改訂			
第5回改訂			

配布ルール
1 変更の場合はこの原図を変更し、改訂履歴を明記する。
2 原図に配布予定先を記入する。
3 変更の都度、全部の配布予定先にコピーを配布する。
4 変更図（コピー）を受領したら旧版は自主廃棄する。

配布予定業者

承認	審査	作成
現場管理責任者		担当者

受領日

椙山女学園星が丘キャンパス大学会館食堂リニューアル工事
1階平面詳細図-2/2
縮尺 A1:1/50 A3:1/100 '26.09.16
清水建設株式会社名古屋支店
仕上－０２