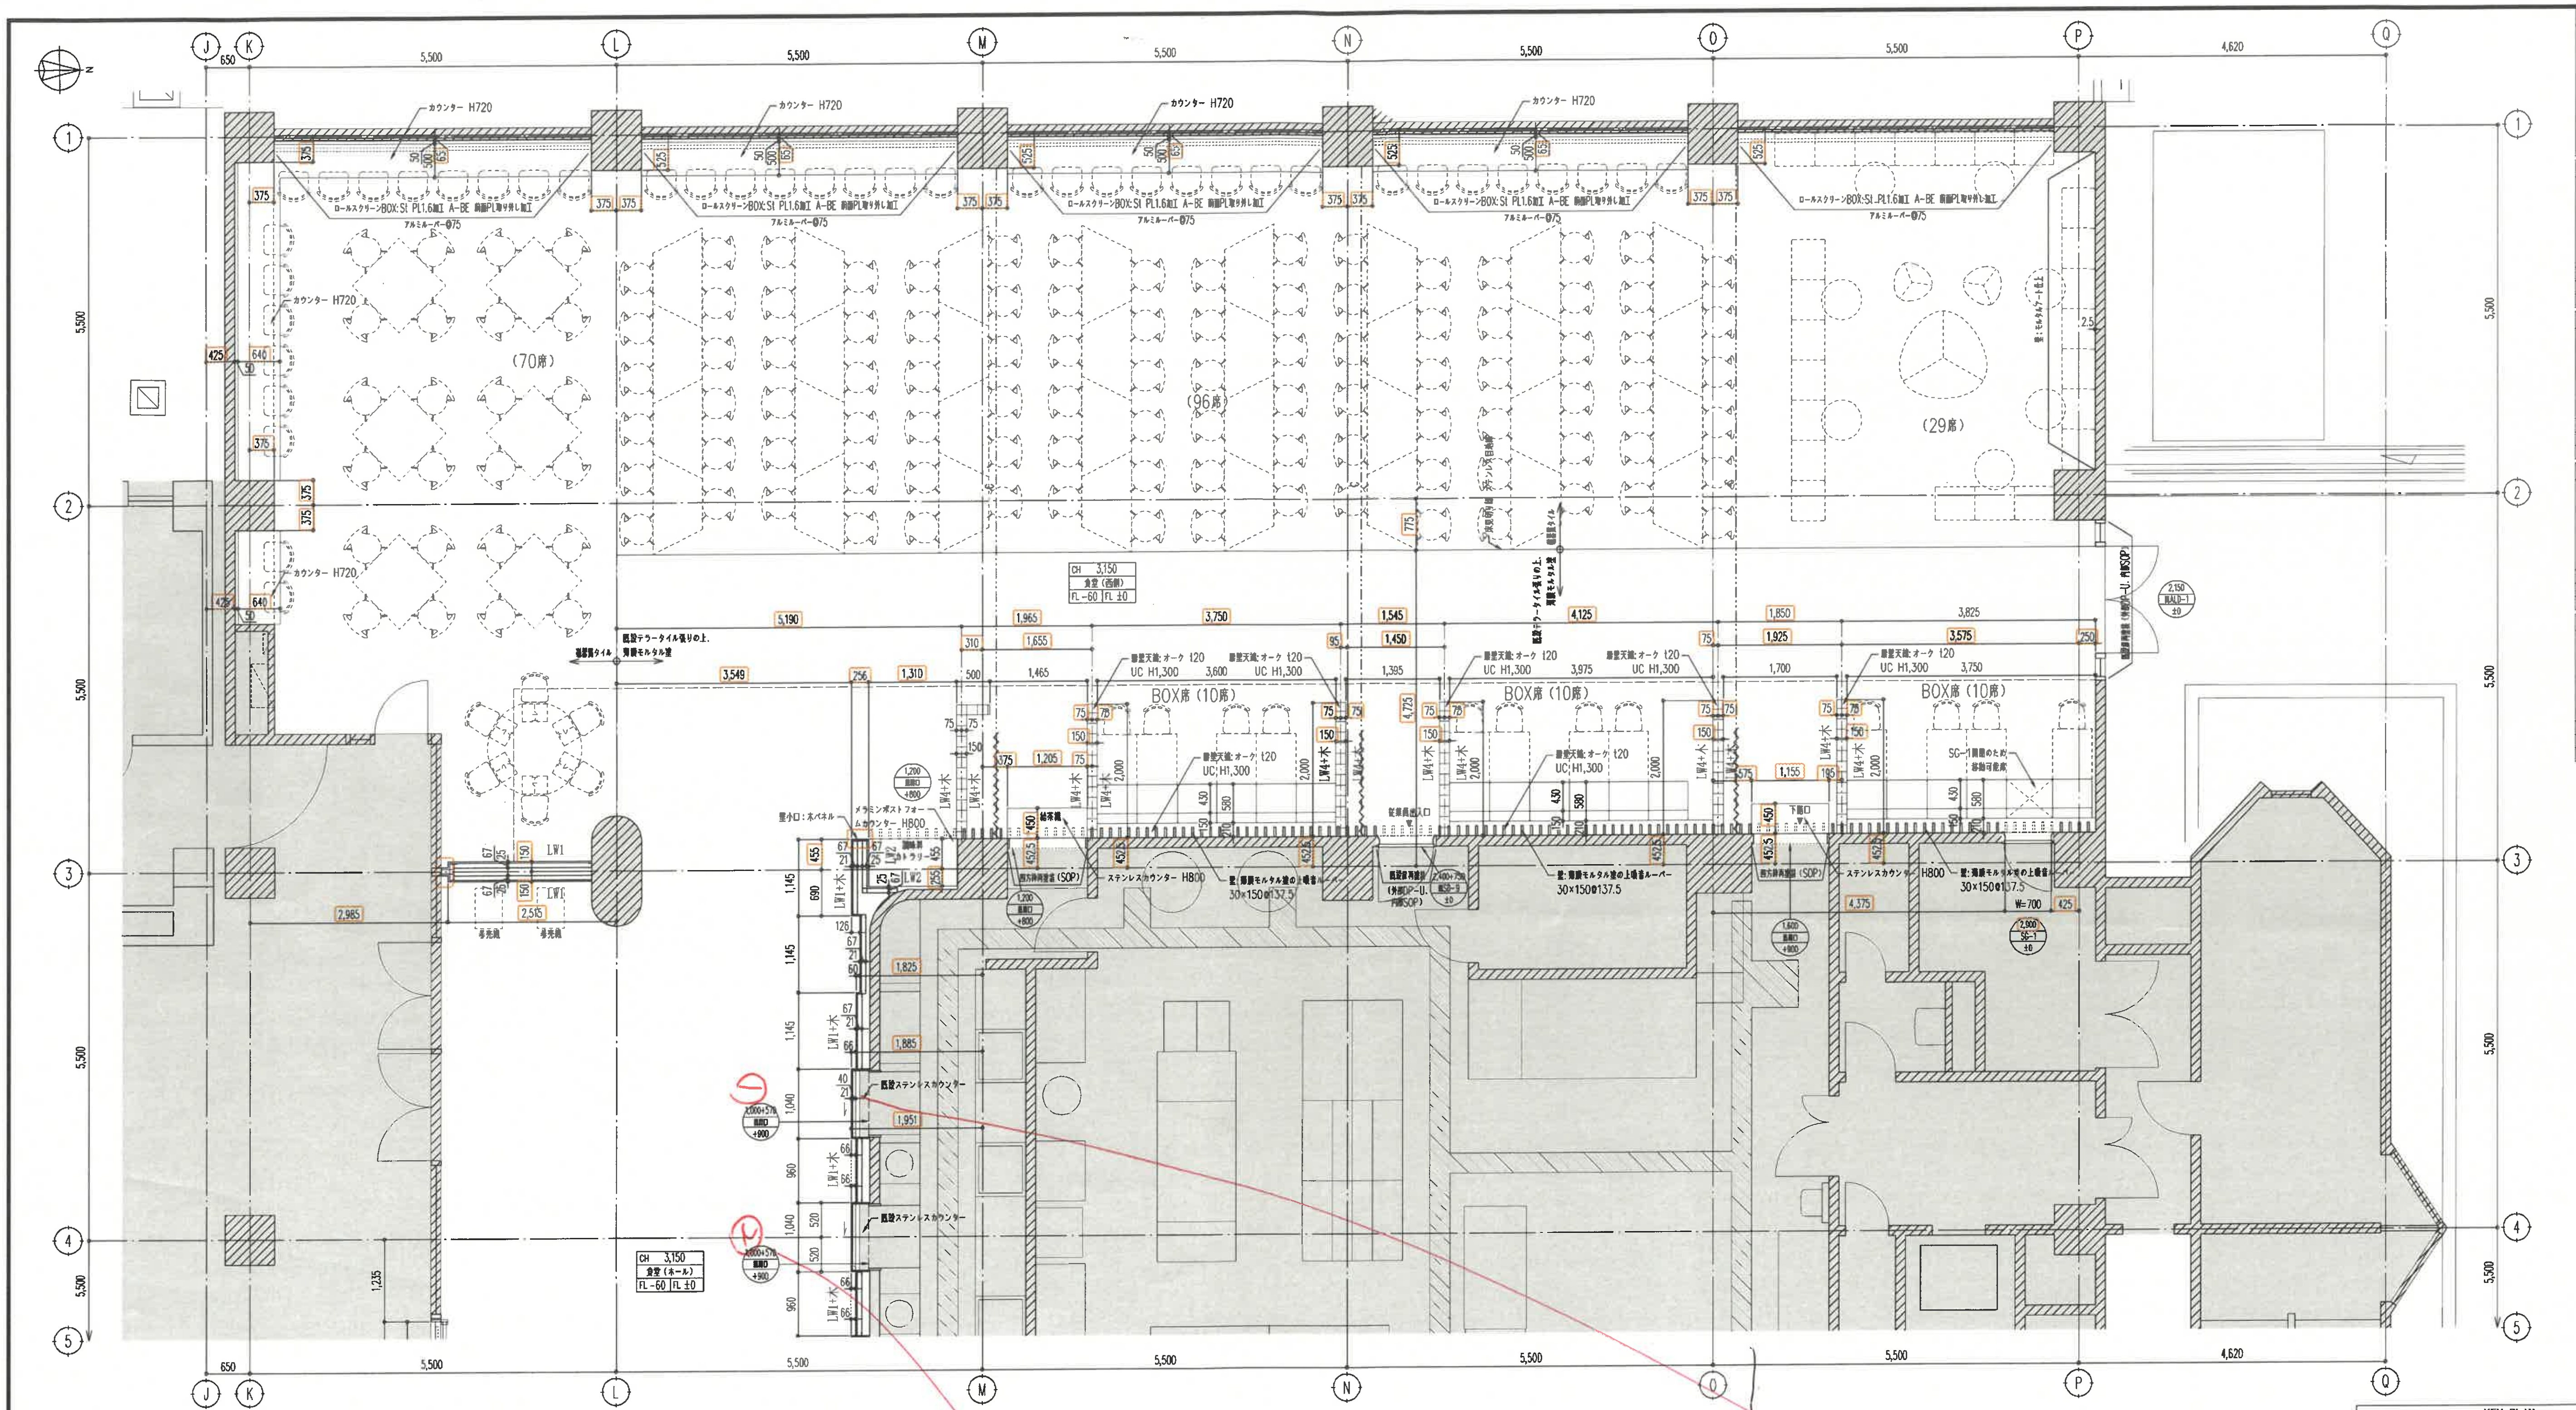

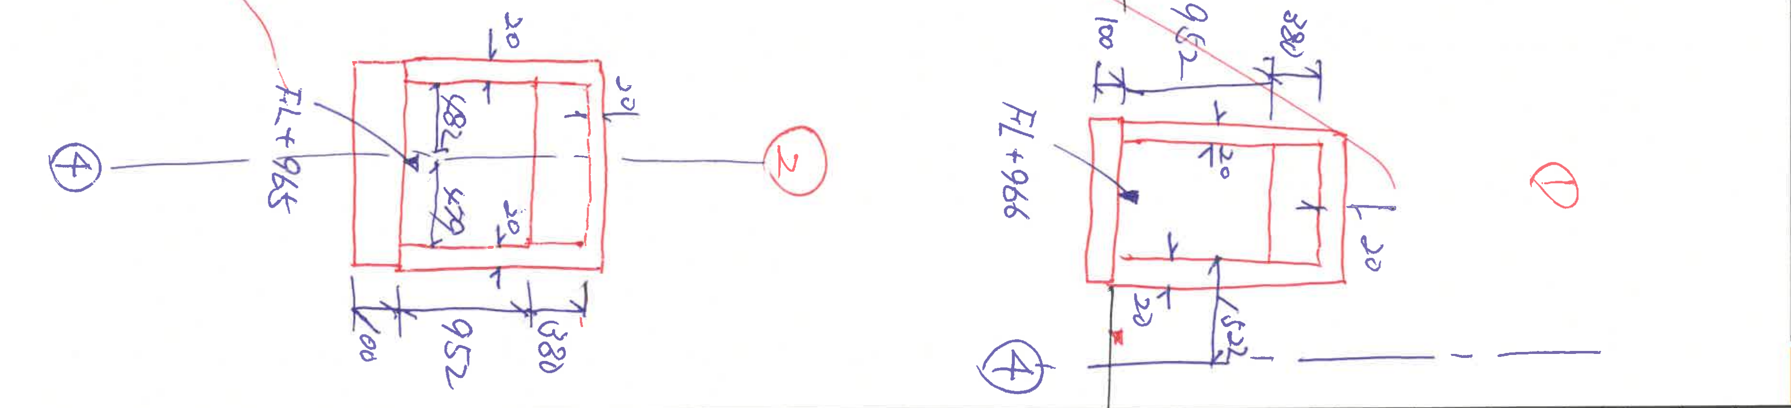

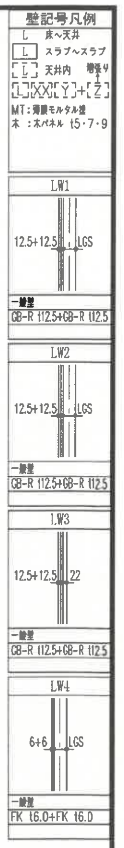
壁記号凡例

- L 床～天井
- L スラブ～スラブ
- L 天井内 増張り
- L XX Y + Z
- MT：薄膜モルタル塗
- 木 ：木パネル t5・7・9

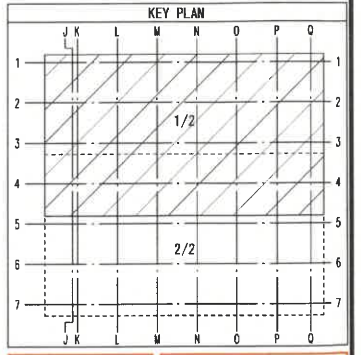
KEY PLAN

ボード略号凡例

略号	内容
GB-R	石膏ボード
GB-R-H	普通硬質石膏ボード
GB-S	シージング石膏ボード
GB-F	強化石膏ボード
GB-L	石膏ラスボード
GB-D	化粧石膏ボード
GB-NC	不燃積層石膏ボード、不燃化粧石膏ボード
GB-P	吸音あなあき石膏ボード
GB-PD	化粧石膏吸音ボード
GB-R-Hc	吸放湿石膏ボード
K	けい酸カルシウム板
KB	化粧けい酸カルシウム板
RB	ロックウール吸音板

食堂（西側）		CH=3,150	躯体レベル FL-60 仕上レベル FL±0
床	仕上	既設テラータイル張りの上薄膜モルタル塗 レベル調整モルタルの上磁器質タイル	
	下地	コンクリート	
巾木		不陸調整の上 磁器巾木 H40	
壁	仕上	吸音ルーバー 既設GB-R t12下地ラフトンジャン吹付～既50角タイル張り	
	下地	軽量鉄骨	●上部薄膜モルタル塗
天井	仕上	DR t12 GB-R t12.5下地EP+吸音ルーバー	
	下地	軽量鉄骨	
廻縁		塩ビ製	
特記		カウンター、腰方枠・三方枠再塗装、ストリングスカーテン +埋込カーテンレール、アルミルーバー+ロールスクリーン	

食堂（ホール）		CH=3,150	躯体レベル FL-60 仕上レベル FL±0
床	仕上	既設テラータイル張りの上薄膜モルタル塗	
	下地	コンクリート	
巾木		不陸調整の上 磁器巾木 H40	
壁	仕上	木パネル 既設GB-R t12下地ラフトンジャン吹付～既50角タイル張り	
	下地	軽量鉄骨	●上部薄膜モルタル塗
天井	仕上	DR t12 GB-R t12.5下地EP+吸音ルーバー	
	下地	軽量鉄骨	
廻縁		ー	
特記		手洗いカウンター（設備工事）・鏡	

凡　例

<階高>　2FL　4,950　1FL

<室名 記号>　天井高さ　室名　躯体天井｜成仕上天井　特記事項

<開口 記号>　H　符号　h　開口寸法 高さ　建具符号　基準高さから建具下枠の上端までの高さ　特記事項（電気設備等）

●●…扉の開き勝手を示す。

記号	内　容	C	ストリングスカーテン
⬚	保留を示す		
⌓	床レベル（FL基準）		
∧	壁ボード目地		
▨	既存（壁・柱）を示す		
▩	既存 を示す		

改訂履歴	改訂日	改訂ヶ所	改訂理由
第１回改訂			
第２回改訂			
第３回改訂			
第４回改訂			
第５回改訂			

配布ルール
1 変更の場合はこの原図を変更し、改訂履歴を明記する。
2 原図に配布予定先を記入する。
3 変更の都度、全部の配布予定先にコピーを配布する。
4 変更図（コピー）を受領したら旧版は自主廃棄する。

配布予定業者

承認	審査	作成
現場管理責任者		担当者

受領日

打合図 '26.10.08

設計図発行日 '26.03.27

相山女学園星が丘キャンパス大学会館食堂リニューアル工事

1階平面詳細図-1/2

縮尺 A1:1/50 A3:1/100　'26.09.16

清水建設株式会社名古屋支店

仕上－０１