1	特記仕様書（1）	—

特記仕様書の適用　追補

a.各特記事項の適用に関するルールは、次による。
1)⊙印の付いたものを適用する。
2)※印は、他の選択肢に○印のない場合に適用する。ただし、※の内容が標仕の内容を示すものである場合は標仕として扱い、他の設計図書に異なる記載がある場合は、その記載を優先する。
3)⊛印は⊙印と同義とする。
4)⊙印と⊛印の両方が付いた場合は、両方とも適用する。

b.各章の章・節・項の番号は、公共建築協会編「民間(七会)連合協定工事請負契約約款に適合した　工事共通仕様書　令和5年版」(以下、「共仕」という。)及び国土交通省大臣官房官庁営繕部監修「公共建築改修工事標準仕様書(電気設備工事編、機械設備工事編) 令和7年版」(以下、「改修標仕」という。)の当該番号に対応する。ただし、項番号の頭に“標”を付したものは、国土交通省大臣官房官庁営繕部監修「公共建築工事標準仕様書(建築工事編)令和7年版」(以下、標仕という)の当該項番号に対応する。

c.章、節、項のタイトル部分に示される注記の意味は、次による。なお、☐ はその章、節又は項の全体に対する注記を示し、[　]は、それを付された項目(号)のみに対する注記を示す。次に例示する。なお、[付加M]等のように、M又はPの文字を付された注記も、その意味はMやPを付されていない注記と変わらない。
1) 置換 :「共仕」、「改修標仕」の当該章、節、項の規定全体を、改修特記仕様書(以下、「改修特仕」という。)の当該規定と置換する。
2) [(b)(2)置換]:「共仕」、「標仕」の(b)(2)号の規定を、「改修特仕」の当該規定と置換する。特仕本文で置換内容を示した場合は、[置換]とする場合がある。
3) 付加 :「共仕」、「改修標仕」に「改修特仕」の当該規定を新規追加する(新設の章、節、項)。
4) [付加]:「共仕」、「改修標仕」に「改修特仕」の当該規定を号単位で追加する。ただし「改修標仕」の当該号が明らかな場合は[(c)付加]のように表示することもある。
5) 追補 :「共仕」、「改修標仕」にない当該規定を新規追加する(新設の章、節、項)。

d.「改修特仕」において、「共仕」又は「改修標仕」等の項番号を引用する場合は、“共仕[○. ○. ○]”、“改修標仕[○. ○. ○]”等と表記する。

e.「共仕」、「改修標仕」及び「改修特仕」において、「共仕」又は「改修標仕」の項番号等を引用している場合で、引用された「共仕」又は「改修標仕」の規定に対して「改修特仕」で追加、読替え等を行っている場合は、それらも併せて適用する。

f.特記事項に示す［表・・］［図・・］の番号は、「共仕」又は「改修標仕」の当該表又は図の番号を表す。

g.「改修標仕」及び「改修特仕」8章耐震改修工事の規定は、耐震改修工事のほか、それ以外の構造関連改修工事にも適用する。ただし、他の特記により適用を除外されるものは除く。

h.「改修特仕」12章シックハウス対応の特記内容と、他の部分の特記内容に相違がある場合は、他の部分の特記が優先する。また、「改修特仕」12章と「改修標仕」の各章の規定に相違がある場合は、「改修特仕」12章の規定が優先する。

第1編　一般共通事項

・第1編　一般共通事項については意匠図の特記仕様書による

3.3 電気設備工事特記仕様書

第1編　一般共通事項　（電気）

第1章　一般事項　（電気）

第1節　総則

1.2.4 工事の記録等

報告書に用いる書式等
※提出書類作成要領・受注者検査要領23による　・

改修標仕　第1編　一般共通事項　（電気）

改修標仕　第1章　一般工事　（電気）

改修標仕　第7節　養生

1.7.1 養生範囲

a.既存部分の養生範囲
※設計図による　⊙意匠図による
ただし、改修工事の着手に当たり、既存物(什器、備品等含む)の損傷等を防止するために、工事作業ごとに養生方法や養生範囲を計画した工事養生計画書を作成し、監理者の承認を受ける。また、養生で使用する材料見本を事前に監理者に提示し確認を受ける。

1.7.2 養生方法及び清掃

a.養生方法
・設計図による
※ビニル床シート、合板、プラスチック製養生ボード、養生シート、養生マット等の適切な方法で行う
b.固定された備品、机、ロッカー等の移動
※行わない　・行う(・設計図による　・　)
c.既存家具等の(固定された備品、机、ロッカー等含む)養生
※設計図による
・ビニル床シート　・プラスチック製養生ボード　・養生シート　・養生マット
d.機材搬入通路及び撤去機材搬出通路の養生
※床面等に合板、ビニル床シート等の適切な方法で養生し、工事終了後に清掃を行う
・

改修標仕　第8節　撤去

1.8.1 一般事項

a.撤去前に内容物(発電機燃料、廃油等)の回収を要する機器、配管
回収を要する機器、配管　※設計図による
内容物の回収等の費用　※本工事　・別途

1.8.2 撤去作業の安全対策

a.石綿含有建材の撤去作業
石綿含有建材の撤去作業は、改修標仕(建築工事編) 9章 環境配慮改修工事 1節 石綿含有建材の除去工事に従う。

改修標仕　第9節　発生材の処理等

1.9.1 一般事項

a.発生材の処理
・発注者に引渡しを要するもの　・有(　)　※無
b.再利用
・現場において再利用を図るもの　・有(　)　※無
c.再資源化
・現場において再資源化を図るもの　・有(　)　※無
なお、再資源化を図るものは、分別を行い、所定の再資源化施設等に搬入する。また、搬入したものの調書を作成して監理者に提出する。
d.特別産業廃棄物の有無及び処理方法
・有(処理方法：　)　※無

第4節　コンクリート工事

2.4.1 一般事項

a.コンクリートの設計基準強度
※18 N/㎟ 以上　・(　) N/㎟ 以上

第7節　塗装工事

2.7.1 一般事項

a.現場で行う塗装の色合わせ
※行わない　・行う(　)
b.現場で行う塗装箇所
さび止め塗装が施された金属製プルボックス等の機材（露出部）
・なし　・
亜鉛めっきが施された機材（露出部）
・なし　・
めっき又は塗装が施されていない金属配管等の機材（露出部）
・なし　・
めっき又は塗装が施されていない金属配管等の機材（隠ぺい部）
・なし　・

第9節　スリーブ工事

2.9.1 付加 スリーブ

a.材料・形式等
・設計図による
※下表による（設計図に記載がある場合を除く）

表　型枠に設ける配管用等のスリーブの使用箇所と材料

使用箇所	材料
外壁貫通部（地上）	⊙つば付きステンレス鋼管 ・設計図による
地下外壁（梁部とも）貫通部	※つば付き鋼管 ・つば付き防水鋳鉄管 ・つば付きステンレス鋼管 ・硬質ポリ塩化ビニル管(・非加硫ブチルゴム系止水材巻付け　・水膨張性ゴム系止水材巻付け） ⊙つば付き溶融亜鉛めっき鋼管（HDZ55） ・
地中で水密性を要しない貫通部	※硬質ポリ塩化ビニル管
屋内一般部	※溶融亜鉛めっき鋼板製又は硬質ポリ塩化ビニル管 ・鋼管（白管）
屋内外一般部（柱梁以外で開口補強が不要な200Φ以下のもの）	※紙製仮枠（取り除き） ・
地下2重ピット、床下配管ピット内（水槽を除く）、免震ピット	※硬質ポリ塩ビニル管 ・
水槽部分ほか水密性が必要な貫通部	・硬質ポリ塩化ビニル管(・非加硫ブチルゴム系止水材巻付け　・水膨張性ゴム系止水材巻付け） ⊙つば付き溶融亜鉛めっき鋼管（HDZ55）

注1）溶融亜鉛めっき鋼板製の円形スリーブは、原則として、筒形の両端を外側に折り曲げてつばを設ける。円筒部を両方から差し込む伸縮形も可とする。
注2）防火区画等の貫通部は、硬質ポリ塩化ビニル管は用いない。
また紙製仮枠の場合は必ず取り除く。

1)工事の着手に先立ち建・電・機の共通の施工計画書、施工図を作成し、監理者の確認を受ける。
2)スリーブ及び止水材等の仕様は、施工部位、工種により適切な材料・形状の物を使用する。

第10節　インサート

2.10.1 一般事項

a.許容引抜荷重（コンクリート圧縮強度が18 [N/㎟] の場合
M10　※2,000 [N] 以上　・
M12　※4,400 [N] 以上　・
M16　※6,500 [N] 以上　・
ただし、M10に代えて W3/8 を採用する場合には、断面積の比に応じた引抜き荷重を確保する。

2.10.2 材料　[付加]

a.アンカー金物の品質は次による。
1)基礎ボルトは、JIS B 1178による。
2)インサート金物は、鋼製又は鋳鋼製で防錆処理を施したものとする。ただし、暗きょ（床下ピット、トレンチ等）、多湿箇所、免震層等ではステンレス製とする。
3)水湿及び腐食のおそれのある部分に使用するアンカー金物は、ステンレス製（SUS304又はSUS316）又は溶融亜鉛めっき（HDZT49(JIS H 8641)）を施したものとする。

第11節　あと施工アンカー　追補

2.11.1 あと施工アンカー

a.原則としてあと施工アンカーは使用しない。
b.使用する場合には、工事の着手に先立ち施工計画書を作成し、監理者の承認を受ける。耐震計算書と施工状況を照合し、自主検査記録書を作成し監理者に提出する。
c.あと施工アンカーの性能試験及び施工後確認試験は、監理者と協議する。
d.あと施工アンカーの施工管理には、工事内容に相応した施工の指導を行う施工管理技術者を置く。受注者は、日本建築あと施工アンカー協会の資格を有する者か、又はあと施工アンカーについて十分習熟し、かつ十分な技能及び経験を有する者が施工を行う。
e.あと施工アンカーの適用は、以下のとおりとする。
1)あと施工アンカーの選定は、日本建築センター「建築設備耐震設計・施工指針」2014年版、空気調和・衛生工学会「建築設備用あと施工アンカー SHASE-S 012」に準拠するとともに、日本建築あと施工アンカー協会(JCAA)の認証品を使用する。また、選定したあと施工アンカー製造者による実技講習会を開催し、受注者は使用するあと施工アンカーの製品知識と十分な技能を習得し施工する。また、許容引抜荷重の計算では、第一種、第二種軽量コンクリートが使用される場合は、一割程度裕度ある選定を行う。
2)あと施工金属拡張アンカーは、おねじ型(スリーブ打込み式、ウェッジ式)とする。やむを得ずめねじ型を使用する場合は、内部コーン打込み式とし、支持重量は20kg以下を原則とする。
3)あと施工接着系アンカーの固着剤は、カプセル方式を原則とし、耐薬品性・耐熱性等の施工条件を考慮して選定する。また、接着系アンカーは配管、ダクト、機器等の天井吊り下げ用及び重量の大きい機器、配管等を支持する壁付ブラケットなどの常時引抜力の掛るボルトに使用してはならない。
4)雨掛りとなるあと施工アンカー部分では、取り合い部分にシーリングを行い、止水処理を行う。
5)防水保護コンクリートへのあと施工アンカーは行わない。やむを得ずあと施工アンカーとする場合は、防水層、鉄筋、埋設配管類に対し損傷影響がない旨の資料を作成し、監理者の承認を受ける。
6)あと施工アンカーは、梁底に打ち込むことを禁止する。
7)コンクリート基礎にあと施工アンカーを打ち込む場合は、事前にコンクリート基礎の配筋状態を確認し、あと施工アンカーが配筋に当たらないようにする。
8)そのほか、改修標仕[第2編 第5章 インサート及びアンカー]に準拠して施工を行う。
9)上記原則以外のことを行う場合は、監理者と協議する。
f.あと施工アンカーを使用する場所における埋込み配管等の探査の範囲及び方法は場所ごとに監理者と協議する。
g.重量機器類のアンカーは、先付アンカーを原則とする。
h.設備工事の共通支持部材用のアンカーボルトやインサートは、原則建築工事に依頼する。
i.配管、ケーブルラック等の吊り用共通支持架台等は、インサートを原則とする。
j.合成スラブ構造用デッキプレートにインサート及びあと施工アンカーを取付ける場合は、原則下図のようにデッキプレートの割付図を確認しデッキプレートの山部に取付ける。

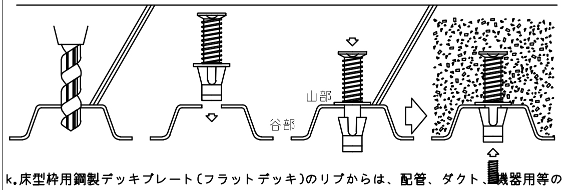

k.床型枠用鋼製デッキプレート(フラットデッキ)のリブからは、配管、ダクト、機器用等の荷重を支持しない。

2.12.4 塗料

a.屋内に用いる塗料は、水性系でホルムアルデヒドの放散量等級がF☆☆☆☆のものとする。またトルエン・キシレン・エチルベンゼンは放散しないか、放散が極めて少ないものとする。やむを得ず、これらの物質を含むものを使用する場合は、その使用量が最小限に抑えられたものとし、十分に枯らし期間を設けるなど改善措置を講ずる。

2.12.5 接着剤

a.各所に用いる接着剤は、ホルムアルデヒド・トルエン・キシレン・エチルベンゼンを含まないものとする。また接着剤に含まれる可塑剤は，フタル酸ジ-n-ブチル・フタル酸ジ-2-エチルヘキシルを含有しない難揮発性のものとする。ただし、設計図又は特仕の指定によりエポキシ樹脂系接着剤を使用する場合は、これらの物質の使用量が最小限に抑えられたものとし、十分に枯らし期間を設けるなど改善措置を講ずる。

2.12.6 施工中の措置

a.施工中、通風・換気(機械換気等を含む)を行い、ホルムアルデヒド・VOCの放散を促進させる。また、必要によりVOC低減のため適切な改善措置を講ずる。

2.12.8 室内設備関連工事におけるシックハウス対応

a.室内設備関連工事については、建築・設備工事の発注区分にかかわらず、相互調整により次のシックハウス対応を行う。
b.室内における配管類・盤・機器等の塗料及び接着剤は、露出・隠ぺい部分ともにホルムアルデヒド・トルエン・キシレン・エチルベンゼンを含まないものとする。また、接着剤に含まれる可塑剤は、フタル酸ジ-n-ブチル・フタル酸ジ-2-エチルヘキシル等を含有しない難揮発性のものとする。やむを得ずこれらを含むものを使用する場合は、その使用量が最小限に抑えられたものとし、十分に枯らし期間を設け換気するなどの措置を講ずる。

第13節　高調波　追補

2.13.1 高調波環境レベル

a.高調波流出電流計算書
※「高圧又は特別高圧電力で受電する需要家の高調波抑制ガイドライン」(H6年制定H16年改正資源エネルギー庁)、「高調波抑制対策技術指針」(JEAG 9702-2023)により作成する。
⊙作成しない

第16節　表示工事　追補

2.16.1 一般事項

a.表示工事施工計画書を作成し、監理者の確認を受ける。

2.16.2 機器類の表示

a.機器類には、機器番号・機器名称・主たる仕様を表示する。
b.表示位置はメンテナンス通路から見やすい位置とし、判別しやすい大きさで表示する。

2.16.3 盤類の表示

a.盤類には、盤記号・盤名称を表示する。
b.盤扉裏には、受注者銘板・締付け確認票を貼り付ける。
c.配線の導体接続用端子台には、規定の締付け後にマーキングを行い、締付け確認票に日付と氏名を記入する。

2.16.4 その他

a.受変電室には、単線結線図を見やすい位置に表示する。詳細は監理者と協議する。
b.盤収納の機器・装置類・計器類には、機器名・設定値・許容値・調整値等を本体又は直近に表示する。
c.インバータの部品等には、耐用年数・交換年数・時期等を表示する。
d.プルボックスには用途表示、配線には回路・行き先等を表示する。
e.天井点検口の裏面には、点検口から保守点検する機器・器具等の項目と位置を示す表示票を貼付する。
f.現地の状況に応じて「危険注意、乗らぬこと」等の注意喚起の表示を行う。
g.バッテリー類は設置場所と交換時期を記載したバッテリーリストを作成のうえ、該当機器の見やすい位置に「バッテリー交換有り」の表示を行う。
h.ケーブルの表示札は接続点付近及び次の部分に行う。
EPS（⊙各階　・(　)階ごと）
横引きケーブルラック（⊙分岐部　・(　)mごと）

改修標仕　第11節　はつり工事

2.11.1 一般事項

a.はつり作業を行う場合に放射線透過検査等による埋設物の調査を行う際は、次による。
※放射線透過検査　・その他（　）

2.11.2 非破壊調査

a.コンクリート床、壁の穴開けを行う際の埋設物、配筋調査は、次による。
※放射線透過検査　・その他（　）

2.11.3 穴開け及び補修

a.貫通場所、口径等
※設計図による　・
b.配管貫通部処理方法
※区画貫通部は、法に準拠した処置を行う。その他の貫通部は、モルタル又はロックウール保温材を充填し、脱落防止の処置を施す。

2.11.4 溝はつり及び補修

a.はつりを行う箇所及びはつり深さ
※設計図による　・

2.11.5 開口部補修等

a.補修が必要な箇所
※設計図による　・
b.防水箇所の貫通処理方法
※設計図による　・
c.意匠を考慮する場合の仕上げ方法
※設計図による　・

改修標仕　第12節　インサート等

2.12.1 一般事項

a.インサートの長期の許容引抜荷重（コンクリート圧縮強度が18 [N/㎟] ）の場合
M10　※2,000 [N] 以上　・
M12　※4,400 [N] 以上　・
M16　※6,500 [N] 以上　・
ただし、M10に代えて W3/8 を採用する場合には断面積の比に応じた引き抜き荷重を確保すること。

2.12.1.1 材料　[付加]

a.アンカー金物の品質は次による。
1)基礎ボルトは、JIS B 1178による。
2)インサート金物は、鋼製又は鋳鋼製で防錆処理を施したものとする。ただし、暗きょ(床下ピット、トレンチ等）、多湿箇所、免震層等ではステンレス製とする。
3)水湿及び腐食のおそれのある部分に使用するアンカー金物は、ステンレス製（SUS304又はSUS316）又は溶融亜鉛めっき（膜厚HDZT35）を施したものとする。

2.12.3 あと施工アンカー

a.あと施工アンカーを使用する場合には、工事の着手に先立ち施工計画書を作成し、監理者の承認を受ける。耐震計算書と施工状況を照合し、自主検査記録書を作成し監理者に提出する。
b.あと施工アンカーの性能試験及び施工後確認試験は、監理者と協議する。
c.あと施工アンカーの施工管理には、工事内容に相応した施工の指導を行う施工管理技術者を置く。受注者は、日本建築あと施工アンカー協会の資格を有する者か、又はあと施工アンカーについて十分習熟し、かつ十分な技能及び経験を有する者が施工を行う。
d.あと施工アンカーの適用は、以下のとおりとする。
1)あと施工アンカーの選定は、日本建築センター「建築設備耐震設計・施工指針」2014年版、空気調和・衛生工学会「建築設備用あと施工アンカー SHASE-S 012」に準拠するとともに、日本建築あと施工アンカー協会(JCAA)の認証品を使用する。また、選定したあと施工アンカー製造者による実技講習会を開催し、受注者は使用するあと施工アンカーの製品知識と十分な技能を習得し施工する。また、許容引抜荷重の計算では、第一種、第二種軽量コンクリートが使用される場合は、一割程度裕度ある選定を行う。
2)あと施工金属拡張アンカーは、おねじ型(スリーブ打込み式、ウェッジ式)とする。やむを得ずめねじ型を使用する場合は、内部コーン打込み式とし、支持重量は20kg以下を原則とする。
3)あと施工接着系アンカーの固着剤は、カプセル方式を原則とし、耐薬品性・耐熱性等の施工条件を考慮して選定する。また、接着系アンカーは配管、ダクト、機器等の天井吊り下げ用及び重量の大きい機器、配管等を支持する壁付ブラケットなどの常時引抜力の掛るボルトに使用してはならない。
4)雨掛りとなるあと施工アンカー部分では、取り合い部分にシーリングを行い、止水処理を行う。
5)防水保護コンクリートへのあと施工アンカーは行わない。やむを得ずあと施工アンカーとする場合は、防水層、鉄筋、埋設配管類に対し損傷影響がない旨の資料を作成し、監理者の承認を受ける。
6)あと施工アンカーは、梁底に打ち込むことを禁止する。
7)コンクリート基礎にあと施工アンカーを打ち込む場合は、事前にコンクリート基礎の配筋状態を確認し、あと施工アンカーが配筋に当たらないようにする。
8)そのほか、改修標仕[第2編 第5章 インサート及びアンカー]に準拠して施工を行う。
9)上記原則以外のことを行う場合は、監理者と協議する。
e.あと施工アンカーを使用する場所における埋込み配管等の探査の範囲及び方法は場所ごとに監理者と協議する。
f.重量機器類のアンカーは、先付アンカーを原則とする。
g.設備工事の共通支持部材用のアンカーボルトやインサートは、原則建築工事に依頼する。
h.配管、ケーブルラック等の吊り用共通支持架台等は、インサートを原則とする。
i.合成スラブ構造用デッキプレートにインサート及びあと施工アンカーを取付ける場合は、原則下図のようにデッキプレートの割付図を確認しデッキプレートの山部に取付ける。

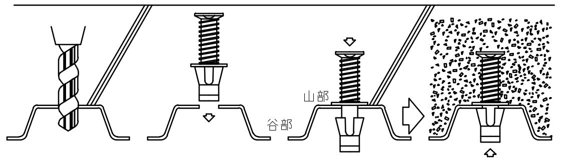

j.床型枠用鋼製デッキプレート(フラットデッキ)のリブからは、配管、ダクト、機器用等の荷重を支持しない。

2.12.4 追補 既存のインサート等の利用

a.工事の施工は、着手に先立ち施工計画書を作成し、監理者の承認を受ける。
b.既存のインサート及びアンカーボルトを利用する場合の条件
引張強度の確認試験（性能確認試験、施工後確認試験）
⊙確認試験を行う　・確認試験を行わない
1)引張強度試験の方法は、非破壊試験とし、試験本数は全本数の0.5%又は3本以上とする。
2)金属拡張アンカーボルトは、設計用引張強度に等しい荷重まで加力試験し、抜け出し等の変形が見られなければ合格とする。
3)接着系アンカーは、設計用引張強度に等しい荷重まで加力試験し、抜け出し等の変形が見られなければ合格とする。

2.12.5 追補 機器の固定

a.アンカーの耐震計算
※0.1kN以内の機器を除き、原則として工事対象機器は、すべて耐震計算を行う。

改修標仕　第14節　仮設備工事

2.14.3 仮電源等

a.受変電設備の仮設備
・仮設備する(設置場所、供給対象等詳細は設計図による)
⊙仮設備しない
b.発電設備の仮設備
・仮設備する(設置場所、供給対象等詳細は設計図による)
⊙仮設備しない

着工	.　.	.　.	
竣工	.　.	.　.	
監理		.　. .　.	
施工		.　. .　.	

惠本　涼太郎　一級建築士
澤村　晋次　意見を聴いた建築設備士

日建設計

2026・03・27　検図者：横井　繁明

椙山女学園/星が丘キャンパス
大学会館食堂リニューアル工事

電気設備特記仕様書（1）

㊺電 −01

J− 241226 − A

1	特記仕様書（2）	—

第2編　電力設備工事

第1章　機材

第1節　電線類

1.1.1　付加 電線類	a.電線種別 ・EM電線、EMケーブル　⊙一般電線、一般ケーブル b. 電線・ケーブル導体種別（耐火電線・ケーブルは除く） ※銅　・アルミ c. バスダクト導体種別 ・銅　・アルミ d.水の影響がある場所に敷設する高圧ケーブル 水の影響がある場所に敷設する高圧CVTケーブルは３層押出構造（E-E）のケーブルを使用する。

第2節　電線保護物類

1.2.1　[付加] 金属管及び附属品	a.使用区分 屋内　※ねじなし電線管　・薄鋼電線管 屋外　※厚鋼電線管（溶融亜鉛めっき）　・ポリエチレン被覆鋼管（ＰＬＰ） ・その他 b.露出部金属管の塗装 露出部　（場所：外構デッキ部　）　⊙指定色　・不要 塗装の仕様（　　　　） c.屋外電路の支持材(吊り台、架台) ⊙鋼材（溶融亜鉛めっき） ・成形品（JIS G3321、JIS G3322）・成形品（JIS G3323） ・成形品(アルミニウム製）　・成形品（ステンレス製） d.屋外電路の固定材(ボルト、ナット類) ⊙溶融亜鉛めっき　・ステンレス製 e.床下、暗きょ、トレンチ内電路の支持材(吊り台、架台) ⊙鋼材（溶融亜鉛めっき） ・成形品（JIS G3321、JIS G3322）・成形品（JIS G3323） ・成形品(アルミニウム製）　・成形品（ステンレス製） f.床下、暗きょ、トレンチ内電路の固定材(ボルト、ナット類) ⊙溶融亜鉛めっき　・ステンレス製
1.2.2　付加 PF管、CD管及び附属品	a.使用区分 ※PF管(隠ぺい部･コンクリート埋設部)　・CD管(コンクリート埋設部)
1.2.6 プルボックス	a.屋内型プルボックスの材質 ※鋼板製　・ステンレス鋼板製　・合成樹脂製 b.屋外型プルボックスの材質 ※鋼板製(溶融亜鉛めっき）・ステンレス鋼板製　・合成樹脂製　・高耐食性めっき鋼板 [付加] c.露出部金属プルボックスの塗装 露出部(　　　)　⊙指定色　・不要 [付加] d.プルボックスのふたの止めねじ 長辺200mmを超える場合は、蝶ねじ又は脱落防止ねじとする。 [付加] e.床下、暗きょ、トレンチ内プルボックスの材質 ※鋼板製(溶融亜鉛めっき）・ステンレス鋼板製　・合成樹脂製　・高耐食性めっき鋼板
1.2.7　付加 金属ダクト	a.金属ダクトのふたの止めねじ 金属ダクトのふたの長辺が200mmを超える場合は、脱落防止ねじとする。
1.2.8　付加 ケーブルラック	a.ケーブルラックの種別 屋内　※鋼板製　・アルミニウム製 屋外　⊙鋼板溶融亜鉛めっき製 ・めっき鋼板（JIS G3321、JIS G3322）製　※めっき鋼板（JIS G3323）製 ・アルミニウム製　・ステンレス製 b.屋内のケーブルラック保護カバー 屋内の露出部は、床上2.3mまでは保護カバー(鋼板メラミン焼付1.2mm厚以上)をケーブルラックの上下両面に設ける。ただし電気室やEPS等の部分は除く。 ・上記以外の屋内場所に保護カバーを設ける。（場所：　　　　） ・屋内保護カバーの材質（・鋼鈑メラミン焼付1.2mm厚以上　・設計図による） c.屋外のケーブルラック保護カバー ・設ける（場所：　　　　） 1）材質（・鋼鈑溶融亜鉛めっき製　・ステンレス製 ・めっき鋼板（JIS G3321、JIS G3322）製　※めっき鋼板（JIS G3323）製 2）塗装　・有り　・なし 3）条件(・風圧力に対応した固定　・人が乗れる耐荷重 ・エンボス付等のノンスリップ仕上げ　・屋根型等の水勾配付 ・ケーブルラック下側にも上側と同じ保護カバーを設ける ・ケーブルラック下側にシート(ネトロン等）付　・設計図による） ⊙設けない d.床下、暗きょ、トレンチ内ケーブルラックの材質 ⊙鋼板溶融亜鉛めっき製 ・めっき鋼板（JIS G3321、JIS G3322）製　※めっき鋼板（JIS G3323）製 ・アルミニウム製　・ステンレス製

第3節　配線器具

1.3.1　付加 配線器具	a.コンセント色 ⊙回路種別により色別(一般：白) ・設計図による b.スイッチ ⊙一般形　・ワイドハンドル形　※設計図による c.プレートの材質 ・新金属製(耐食アルミニウム合金製）⊙合成樹脂製(神保電機NKシリーズ相当品） ※設計図による　・ステンレス鋼板製

第4節　照明器具

1.4.1　付加 一般事項	a.LED照明器具の規格 PSEマークを有する。 ・直管形LEDランプ　・JIS C 8159-1に準拠　・JEL802に準拠　※設計図による
1.4.2 構造一般	a.外灯ポール内開閉器 ⊙不要　・配線用遮断器　・カットアウトスイッチ
1.4.3　付加 部品	a.LEDモジュールは、JIS C 8155「一般照明用LEDモジュール性能要求事項」による。 b.LED制御装置は、JIS C 61000-3-2「電磁両立性-第3-2部：限度値-高調波発生限度値（1相当たりの入力電流は20A以下の機器）」に適合するものを使用する。 c.LED照明器具は採用する器具電源部の定格力率と点灯時突入電流を調べ、回路のMCCBがトリップしないことを確認する。 d.屋外に用いるLED照明器具は、その漏れ電流を調べ、回路のELCBがトリップしないことを確認する。
1.4.4　[付加] 光源	a.LEDモジュールを交換可能な照明器具とする条件 ・寿命30,000時間以内のLEDモジュールを使用する照明器具 ・LEDモジュールを使用するすべてのLED照明器具 b.光源色の相関色温度 ・4,600～5,500K（昼白色）　※設計図による c.LED照明器具の平均演色評価数（Ｒａ） ベースライト形器具　※80以上　・95以上　⊙設計図による ダウンライト形器具　※70以上　・80以上　・95以上　⊙設計図による 高天井形器具　※70以上　・80以上　・95以上　⊙設計図による

第7節、第9節～第12節、第14節　キャビネット共通

（照明制御盤、分電盤、OA盤、実験盤、開閉器箱、制御盤、電気自動車用充電装置）

1.7.3、 1.9.3～1.12.3、 1.14.3 キャビネット	a.屋内用キャビネットの材質 ※鋼板製　・ステンレス鋼板製 b.錠の鍵 ※製造者の標準　・設計図による ・その他(　　　　) c.ドアハンドルの施錠解錠表示 ※製造者の標準　・あり [付加] d.屋内用キャビネットの塗装色 ⊙製造者の標準色　・指定色　・設計図による [付加] e.接地端子 ※回路数と同数の接地端子を設ける。　・設計図による　・その他(　　　) f.屋外用キャビネットの材質 ※鋼板製(塗装）　・鋼板製(溶融亜鉛めっき）　・ステンレス鋼板製 [付加] g.屋外用キャビネットの表面仕上げ ・耐塩塗装(製造者標準)・重耐塩塗装(製造者標準）⊙製造者の標準　・その他(　) [付加] h.屋外用キャビネットの塗装色 ⊙製造者の標準色　・指定色、指定艶 [付加] i.チャンネルベース キャビネットの材質、塗装と同じとするが、屋外用キャビネットについては下記による ※鋼製(溶融亜鉛めっき）・ステンレス鋼製　・その他(　)
1.7.4　付加 導電部	a.母線接続部 ※盤の母線(接続部)には、不可逆性示温材(70℃等)を設ける。
1.7.6 器具類	a.積算計器の種類 ・無検定　・検定付　※設計図による ・設計図に記載の箇所に加え検定付積算計器とする箇所 (　　　　) [付加] b.積算計器の伝送方式 ・パルス発信機能　・MODBUS RTU通信　・メーカ独自通信（B/NET等） c.低圧用SPD ※クラスⅡ(ただし接地極間連結用はクラスⅠ）　・設計図による d.低圧用SPDクラスⅡの性能（1線当たりとし、対地間の値を示す。） 1）公称放電電流（印加電流波形8/20μｓの場合）　※5ｋA以上　・設計図による 2）電圧防護レベル（単相100V、200V、三相200V）　※1,500V以下　・設計図による 3）電圧防護レベル（三相400Vで対地電圧が300V以下の場合） ※2,500V以下　・設計図による f.接地極間連結用SPDの警報監視 ・劣化警報を中央監視に移報　⊙劣化警報を中央監視に移報しない

第9節　OA盤

1.9.3　[付加] キャビネット	a.ドアの形式 ※開閉式　・着脱式 [付加] b. 外部配線の通過の有無 ※不通過　・通過する c. 端子盤部セパレータの仕様 ※鋼板製　・樹脂製 d. 端子盤部の許容温度対策 ※通気口(フィルター付）　・冷却用ファン　・設計図による

第12節　制御盤

1.12.1　付加 一般事項	a.主幹器具 ※配線用遮断器　・漏電遮断器　・設計図による b.インバータ等を収納する屋外用キャビネットの遮熱対策 通気口又は換気装置に加えて以下の対策を施す。 ・遮熱板を底面を除く5面に設置する。 ・遮熱塗料を塗布する。 ・直接日射を受ける面に遮熱シートを貼る。

第2章　施工

第1節　共通事項

2.1.13　付加 耐震施工	a.機器固定の設計用水平震度と鉛直震度 ⊙「工事概要書 2-3 総合耐震クライテリア」による。　・設計図による b.耐震安全性の分類と耐震支持 ・標仕[表2.1.2]、[表2.1.3]による ・特定の施設 ・一般の施設 ⊙「工事概要書 2-3 総合耐震クライテリア」による。 ただし、耐震支持はC号(敷地および建築物各部の耐震要求性能)による c.「工事概要書 2-3 総合耐震クライテリア」による場合の横引き配管等の耐震支持 1）機器の耐震クラスがSの場合耐震支持はSA種とする 2）機器の耐震クラスがA又はBならばA種とする 3）他種の耐震支持を使用せざるを得ない部分は監理者の承認を受ける 4）ただし、標準仕様書の耐震支持に関する除外対象については本事項は適用しない 5）耐震支持材の選定は耐震計算書により行う。 d.建築物への引込み部の地盤変位への対応方法 地中側配管種別　⊙波付硬質合成樹脂管　・鋼管　・設計図による 想定沈下量　⊙0.2ｍ以下　・0.6m以下　・1m以下 e.エキスパンションジョイント部の耐震処置方法 ⊙金属性可とう電線管又はPF管工事　・ケーブル工事　・設計図による

第2節～第4節　金属管配線・合成樹脂管配線(PF管、CD管、硬質ビニル管)

2.2.3　付加 ～2.4.3 隠ぺい配管の敷設	a.最上階の上部スラブ及び外壁には配管を埋設してはならない。 b.インバータ制御機器等、電磁障害を発生させる機器への動力制御盤からの配管仕様は以下とする。 ※金属管　・設計図による

第10節　ケーブル配線

2.10.1.5　付加 二重天井内配線	a.T/Uリモコンリレーを天井内に設ける場合はケーブル接続部に張力がかからぬよう処置固定し、点検可能な位置とする。 b.グリッド照明等で移動可能とする照明は移動距離(　　cm)のケーブル余長を見込む。

第18節　施工の立会い及び試験

2.18.2 施工の試験	a.構造体利用とした接地極、環状接地極、網状接地極又は基礎接地極を採用した場合の電圧降下法による接地抵抗測定 ・測定する(測定時期:(　　　　)：回数：(　　　　)) ⊙測定しない（等価表面積置換法により計算で代替(安全係数：3)) b.一般照明の照度測定 1)測定箇所 ※全室(PS、DSを除く）　・その他(　　　　) [付加] 2)施工前の照度分布図 ※作成する（室名：　全室　） ・作成しない [付加] c.計測計器の照合 1）施工前に計測計器の設置箇所と種別の確認 計測計器の設置箇所と検定有無等がわかるメーターツリーを作成する。 2）信号の受け渡し確認 計測計器と中央監視装置側との信号の受け渡しを照合し、整合性を確認する。

改修標仕　第2編　電力設備工事

改修標仕　第2章　施工

改修標仕　第1節　共通事項

2.1.1　付加 事前確認	a.改修前の使用電力量測定 ・行う　⊙行わない b.照明改修を行う場合の対象室の改修前後の照度の測定箇所数 ※各室1箇所(中央部）　⊙3×3ｍごとに１か所 c.照明改修を行う場合の改修前後の回路電流値の測定対象 ※改修対象の全回路　・設計図による d.事前確認項目(改修標仕[表2.1.1])への追加項目 配線の確認　⊙照明器具　⊙スイッチ　⊙コンセント 機器と開閉器等の対照　⊙スイッチ 制御回路の確認　⊙スイッチ
2.1.15　付加 配管・配線等の改修	a.既設埋設配管配線の位置を特定する調査を行う。これらの配管配線の種別とその経路は、事前に次により調査し、マーキングを行い、監理者の確認を受け施工する。 1)既設施工図による調査 2)管理者へのヒヤリング 3)電気的な導通試験による特定化 4)放射線透過検査等による埋設配管調査 b.既設埋設配管配線の撤去 露出配管配線・ケーブル ⊙撤去する　(・すべて　⊙配線、ケーブルのみ）　・撤去しない 天井内隠ぺい配管配線・ケーブル ⊙撤去する　(・すべて　⊙配線、ケーブルのみ）　・撤去しない コンクリート埋設配管の配線・ケーブル ⊙撤去する　・撤去しない c.機械室、EPS等の金属管の塗装 金属管の塗装 ※不要　・指定色　・標準色 d.配線引抜き後の空配管の導入線 ※入れる　・不要
2.13.7　追補 地中配管・配線の改修	a.既設部分に地中埋設配管配線する場合は、施工前に配管配線を埋設する経路の調査を行う。
2.15.8　追補 回路名称プレート・修正図面	a.改修により回路変更になった低圧配電盤、分電盤、動力制御盤、端子盤等の回路名称プレートは修正し、その部分に張り付けると同時に修正図面を図面ホルダーに差し替える。 b.改修部分には改修年月を表示する。

改修標仕　第19節　施工の立会い及び試験

2.19.2 施工の試験	a.環状接地極又は基礎接地極の場合における電位降下法による接地抵抗測定 ・測定する(測定時期:(　　　　)：回数：(　　　　)) ⊙測定しない（等価表面積置換法により計算で代替(安全係数：3)) b.一般照明の照度測定 1)測定箇所 ※全室(PS、DSを除く）　・その他(　　　　) [付加] 2)施工前の照度分布図 ※作成する（室名：　全室　） ・作成しない c.照明回路の使用電力量の測定 ・行う　⊙行わない d.総合動作試験 ⊙行う　・行わない [付加] c.計測計器の照合 1）施工前に計測計器の設置箇所と種別の確認 計測計器の設置箇所と検定有無等がわかるメーターツリーを作成する。 2）信号の受け渡し確認 計測計器と中央監視装置側との信号の受け渡しを照合し、整合性を確認する。

改修標仕第2章　施工

改修標仕第1節　共通事項

2.1.1　付加 事前確認	a.既存の受変電設備に、新たに負荷設備を接続又は切り離す等、設備容量を増減する場合は、既存設備の計測計器・保護継電器・CT・VT・リレー等の整定値設定変更や容量増、減による取替え、母線導体のサイズアップ等の必要な改修を行う。 b. 受変電機器改修後の絶縁耐力試験が、規定の試験電圧で困難な場合は監理者と協議する。

第2章　施工

第1節　据付け

2.1.1　付加 盤類	a.架台、盤類等の固定部設計用震度 ※工事概要書2-3　総合耐震クライテリアによる　・設計図による [付加] b.ナット、ワッシャなどの落下による内部短絡を起こさないよう、盤上部の排気口上には極力設備機器を配置しないよう施工する。やむなく上部に設備機器を配置する場合には、換気口に簡易な防護フードを設置する。 [付加] c.簡易形、ラインインタラクティブ方式、常時商用給電方式の据付け ※水平移動、転倒の事故を防止できるよう床への固定を施す ・常用インバーター給電方式の固定方法に準ずる耐震固定を行う

第6編　通信・情報設備工事

第1章　機材

第1節　電線類

1.1.1 電線類　[付加]	a.電線種別 ・EM電線、EMケーブル　⊙一般電線、一般ケーブル

第3節　配線器具

1.3.1　付加 モジュラコネクタ	a.モジュラコネクタ ※カテゴリ6　・カテゴリ6A　・その他
1.3.2 光コネクタ	a.コネクタ種別 ⊙SCコネクタ　・LCコネクタ　・その他

第4節　端子盤・機器収納ラック等

1.4.2 端子盤等	a.屋内用キャビネット ※鋼板製(塗装）　・ステンレス鋼板製　・鋼板製(溶融亜鉛めっき） b.錠の鍵 ※製造者の標準　・設計図による ・その他(　　　　) c.ドアハンドルの施錠解錠表示 ※製造者の標準　・あり [付加] d.キャビネットの塗装色 ⊙製造者の標準色　・指定色　・設計図による e.屋外用キャビネットの材質 ※鋼板製(塗装）　・ステンレス鋼板製　・鋼板製(溶融亜鉛めっき）
1.4.3 機器収納ラック	a.錠の鍵 ※製造者の標準　・設計図による ・その他(　　　　) b.ドアハンドルの施錠解錠表示 ※製造者の標準　・あり
1.4.4 端子類	a.端子板 ・B形　⊙D形　・E1形　・F形　・G1形　・G2形　・I形
1.4.5 通信用SPD	a.SPDの設置カテゴリ 構内情報通信網設備用 ・カテゴリＣ2　・カテゴリＤ1 構内交換設備用 ・カテゴリＣ2　・カテゴリＤ1 拡声設備用 ⊙カテゴリＣ2　・カテゴリＤ1 火災報知設備用 ⊙カテゴリＣ2　・カテゴリＤ1

第24節　自動火災報知設備　第25節　自動閉鎖設備（自動閉鎖機構）　第27節　ガス漏れ火災警報設備

2.24.3　[付加] 2.25.3 2.27.3 その他	a.連動動作 他設備機器との火災連動、排煙連動、排煙口と自動閉鎖装置との連動、警戒区域とスモークダンパーの連動について連動表を作成し、全数試験を実施する。

第28節　施工の立会い及び試験

2.28.2 施工の試験	a.映像・音響設備の試験の追加 ・インピーダンス測定　・残響時間測定　・伝送周波数特性測定　・音圧分布測定 b.テレビ共同受信設備の試験の追加 ・CATVチャンネルの測定　・CSチャンネルの測定 c.テレビ電波障害防除設備の試験の追加 ・CATVチャンネルの測定　・CSチャンネルの測定

改修標仕　第2章　施工

改修標仕　第1節　共通事項

2.1.1 事前確認	a.事前確認の項目(改修標仕[表2.1.1])への追加項目 ⊙取外す末端機器への配線確認 ⊙取外す端末機器等と主装置等の対照の確認 ・その他（　　　　）
2.1.15　[付加] 主装置等の更新	a.主装置等の撤去時に、接続されている電線収容物、ケーブル保護物が支障となる機器 ※接続されている電線収容物、ケーブル保護物を一部撤去、更新 ・その他(　　　)
2.1.17 自動火災報知設備等の改修	a.感知器等の増設や変更等に伴う受信機の設定変更 ※感知器の登録、連動設定、画面表示などの変更を行う。 ・

着工	. .	. .	
竣工	. .	. .	
監理		. .	
		. .	
施工		. .	
		. .	

惠本　涼太郎　一級建築士
澤村　晋次　意見を聴いた建築設備士

日建設計

2026. 03 .27　検図者：横井　繁明

椙山女学園／星が丘キャンパス
大学会館食堂リニューアル工事

電気設備特記仕様書（2）

㊂ －02

J－ 241226 － A

1　電気設備概要　—

1）電力設備
- ・食堂内新規電源供給用として分電盤を新設する。
- ・幹線ケーブルは既存ケーブルを撤去し、文学部棟電気室より既存分電盤1L-1まで幹線を新設する。
- ・上記、既設分電盤の幹線ケーブル用の配管は既設利用とする。
- ・新設分電盤用の幹線は既設分電盤1L-1の主幹遮断器の二次側より分岐とする。

２）動力制御設備
- ・空調室内機、ファン等の改修がないため、動力設備の改修は行わない。

３）照明設備
- ・低天井部分の照明改修を行う。
- ・既設照明を撤去の上、Φ75～125程度のLEDダウンライトを主体として設置する。
- ・食堂の目標照度は既設の照度程度とし、平均机上面照度は約400lxとする。

４）コンセント設備
- ・コンセント電源は新設分電盤からの電源供給とする。(一部既存再利用)
- ・カウンター席は什器組込コンセントを設置し、電源供給を行う。
- ・食堂東側出入口の自動ドアへの電源供給を行う。

５）通信情報設備
- ・電話、LAN用は配管のみ本工事とし、機器および配線は別途工事とする。
- ・既設音響用スピーカの撤去及び新設、BGM用アンプの新設を行う。
- ・非常放送スピーカーの撤去及び新設を行う。
- ・非常放送スピーカー改修に伴う主装置の調整を行う。

６）防災設備
- ・低天井部の改修に伴い、既設感知器及び発信機の撤去及び新設を行う。
- ・発信機1次側配線は既存再利用とし、発信機2次側の配線は撤去の上、新設とする。
- ・既設誘導灯の撤去を行い、LED電池内蔵型誘導灯を新設する。
- ・非常用照明は学校用途でかつ既存にも設置がないため、今回工事での追加設置は行わないものとする。
- ・改修に伴い、自動火災報知設備の受信機の調整を行う。

７）別途工事
- ・電話設備機器および配線工事（電源および配管は本工事）
- ・LAN設備機器および配線工事（電源および配管は本工事）
- ・AV設備（BGMスピーカー以外のプロジェクタ、マイク等）

2　施工留意点　—

- ・天井チャンバー（空調・換気用）方式の天井内区画壁貫通パイプ・ラック等の穴埋めは十分に行う事。
- ・外壁の打込配管は、原則として行わないこと。やむを得ず行う場合の外壁の打込ボックスには、　断熱材を充填すること。又、断熱材のある躯体を貫通する部分は内壁配管に結露を生じさせない様に対策すること。
- ・上記設計図書に示す範囲にて明示がない部分でも、技術上、施工上、もしくは保安上当然必要と認めらめられる工事は請負者負担にて施工する。
- ・本工事は工事着手前に十分調査を行い、現場の納まり取付位置、ダクト、配管、配線経路の変更等軽微な変更による請負金額の増減はしない。
- ・配管サイズ31mm(28mm)以上は原則としていんぺい配管とする。
- ・ケーブル支持材は専用(難燃以上)のものを使用する。
- ・ケーブル工事(天井いんぺい)はメッセンジャーワイヤー、吊ボルト等を利用し、整然と施工する。
- ・壁、柱等の引下げ部分は配管工事とする。(パーティション壁を除く)
- ・長さ1m以上の入線しない電線管には、呼び線として1.2mm以上のビニル被覆銅線を挿入する。
- ・配電盤・制御盤・分電盤・端子盤等盤類の鍵は、建築及び他設備施工者と協議の上、全て統一する事。
- ・防火区画を貫通する配管配線は耐火処理を行い、区画は建築防災図により見込む。
- ・官公署その他への諸手続きに必要な提出書類及び竣工図に使用する単位はSI単位系とする。
- ・ダウンライト等からの天井内漏れ光により、空調吹出口・レタンスリットなどから天井下に光が漏れる可能性がある場所は施工段階で十分検証し天井内に遮光板を設置するなどの対策を施すこと。
- ・工事の着手に先立ち、施工計画書を作成し、監理者の承認を受ける。
  各工事請負者間で十分に調整を行い、詳細に記載する。
- ・保守および機器取扱い説明書を作成し、監理者の確認を受けた後に発注者に対し、取り扱い説明会を実施する。
- ・瞬停時(瞬時電圧低下時を含む)に全ての機器において、警報を出さずに通電後に瞬停前と同じ状態で運転できるように瞬停対策を行う。(約1秒以下)
- ・工事に先立ち、監理者の指示する電気設備各種計算書を作成する。
- ・LED照明のスイッチは特記なき限り2Pとする。
- ・屋内外露出部分のケーブルラック、配管、プルボックス、ジョイントボックス、アウトレットボックス、吊ボルトは全て指定色塗装とする。(EPS、PS、DS機械室等、屋上機械置場を除く)
- ・構内道路への埋設管路付設に際しては、既設埋設管路の調査を確実に行い、同管路、ケーブルなどを損傷することのないよう十分注意すること。
- ・点検口の裏面には設備種別・用途の表示を行うこと。
- ・コンセントプレート、OAタップには分電盤名称・回路番号の表示を行う。
- ・EPS、CPS内のケーブルには線名札を取り付けること。

3　その他特記事項　—

1．施工
- ・原則としてスラブ内への打込み配管は行わないこと。ただし床アウトレットへの配管は除外するものとするが、最寄り壁での立下げとすること。
- ・上記には防火区画貫通箇所等で行われる短距離の打込み配管（梁跨ぎ配管）も含まれる。
- ・断熱、シールド貫通、気密処理等の機能性を求められる場所の施工については、施工要領書と施工記録（写真）の対比ができるようデータを管理すること。

２．その他
- ・別途工事との調整を十分に行い、必要な配管・配線・ルート・電源対応を行うこと。
- ・外部と接続する盤及び機器には、特記なき限りSPD（クラスⅠ、カテゴリD）+メーカー推奨の分離器を設置すること。(外部と接続しないものはクラスⅡ)
- ・現場変更により軽微変更届出または変更申請が必要となった場合、変更図作成等に協力すること。
- ・地中梁スリーブの外部側管端処理は、公共建築設備工事標準図の施工方法とし、
  予備スリーブは防水キャップを施すこと。
- ・照明点滅区分図・器具リスト・発電機回路エリア図等、現場段階で発注者確認に必要な書類作成に協力すること。
- ・各種申請に必要とする業務及び費用は全て本工事に見込むこと。
- ・各種インフラの引込み等に関わる直接工事は全て本工事とし、それらに関連するその他工事と他地下埋設物との関係に十分配慮し、事前に調整を行い施工計画と工程を作成すること。
- ・工事着手に先立ち、施工計画書を作成し、監理者の承認を受けること。
  各工事請負者間で十分調整を行い、詳細に記載する。
- ・断熱材のある躯体を貫通する部分は内壁配管に結露を生じさせない様に対策すること。
- ・防火区画等を貫通する配管配線は耐火処理を行う。
- ・官公署その他への諸手続きに必要な提出書類および竣工図に使用する単位はSI単位系とする。
- ・各設備の防振仕様・範囲は、図示の仕様に関わらず、室内許容騒音値以下とするための必要な対策を行うこと。許容騒音値以下となるよう騒音（振動）計算を行い、防振選定計算書を提出すること。計算に当っては、各振動設備（機器・配管・ダクト・ヘッダー類）以外の他工事施工事施工業者と協調し、関連設備（発電機等）を全て見込むこと。特に、重要室、敷地境界においては、引渡し前に騒音、振動の計測記録を十分整理し、測定結果については監理者の承認を受けること。
- ・耐震ストッパーは非接触型とし、設置後、視認・写真による確認、記録、報告すること。
- ・計画変更申請や軽微な変更申請が必要な場合は、監理者の指示に従い、必要な図面・計算書の作成に協力すること。
- ・保守および機器取扱い説明書を作成し、監理者の確認を受けた後に発注者に対し、取扱い説明会を実施する。取扱い説明書は機器単体のメーカー作成のものに加え、建物全体の運転管理、保守に必要な以下をとりまとめたものとする。
  - ・設計主旨、設備概要、各室条件リスト（設計図の修正で可）
  - ・各種システム図、系統図、ゾーニング図、機器プロット図
  - ・保守・管理項目一覧
  - ・その他、発注者、監理者の指示する書類
- ・設計図書に示す範囲にて明示がない部分でも、技術上、施工上、もしくは保安上当然必要と認められる工事は請負者負担にて施工する。
- ・本工事において発生する補修仕上工事で建築図に明示なき部分は、本工事に含むこと。
- ・防火区画及び114条区画には防火区画貫通処理(国土交通省大臣認定工法　1時間耐火)を施すこと。
  なお、防火区画および114条区画は建築防災図に示す。
- ・図中に特記がある場合でも、分電盤より第１ボックスまでのケーブル長が概ね
  - ・20mまでは　5.5sq
  - ・30mまでは　8sq
  - ・60mまでは　14sq
  - ・100mまでは　22sq
  - ・170mまでは　38sq　とする。

4　凡例　—

注）下記に図示の凡例は標準的な機器・器具である為、各設備図面も参照すること。
（各図面と凡例との相違がある場合は、各設備図面を優先する）

記　号	名　称	記　号	名　称
配管配線		拡声	
———	天井隠ぺい配線	◁ ◀	非常放送スピーカ　天井付，壁付
- - - -	床隠ぺい配線	◁ ◀	同上、アッテネーター付
------	露出配線	∝◁	ホーン形スピーカ
——-——	天井ころがし配線	↗	アッテネータ
——--——	地中埋設配線	AMP	増幅器
——---——	床下内配線	RM	リモートマイク
——o——	空配管	C	電源カットリレー
↗ ↗ ↗	立上り，素通し，引下げ	—o—	ワイヤレスアンテナ
⏚	接地極		
□	ジョイントボックス		
⊠	プルボックス		
▥	ケーブルラック及び防火区画貫通部		
↗ ↗ ↗	ケーブルラック立上り，素通し，引下げ	インターホン・緊急呼出	
=⊠=	群配管配線	ⓣ	インターホン親機
⊠⌒⊠	エキスパンションジョイント	ⓣ	インターホン子機
=□=	レースウェイ	Ⓓ	ドアホン親機
M	マンホール	Ⓓ	ドアホン子機
H	ハンドホール	▥	呼出表示器(nは窓数）
▥	壁貫通処理（屋外は防水処理のこと）	n	呼出ボタン
		⊗	ブザー付表示灯
		⊠	復旧ボタン
照明・コンセント		テレビ共同受信	
▭	LED　天井付	UHF	テレビアンテナ(UHF)
▭	LED　壁付	⊠	BS・CSアンテナ
○	LED　ダウンライト	Ⓥ	混合(分波)器
◐	LED　壁付	▽	増幅器
●	非常用照明器具（非常灯）	-○-	分岐器
○	ウオールウォッシャー（シングル）	-○-	分配器
▽	投光器（スポットライト，ライトアップ）	◎	直列ユニット　テレビ端子 F形接栓
⊗	外灯	D	機器収容箱
⊗	誘導灯（避難口誘導灯・通路誘導灯）	HE	ヘッドエンド装置
⊗	誘導灯（階段通路誘導灯・非常照明兼用）		
•	タンブラスイッチ　2P15A×1		
•2	タンブラスイッチ　2P15A×2	警備・防犯	
•3	タンブラスイッチ　2P15A×3	▭	テレビカメラ
•4	タンブラスイッチ　2P15A×4	ITV	ＩＴＶモニター装置架
•WP	タンブラスイッチ　2P15A×1（防水形）	⬭	ＩＴＶ副操作装置
⊗nL	リモコンスイッチ(nは回路数）	SE	入退室管理副監視装置
↗	調光器	EC	電気錠制御盤
⊖	壁付コンセント　2P15A×2（接地極付）	CR	カードリーダ
⊖20A	壁付コンセント　2P20A×1	EK	電気錠
⊖LK	壁付コンセント　2P15A×1（抜け止め形）	⊡	電気錠解錠スイッチ
⊖FC	ファンコイル用壁付コンセント　3P15A×1（引掛用）	KB	キーボックス
⊖ET	壁付コンセント及び接地端子　2P15A×2 ET×1	FG	フラッパーゲート
⊖WP	壁付コンセント　2P15A×1（接地端子付，防水形）	□K	センサー類アウトレット
◎	壁付コンセント　250V2P15A×1（接地極付、接地端子付）	Ⓜ	マグネットセンサー
⦶	床コンセント　2P15A×2	Ⓢ	シャッターセンサー
⦶	天井コンセント　2P15A×1（抜け止め形）	Ⓖ	ガラスセンサー
⦶	OAタップ　2P15A×4□	Ⓟ	パッシブセンサー
H	ハーネスジョイント（2分岐、4分岐）		
動力			
Ⓜ	電動機		
Ⓕ	換気扇		
S	開閉器箱		
⊡	押釦スイッチ		
⊙F	フロートスイッチ		
盤類			
◪	分電盤		
⧓	動力制御盤		
⧓	電灯動力盤		
⊟	端子盤		
電話・情報			
PBX	電話交換機		
MDF	MDF(本配線盤）		
⊙	床付電話用アウトレット		
⊙	壁付電話用アウトレット		
⊙	床付情報用アウトレット		
⊙	壁付情報用アウトレット		
Wi-Fi	Wi-Fiアクセスポイント		

着工	．．	．．
竣工	．．	．．
監理		．． ．．
施工		．． ．．

J241226A26031703_電気設備概要、施工留意点、その他特記事項、凡例

惠本　涼太郎　一級建築士
澤村　晋次　　意見を聴いた建築設備士

日建設計

2026・03・27　検図者：横井　繁明

相山女学園／星が丘キャンパス
大学会館食堂リニューアル工事

電気設備概要、施工留意点、その他特記事項、凡例

電　－03

Ｊ－ 241226 － A

1	外構設備図（既設図）	A1:1/ 800 A3:1/1600	注）1. ×、▨は撤去を示す。

埋中埋設配管

Ⓐ			
12	CV 150□/3c E38	E(G82)	1φ3W
13	CV 250□/3C	〃（100）	1φ3W
33	CV 250□/3c	〃（100）	3φ3W
34	CV 250□/3c	〃（100）	3φ3W
35	CV 250□/3c	〃（100）	3φ3W

天井露出配管

Ⓔ			
12	150□×3 E38	（82）	1φ3W
13	250□×3	（82）	1φ3W
33	〃	（82）	3φ3W
34	〃	（82）	3φ3W
35	〃	（82）	3φ3W

改修内容

- 文学部棟電気室から1L−1、2L−1までの幹線（CV250□−3C）を撤去する。
  ただし、配管は残置とする。

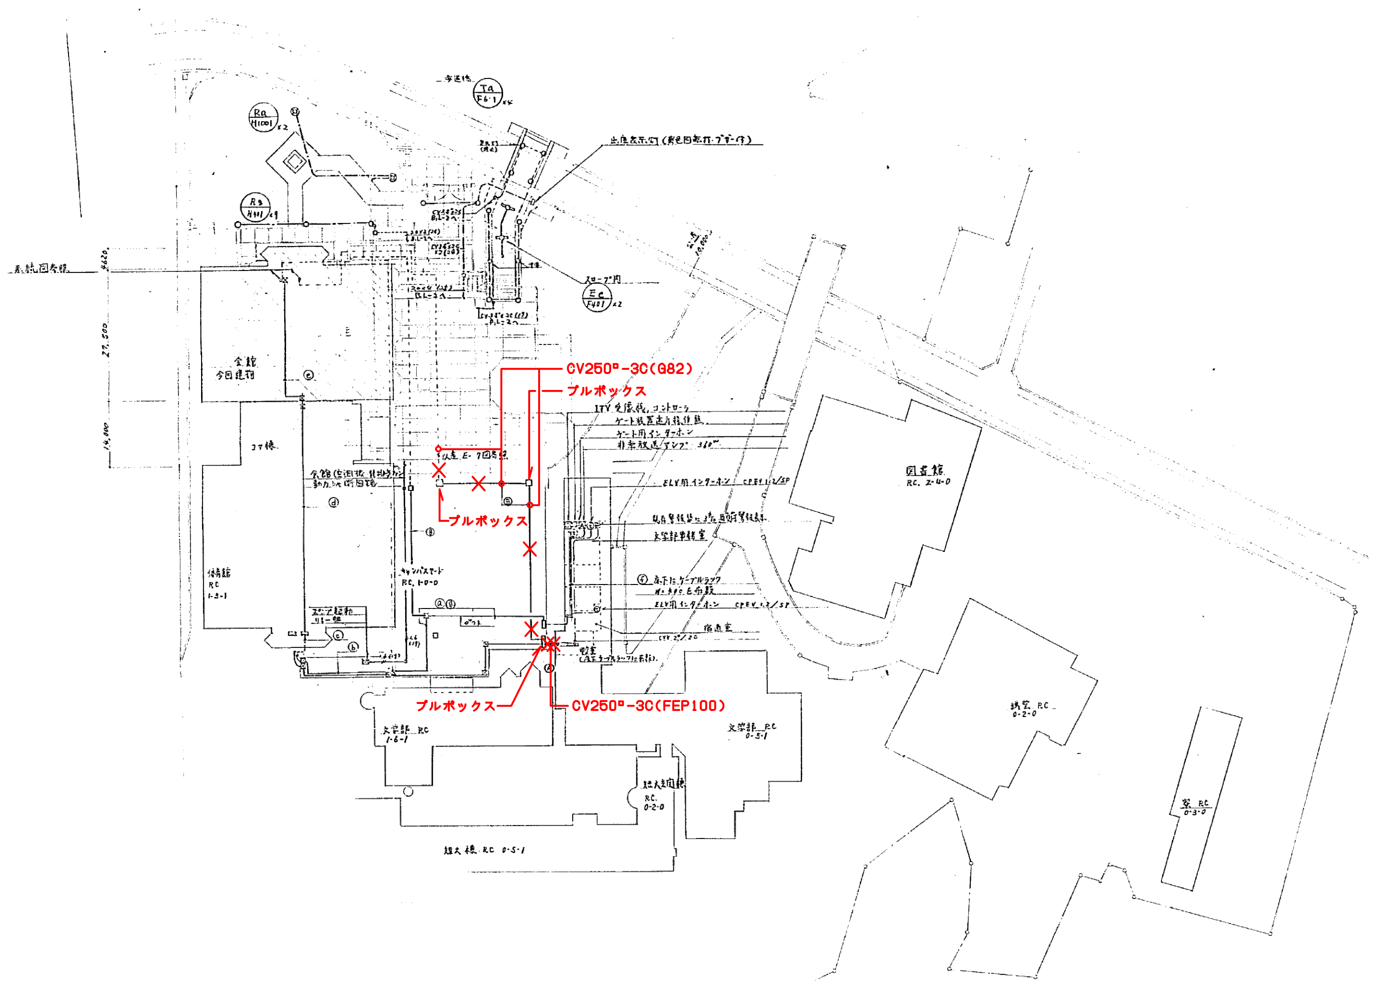
CV250□−3C(G82)
プルボックス
プルボックス
プルボックス
CV250□−3C(FEP100)
ITV受像機、コントローラ
ゲート装置遠方操作盤
ゲート用インターホン
非常放送アンプ
ELV用インターホン CPEV1.2/5P
文学部事務室
床下にケーブルラック
ELV用インターホン CPEV1.2/5P
宿直室
電室
系統図参照
スロープ内
Ec F401 ×2
図書館 RC. 2-4-0
文学部 RC 1-6-1
文学部 RC 0-5-1
短大玄関棟 RC. 0-2-0
講堂 RC 0-2-0
体育館 RC 1-3-1
キャンパスマート RC, 1-0-0
全館 今回建物
コア棟

2	外構設備図（改修図）	A1:1/ 800 A3:1/1600

改修内容

- 文学部棟電気室から1L−1、2L−1までの幹線（CV250□−3C）を新設する。
  ただし、配管は既存利用とする。
- SFD、空調機から受信機まで配管配線を新設する。

注記）

1. 配管配線の新設に伴う開口新設、防火区画貫通処理の撤去、復旧等は適宜見込むこと。

追変−電02

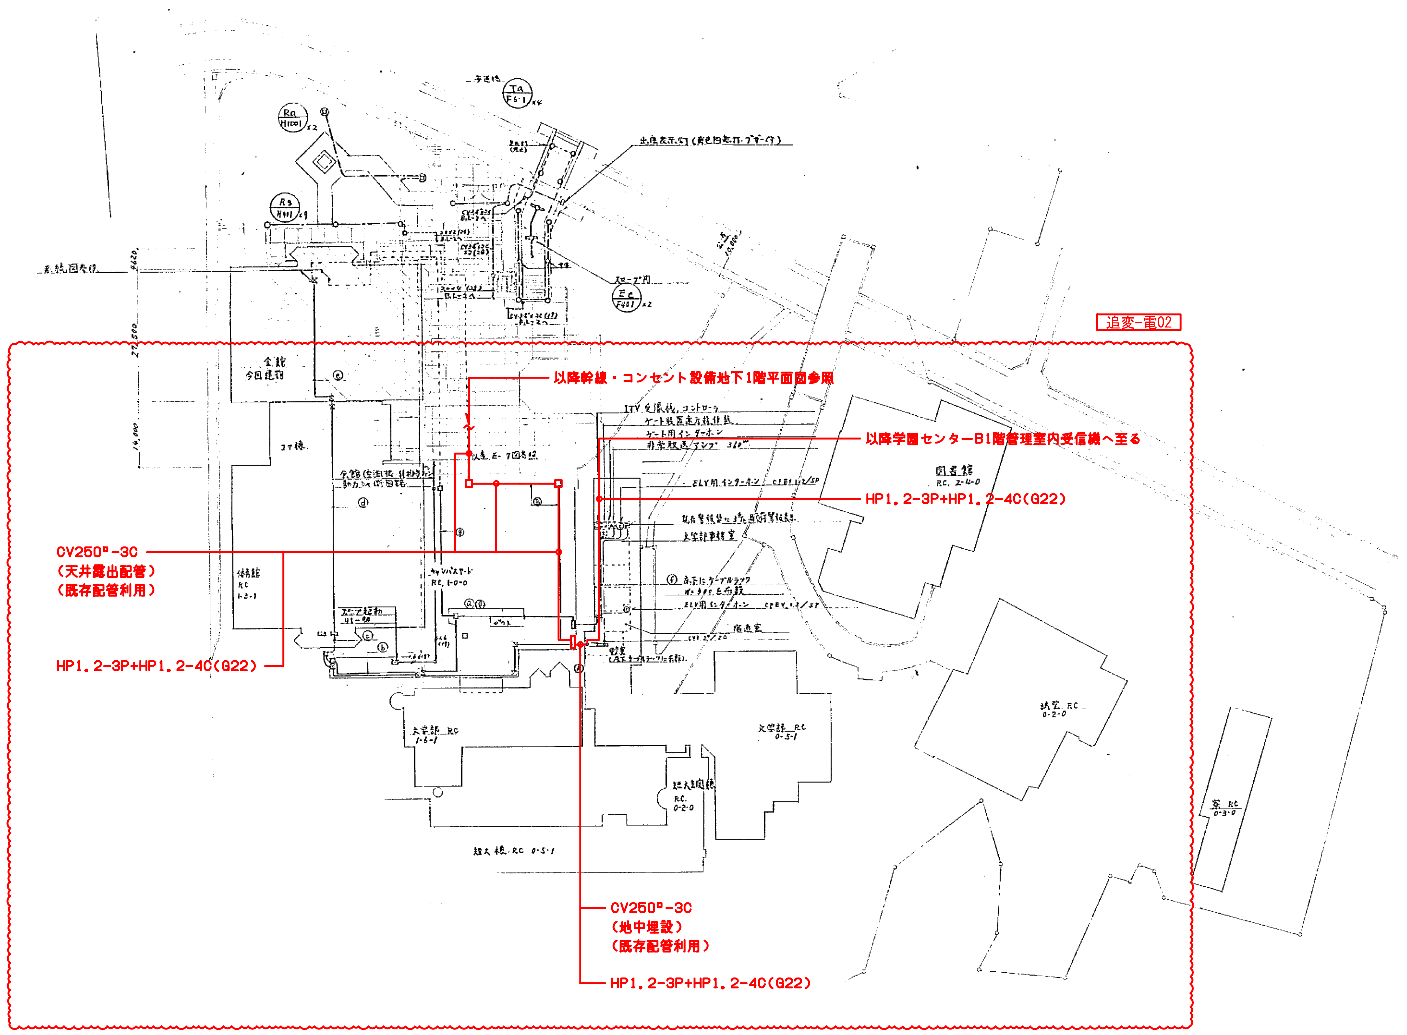
追変−電02
以降幹線・コンセント設備地下1階平面図参照
以降学園センターB1階管理室内受信機へ至る
HP1.2−3P+HP1.2−4C(G22)
CV250□−3C
（天井露出配管）
（既存配管利用）
HP1.2−3P+HP1.2−4C(G22)
CV250□−3C
（地中埋設）
（既存配管利用）
HP1.2−3P+HP1.2−4C(G22)
図書館 RC. 2-4-0
文学部 RC 1-6-1
文学部 RC 0-5-1
短大玄関棟 RC. 0-2-0
講堂 RC 0-2-0
体育館 RC 1-3-1
キャンパスマート RC, 1-0-0
全館 今回建物
コア棟

着工	. .	. .
竣工	. .	. .
監理		. .
施工		. .

惠本　涼太郎　一級建築士
澤村　晋次　　意見を聴いた建築設備士

日建設計

2026・03・27　検図者：横井　繁明

椙山女学園／星が丘キャンパス
大学会館食堂リニューアル工事

外構設備図（既設図）（改修図）

㊆ −04

No. J− 241226 − A

J241226A26080304_外構設備図（既設図）（改修図）

1 | 変電設備図(既設図) | — | 注)1. ×、▨ は撤去を示す。

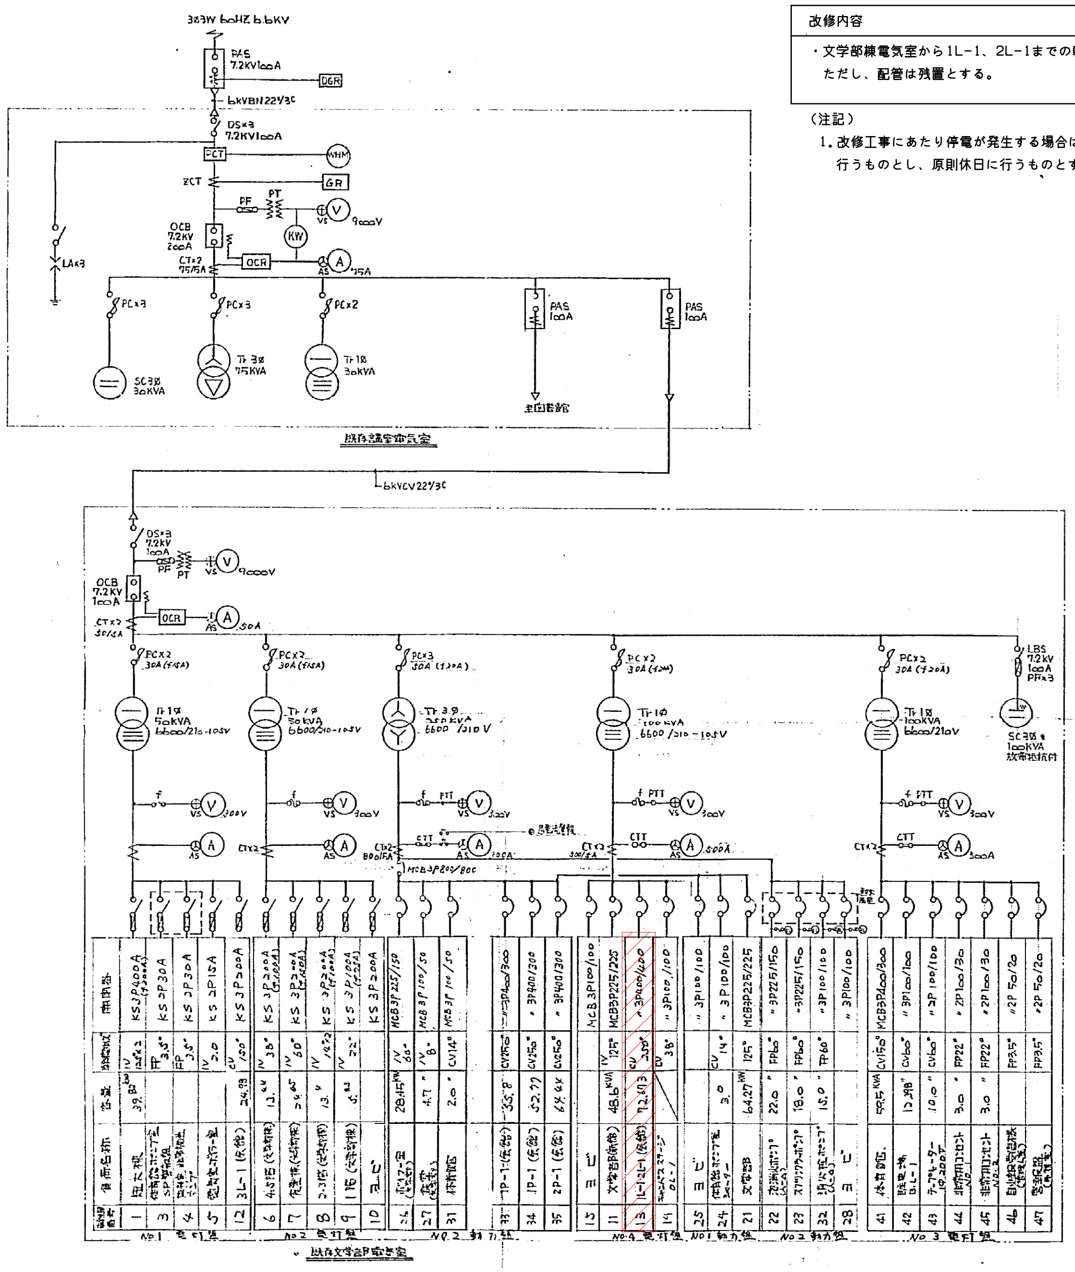

改修内容

・文学部棟電気室から1L-1、2L-1までの幹線(CV250□-3C)を撤去する。
　ただし、配管は残置とする。

(注記)

1. 改修工事にあたり停電が発生する場合は、発注者と協議の上、日程を決定して行うものとし、原則休日に行うものとする。

---

2 | 変電設備図(改修図) | —

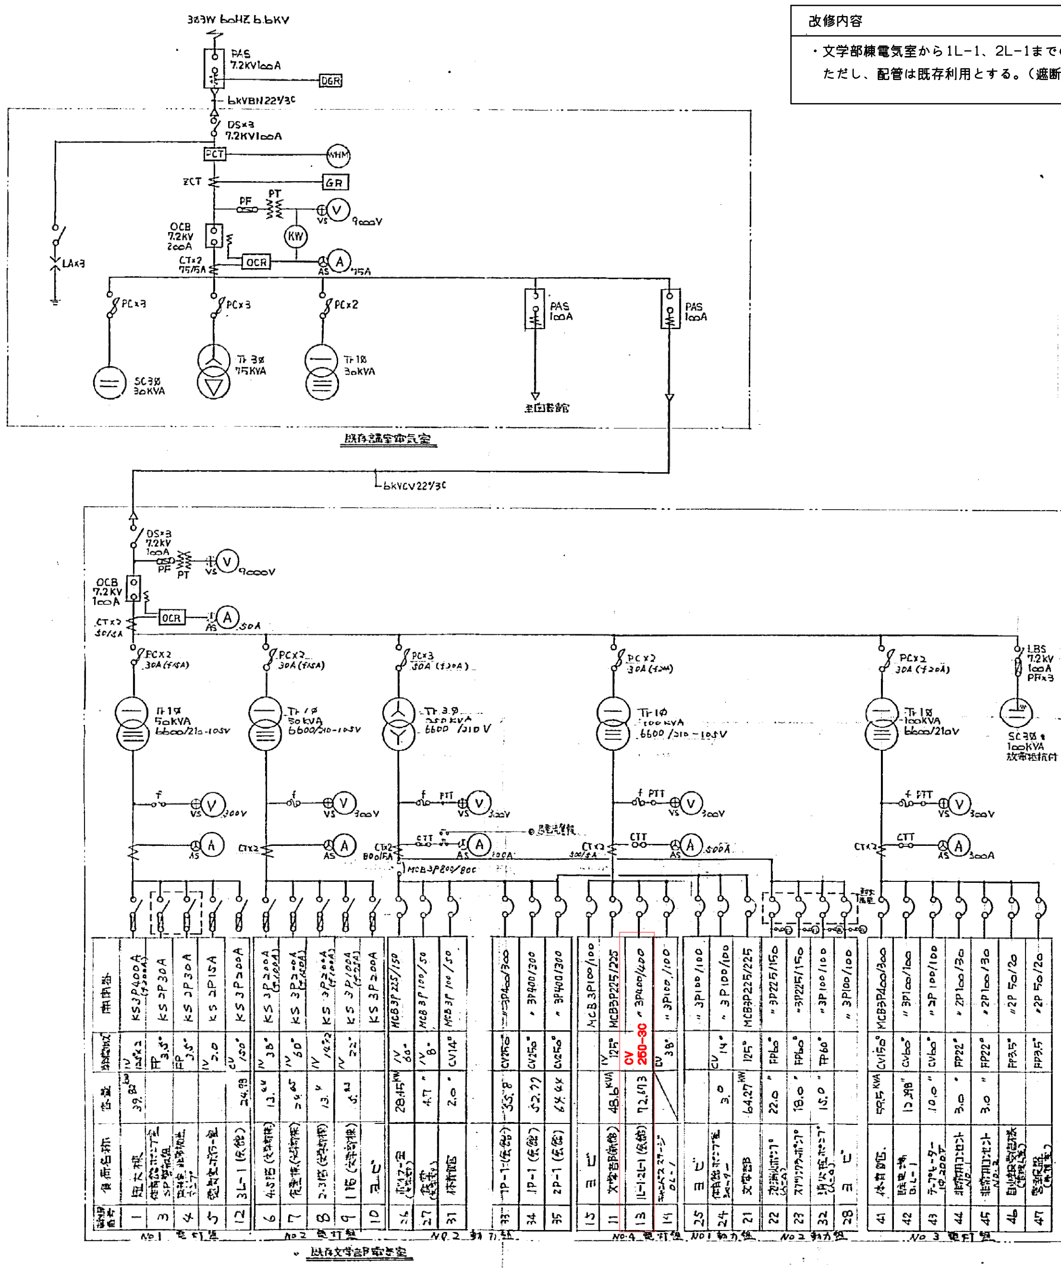

改修内容

・文学部棟電気室から1L-1、2L-1までの幹線(CV250□-3C)を新設する。
　ただし、配管は既存利用とする。(遮断器は既存利用)

---

3 | 幹線系統図(既設図) | — | 注)1. ×、▨ は撤去を示す。

改修内容

・文学部棟電気室から1L-1、2L-1までの幹線(CV250□-3C(分岐以降CV100□-3C))を撤去する。
　ただし、配管は残置とする。

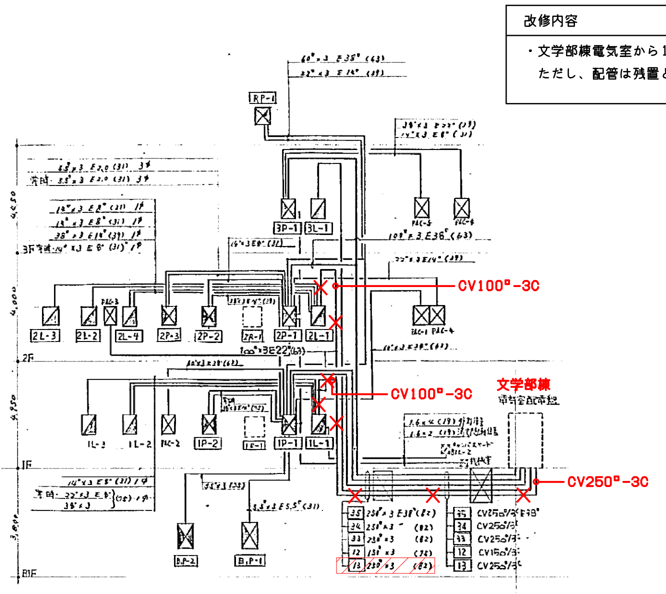
CV100□-3C
CV100□-3C
文学部棟
CV250□-3C
2L-3
2L-2
2L-4
1L-3
1L-2
2F
1F
B1F

---

4 | 幹線系統図(改修図) | —

改修内容

・既存幹線は撤去前に絶縁抵抗測定を行う。
・文学部棟電気室から1L-1、2L-1までの幹線(CV250□-3C(分岐以降CV100□-3C))を新設する。
　ただし、配管は既存利用とする。
・分電盤(1L-1-2)を新設し、既設分電盤(1L-1)より幹線(CVT38□)を新設する。

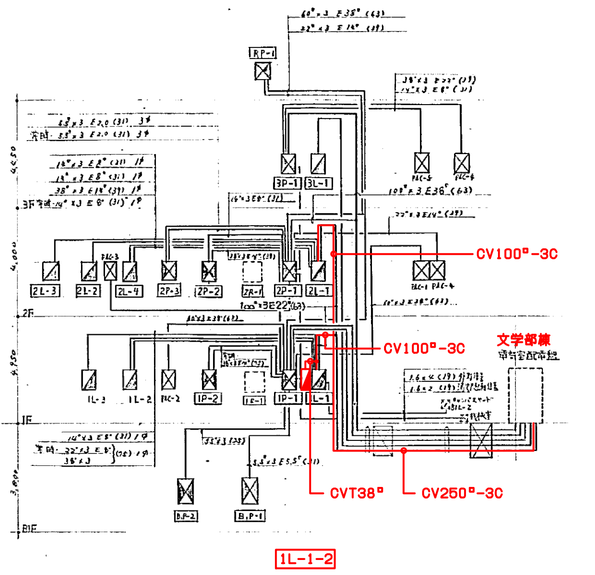
CV100□-3C
CV100□-3C
文学部棟
CVT38□
CV250□-3C
1L-1-2
2F
1F
B1F

改修部幹線系統図

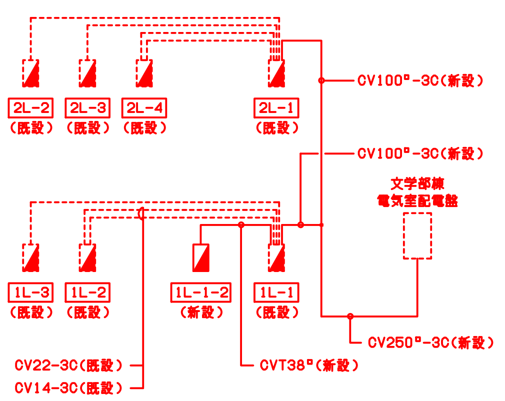
2L-2
(既設)
2L-3
(既設)
2L-4
(既設)
2L-1
(既設)
CV100□-3C(新設)
CV100□-3C(新設)
文学部棟
電気室配電盤
1L-3
(既設)
1L-2
(既設)
1L-1-2
(新設)
1L-1
(既設)
CV250□-3C(新設)
CV22-3C(既設)
CV14-3C(既設)
CVT38□(新設)

J241226A26031705_変電設備図、幹線系統図(既設図)(改修図)

着工	. .	. .	
竣工	. .	. .	
監理		. .	
		. .	
施工		. .	

惠本　涼太郎　一級建築士
澤村　晋次　　意見を聴いた建築設備士

日建設計

2026・03・27　　検図者：横井　繁明

椙山女学園／星が丘キャンパス
大学会館食堂リニューアル工事

変電設備図、幹線系統図(既設図)(改修図)

㊀電 −05

No. J − 241226 − A

1	地下1階平面図(既設図)	A1:1/100 A3:1/200	注)1. ×、▨は撤去を示す。

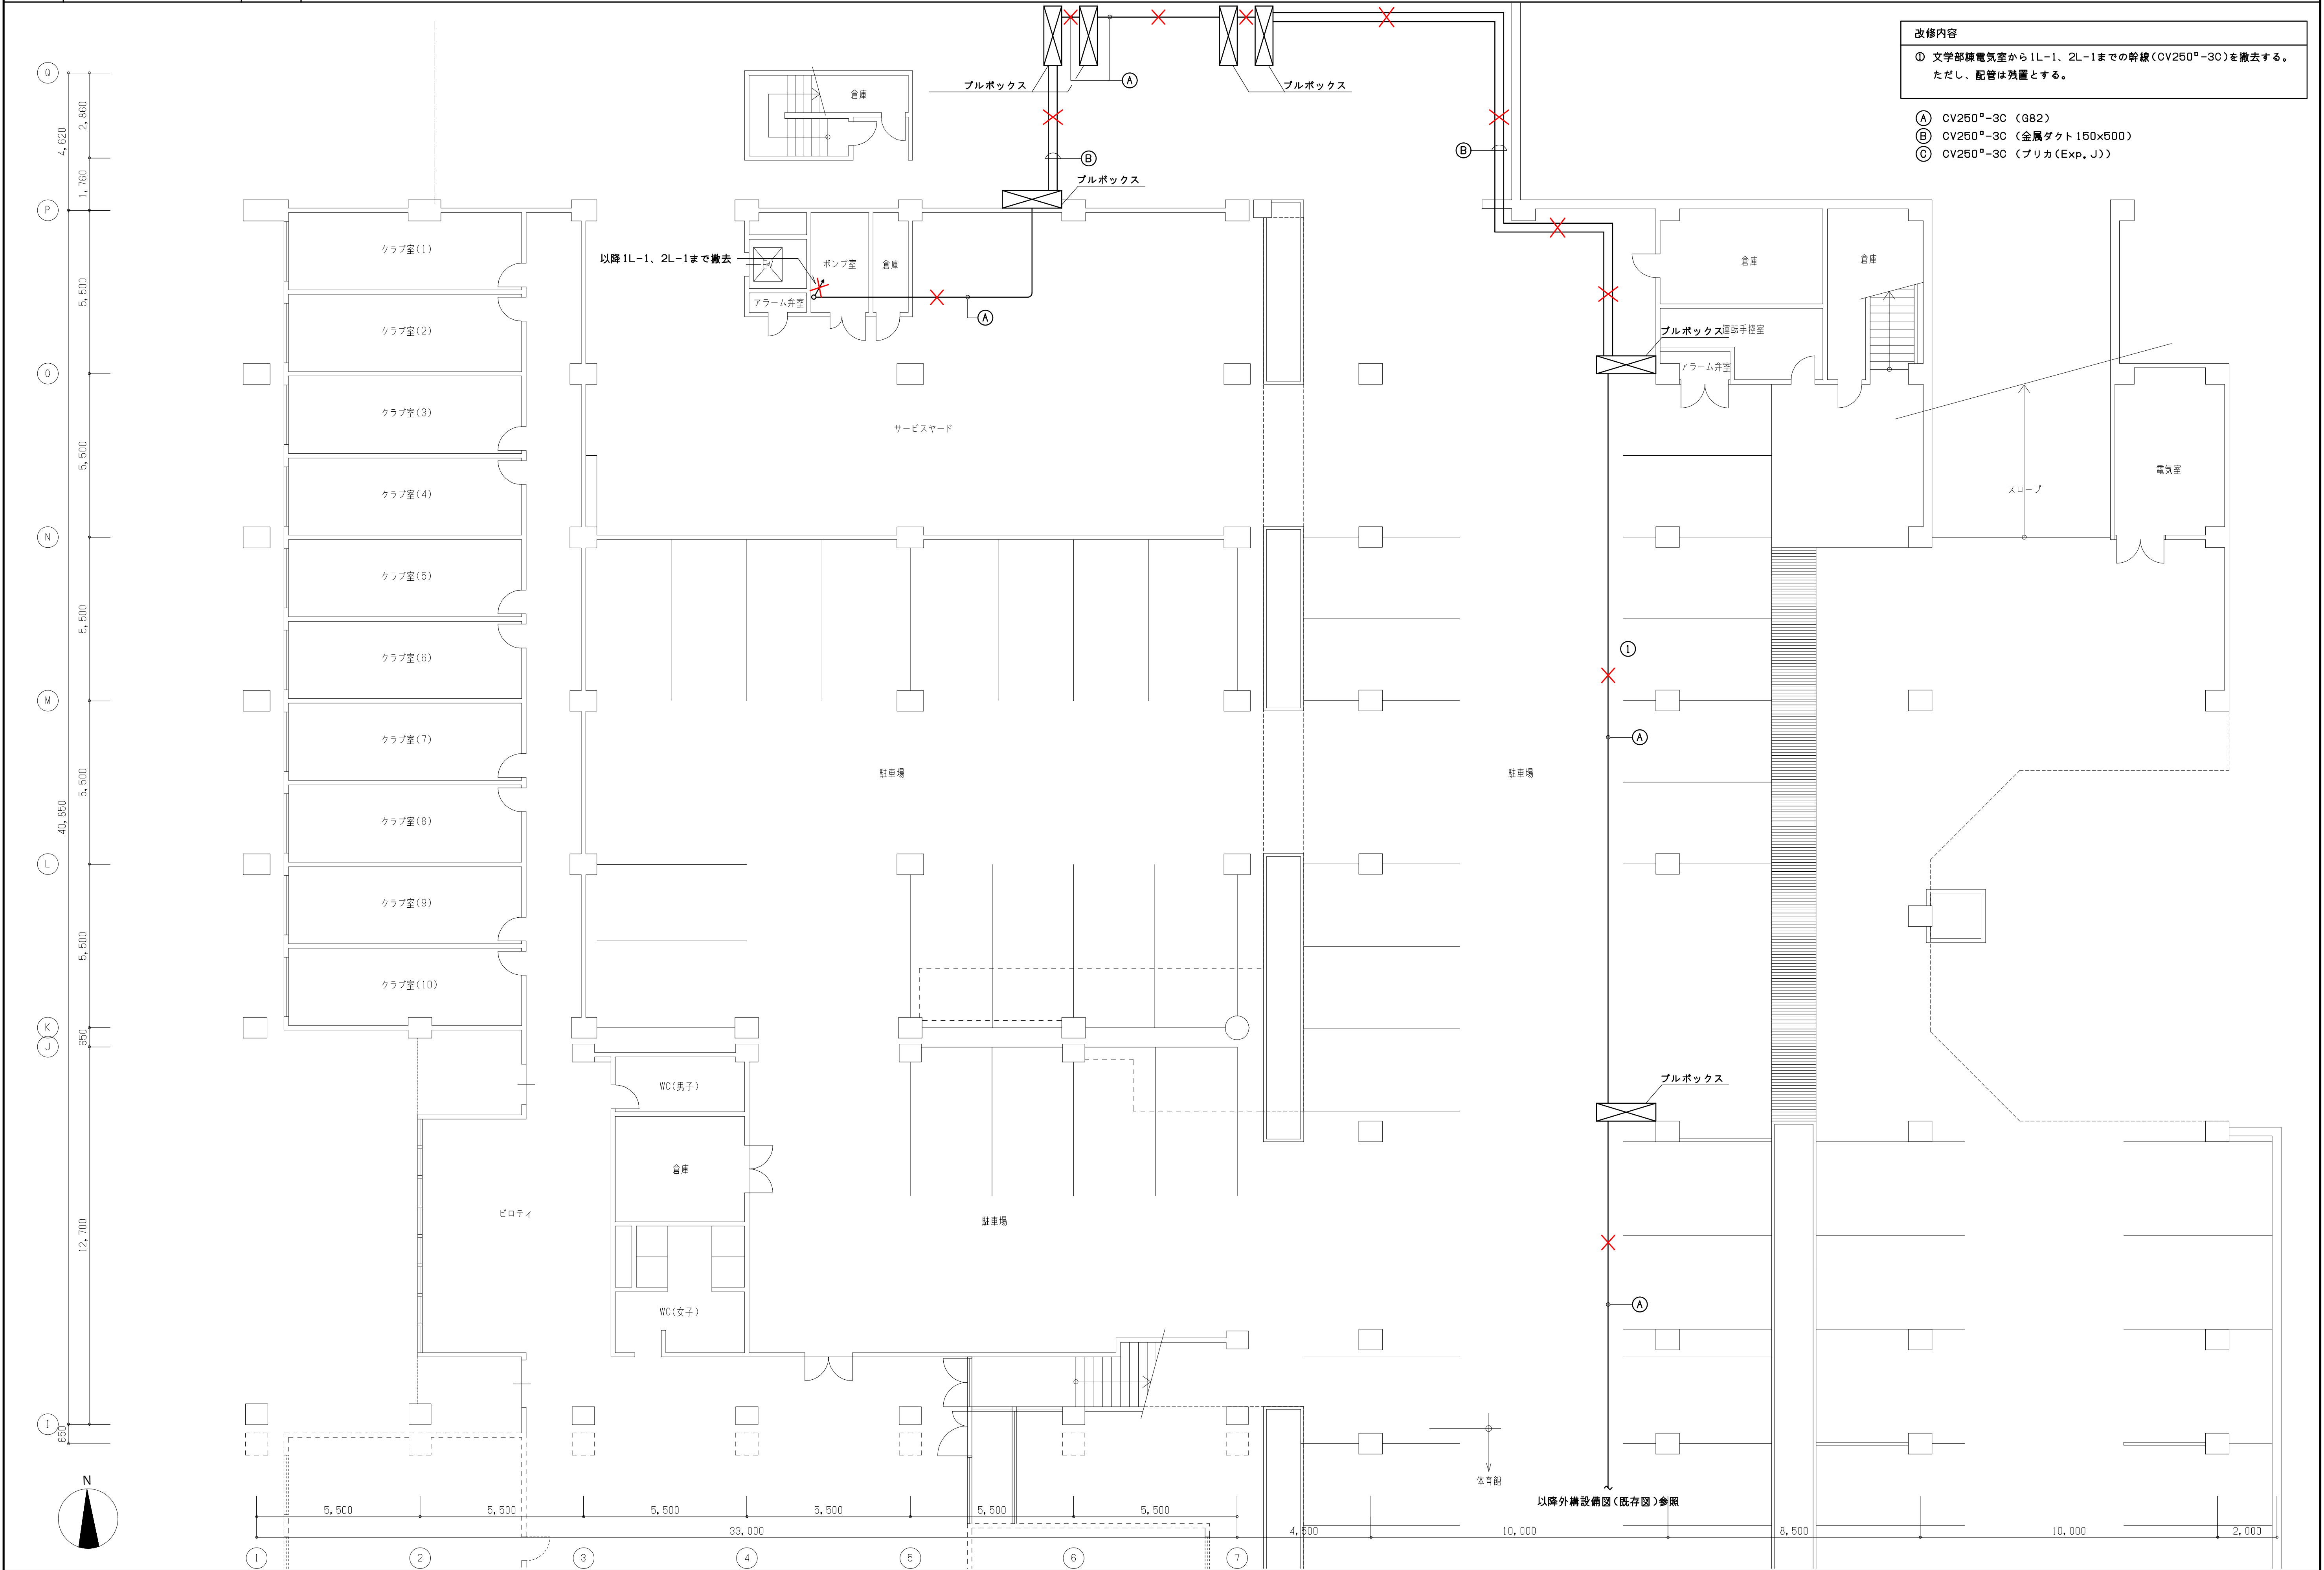

倉庫
プルボックス
Ⓐ
Ⓑ
プルボックス
プルボックス
Ⓑ
以降1L-1、2L-1まで撤去
ポンプ室
倉庫
アラーム弁室
Ⓐ
クラブ室(1)
クラブ室(2)
クラブ室(3)
クラブ室(4)
クラブ室(5)
クラブ室(6)
クラブ室(7)
クラブ室(8)
クラブ室(9)
クラブ室(10)
サービスヤード
駐車場
駐車場
駐車場
倉庫
倉庫
プルボックス運転手控室
アラーム弁室
スロープ
電気室
①
Ⓐ
プルボックス
Ⓐ
WC(男子)
倉庫
WC(女子)
ピロティ
体育館
以降外構設備図(既存図)参照
Q
P
O
N
M
L
K
J
I
2,860
1,760
4,620
5,500
5,500
5,500
5,500
5,500
40,850
650
12,700
650
N
5,500
5,500
5,500
5,500
5,500
5,500
33,000
4,500
10,000
8,500
10,000
2,000
1
2
3
4
5
6
7

改修内容

① 文学部棟電気室から1L-1、2L-1までの幹線(CV250ᴰ-3C)を撤去する。
ただし、配管は残置とする。

Ⓐ CV250ᴰ-3C (G82)
Ⓑ CV250ᴰ-3C (金属ダクト150×500)
Ⓒ CV250ᴰ-3C (プリカ(Exp.J))

J241226A26030406_幹線・コンセント設備 凡例、地下1階平面図(既設図)

着工	. .	. .	
竣工	. .	. .	
監理		. . . .	
施工		. .	

惠本 涼太郎 一級建築士
澤村 晋次 意見を聴いた建築設備士

日建設計

2026・03・27
検図者：横井 繁明

椙山女学園/星が丘キャンパス
大学会館食堂リニューアル工事

幹線・コンセント設備 凡例、地下1階平面図(既設図)

㊂ －06

No. J－ 241226 － A

1	地下1階平面図（改修）	A1:1/100 A3:1/200	注）1.破線は既設を示す。

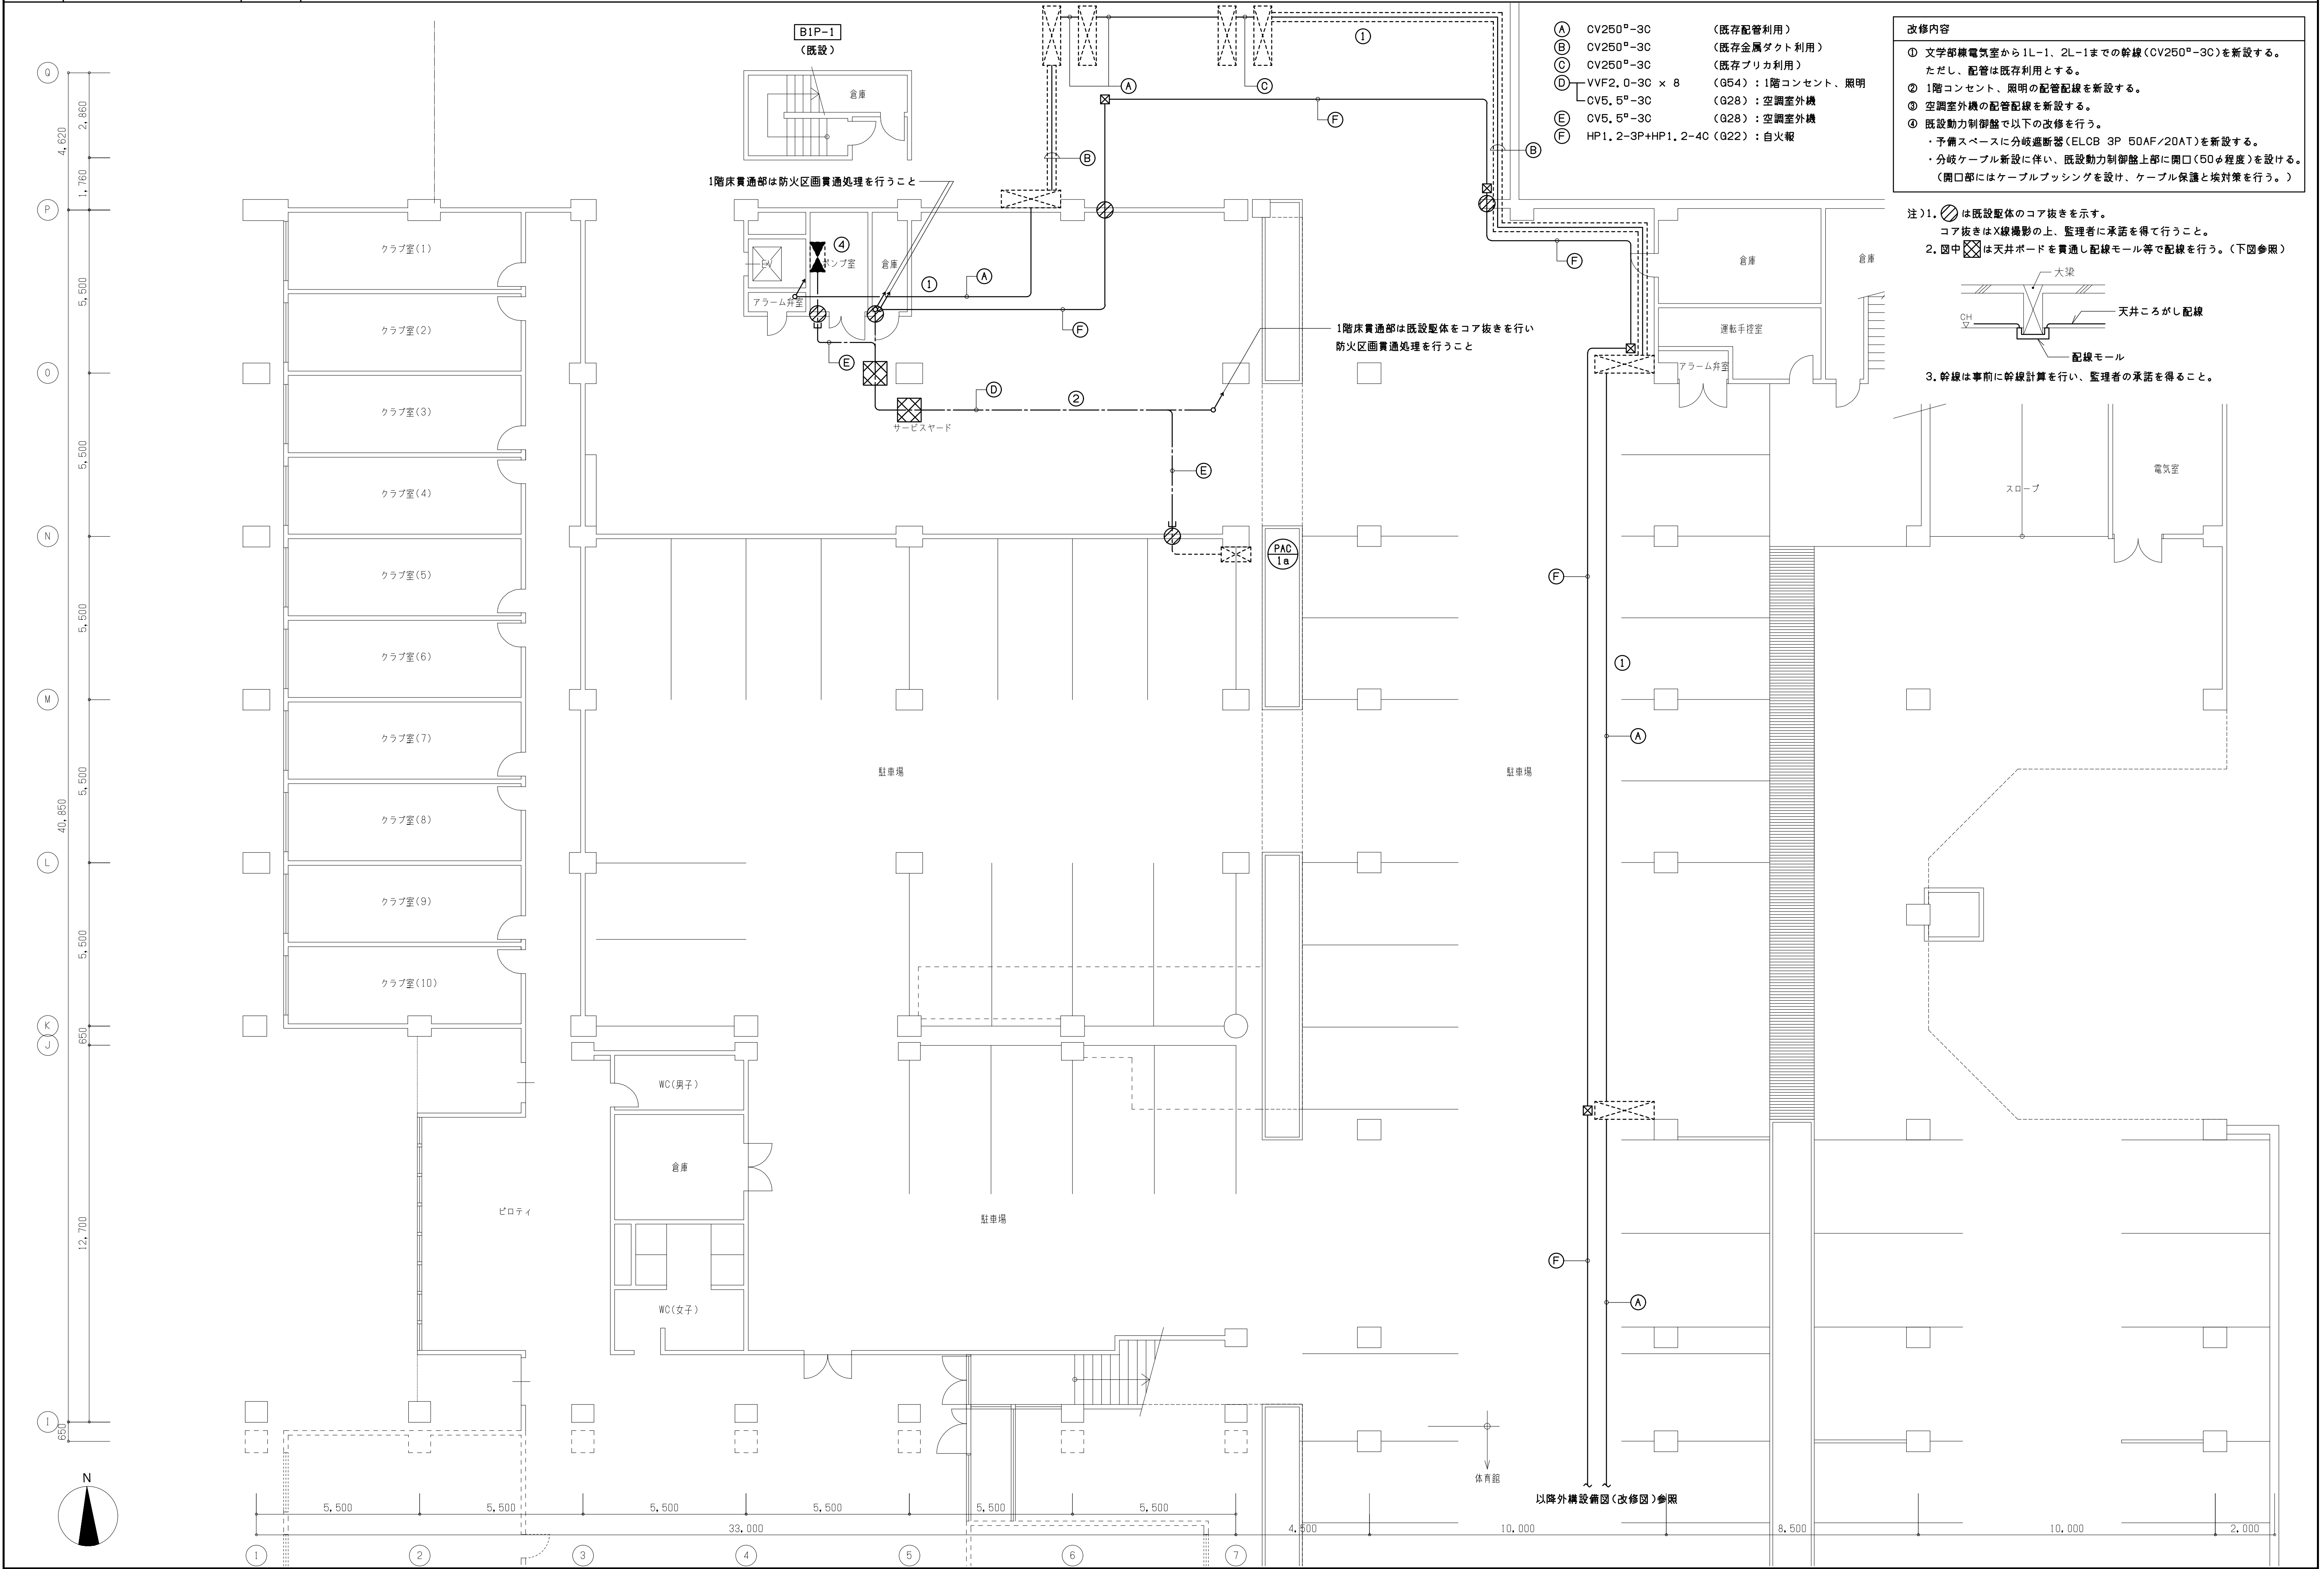
B1P-1
（既設）
倉庫
1階床貫通部は防火区画貫通処理を行うこと
EV
ポンプ室
アラーム弁室
サービスヤード
1階床貫通部は既設駆体をコア抜きを行い
防火区画貫通処理を行うこと
PAC
1a
①
②
④
Ⓐ
Ⓑ
Ⓒ
Ⓓ
Ⓔ
Ⓕ
運転手控室
スロープ
電気室
クラブ室(1)
クラブ室(2)
クラブ室(3)
クラブ室(4)
クラブ室(5)
クラブ室(6)
クラブ室(7)
クラブ室(8)
クラブ室(9)
クラブ室(10)
駐車場
WC(男子)
WC(女子)
ピロティ
体育館
以降外構設備図（改修図）参照
Q
P
O
N
M
L
K
J
I
1
2
3
4
5
6
7
4,620
2,860
1,760
5,500
5,500
5,500
5,500
5,500
40,850
650
12,700
650
5,500
5,500
5,500
5,500
5,500
5,500
33,000
4,500
10,000
8,500
10,000
2,000
N
大梁
CH
天井ころがし配線
配線モール

Ⓐ CV250□-3C （既存配管利用）
Ⓑ CV250□-3C （既存金属ダクト利用）
Ⓒ CV250□-3C （既存プリカ利用）
Ⓓ ┬VVF2.0-3C × 8 （G54）：1階コンセント、照明
└CV5.5□-3C （G28）：空調室外機
Ⓔ CV5.5□-3C （G28）：空調室外機
Ⓕ HP1.2-3P+HP1.2-4C（G22）：自火報

改修内容

① 文学部棟電気室から1L-1、2L-1までの幹線（CV250□-3C）を新設する。
　ただし、配管は既存利用とする。
② 1階コンセント、照明の配管配線を新設する。
③ 空調室外機の配管配線を新設する。
④ 既設動力制御盤で以下の改修を行う。
　・予備スペースに分岐遮断器（ELCB 3P 50AF/20AT）を新設する。
　・分岐ケーブル新設に伴い、既設動力制御盤上部に開口（50φ程度）を設ける。
　　（開口部にはケーブルブッシングを設け、ケーブル保護と埃対策を行う。）

注）1. ▨ は既設駆体のコア抜きを示す。
　コア抜きはX線撮影の上、監理者に承諾を得て行うこと。
2. 図中 ☒ は天井ボードを貫通し配線モール等で配線を行う。（下図参照）
3. 幹線は事前に幹線計算を行い、監理者の承諾を得ること。

着工	． ．	． ．	
竣工	． ．	． ．	
監理		． ．	
施工		． ．	

惠本　涼太郎　一級建築士
澤村　晋次　　意見を聴いた建築設備士

日建設計

2026・03・27　検図者：横井　繁明

椙山女学園／星が丘キャンパス
大学会館食堂リニューアル工事

幹線・コンセント設備 凡例、地下1階平面図（改修図）

㊔ －07

No. J－ 241226 － A

J241226A26080307_幹線・コンセント設備 凡例、地下1階平面図(改修図)

1	1階平面図（既設図）	A1:1/100 A3:1/200	注）1. ▭ は改修範囲外を示す。　注）2. ×、▨ は撤去を示す。

改修内容

① 文学部棟電気室から幹線（CV250□-3C、分岐以降CV100□-3C）を撤去する。
　ただし、幹線分岐位置は1階EPS内（1FL+2000mm）とする。
　（断面図詳細図参照）（配管、プルボックスは残置）
② コンセントおよび配管配線を撤去する。

記号	名　称	備　考
◩	電灯分電盤	
ⓤ	壁付コンセント　2P15A×2	Eは接地極付

注記）
1. 特記なき配管配線は下記とする。
　──── VVF2.0-3C　（PF16）

EPS周囲幹線新設部断面図

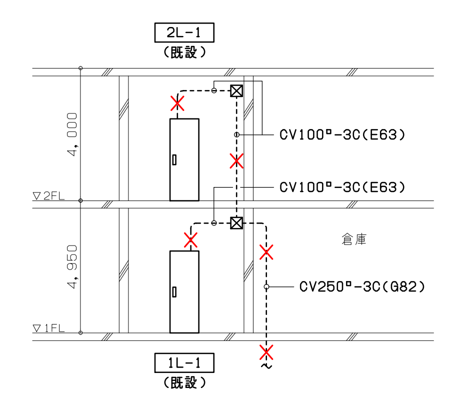

2L-1
（既設）
4,000
▽2FL
4,950
▽1FL
CV100□-3C(E63)
CV100□-3C(E63)
倉庫
CV250□-3C(G82)
1L-1
（既設）

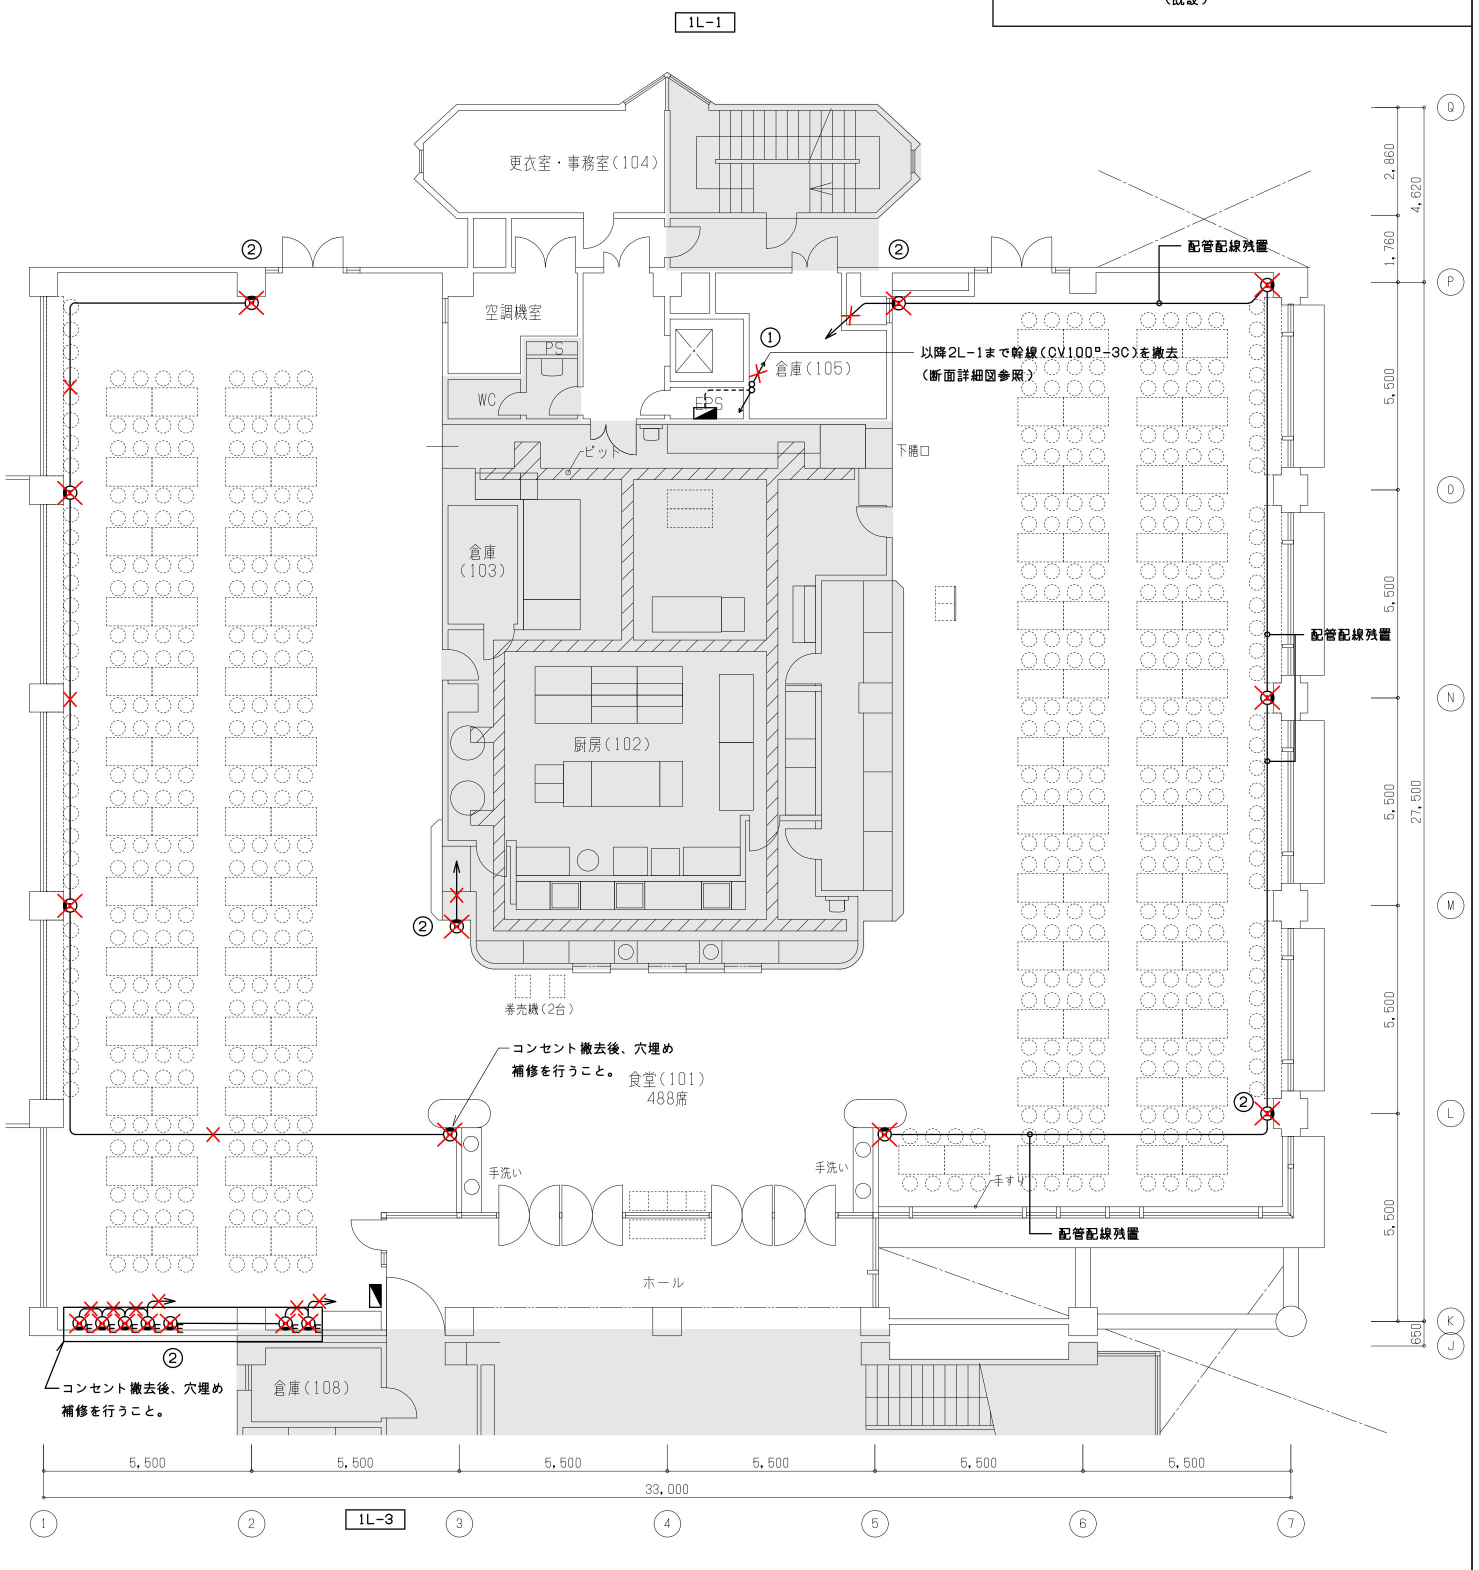

1L-1
更衣室・事務室（104）
空調機室
PS
WC
倉庫（105）
ピット
下膳口
倉庫（103）
厨房（102）
券売機（2台）
食堂（101）
488席
手洗い
手洗い
ホール
倉庫（108）
①
以降2L-1まで幹線（CV100□-3C）を撤去
（断面図詳細図参照）
配管配線残置
配管配線残置
配管配線残置
②
②
②
②
②
コンセント撤去後、穴埋め補修を行うこと。
コンセント撤去後、穴埋め補修を行うこと。
1L-3
Q
P
O
N
M
L
K
J
2,860
4,620
1,760
5,500
5,500
5,500
5,500
5,500
27,500
650
5,500
5,500
5,500
5,500
5,500
5,500
33,000
1
2
3
4
5
6
7

2	1階平面図（改修）	A1:1/100 A3:1/200	注）1. ▭ は改修範囲外を示す。 2. 破線は既設を示す。

改修内容

① 文学部棟電気室から幹線（CV250□-3C、分岐以降CV100□-3C）を新設する。
　ただし、幹線分岐位置は1階EPS内（1FL+2000mm）とする。
　（断面図詳細図参照）
② 分電盤（1L-1-2）を新設し、既設分電盤（1L-1）より幹線（CVT38□）を新設する。
③ 平面図に示すコンセントおよび二次側配管配線を新設する。
④ コンセント撤去跡にブランクプレートを新設する。

記号	名　称	備　考
◩	電灯分電盤	
ⓤ	壁付コンセント　2P15A×2	
ⓤK	壁付コンセント　2P15A×2	家具用　神保電機　KAG-2501相当品 取付詳細　意匠図1-16図参照
ⓤEH	壁付コンセント　2P15A×1　E付	電気給湯機用
⊗	ブランクプレート	
□AD	自動ドア電源送り	
●L	タンブラスイッチ（1P15A×1）	自動ドア用
⬚	空調室内機	別途機械設備工事

注記）
1. 特記なき配管配線は下記とする。

		隠ぺい	露出	屋外
──/──	VVF2.0-2C	（PF16）	（E19）	（G16）
────	VVF2.0-3C	（PF16）	（E19）	（G16）

2. ▨ は既設躯体のコア抜きを示す。
　⊗ は既設躯体のコア抜きの上、防火区画貫通処理を行う。
　コア抜きはX線撮影の上、監理者に承諾を得て行うこと。
3. 幹線は事前に幹線計算を行い、監理者の承諾を得ること。
4. 特記なき限りコンセントの取付高さはFL+300mmとする。
　また、家具コンセントの取付高さは西側カウンターはFL+800mm、南側カウンターはFL+800mm、西側ソファー席はFL+300mmとする。

EPS周囲幹線新設部断面図

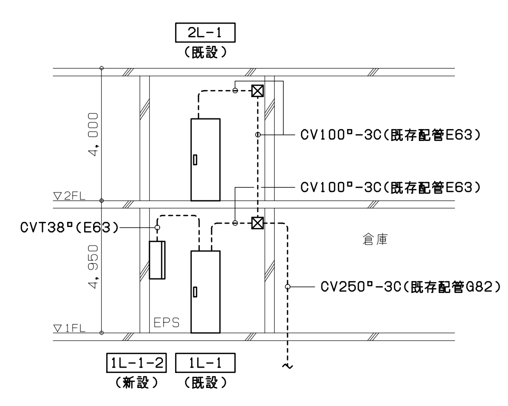

2L-1
（既設）
4,000
▽2FL
4,950
▽1FL
CV100□-3C(既存配管E63)
CV100□-3C(既存配管E63)
CVT38□(E63)
倉庫
EPS
CV250□-3C(既存配管G82)
1L-1-2
（新設）
1L-1
（既設）

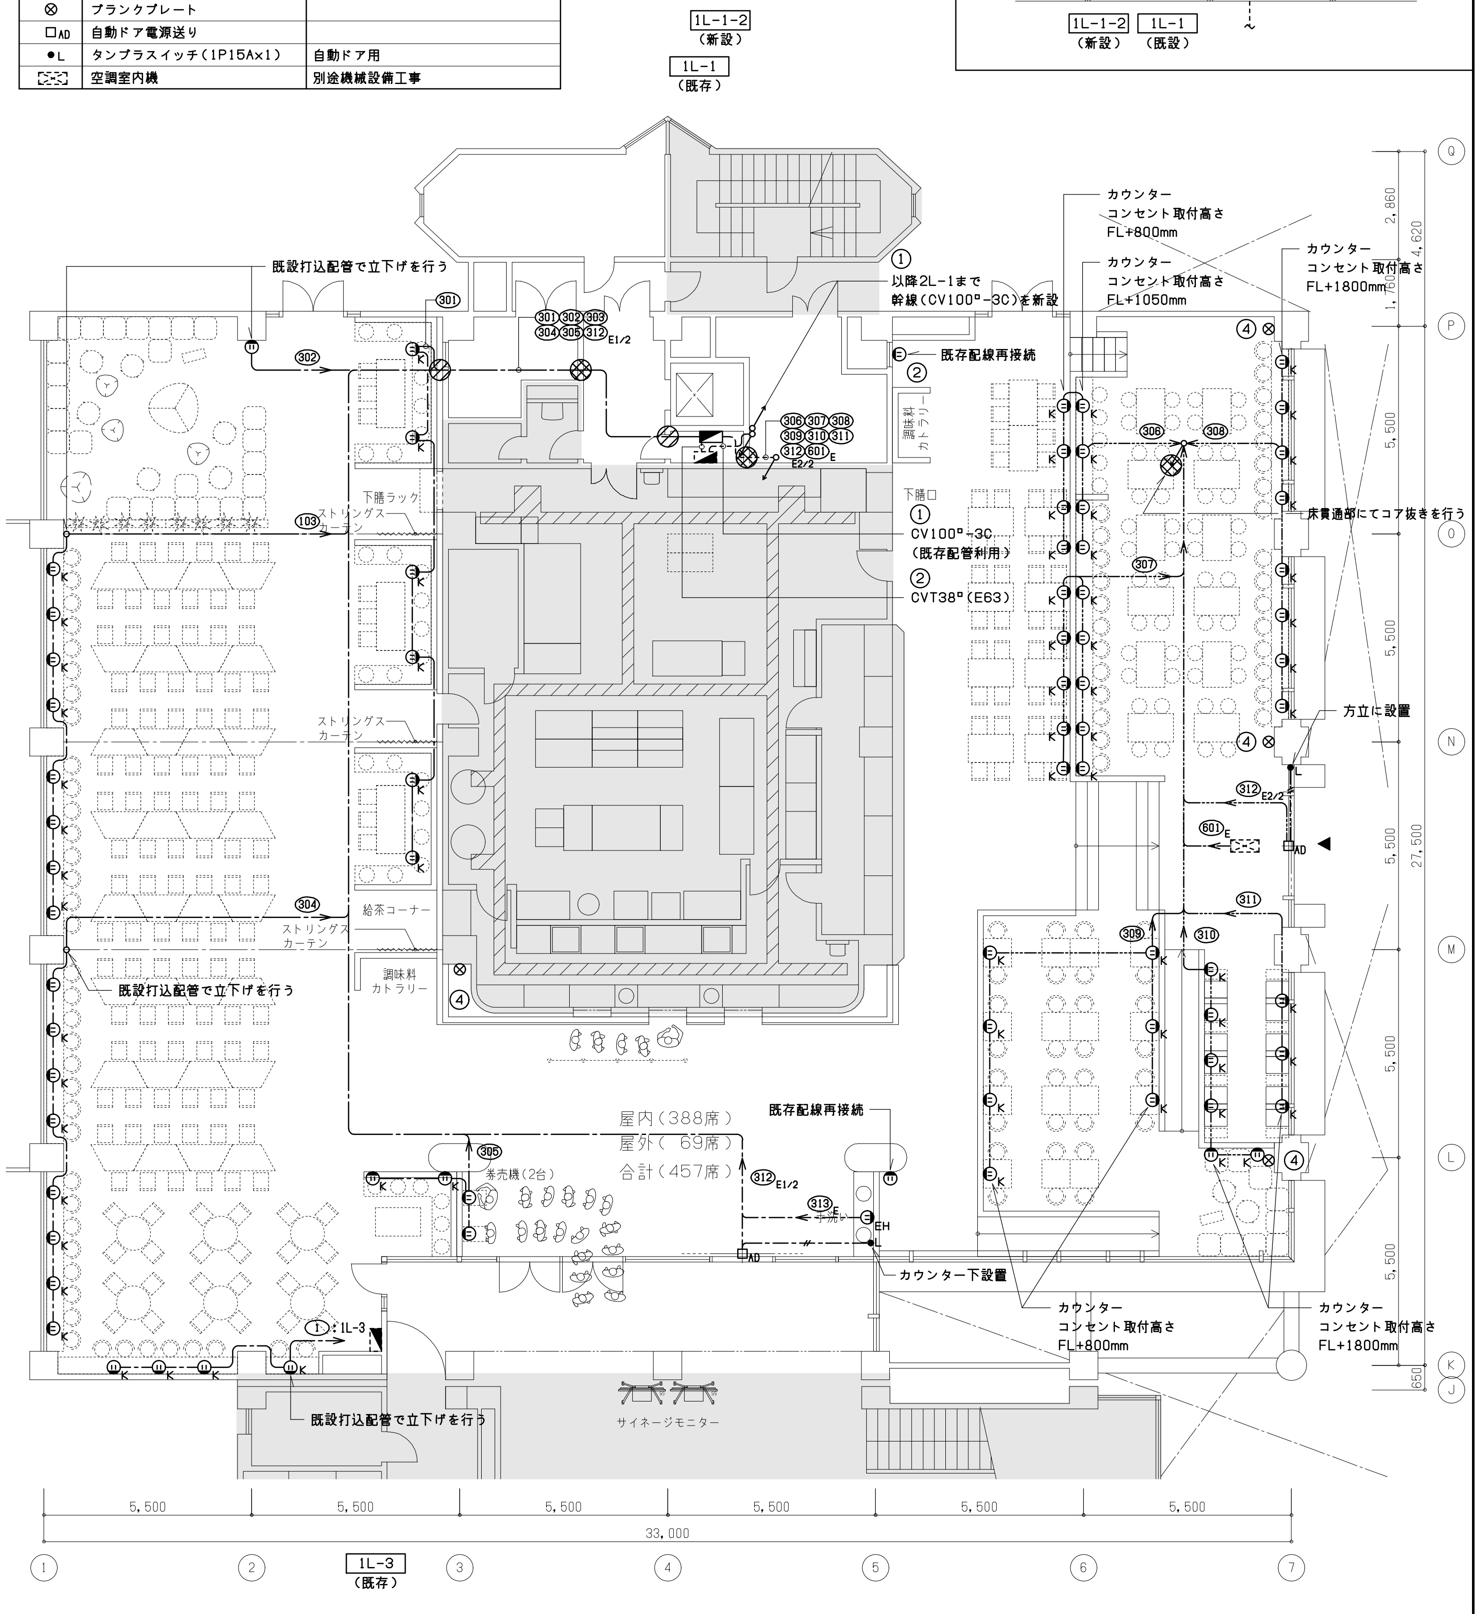

1L-1-2
（新設）
1L-1
（既存）
既設打込配管で立下げを行う
既設打込配管で立下げを行う
既設打込配管で立下げを行う
301
302
301 302 303
304 305 312
E1/2
306 307 308
309 310 311
312 601 E
E2/2
①
以降2L-1まで
幹線（CV100□-3C）を新設
既存配線再接続
既存配線再接続
②
調味料
カトラリー
下膳ラック
下膳口
①
CV100□-3C
（既存配管利用）
②
CVT38□(E63)
103
ストリングス
カーテン
ストリングス
カーテン
304
給茶コーナー
ストリングス
カーテン
調味料
カトラリー
④
カウンター
コンセント取付高さ
FL+800mm
カウンター
コンセント取付高さ
FL+1050mm
カウンター
コンセント取付高さ
FL+1800mm
④
306
308
307
床貫通部にてコア抜きを行う
方立に設置
④
312
E2/2
601
E
AD
311
309
310
K
④
屋内（388席）
屋外（ 69席）
合計（457席）
305
券売機（2台）
312
E1/2
313
EH
AD
カウンター下設置
カウンター
コンセント取付高さ
FL+800mm
カウンター
コンセント取付高さ
FL+1800mm
①
1L-3
サイネージモニター
1L-3
（既存）
Q
P
O
N
M
L
K
J
2,860
4,620
1,760
5,500
5,500
5,500
5,500
5,500
27,500
650
5,500
5,500
5,500
5,500
5,500
5,500
33,000
1
2
3
4
5
6
7

着工	・　・	・　・	
竣工	・　・	・　・	
監理		・　・	
		・　・	
施工		・　・	

惠本　涼太郎　一級建築士
澤村　晋次　　意見を聴いた建築設備士

日建設計

2026・03・27
検図者：横井　繁明

椙山女学園／星が丘キャンパス
大学会館食堂リニューアル工事

幹線・コンセント設備 凡例、1階平面図（既設図）（改修図）

電
－08

No.　J－ 241226 － A

J241226A26080308_幹線・コンセント設備　凡例、1階平面図（既設図）（改修図）

1 新設分電盤（1L-1-2）注記 —

注）新設分電盤（1L-1-2）にのみ適用する。

1. 盤面表示ランプはLEDとする。
2. 分電盤の1次側、2次側配線とも、クランプメータで測定可能な構造とする。
3. 主幹配線用遮断器は漏電表示付とする。
4. MCCB1Pブレーカはニュートラルスイッチ（NS）付ブレーカとする。
5. 分電盤の接地端子数は、分岐ブレーカ数分設置すること。（予備スペース分見込むこと）
6. 分電盤に設置するSPDの仕様は下記とする。

避雷器方式　：酸化亜鉛型（切離し装置内蔵）
避雷器形式　：着脱可能型（動作表示付）
定格電圧　　：110V、220V
公称放電電流：1,500A
制限電圧　　：（8／20μS、1,500A）560V以下（110V回路）
　　　　　　　1,000V以下（220V以下回路）
放電耐量　　：雷インパルス大電流（4／10μS）20kA 2回

7. 分岐ブレーカは、2個の予備ブレーカを実装するものとし、予備スペースを設ける。
8. 特記なき分電盤回路の回路種別及び添字は下記とする。

（一般回路）
- (10n) 1φ100V 照明
- (20n) 1φ200V 照明
- (30n) 1φ100V コンセント
- (40n) 1φ200V コンセント

（一般回路）
- (En) 1φ100V 誘導灯
- ( )E ELB回路
- ( )R リモコン回路
- ( )ER リモコン回路（ELB回路）
- ( )ET タイムスイッチ回路（ELB回路）

（凡例）

記号	名称	記号	名称
─/×─	MCCB 1P 50AF／20AT(NS付)	Wh	電力量計(検定付)
─//×─	MCCB 2P 50AF／20AT	PL	パイロットランプ
─//×─ ELB	ELCB 2P 50AF／20AT	RT	リモコントランス
─▲─	リモコンリレー 2P 20A(両切)	LA	SPD

2 分電盤姿図（壁掛型） —

新設（1L-1-2）

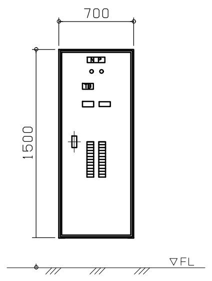

正面図

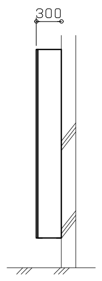

側面図

※製造者標準色塗装とする。
※外扉無し、内扉付きとする。
※寸法は参考とする。

3 分電盤結線図 —

分電盤（1L-1）結線図（改修）

注）破線は既設を示す。

改修内容
- 主幹遮断器二次側端子で新設ケーブルを共ばさみで接続する。
- 既設部分の分電盤改修内容は、分電盤リスト参照とする。
- 1L-1-2へのケーブル新設に伴い、既設分電盤上部に開口（50φ程度）を設ける。（上記開口にはケーブルブッシングを設け、ケーブル保護と埃対策を行う。）

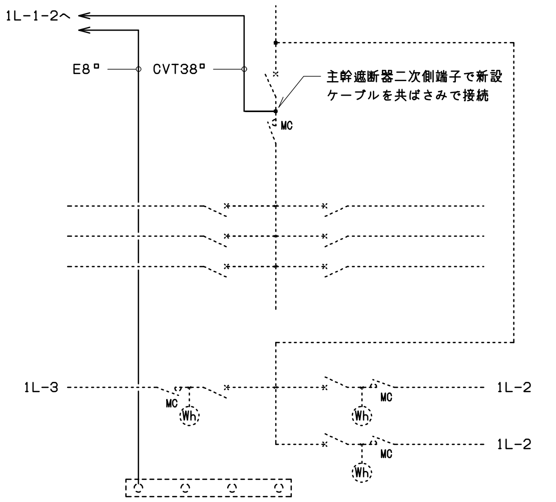

分電盤（1L-3）結線図（改修）

注）破線は既設を示す。

改修内容
- 既設ブレーカ二次側を全て撤去し、新設負荷を接続する。

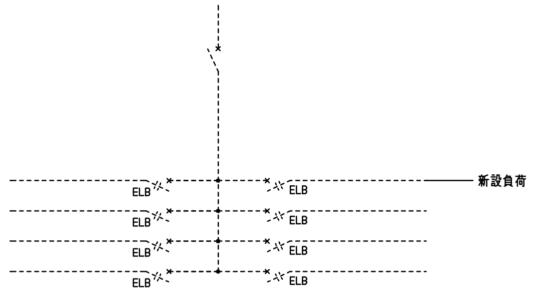

分電盤（1L-1-2）結線図（新設）

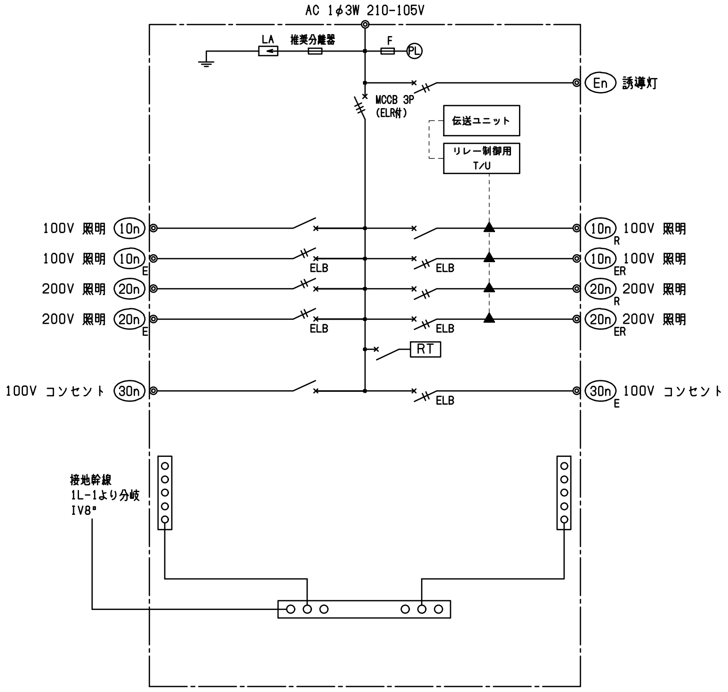

4 分電盤リスト（1L-1）（改修） —

盤名（盤形式） 幹線番号 幹線サイズ	電気方式 主幹 合計容量	WHM	分岐回路 電圧［V］	分岐回路 番号	分岐回路 配線用遮断器［AF／AT］	負荷名称	負荷容量［VA］	備考	改修内容
1L-1	AC 1φ3W 210／105V		100	21	MCCB1P 50／20	コンセント	150		
幹線番号：12	MCCB3P		100	22	MCCB1P 50／20	予備			
幹線サイズ：CV100°-3C	225AF／150AT		100	23	MCCB1P 50／20	電灯	190		
			100	24	MCCB1P 50／20	予備			
			100	25	MCCB1P 50／20	予備			
	L=4,980VA								
	C=1,150VA		100	1	MCCB1P 50／20	電灯	380	MC	
	主幹一次側送り 15,896VA		100	2	ELCB2P 50／20	外灯	450	TS・MC付	
	主幹二次側送り 16,200VA		100	3	MCCB1P 50／20	予備			負荷撤去後、ブレーカー残置
	T=38,226VA								
			100	1	MCCB1P 50／20	予備		RR×3	負荷撤去後、ブレーカー残置
			100	2	MCCB1P 50／20	予備		RR×2	負荷撤去後、ブレーカー残置
			100	3	MCCB1P 50／20	予備		RR×2	負荷撤去後、ブレーカー残置
			100	4	MCCB1P 50／20	予備			負荷撤去後、ブレーカー残置
			100	5	MCCB1P 50／20	予備			負荷撤去後、ブレーカー残置
			100	6	MCCB1P 50／20	電灯	1260		
			100	7	MCCB1P 50／20	電灯	1200		
			100	8	MCCB1P 50／20	予備			負荷撤去後、ブレーカー残置
			100	9	MCCB1P 50／20	換気用	500	RR×3	
			100	10	MCCB1P 50／20	予備			負荷撤去後、ブレーカー残置
			100	11	MCCB1P 50／20	予備		WH付	負荷撤去後、ブレーカー残置
			100	12	MCCB1P 50／20	電灯	200	RR×2	負荷一部撤去、容量見直し
			100	13	MCCB1P 50／20	1R-1・2R-1	500	制御回路	
			100	14	MCCB1P 50／20	電灯	1200	RR×2	
			100	15	MCCB1P 50／20	予備			
			100	16	MCCB1P 50／20	R-T	100		
			200／100	主幹一次側送り	MCCB3P 100／100	1L-2	7922	WH付	
			200／100	主幹一次側送り	MCCB3P 100／100	1L-2	7474	WH付	
			200／100	主幹一次側送り	MCCB3P 50／20	1L-3	500	WH付	負荷容量見直し
			200／100	主幹二次側送り		1L-1-2	14765		負荷追加 1L-1主幹遮断器二次側で配線接続

5 分電盤リスト（1L-3）（改修） —

盤名（盤形式） 幹線番号 幹線サイズ	電気方式 主幹 合計容量	WHM	分岐回路 電圧［V］	分岐回路 番号	分岐回路 配線用遮断器［AF／AT］	負荷名称	負荷容量［VA］	備考	改修内容
1L-3	AC 1φ3W 210／105V		100	1	MCCB2P 50／20	コンセント	500		負荷撤去後、再接続 ELCB撤去、MCCB新設
幹線番号：1L-1より分岐	MCCB3P		100	2	ELCB2P 50／20	予備			負荷撤去後、ブレーカー残置
幹線サイズ：CV14°-3C	50AF／50AT		100	3	ELCB2P 50／20	予備			負荷撤去後、ブレーカー残置
			100	4	ELCB2P 50／20	予備			負荷撤去後、ブレーカー残置
			100	5	ELCB2P 50／20	予備			負荷撤去後、ブレーカー残置
			100	6	ELCB2P 50／20	予備			負荷撤去後、ブレーカー残置
	C=500VA		100	7	ELCB2P 50／20	予備			負荷撤去後、ブレーカー残置
	T=500VA		100	8	ELCB2P 50／20				

6 分電盤リスト（1L-1-2）（新設） —

盤名称 盤形状 結線タイプ	回路種別 電気方式・電圧 主幹器具	警報 トリップ	警報 漏電	分岐回路 回路番号	分岐回路 分岐遮断器	分岐回路 負荷容量［VA］	分岐回路 負荷名称	リモコンリレー 2P 20A	備考
1L-1-2	AC1φ3W 200-100V	○	○	E1	MCCB 2P 1E 50AF／20AT	6	誘導灯		
屋内壁掛型	MCCB 3P 100AF／100AT								
	合計容量：14.8kVA			101	MCCB 2P 1E 50AF／20AT	470	西側間接照明、ペンダントライト	3	
				102	MCCB 2P 1E 50AF／20AT	406	南側スポットライト	1	
				103	MCCB 2P 1E 50AF／20AT	720	東側スポットライト、ブラケットライト	2	
				104	ELCB 2P 1E 50AF／20AT	240	外構スポットライト	2	別途外構工事分
					MCCB 2P 1E 50AF／20AT		予備		
				201	MCCB 2P 2E 50AF／20AT	1,272	西側ダウンライト	3	
				202	MCCB 2P 2E 50AF／20AT	2,528	南側光天井、間接照明、手洗い間接照明	3	
				203	ELCB 2P 2E 50AF／20AT	938	外構間接照明	2	別途外構工事分
				301	MCCB 2P 1E 50AF／20AT	600	西側家具コンセント		
				302	MCCB 2P 1E 50AF／20AT	150	北側壁コンセント		
				303	MCCB 2P 1E 50AF／20AT	800	西側家具コンセント		
				304	MCCB 2P 1E 50AF／20AT	800	西側家具コンセント		
				305	MCCB 2P 1E 50AF／20AT	500	南側家具コンセント、券売機		
				306	MCCB 2P 1E 50AF／20AT	800	東側家具コンセント		
				307	MCCB 2P 1E 50AF／20AT	800	東側家具コンセント		
				308	MCCB 2P 1E 50AF／20AT	800	東側家具コンセント		
				309	MCCB 2P 1E 50AF／20AT	700	東側家具コンセント		
				310	MCCB 2P 1E 50AF／20AT	600	東側家具コンセント		
				311	MCCB 2P 1E 50AF／20AT	300	東側家具コンセント		
				312	ELCB 2P 1E 50AF／20AT	200	自動ドア		
				313	ELCB 2P 1E 50AF／20AT	1,100	電気給湯機		
				601	ELCB 2P 1E 50AF／20AT	140	空調室内機		
					MCCB 2P 1E 50AF／20AT		リモコントランス		
					その他機器：年間プログラムタイマー×1、リレー制御用T/U（4回路用）×4				

着工	. .	. .	
竣工	. .	. .	
監理		. .	
		. .	
施工		. .	
		. .	

惠本　涼太郎　一級建築士
澤村　晋次　　意見を聴いた建築設備士

日建設計

2026・03・27　　検図者：横井 繁明

椙山女学園／星が丘キャンパス
大学会館食堂リニューアル工事

分電盤注記、分電盤リスト

電
－09

No. J－ 241226 － A

J241226A26080309_分電盤注記、分電盤リスト

1	照明器具姿図（既設図）	—	2	照明器具姿図（改修図）	—

C	
Ca	LDL40W×1
Cb	LDL20W×1

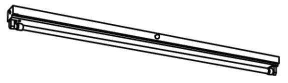

Ca ：パナソニック NNF41030 LE9
Cb ：パナソニック NNF21030 LE9

E	
Ea	FL40W×2

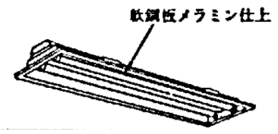

パナソニック 埋込425K

A	埋込形下面開放					
Aa186c	LED186W以下	13900lm	LZ	㊕	㊫	3500K、Ra84

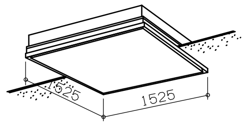

パナソニック 光天井XFY6600CLT9×1+FYY80071相当品

I	間接照明用					
Id20	LED20W以下	2220lm	LN	㊢	㊫	4200K、Ra86
Id18	LED18W以下	1930lm	LN	㊢	㊫	4200K、Ra86
Id17	LED17W以下	1840lm	LN	㊢	㊫	4200K、Ra86
Id8	LED8W以下	820lm	LN	㊢	㊫	4200K、Ra86
Id5	LED5W以下	500lm	LN	㊢	㊫	4200K、Ra86

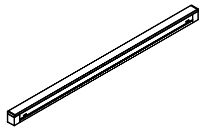

DNライティング SFL-S相当品

I	間接照明用					
Ia49c	LED49W以下	3910lm	LZ	㊢	㊫	3500K、Ra85
						23灯

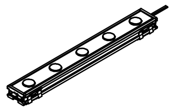

パナソニック PTSGB/100/35K/M/23相当品

K	
Ka	LED14W×1

パナソニック NYY46301K

L	
Lc	FL10W×1

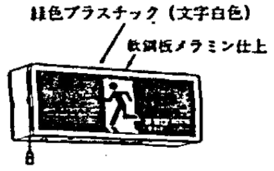

パナソニック FA11971K

I	間接照明用					
Ib24c	LED24W以下	955lm	LZ	㊢	㊫	3500K、Ra83
Ib27c	LED27W以下	1130lm	LZ	㊢	㊫	3500K、Ra83

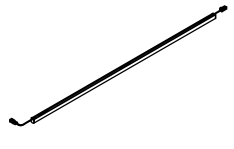

Ib24c ：パナソニック NTN81062相当品
Ib27c ：パナソニック NTN81042相当品

a	ダウンライト					
aa13c	LED13W以下	1170lm	LZ	㊢	㊫	3500K、Ra85

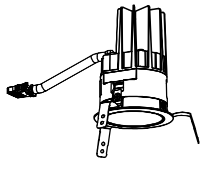

パナソニック NTS72892W-100+NTS90101LJ9相当品

a	ダウンライト					
ab12c	LED12W以下	1570lm	LZ	㊢	㊫	3500K、Ra85

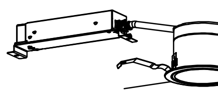

パナソニック ダウンライトXND1537WVLJ9相当品

L	
Lg	FL20W×1

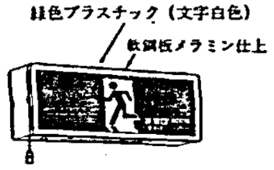

パナソニック FW11977

X	
Xc2E	LED2W

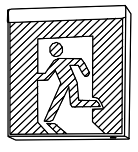

パナソニック FA10312

a	ダウンライト					
ac12c	LED12W以下	1590lm	LZ	㊢	㊫	3500K、Ra85

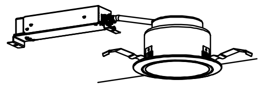

パナソニック ダウンライトXND1557WVLJ9相当品

s	スポットライト					
sa14	LED14W以下	1070lm	LN	㊢	㊯	3500K、Ra83

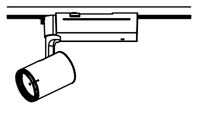

パナソニック NTS00152B相当品

X	避難口誘導灯					
Xb2E	LED2W以下			㊢	㊯	電池内蔵型、直付型 B級BL形

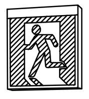

パナソニック FA20312CLE1相当品

P	ペンダントライト					
Pa12	LED12W以下	1520lm	LN	㊢	㊫	2700K、220°配光

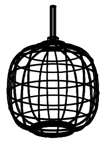

注）コード長さを調整の上、納品とする。
（長さは現場指示とする）

ルイスポールセン VL45ラジオハウスペンダント相当品

R	ブラケットライト					
Ra60	JD60W以下	790lm	LN	㊢	㊫	2900K

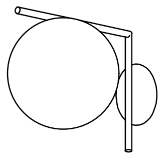

FLOS（フロス）IC Lights C/W1相当品

シンボルおよび説明

照明器具記号

基本記号

1 LED、OEL系

A a 20 （×3） wp
- 型式記号
- 型式補助記号
- 消費電力（小数点以下切上げ）
- 台数（システムダウンライトなど制御装置を複数含む場合）
- 補助記号

*型式補助記号は同じ型式で複数の種類がある場合に使用する。

2 蛍光灯、白熱灯、放電灯系

A a 32 2 wp
- 型式記号
- 型式補助記号
- 使用管球
- 球数
- 補助記号

*型式補助記号は同じ型式で複数の種類がある場合に使用する。

補助記号						
wp	防雨型	P	パイプ吊	E	誘導灯（電池内蔵型）
mp	防湿型	G	ガード付	EL	誘導灯（電池内蔵、長時間型）
c	調光型	D	非常用照明（電池内蔵型）	e	誘導灯（電源別置型）
s	人感センサー付	DL	非常用照明（電池内蔵、長時間型）		
l	リフター付	d	非常用照明（電源別置型）		

照明器具型式記号

記号	型式	記号	型式	記号	型式	記号	型式
A	埋込形下面開放	N	流し元灯	a	ダウンライト	n	
B	埋込形カバー付	O	低温用	b	ユニバーサルダウンライト	o	
C	埋込形ルーバ付	P	ペンダント	c	ウォールウォッシャーダウンライト	p	水中照明
D	直付型	Q	黒板灯	d	シーリングダウンライト	q	システムダウンライト
E	防爆型	R	ブラケット、ウォールライト	e	非常用照明	r	レンジフード用
F	逆富士形	S	システム天井用	f	フットライト	s	スポットライト
G	殺菌灯	T	トラフ形	g	赤色表示灯	t	タスクライト
H	クリーンルーム用	U	殺虫灯	h	高天井用	u	地中埋込アッパーライト
I	間接照明用	V	防災設備表示灯	i		v	ボラードライト
J	電磁波低減型	W		j		w	投光器
K	反射笠付	X	避難口誘導灯	k		x	
L	片反射付	Y	通路誘導灯	l		y	
M	階段通路誘導灯	Z	外灯	m		z	

ランプ記号

LED、OEL		蛍光灯		白熱灯	
LED	LED一体型	FL	直管	IL	シリカランプ
LDL	直管型LEDランプ	FHF	Hf	KR	クリプトンランプ
LDA	電球型LEDランプ	FC	丸形	WB	ボールランプ
OEL	有機EL	FPL	ツイン1	RF	リフレクタランプ
HID		FDL	ツイン2	JD	ミニハロゲンランプ
H	高圧水銀灯	FHT	ツイン3	JDR	ミニハロゲンランプ（ダイクロミラー付）
MH	メタルハライドランプ	FHP	Hfツイン1	JE	非常用照明用ミニハロゲンランプ
CDM	セラミックメタルハライドランプ	FG	殺菌灯		
NH	高圧ナトリウムランプ				
NL	低圧ナトリウムランプ				

LED制御装置、安定器特性

LED		蛍光灯	
LN	一般形	PH	一般形（高出力）
LJ	初期照度補正形	PN	一般形（定格出力）
LX	連続調光形（調光下限値35%以下）	PR	一般形（省電力出力）
LZ	連続調光形（調光下限値5%以下）	PK	初期照度補正形（高出力）
		PJ	初期照度補正形（定格出力）
		PW	連続調光形（調光下限値60%以下）
HID		PX	連続調光形（調光下限値35%以下）
BP	電子安定器	PZ	連続調光形（調光下限値5%以下）
BH	一般形高効率形		
BC	低始動電流形		

姿図欄器具形式説明

LED一体型、OEL系

（基本記号）	（ランプ特性）	（器具光束（以上））	（LED制御装置特性）	（性能・形状）	（塗装色）	（備考）
Sa40c	LED40W	4000lm	LZ	㊢	㊫	4000K、Ra84以上

- ランプ記号
- 消費電力
- ㊫は製造者標準色、㊯は指定色
- ㊢は製造者標準品、㊕は特注品

LEDランプ系

（基本記号）	（ランプ特性）	（器具光束（以上））	（LED制御装置特性）	（性能・形状）	（塗装色）	（備考）
Aa62	LDL40×2	7000lm	LJ	㊢	㊫	4000K、Ra84以上

- ランプ記号
- 使用管球、灯数
- ㊫は製造者標準色、㊯は指定色
- ㊢は製造者標準品、㊕は特注品

蛍光灯、白熱灯、放電灯系

（基本記号）	（ランプ特性）	（器具光束（以上））	（安定器特性）	（性能・形状）	（塗装色）	（備考）
Ka322	FHF32W×2	9350lm	PK	㊢	㊫	5000K、Ra84以上

- ランプ記号
- 使用管球、灯数
- ㊫は製造者標準色、㊯は指定色
- ㊢は製造者標準品、㊕は特注品

注記事項

- LED制御装置、安定器などが別置型の器具については、器具に含めて見込むこと。
- 電池内蔵型の非常用照明および誘導灯は、リモコン自己点検機能付とする。
- 外灯、ボラードライトについては、コンクリート基礎も見込むこと。基礎サイズは図示がない場合、製造者推奨のものとする。
- LED器具については、器具のモデルチェンジ周期が短いため、図面記載相当品が製造中止または製造中止予定になった段階で代替品に置き換えた上で監理者に提示し再確認して決定すること。
- 特記なきは、使用電圧100~242Vのボルトフリーとする。
- 特定天井へ設置する照明器具については照明器具の耐震設計・施工ガイドライン（2014）に準拠し施工すること。
- 照明器具の消費電力はJIS C 8105-3の測定方法による。
- 下記に示す器具については、見本を用意し現場事務所内で点灯確認すること。（Aa186c、Pa12、Ra60）
- 照明器具は取付金具、連結金具、落下防止金具等の付属品も見込むこと。

着工	． ．	． ．	
竣工	． ．	． ．	
監理		． ．	
		． ．	
施工		． ．	
		． ．	

惠本　涼太郎　一級建築士
澤村　晋次　意見を聴いた建築設備士

日建設計

2026・03・27

検図者：横井 繁明

椙山女学園／星が丘キャンパス
大学会館食堂リニューアル工事

照明器具姿図

電

—10

J — 241226 - A

J241226A26080310_照明器具姿図

1　照明制御システムブロック図　—　（新設）

＜調光システム概要＞
- 食堂内の照明器具の明るさを調光ユニットで制御する。
- 調光ユニットは4回路または6回路の調光が可能なものとする。
- シーン設定は現地調整とし、シーン選択器ですべての調光ユニットのシーンを一括で呼出可能なシステムとする。
- ペンダントライト等、非調光型の照明器具は発停制御のみとする。

＜凡例＞

I/F ：信号変換インターフェース
▨ ：調光器具盤
LD ：配線ダクト
Ⓢp ：無線調光リモコン
○ ：ダウンライト
▽ ：スポットライト
▭ ：間接照明
⊖ ：ペンダントライト
♀ ：アジャスタブルライト

注）1. 調光器具盤は木板等に図示の調光器具を取り付けたものとする。
2. 特記なき配管配線は下記とする。
—S— ：CPEVS 0.9-1P(PF16)
—3P— ：CPEVS 0.9-3P(PF16)
—— ：VVF2.0-3C　(PF22)
—S— ：CPEVS 0.9-1P+VVF2.0-3C(PF28)
3. 全ての照明器具とのマッチング試験を行うこと。

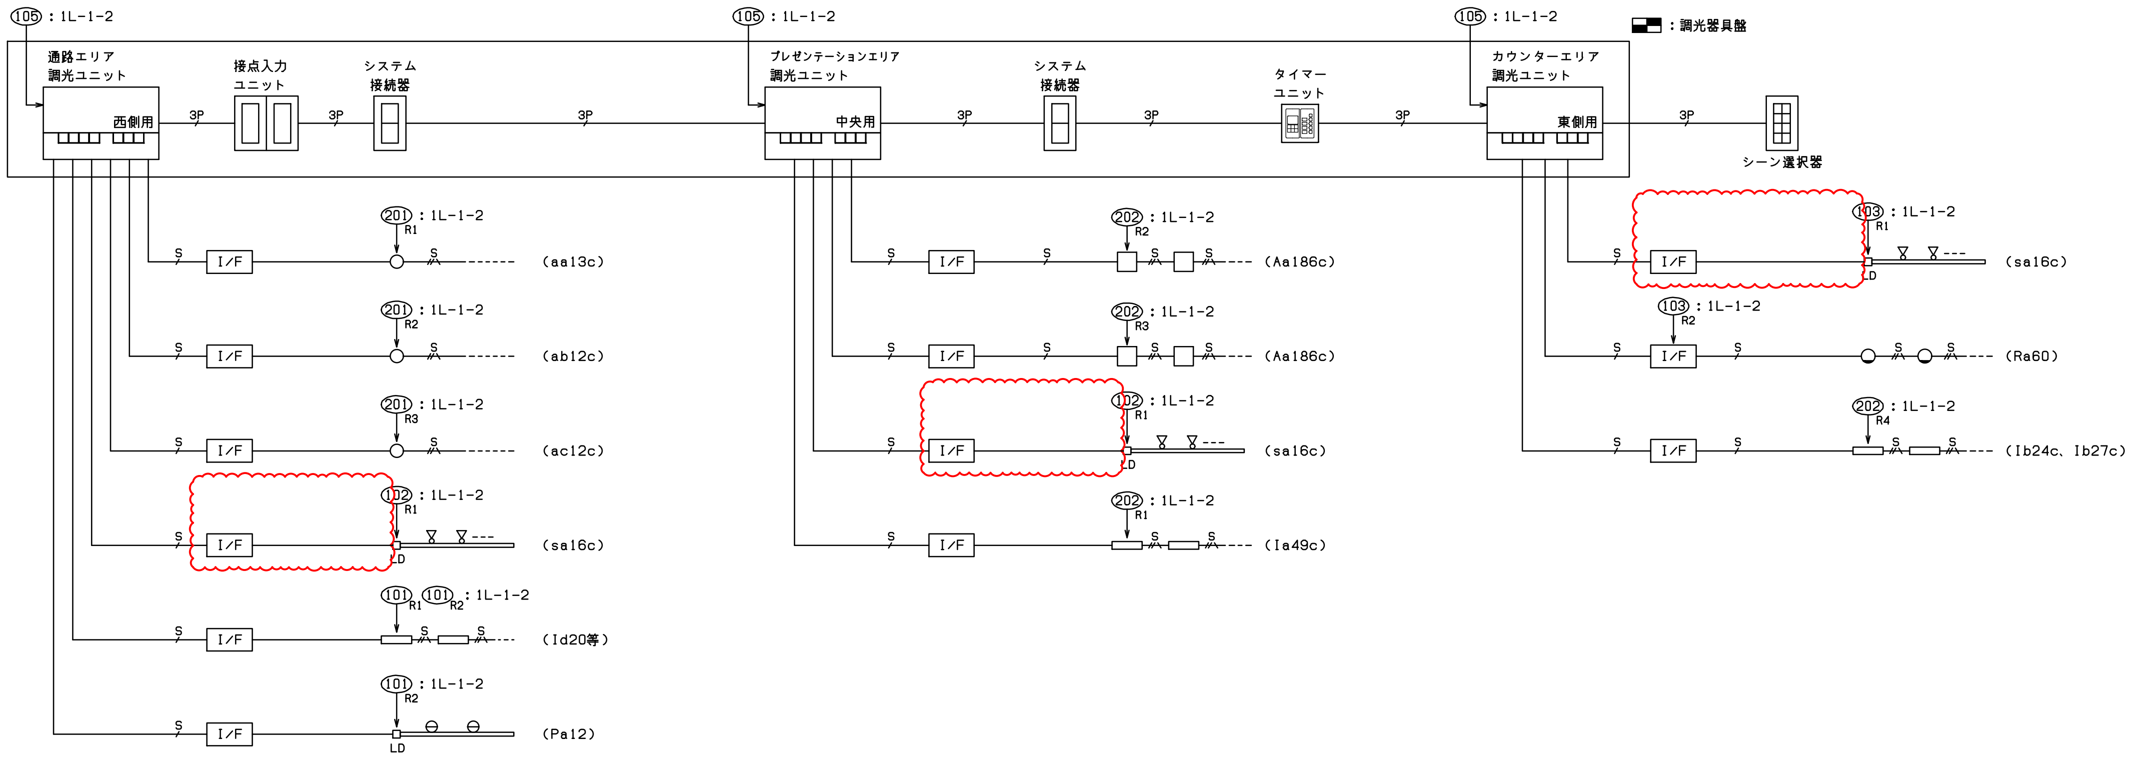
105 : 1L-1-2
通路エリア調光ユニット
西側用
接点入力ユニット
システム接続器
3P
105 : 1L-1-2
プレゼンテーションエリア調光ユニット
中央用
システム接続器
タイマーユニット
105 : 1L-1-2
カウンターエリア調光ユニット
東側用
シーン選択器
▨ : 調光器具盤
S
I/F
201 : 1L-1-2
R1
R2
R3
(aa13c)
(ab12c)
(ac12c)
102 : 1L-1-2
LD
(sa16c)
101 R1 101 R2 : 1L-1-2
(Id20等)
101 : 1L-1-2
(Pa12)
202 : 1L-1-2
(Aa186c)
(Ia49c)
103 : 1L-1-2
(Ra60)
202 : 1L-1-2
R4
(Ib24c、Ib27c)

2　機器姿図　—

調光ユニット

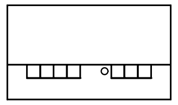

パナソニック　NQ28841K相当品

定格電圧	AC100V
調光回路数	4回路
操作シーン数	4シーン＋OFF
適合スイッチボックス	JIS 4コ用金属製（カバー付）

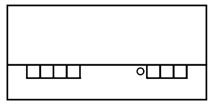

パナソニック　NQ28861K相当品

定格電圧	AC100V
調光回路数	6回路
操作シーン数	4シーン＋OFF
適合スイッチボックス	JIS 5コ用金属製（カバー付）

シーン選択器

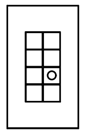

パナソニック　NK28814相当品

操作シーン数	4シーン（1～4または5～8）＋ON／OFF
適合スイッチボックス	JIS 1コ用（カバー付）

接点入力ユニット

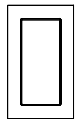

パナソニック　NK28892相当品

機能	外部接点入力によりシーン切替
適合スイッチボックス	JIS 1コ用（カバー付）

タイマーユニット

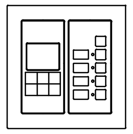

パナソニック　NK28891相当品

設定数	3スケジュール＋自動再生1、7日間スケジュール
適合スイッチボックス	JIS 2コ用（カバー付）

システム接続器

 

パナソニック　NK28800相当品

機能	親器同士のシーン再生・全消灯（子器操作含む）の連動・非連動を設定
適合スイッチボックス	JIS 1コ用（カバー付）

着工	. .	. .
竣工	. .	. .
監理		. . . .
施工		. . . .

惠本　涼太郎　一級建築士
澤村　晋次　意見を聴いた建築設備士

日建設計

椙山女学園／星が丘キャンパス
大学会館食堂リニューアル工事

電 －11

2026・03・27
検図者：横井　繁明

照明制御設備 システム概要、機器仕様、機器姿図、系統図(改修図)

J－ 241226 － A

J241226A26080311_照明制御設備 システム概要、機器仕様、機器姿図、系統図(改修図)

1　1階平面図（既設図）

A1:1/100
A3:1/200

注）1. ▭ は改修範囲外を示す。　注）2. ×、▨ は撤去を示す。

記号	名　称	備 考
◢	電灯分電盤	
▭	天井付照明器具（蛍光灯、LED）	
⊗	避難口誘導灯	
⊗	通路誘導灯	
○	ブラケットライト（LED）	

注記）

1. 特記なき配管配線は下記とする。

	隠ぺい	露出	屋外
―― VVF1.6-3C	(PF16)	(E19)	(G16)

改修内容

① 照明、誘導灯および配管配線を撤去する。

食堂			
Ca	108	Lc	1
Cb	12	Lg	2
Ea	46	Xc2E	2
Ka	4		

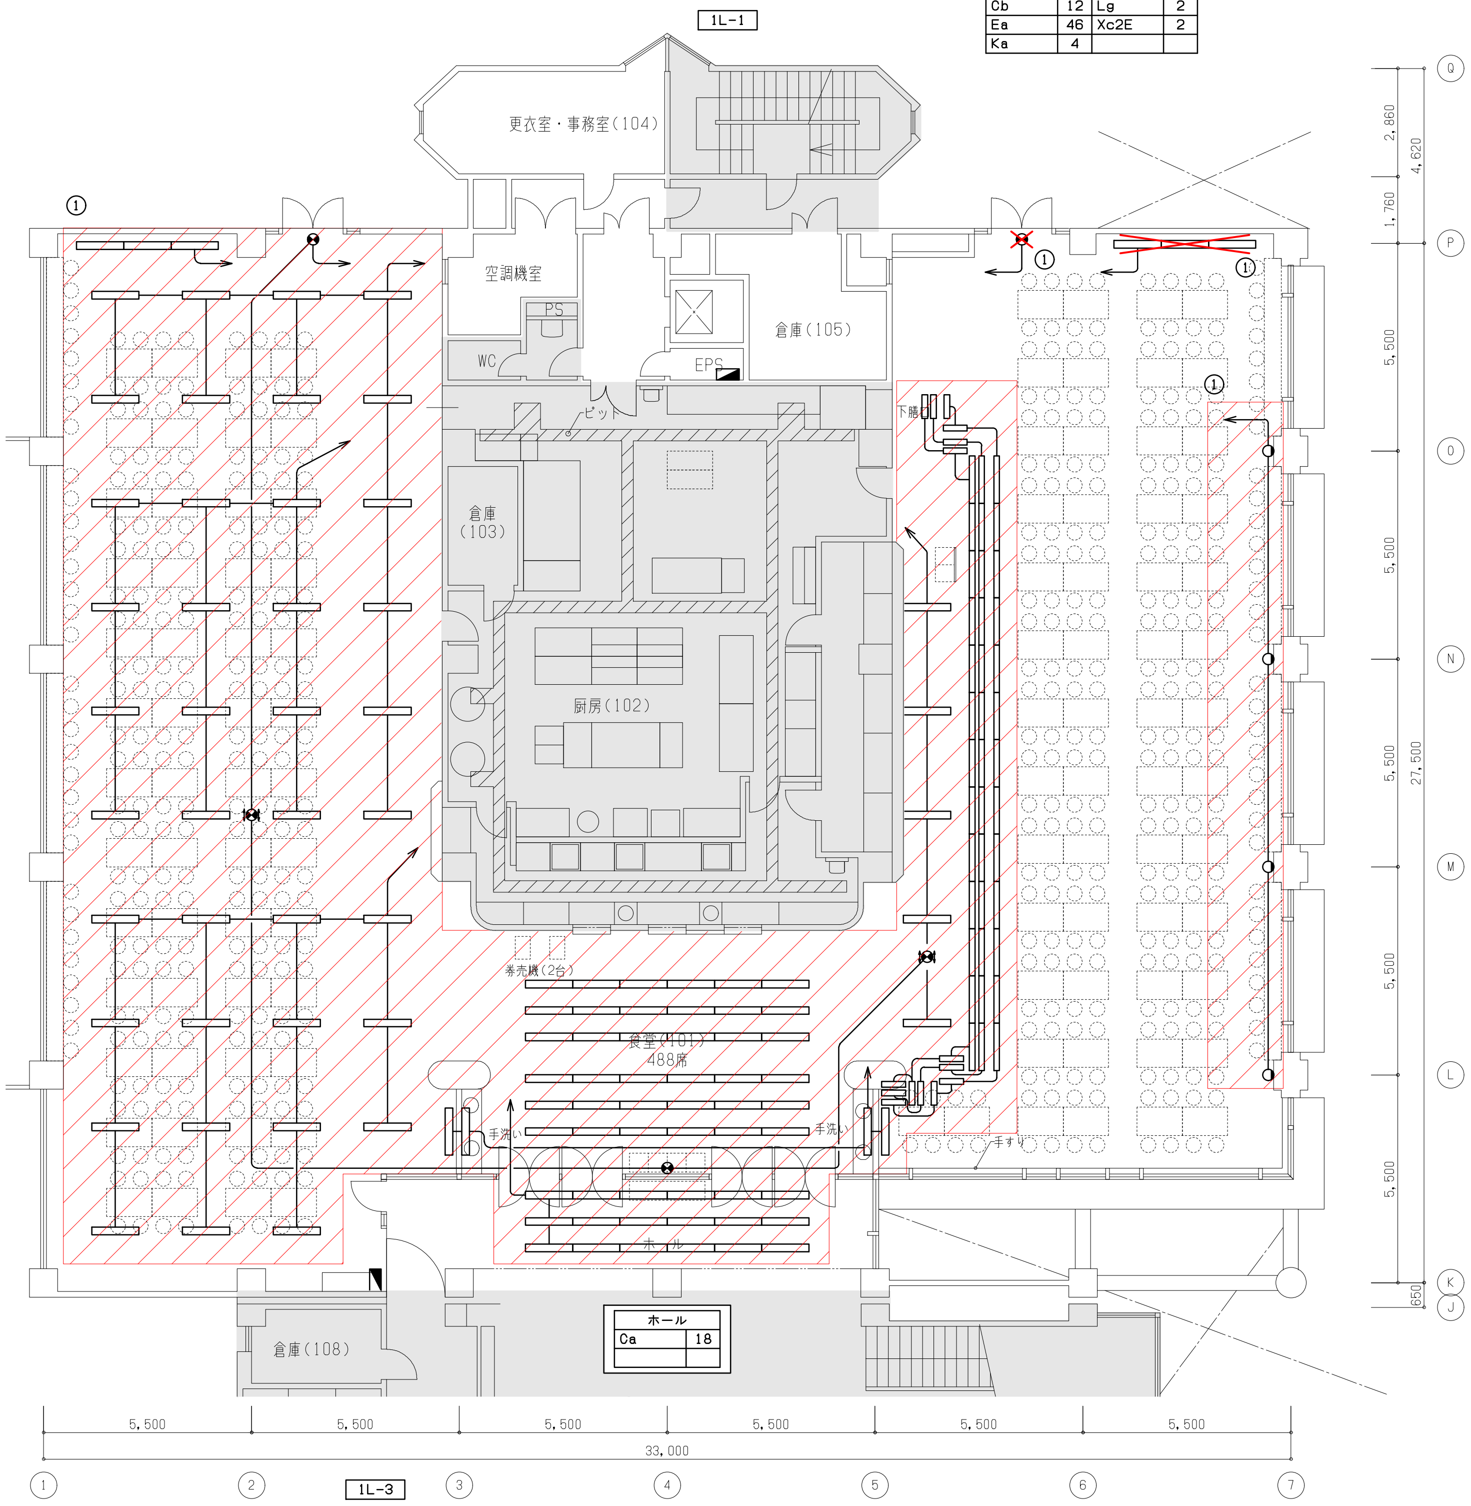
1L-1
更衣室・事務室(104)
①
空調機室
PS
WC
EPS
倉庫(105)
ピット
下膳
倉庫(103)
厨房(102)
券売機(2台)
食堂(101)
488席
手洗い
ホール
倉庫(108)
2,860
4,620
1,760
5,500
27,500
650
Q
P
O
N
M
L
K
J
5,500
33,000
1L-3
1
2
3
4
5
6
7

ホール	
Ca	18

2　1階平面図（改修）

A1:1/100
A3:1/200

注）1. ▭ は改修範囲外を示す。 2. 破線は既設を示す。

記号	名　称	備 考
◢	電灯分電盤	
▦	調光器盤	
▭	LED間接照明	
▽	LEDスポットライト	
□	LEDスクエア照明	
○75	LEDダウンライト（75φ）	
○100	LEDダウンライト（100φ）	
○125	LEDダウンライト（125φ）	
⊖	LEDペンダントライト	
□LD	ライティングダクト	
⊗nL	リモコンスイッチ	nは窓数
⊗S	シーン操作スイッチ	調光設備図参照
ⓢP	無線調光リモコン	
⊗	避難口誘導灯	

注記）

1. 特記なき配管配線は下記とする。

	隠ぺい	露出	屋外
―― VVF1.6-3C	(PF16)	(E19)	(G16)
―S― CPEV1.2-1P	(PF16)	(E19)	(G16)
―S― VVF2.0-3C+CPEV1.2-1P	(PF22)	(E25)	(G22)
―3P― CPEV1.2-3P	(PF22)	(E25)	(G22)

2. ⊘は既設躯体のコア抜きを示す。
⊗は既設躯体のコア抜きの上、防火区画貫通処理を行う。
コア抜きはX線撮影の上、監理者に承諾を得て行うこと。

改修内容

① 照明、誘導灯および配管配線を新設する。
② 調光リモコンを新設する。

食堂（南）			
Aa186c	12	Ia49c	5
Ib27c	1	sa14	29
Ib24c	1	Xb2E	1

食堂（西）			
aa13c	36	Id17	3
ab12c	36	Id8	1
ac12c	31	Id5	1
Id20	14	Xb2E	1
Id18	1	Pa12	9

食堂（東）	
sa14	30
Ra60	5
Xb2E	2

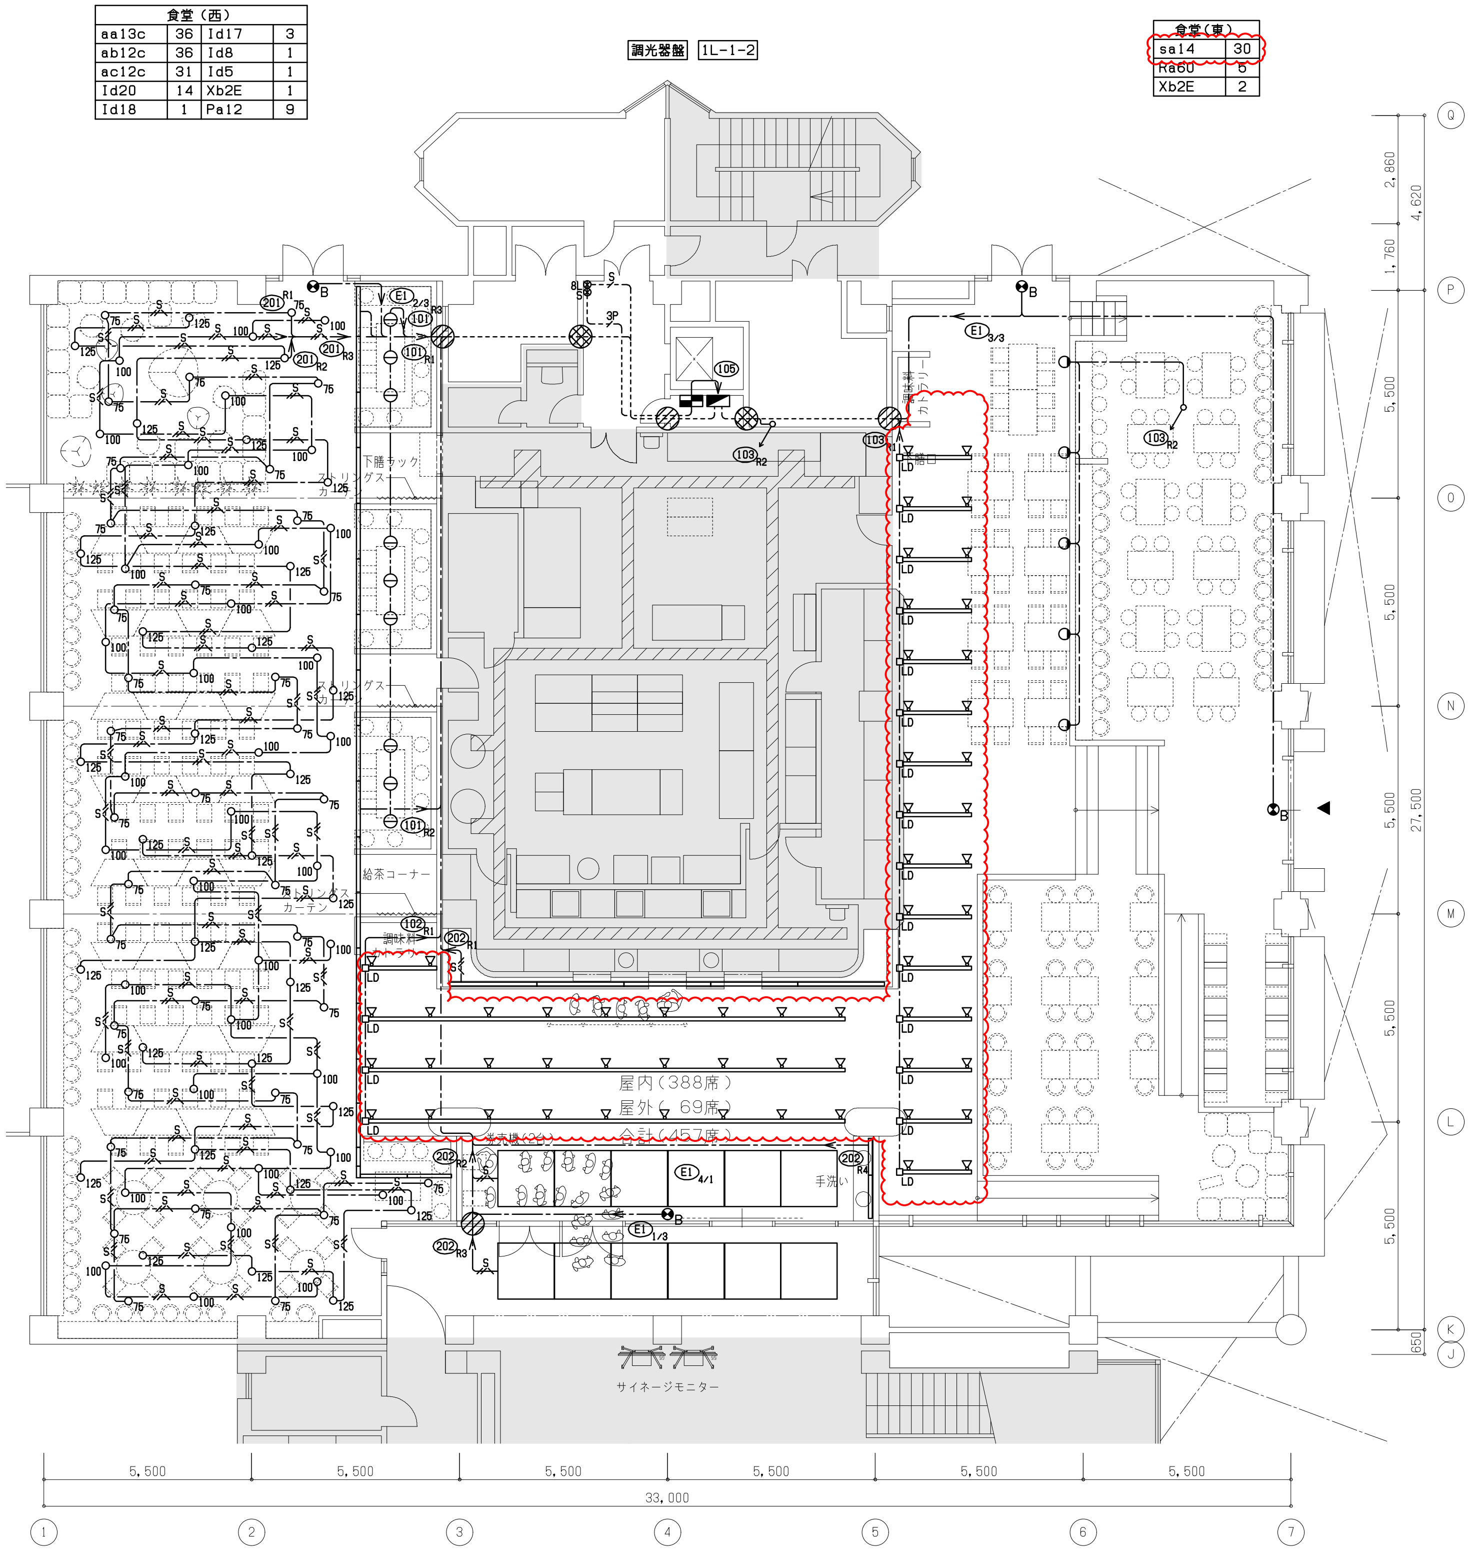
調光器盤
1L-1-2
下膳ラック
リサイクル
給茶コーナー
調味料
屋内(388席)
屋外(69席)
合計(457席)
手洗い
サイネージモニター
E1 2/3
E1 3/3
E1 4/1
E1 1/3
B
LD
75
100
125
101
102
103
105
201
202
2,860
4,620
1,760
5,500
27,500
650
Q
P
O
N
M
L
K
J
5,500
33,000
1
2
3
4
5
6
7

J241226A26080312_照明、誘導灯設備 凡例、1階平面図（既設図）（改修図）

着工	. .	. .	
竣工	. .	. .	
監理		. . . .	
施工		. .	

惠本　涼太郎　一級建築士
澤村　晋次　　意見を聴いた建築設備士

日建設計

2026・03・27　　検図者：横井　繁明

椙山女学園／星が丘キャンパス
大学会館食堂リニューアル工事

照明、誘導灯設備 凡例、1階平面図(既設図)(改修図)

電　－12

No. J － 241226 － A

1 BGM放送設備 システムブロック図（既設図） — 注）1．×、▨は撤去を示す。

注記）
1．特記なき配管配線は下記とする。
5P OP1．2-5P(25)
OP1．2-2C(16)

凡例）
⊟：端子盤（1T-1）
▣：配線接続アウトレット
BGMスピーカ

改修内容
- BGMスピーカ、配線接続アウトレット（ノズルプレート）および配管配線を撤去する。
- 1T-1は配線撤去のうえ、残置とする。

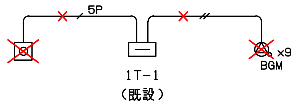
5P
1T-1
（既設）
x9
BGM

2 非常放送設備系統図（既設図） — 注）1．×、▨は撤去を示す。

改修内容
- 非常放送スピーカ、カットリレーを撤去する。
（カットリレー用の配線は残置）

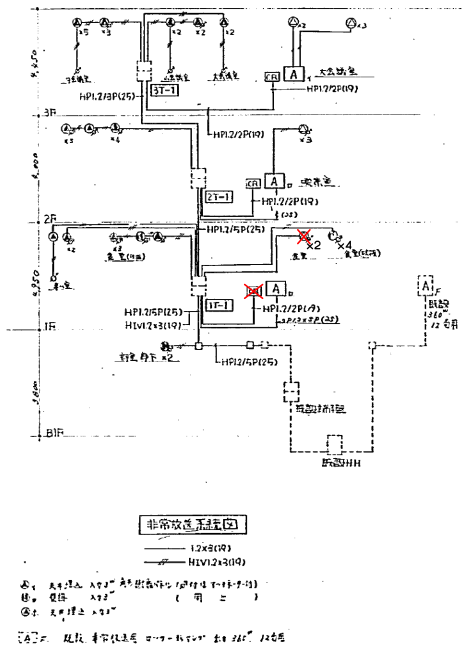
3F
2F
1F
B1F
1T-1
2T-1
3T-1
A
非常放送系統図

3 BGM放送設備 システムブロック図（改修図） — （新設）

注記）
1．特記なき配管配線は下記とする。

		隠ぺい	露出	屋外
	AE1．2-2C	（PF16）	（E19）	（G16）

凡例）
Ⓒ：電源カットリレー
▣：配線接続アウトレット（ノズルプレート）

改修内容
- 図示のBGM放送設備を新設する。

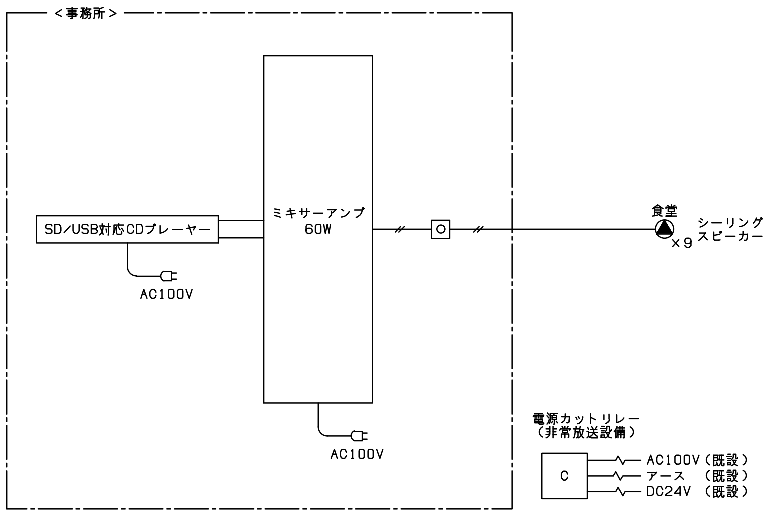
＜事務所＞
SD/USB対応CDプレーヤー
ミキサーアンプ
60W
AC100V
AC100V
食堂
×9
シーリング
スピーカー
電源カットリレー
（非常放送設備）
C
AC100V（既設）
アース（既設）
DC24V（既設）

4 非常放送設備系統図（改修図） —

改修内容
① カットリレーを新設する。（既設配線再接続）
② 非常放送スピーカを新設する。
③ 非常放送アンプの設定変更、調整を行う。

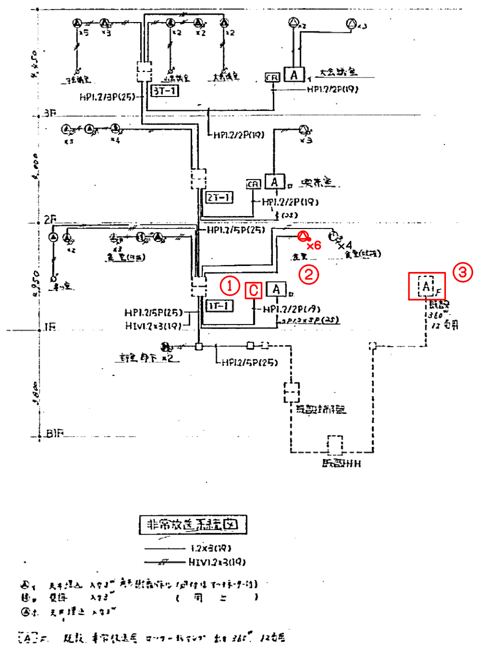
①
②
③
x6
3F
2F
1F
B1F
1T-1
2T-1
3T-1
A
C
非常放送系統図

5 機器姿図（改修図） — 更新機器

BGM BGMワゴン

No.	名称
1	木製ラック
2	ミキサーアンプ
3	SD/USB対応CDプレーヤー
4	主電源パネル

電 源	AC100V 50/60Hz
木製ラック	表面コート紙 黒
	ガラス扉透明強化ガラス（鍵付）、270°開閉
ミキサーアンプ	定格出力60W
	入力4（入力1、2は切換式）
SD/USB対応CDプレーヤー	対応メディアCD、CD-R、CD-RW
	USBメモリー、SDカード、SDHCカード
	Bluetooth付

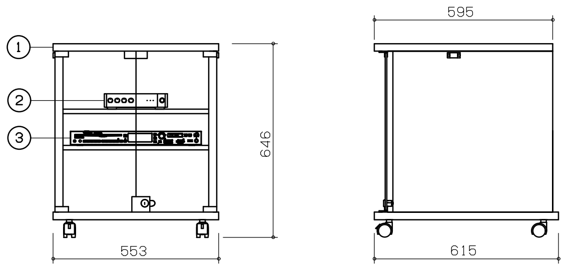
①
②
③
646
553
595
615

シーリングスピーカー

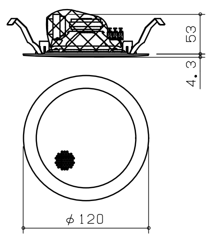

天井埋込型スピーカー ATT付

L級

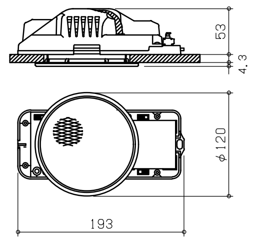
53
4.3
φ120
193

定格入力	6W（1．7kΩ）、3W（3．3kΩ）、 1．5W（6．7kΩ）、0．8W（13kΩ）、 6W（8Ω）
出力音圧レベル	93dB（1W、1m）
周波数特性	45Hz～20kHz（ピーク-20dB時）
スピーカー	8cmダブルコーン型
仕上	枠、ネット鋼板オフホワイト

定格入力	3W（3．3kΩ）、1W（10kΩ）
出力音圧レベル	95dB（1W、1m）
周波数特性	90Hz～15kHz
スピーカー	8cmコーン型
仕上	ネットアルミ
その他	防塵カバー一体型
	音量調節5段切換

C 電源カットリレー

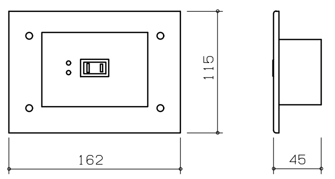

材質：新金属製

電源	AC100V50/60Hz
電力容量	最大800W
電流容量	最大10A
制御方式	制御電源によりAC100 V断制御
制御電流	DC24 V 0．3 mA
仕上	パネル：アルミ
適合ボックス	埋込：JIS 3個用スイッチボックスカバー付

着工	． ．	． ．
竣工	． ．	． ．
監理		． ．
		． ．
施工		． ．
		． ．

惠本 涼太郎 一級建築士
澤村 晋次 意見を聴いた建築設備士

日建設計
2026．03．27 検図者：横井 繁明

椙山女学園／星が丘キャンパス
大学会館食堂リニューアル工事
業務用兼用非常放送設備 システム図、機器姿図、系統図（既設図）（改修図）

㊂ －13
J－ 241226 － A

J241226A26030913_業務用兼用非常放送設備 システム図、機器姿図、系統図（既設図）（改修図）

1	1階平面図（既設図）	A1:1/100 A3:1/200	注）1. ▭ は改修範囲外を示す。　注）2. ×、▨ は撤去を示す。

記号	名　称	備　考
⊟	端子盤	
△	非常放送スピーカ	
△BGM	BGM用スピーカ	
Ⓒ	カットリレー	
⊡	配線接続アウトレット	
◐	壁付LANアウトレット	
□AP	無線アクセスポイント	

注記）

1. 特記なき配管配線は下記とする。

5P	OP1.2-5P　(25)
//	OP1.2-2C　(16)
///	OP1.2-3C　(16)
UTP	UTP0.5-4P (16)

改修内容

① 非常放送、スピーカ、BGMスピーカおよび配管配線を撤去する。
② LANアウトレット、WIFIアクセスポイントを撤去する。
③ カットリレー、配線接続アウトレットを撤去する。

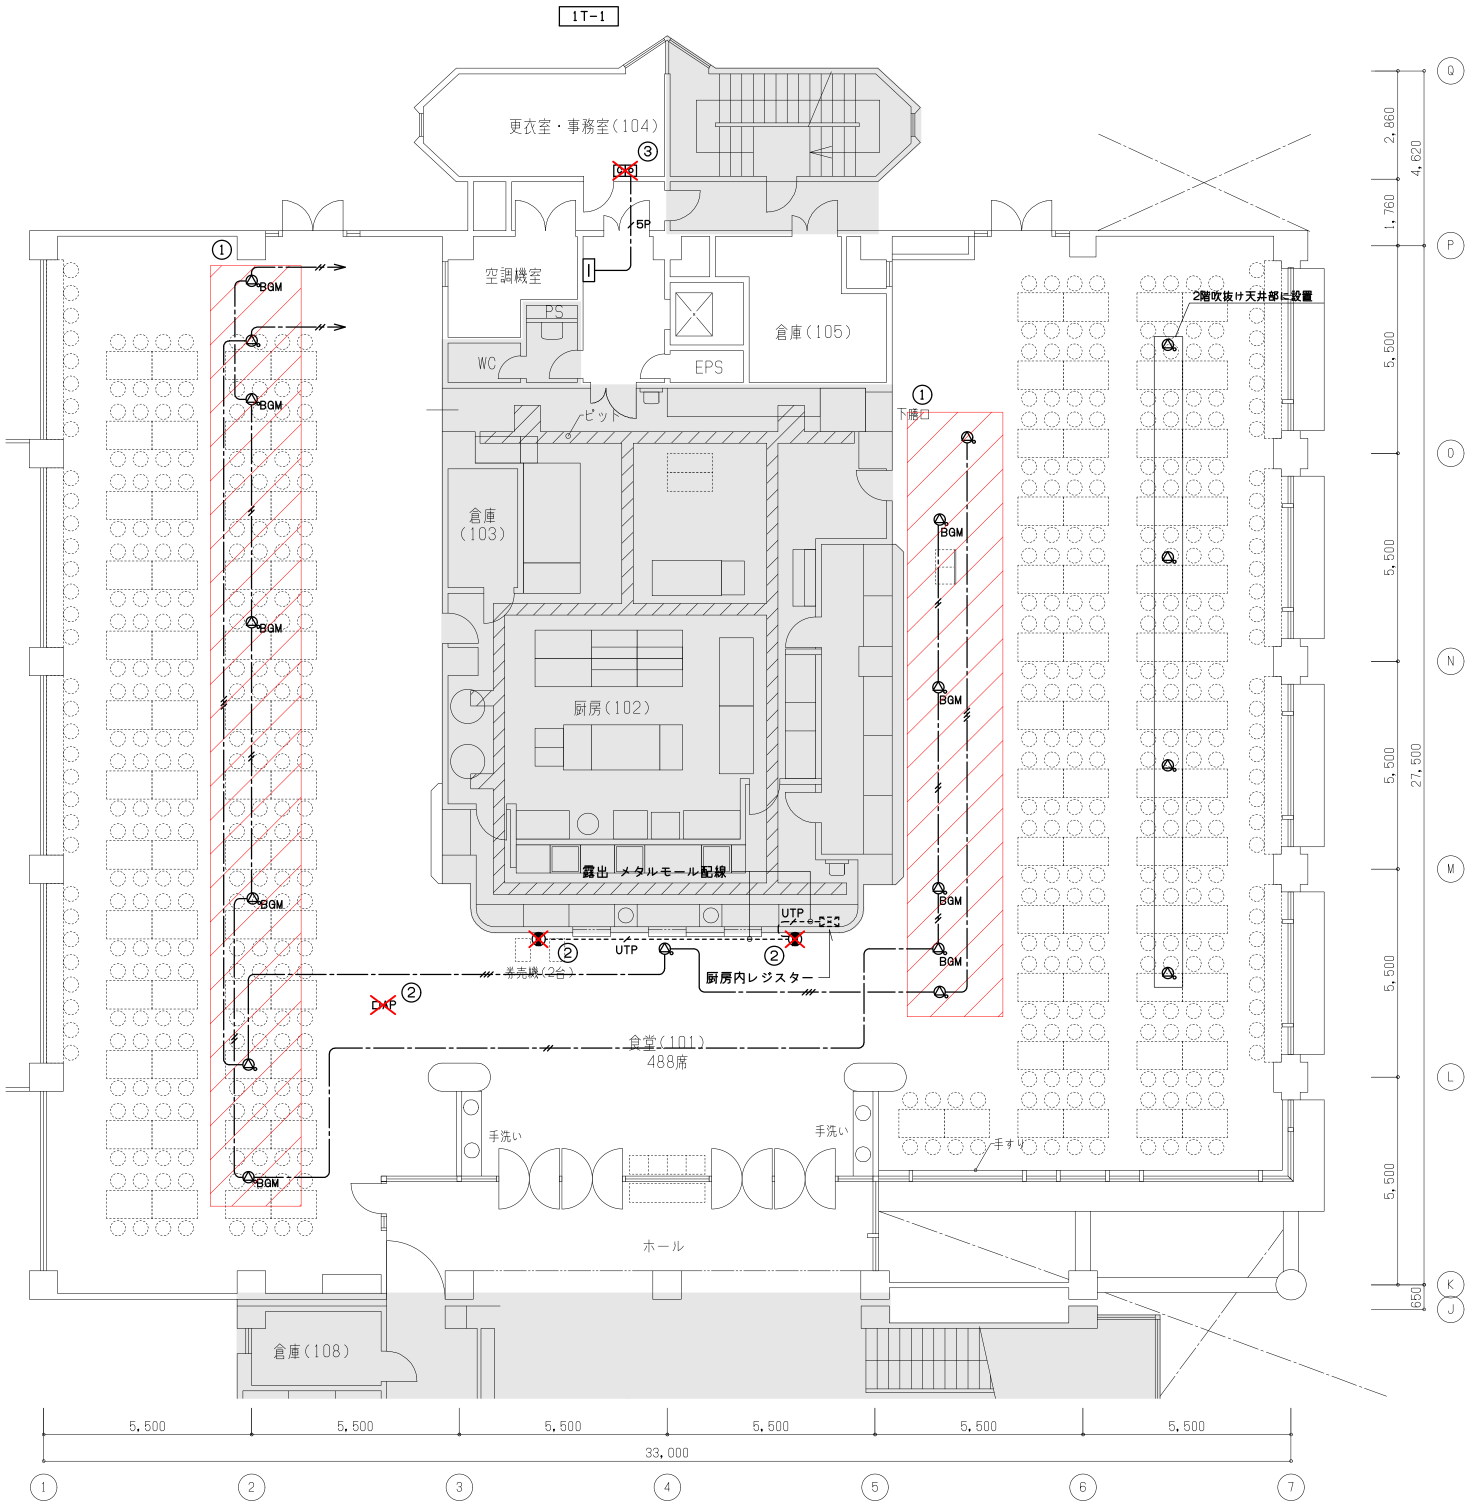
1T-1
更衣室・事務室(104)
③
5P
空調機室
PS
WC
EPS
倉庫(105)
ピット
①
下膳口
2階吹抜け天井部に設置
BGM
倉庫(103)
厨房(102)
露出　メタルモール配線
UTP
②
券売機(2台)
厨房内レジスター
AP
食堂(101)
488席
手洗い
手すり
ホール
倉庫(108)
2,860
4,620
1,760
5,500
27,500
650
5,500
33,000
Q
P
O
N
M
L
K
J
1
2
3
4
5
6
7

2	1階平面図（改修）	A1:1/100 A3:1/200	注）1. ▭ は改修範囲外を示す。 2. 破線は既設を示す。

記号	名　称	備　考
⊟	端子盤	
△	非常放送スピーカ	
▲	BGM用スピーカ	
Ⓒ	カットリレー	
⊡	配線接続アウトレット	
◐	壁付LANアウトレット	
□AP	無線アクセスポイント	
BGM	BGMワゴン	

注記）

1. 特記なき配管配線は下記とする。

		隠ぺい	露出	屋外
3C	HP1.2-3C	(PF16)	(E19)	(G22)
//	AE1.2-2C	(PF16)	(E19)	(G16)
—o—	空配管	(PF22)	(E19)	(G22)

2. ▨ は既設駆体のコア抜きを示す。
⊗ は既設駆体のコア抜きの上、防火区画貫通処理を行う。
コア抜きはX線撮影の上、監理者に承諾を得て行うこと。

改修内容

① 非常放送、スピーカ、BGMスピーカおよび配管配線を新設する。
② BGMアンプ、カットリレー、配線接続アウトレットを新設する。

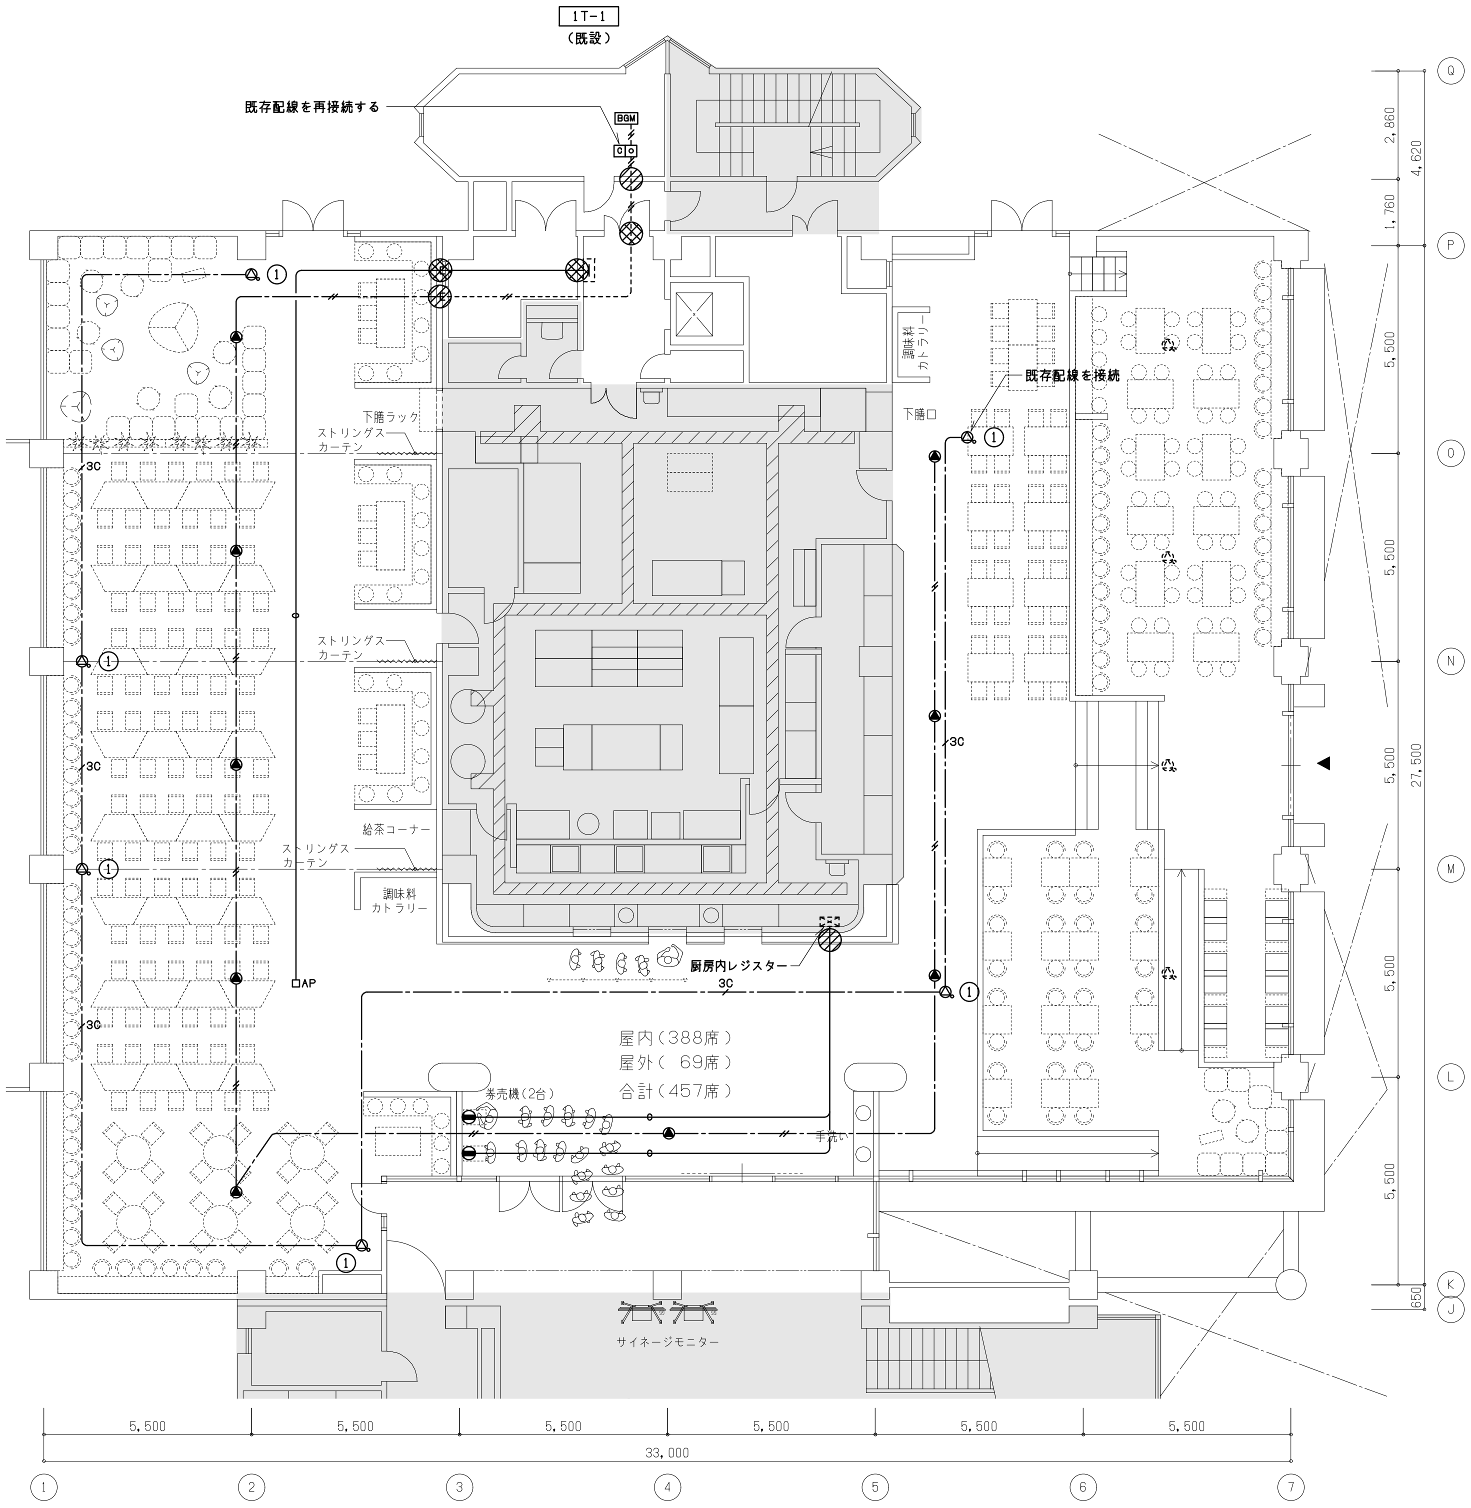
1T-1
(既設)
既存配線を再接続する
BGM
C
①
下膳ラック
ストリングスカーテン
3C
調味料カトラリー
既存配線を接続
下膳口
給茶コーナー
AP
厨房内レジスター
屋内(388席)
屋外(69席)
合計(457席)
券売機(2台)
手洗い
サイネージモニター
2,860
4,620
1,760
5,500
27,500
650
5,500
33,000
Q
P
O
N
M
L
K
J
1
2
3
4
5
6
7

J241226A26031714_業務用兼用非常放送設備　凡例、1階平面図（既設図）（改修図）

着工	. .	. .	
竣工	. .	. .	
監理		. .	
施工		. .	

惠本　涼太郎　一級建築士
澤村　晋次　　意見を聴いた建築設備士

日建設計

2026・03・27

検図者：横井　繁明

桐山女学園／星が丘キャンパス
大学会館食堂リニューアル工事

業務用兼用非常放送設備 凡例、1階平面図(既設図)(改修図)

㊫

－14

No. J－ 241226 － A

1	自動火災報知設備 系統図（既設図）	―	注）1．×、▨ は撤去を示す。

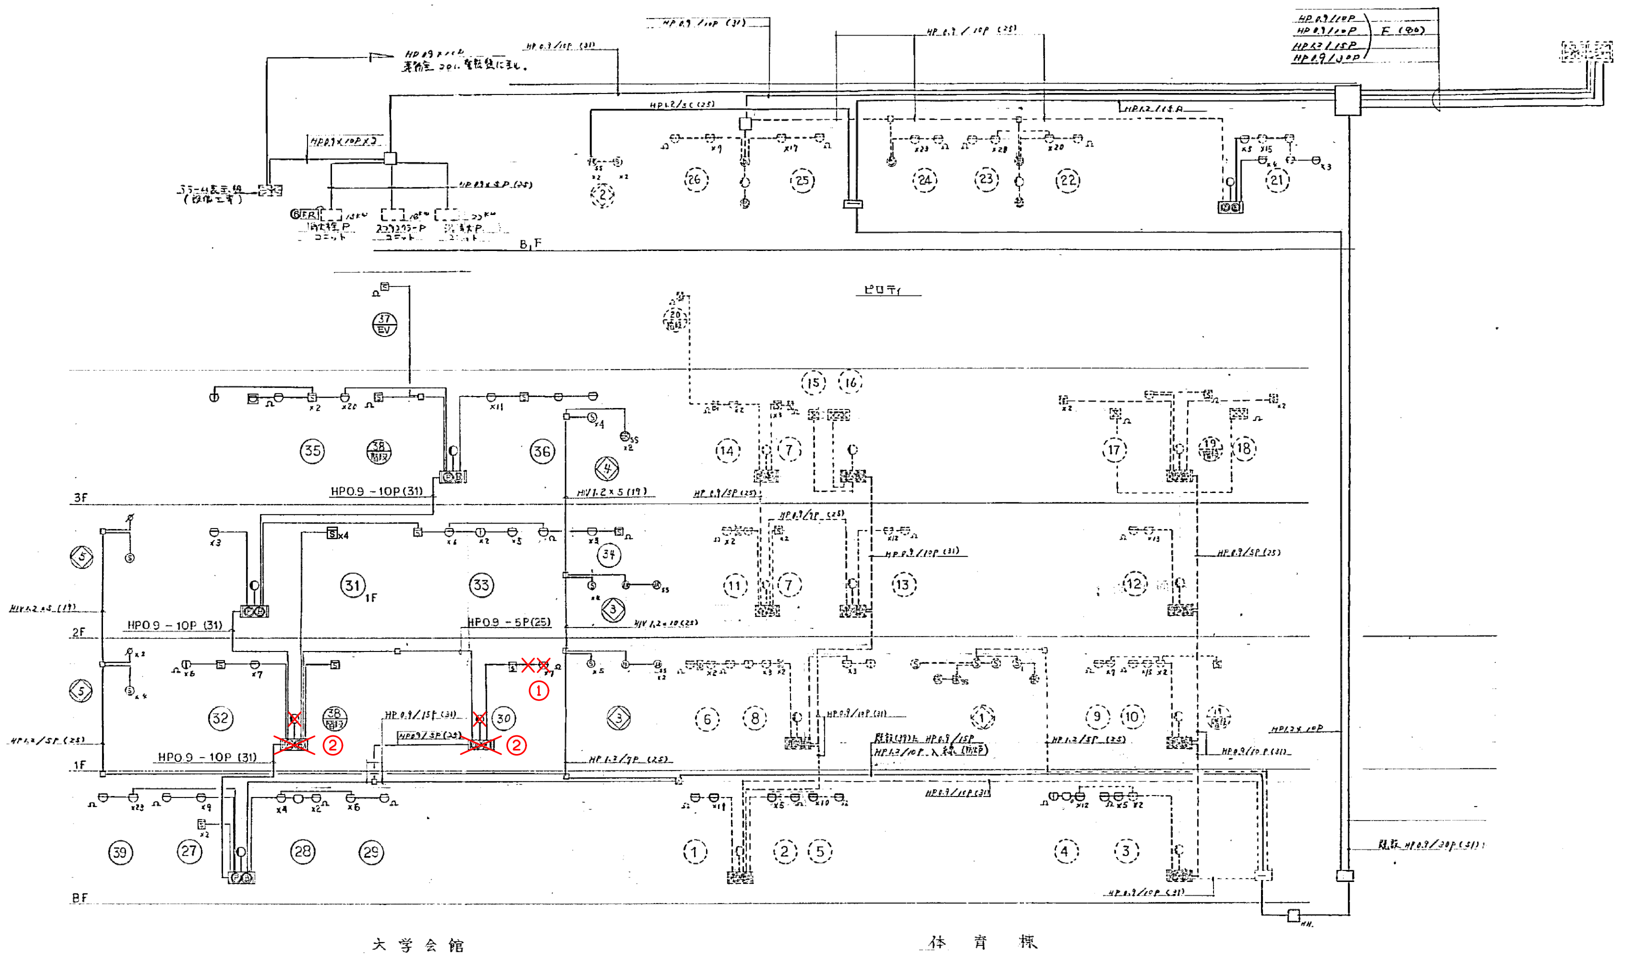
B1F
ピロティ
3F
2F
1F
BF
HP09－10P（31）
HP09－5P（25）
①
②
②
大学会館
体育棟

改修内容

① 発信器、ベル、表示灯を撤去する。（配線残置）
② 感知器を撤去する。

2	自動火災報知設備 系統図（改修図）	―

記号	名　称	備　考
[S]	光電式スポット型感知器	
Ⓟ	発信器	
Ⓑ	地区音響ベル	
◒	表示灯	
⌀SFD	防火防煙ダンパ	
[AC]	空調機	

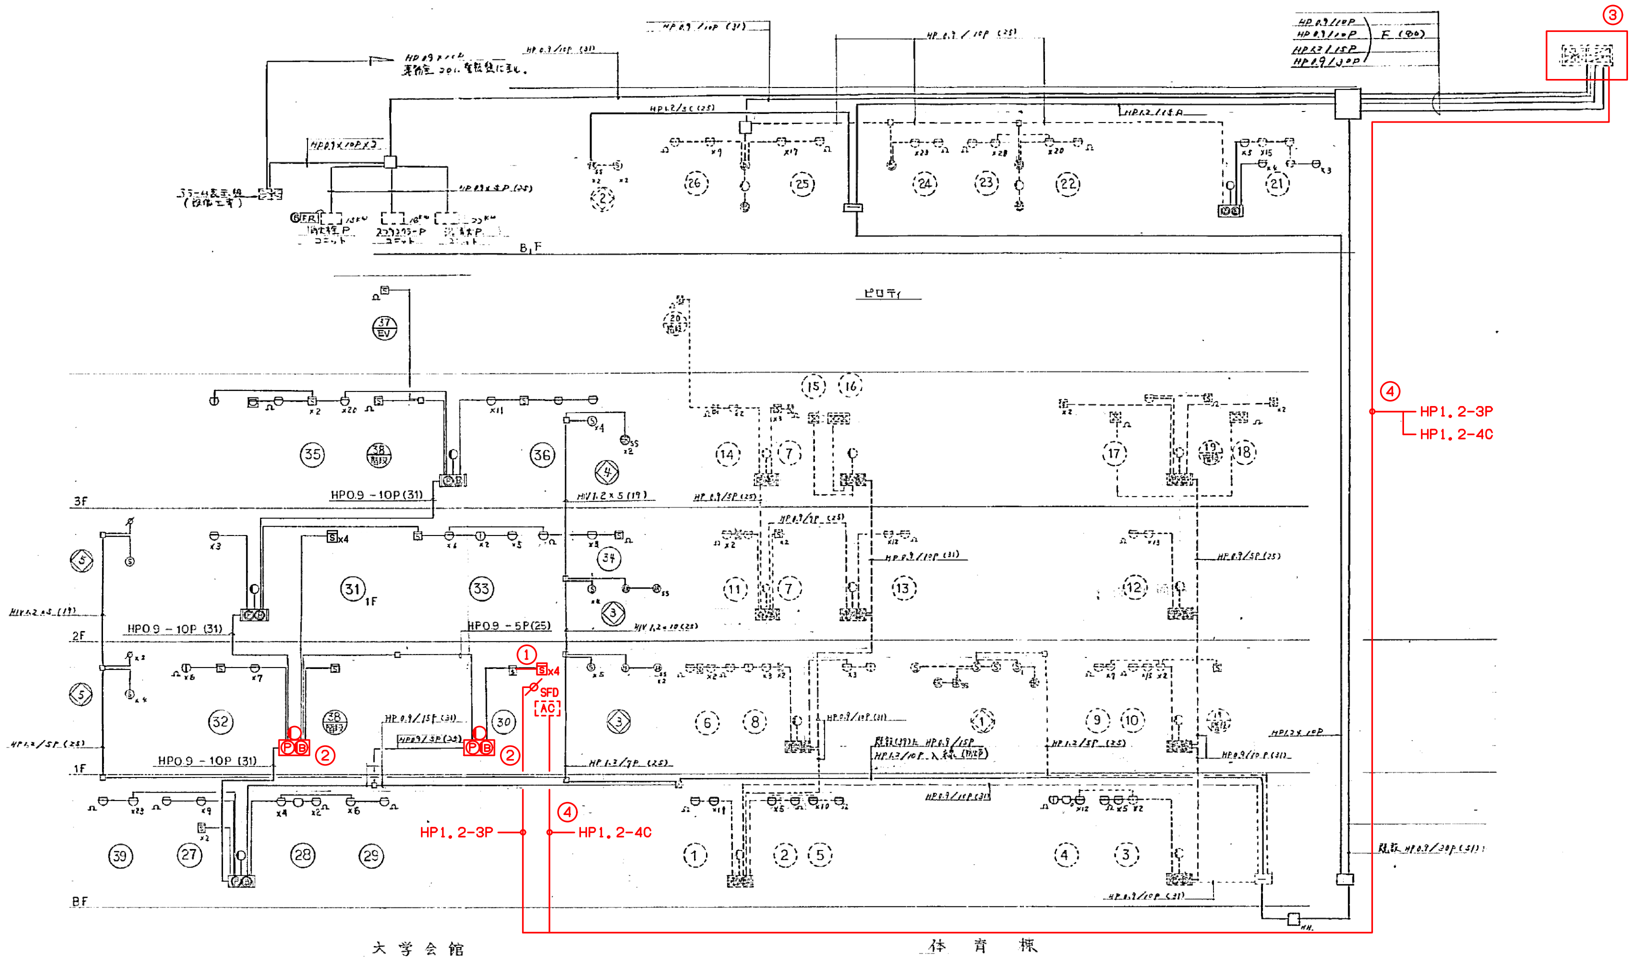
③
④
HP1.2－3P
HP1.2－4C
B1F
ピロティ
3F
2F
1F
BF
HP09－10P（31）
HP09－5P（25）
①
SFD
AC
②
②
④
HP1.2－3P
HP1.2－4C
大学会館
体育棟

改修内容

① 発信器を新設する。配線は既存感知器へ接続する。
② 発信器、ベル、表示灯を新設する。（配線再接続）
③ 受信機の設定変更、調整を行う。
④ SFD、空調機から受信機まで配管配線を新設する。

着工	・ ・	・ ・	
竣工	・ ・	・ ・	
監理		・ ・ ・ ・	
施工		・ ・	

惠本　涼太郎　一級建築士
澤村　晋次　　意見を聴いた建築設備士

日建設計

2026・03・27
検図者：横井　繁明

椙山女学園／星が丘キャンパス
大学会館食堂リニューアル工事

自動火災報知設備　系統図（既設図）（改修図）

㊂電
－15

No.　J－ 241226 － A

J241226A26080315_自動火災報知設備　系統図（既設図）（改修図）

1	1階平面図(既設図)	A1:1/100 A3:1/200	注)1. ▭ は改修範囲外を示す。　注)2. ×、▨ は撤去を示す。

記号	名　称	備　考
⊖	差動式スポット型感知器	
Ⓢ	光電式スポット型感知器	
Ⓟ	発信器	
Ⓑ	地区音響ベル	
◒	表示灯	

改修内容

① 感知器および配管配線を撤去する。

② 発信器、表示灯、ベルを撤去する。(配線残置)

注記)

1. 特記なき配管配線は下記とする。

—//— IV1.2x2(19)

—////— IV1.2x4(19)

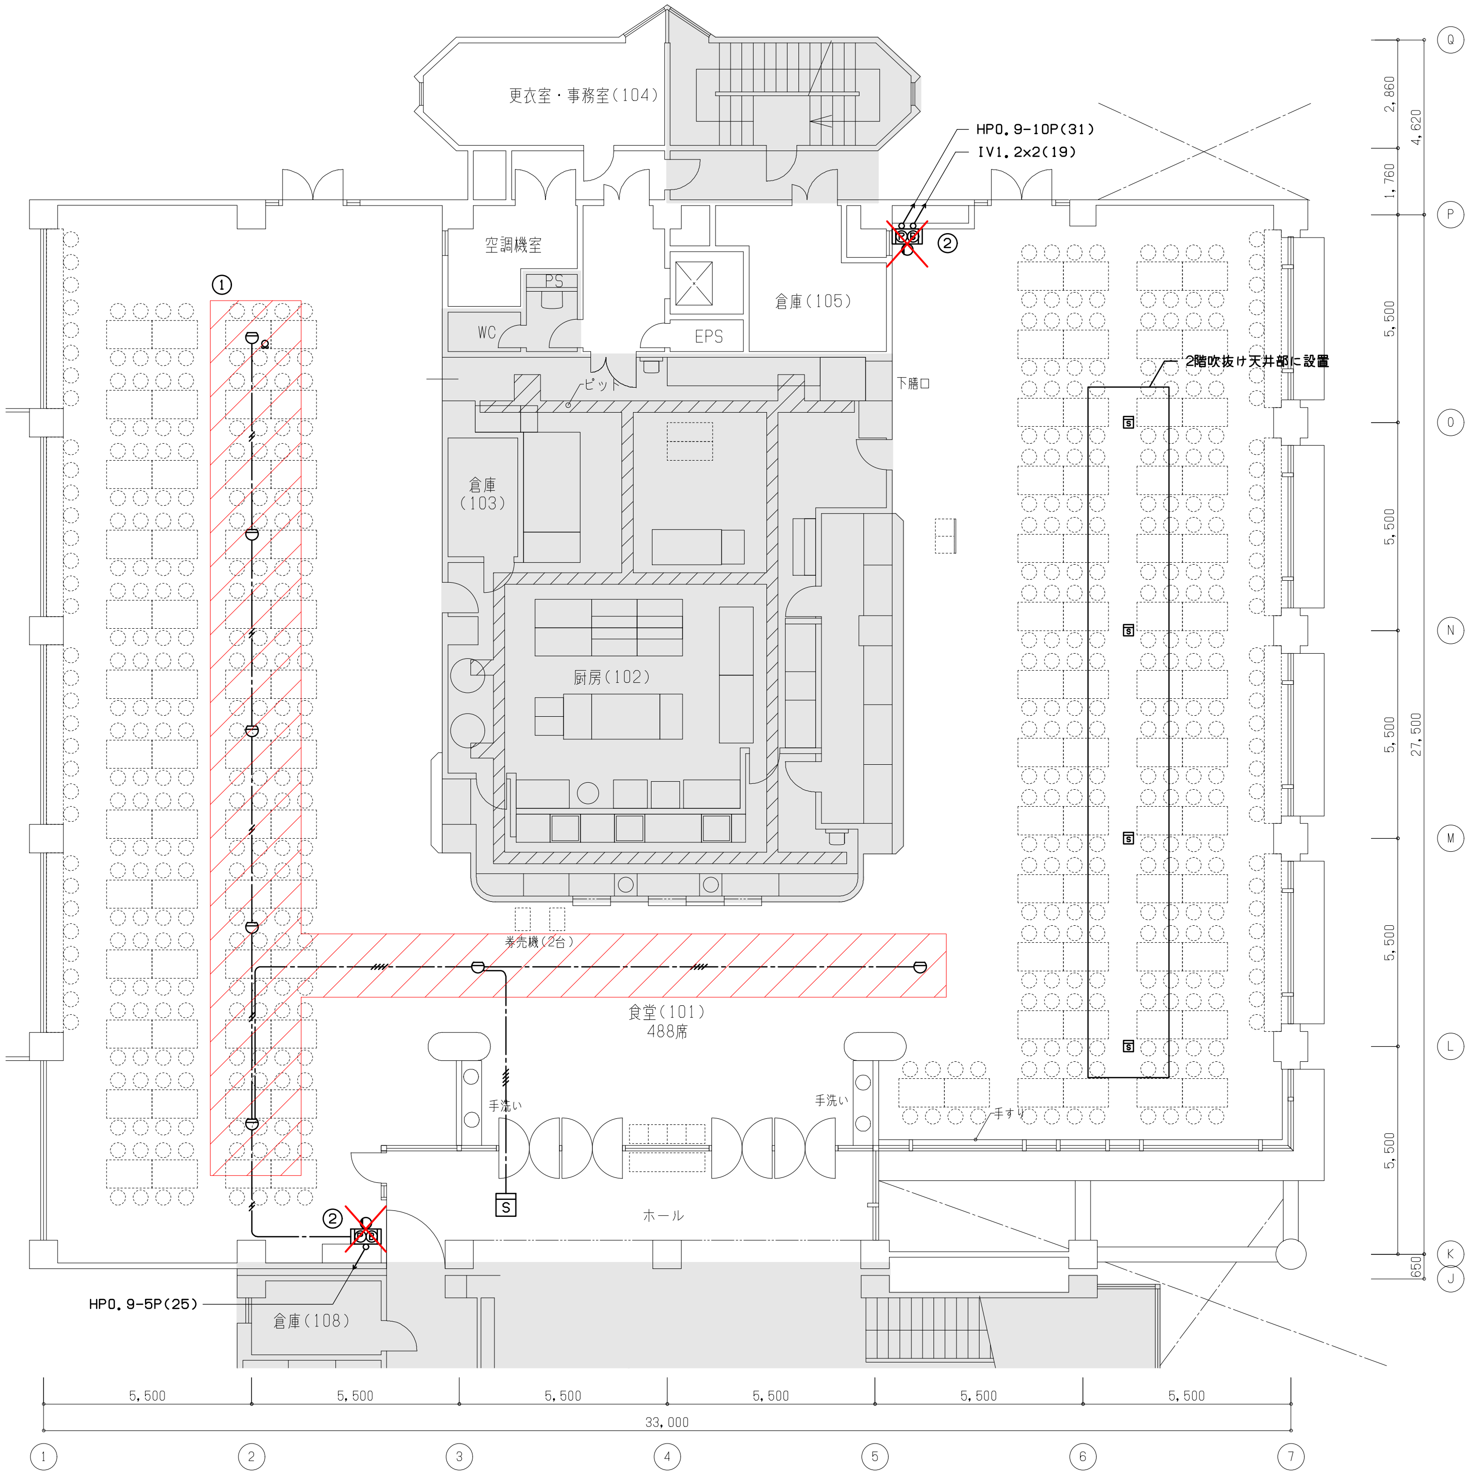

更衣室・事務室(104)
空調機室
PS
WC
EPS
倉庫(105)
ピット
下膳口
倉庫(103)
厨房(102)
HP0.9-10P(31)
IV1.2x2(19)
②
①
2階吹抜け天井部に設置
券売機(2台)
食堂(101)
488席
手洗い
手洗い
手すり
ホール
S
②
HP0.9-5P(25)
倉庫(108)
2,860
4,620
1,760
5,500
5,500
5,500
27,500
5,500
5,500
650
Q
P
O
N
M
L
K
J
5,500
5,500
5,500
5,500
5,500
5,500
33,000
1
2
3
4
5
6
7

2	1階平面図(改修)	A1:1/100 A3:1/200	注)1. ▭ は改修範囲外を示す。 2.破線は既設を示す。

記号	名　称	備　考
Ⓢ	光電式スポット型感知器	2種、小型埋込型
Ⓟ	発信器	
Ⓑ	地区音響ベル	
◒	LED表示灯	

改修内容

① 感知器および配管配線を新設する。

② 発信器、表示灯、ベルを新設する。(配線再接続)

③ 改修に伴い、既設受信機(文学部棟設置)の設定変更、調整等を行う。

④ SFD、空調機から受信機まで配管配線を新設する。

注記)

1. 特記なき配管配線は下記とする。

	隠ぺい	露出	屋外
—//— HP1.2-2C	(PF16)	(E19)	(G22)
—////— HP1.2-4C	(PF16)	(E19)	(G22)

2. 改修工事に際し、事前に所轄消防と協議を行い、改修内容について確認を行うこと。

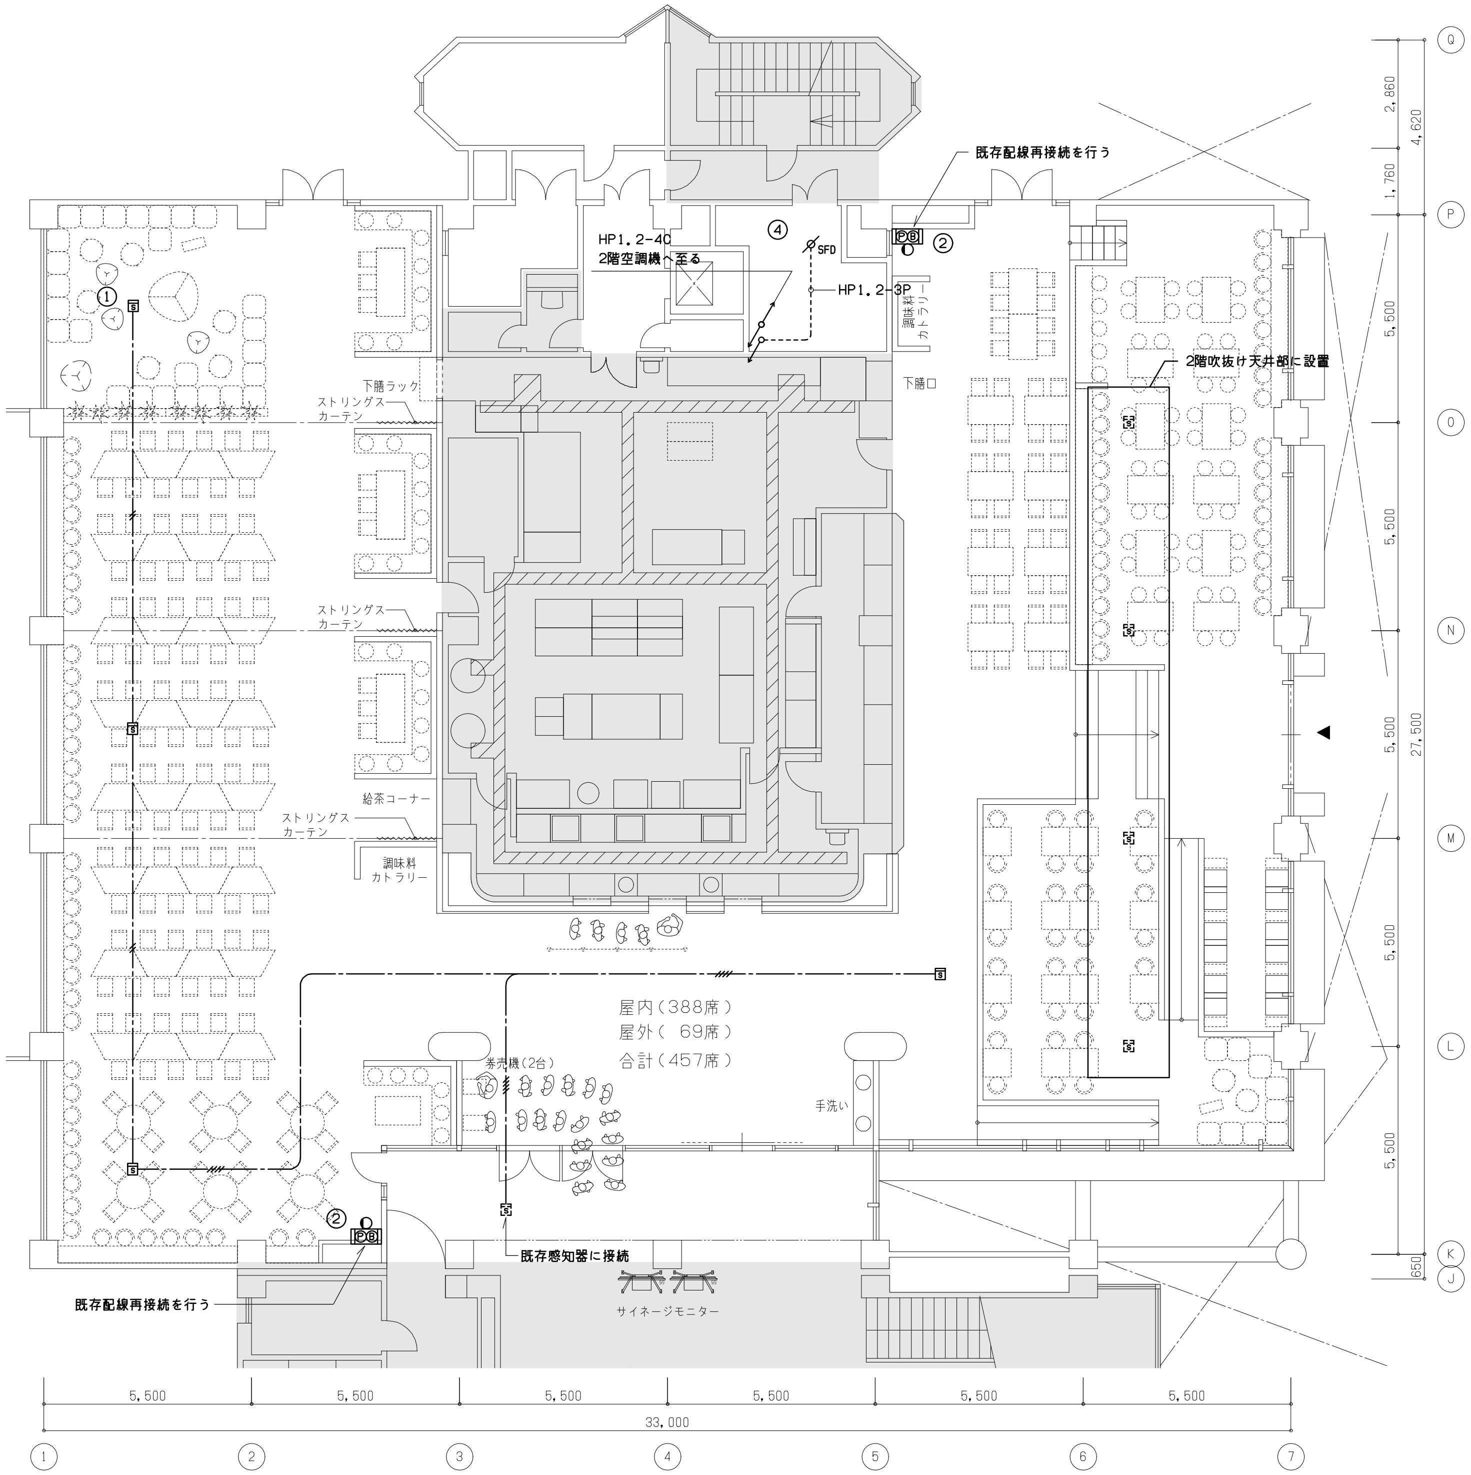

既存配線再接続を行う
HP1.2-4C
2階空調機へ至る
④
SFD
HP1.2-3P
②
調味料
カトラリー
下膳口
①
下膳ラック
ストリングス
カーテン
ストリングス
カーテン
ストリングス
カーテン
給茶コーナー
調味料
カトラリー
2階吹抜け天井部に設置
屋内(388席)
屋外(69席)
合計(457席)
券売機(2台)
手洗い
②
既存感知器に接続
既存配線再接続を行う
サイネージモニター
2,860
4,620
1,760
5,500
5,500
5,500
27,500
5,500
5,500
650
Q
P
O
N
M
L
K
J
5,500
5,500
5,500
5,500
5,500
5,500
33,000
1
2
3
4
5
6
7

J241226A26080316_自動火災報知設備　1階平面図(既設図)(改修図)

着工	. .	. .	
竣工	. .	. .	
監理		. .	
		. .	
施工		. .	

惠本　涼太郎　一級建築士
澤村　晋次　　意見を聴いた建築設備士

日建設計

2026・03・27

検図者：横井　繁明

椙山女学園/星が丘キャンパス
大学会館食堂リニューアル工事

自動火災報知設備　1階平面図(既設図)(改修図)

㊂ －16

No. J－ 241226 － A

1	防火区画貫通処理工法別要領図	―	※下記の要領図は参考図とする。同等の性能を有する別な大臣認定工法・在来工法を採用する場合には、施工要領書にて監理者の承認を得ること。

国土交通大臣認定工法

A　ケーブルラック床貫通部

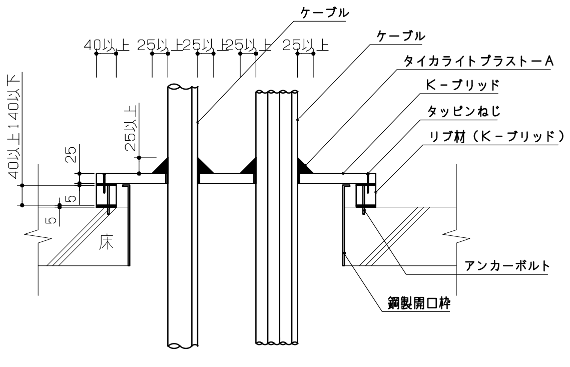
ケーブル
ケーブル
タイカライトプラストーA
Kーブリッド
タッピンねじ
リブ材（Kーブリッド）
40以上 25以上 25以上 25以上 25以上
40以上140以下
25以上
25
5
5
床
アンカーボルト
鋼製開口枠

認定番号：PS060FL-0032

B　ケーブルラック壁貫通部（コンクリート）

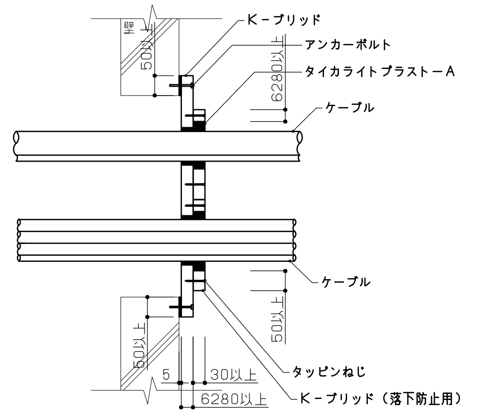
Kーブリッド
アンカーボルト
タイカライトプラストーA
ケーブル
壁
50以上
6280以上
ケーブル
50以上
50以上
タッピンねじ
5
30以上
6280以上
Kーブリッド（落下防止用）

認定番号：PS060WL-0031

C　ケーブルラック壁貫通部（中空壁）

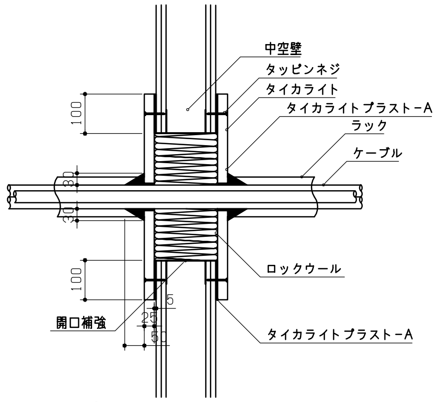
中空壁
タッピンネジ
タイカライト
タイカライトプラストーA
ラック
ケーブル
100
30
30
100
ロックウール
開口補強
5
25
50
タイカライトプラストーA

認定番号：PS060WL-9273

D　バスダクト床貫通部

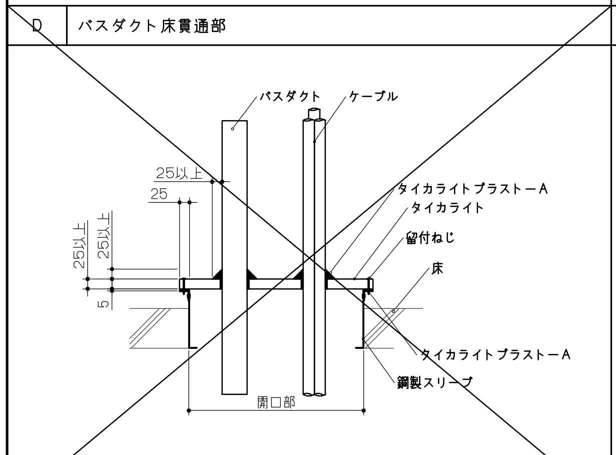
バスダクト
ケーブル
25以上
25
25以上
25以上
5
タイカライトプラストーA
タイカライト
留付ねじ
床
タイカライトプラストーA
鋼製スリーブ
開口部

認定番号：PS060FL-0365

E　バスダクト壁貫通部（コンクリート・中空壁）

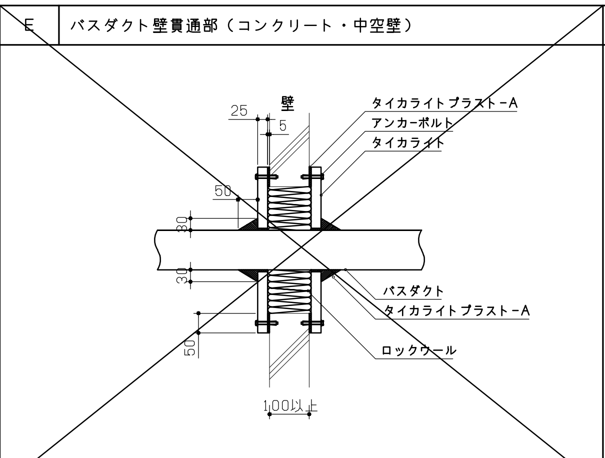
壁
25
5
タイカライトプラストーA
アンカーボルト
タイカライト
50
30
30
50
バスダクト
タイカライトプラストーA
ロックウール
100以上

認定番号：PS060WL-9270

F　ケーブル・電線管壁貫通（コンクリート）

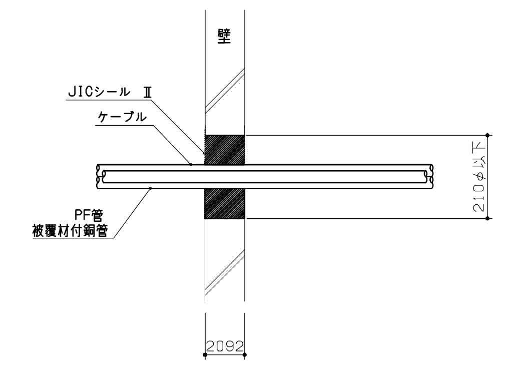
壁
JICシール Ⅱ
ケーブル
PF管
被覆材付鋼管
210φ以下
2092

認定番号：PS060WL-0395

G　ケーブル・電線管床貫通（コンクリート）

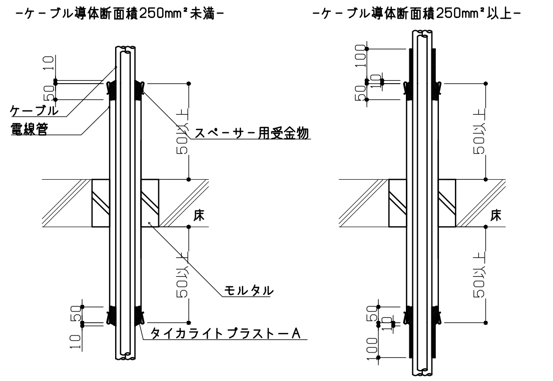
-ケーブル導体断面積250mm²未満-
-ケーブル導体断面積250mm²以上-
10
50
ケーブル
電線管
スペーサー用受金物
50以上
床
50以上
モルタル
50
10
タイカライトプラストーA
100
10
50
50以上
50以上
50
10
100

認定番号：PS060FL-9292

H　ケーブル・電線管壁貫通（中空壁）

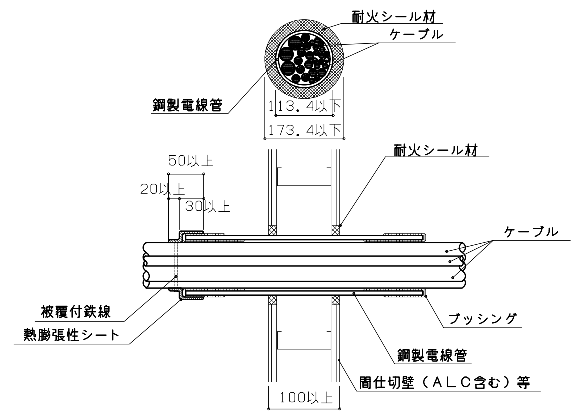
耐火シール材
ケーブル
鋼製電線管
113.4以下
173.4以下
耐火シール材
50以上
20以上
30以上
ケーブル
被覆付鉄線
熱膨張性シート
ブッシング
鋼製電線管
間仕切壁（ALC含む）等
100以上

認定番号：PS060WL-0269

I　PF管壁貫通（中空壁）

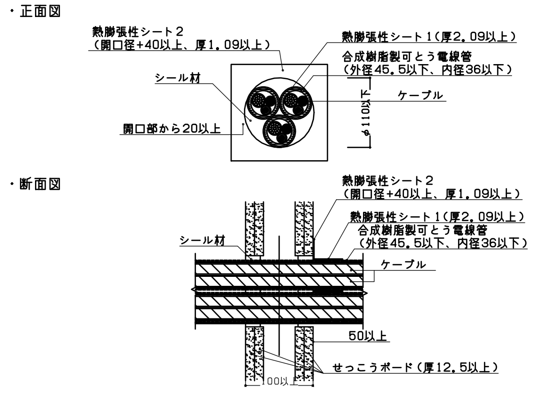
・正面図
熱膨張性シート2
（開口径+40以上、厚1.09以上）
熱膨張性シート1（厚2.09以上）
合成樹脂製可とう電線管
（外径45.5以下、内径36以下）
シール材
ケーブル
φ110以下
開口部から20以上
・断面図
熱膨張性シート2
（開口径+40以上、厚1.09以上）
熱膨張性シート1（厚2.09以上）
合成樹脂製可とう電線管
（外径45.5以下、内径36以下）
シール材
ケーブル
50以上
せっこうボード（厚12.5以上）
100以上

認定番号：PS060WL-0213

J　PF管壁貫通（片面ボード張）

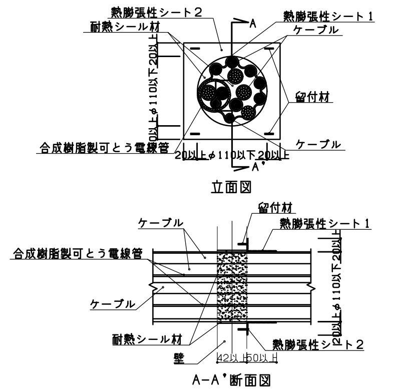
熱膨張性シート2
耐熱シール材
熱膨張性シート1
ケーブル
A
留付材
ケーブル
20以上φ110以下20以上
合成樹脂製可とう電線管
20以上φ110以下20以上
A'
立面図
留付材
熱膨張性シート1
ケーブル
合成樹脂製可とう電線管
ケーブル
20以上φ110以下20以上
耐熱シール材
壁
42以上
50以上
熱膨張性シート2
A-A'断面図

認定番号：PS060WL-0358

K　アウトレットボックス取付部（中空壁）

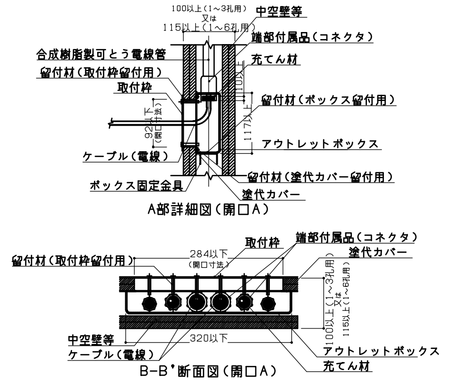
100以上（1～3孔用）
又は
115以上（1～6孔用）
中空壁等
端部付属品（コネクタ）
合成樹脂製可とう電線管
充てん材
留付材（取付枠留付用）
取付枠
10以上
留付材（ボックス留付用）
92以下（開口寸法）
117以上
アウトレットボックス
ケーブル（電線）
留付材（塗代カバー留付用）
ボックス固定金具
塗代カバー
A部詳細図（開口A）
取付枠
端部付属品（コネクタ）
塗代カバー
留付材（取付枠留付用）
284以下（開口寸法）
100以上（1～3孔用）
又は
115以上（1～6孔用）
中空壁等
320以下
ケーブル（電線）
アウトレットボックス
充てん材
B-B'断面図（開口A）

認定番号：PS060WL-0452

L　アウトレットボックス取付部（片面ボード張）

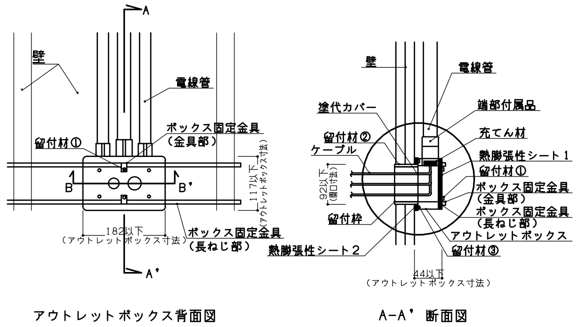
A
壁
電線管
ボックス固定金具
（金具部）
留付材①
B
B'
117以下
（アウトレットボックス寸法）
182以下
（アウトレットボックス寸法）
ボックス固定金具
（長ねじ部）
A'
アウトレットボックス背面図
壁
電線管
塗代カバー
端部付属品
充てん材
留付材②
ケーブル
熱膨張性シート1
留付材①
92以下
（開口寸法）
ボックス固定金具
（金具部）
ボックス固定金具
（長ねじ部）
留付枠
アウトレットボックス
熱膨張性シート2
留付材③
44以下
（アウトレットボックス寸法）
A-A' 断面図

認定番号：PS060WL-0532

M　OAフロア内壁貫通部

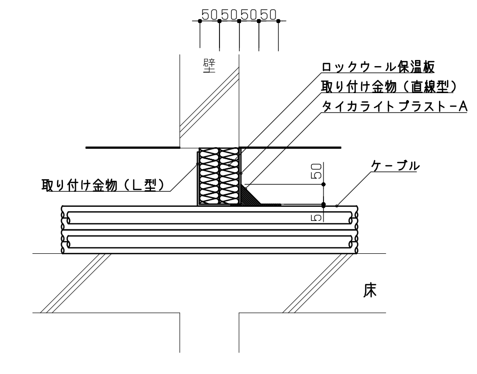
50 50 50 50
壁
ロックウール保温板
取り付け金物（直線型）
タイカライトプラストーA
取り付け金物（L型）
50
ケーブル
5
床

認定番号：PS060WL-9283

在来工法

a　電線管壁・床貫通部（コンクリート）

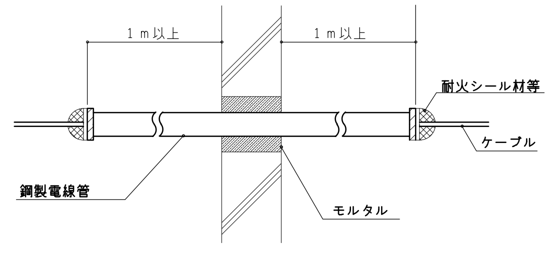
1m以上
1m以上
耐火シール材等
ケーブル
鋼製電線管
モルタル

鋼製電線管を用いた防火区画貫通部措置
（コンクリート（ALC含む）壁・床）

b　電線管壁貫通部（中空壁）

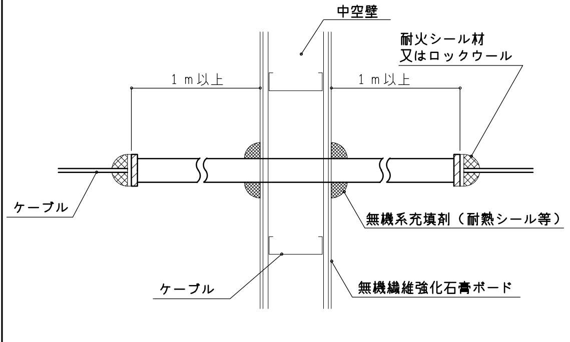
中空壁
耐火シール材
又はロックウール
1m以上
1m以上
ケーブル
無機系充填剤（耐熱シール等）
ケーブル
無機繊維強化石膏ボード

鋼製電線管を用いた防火区画貫通部措置
（中空壁）

c　電線管壁・床貫通部：プルボックス止

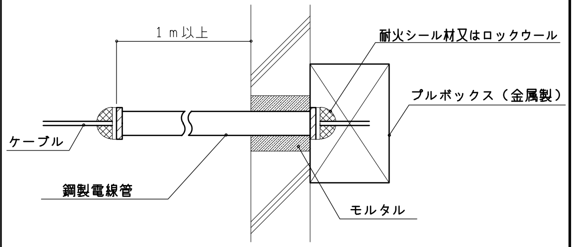
1m以上
耐火シール材又はロックウール
プルボックス（金属製）
ケーブル
鋼製電線管
モルタル

鋼製電線管を用いた防火区画貫通部措置
（コンクリート壁・床　片側プルボックス取付）

d　合成樹脂可とう管コンクリート打込部

① スラブ打ち込みの場合

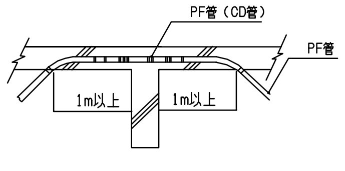
PF管（CD管）
PF管
1m以上
1m以上

J241226A26030317_防火区画貫通処理要領図

着工	. .	. .	
竣工	. .	. .	
監理		. . . .	
施工		. .	

惠本　涼太郎　一級建築士
澤村　晋次　　意見を聴いた建築設備士

日建設計

2026・03・27　　検図者：横井 繁明

椙山女学園/星が丘キャンパス
大学会館食堂リニューアル工事

防火区画貫通処理要領図

㊄ 電 －17

No. J－ 241226 － A