椙山女学園/星が丘キャンパス
大学会館食堂リニューアル工事

東側・西側窓際カウンター下地

打合図

2026 年 11 月02 日

出図・訂正記事

	年	月	日	備考	
⓪	2026	11	02	初図	
①					
②					

質疑・回 答☁ 表示（図中雲マーク）

年	月	日	質疑事項	年	月	日	回答

仕上材質

下地:錆止めマデ

取付予定日	製作日数	受領希望日	受領日	取極No.
年 月 日	日	年 月 日	年 月 日	No.

三友建材株式会社

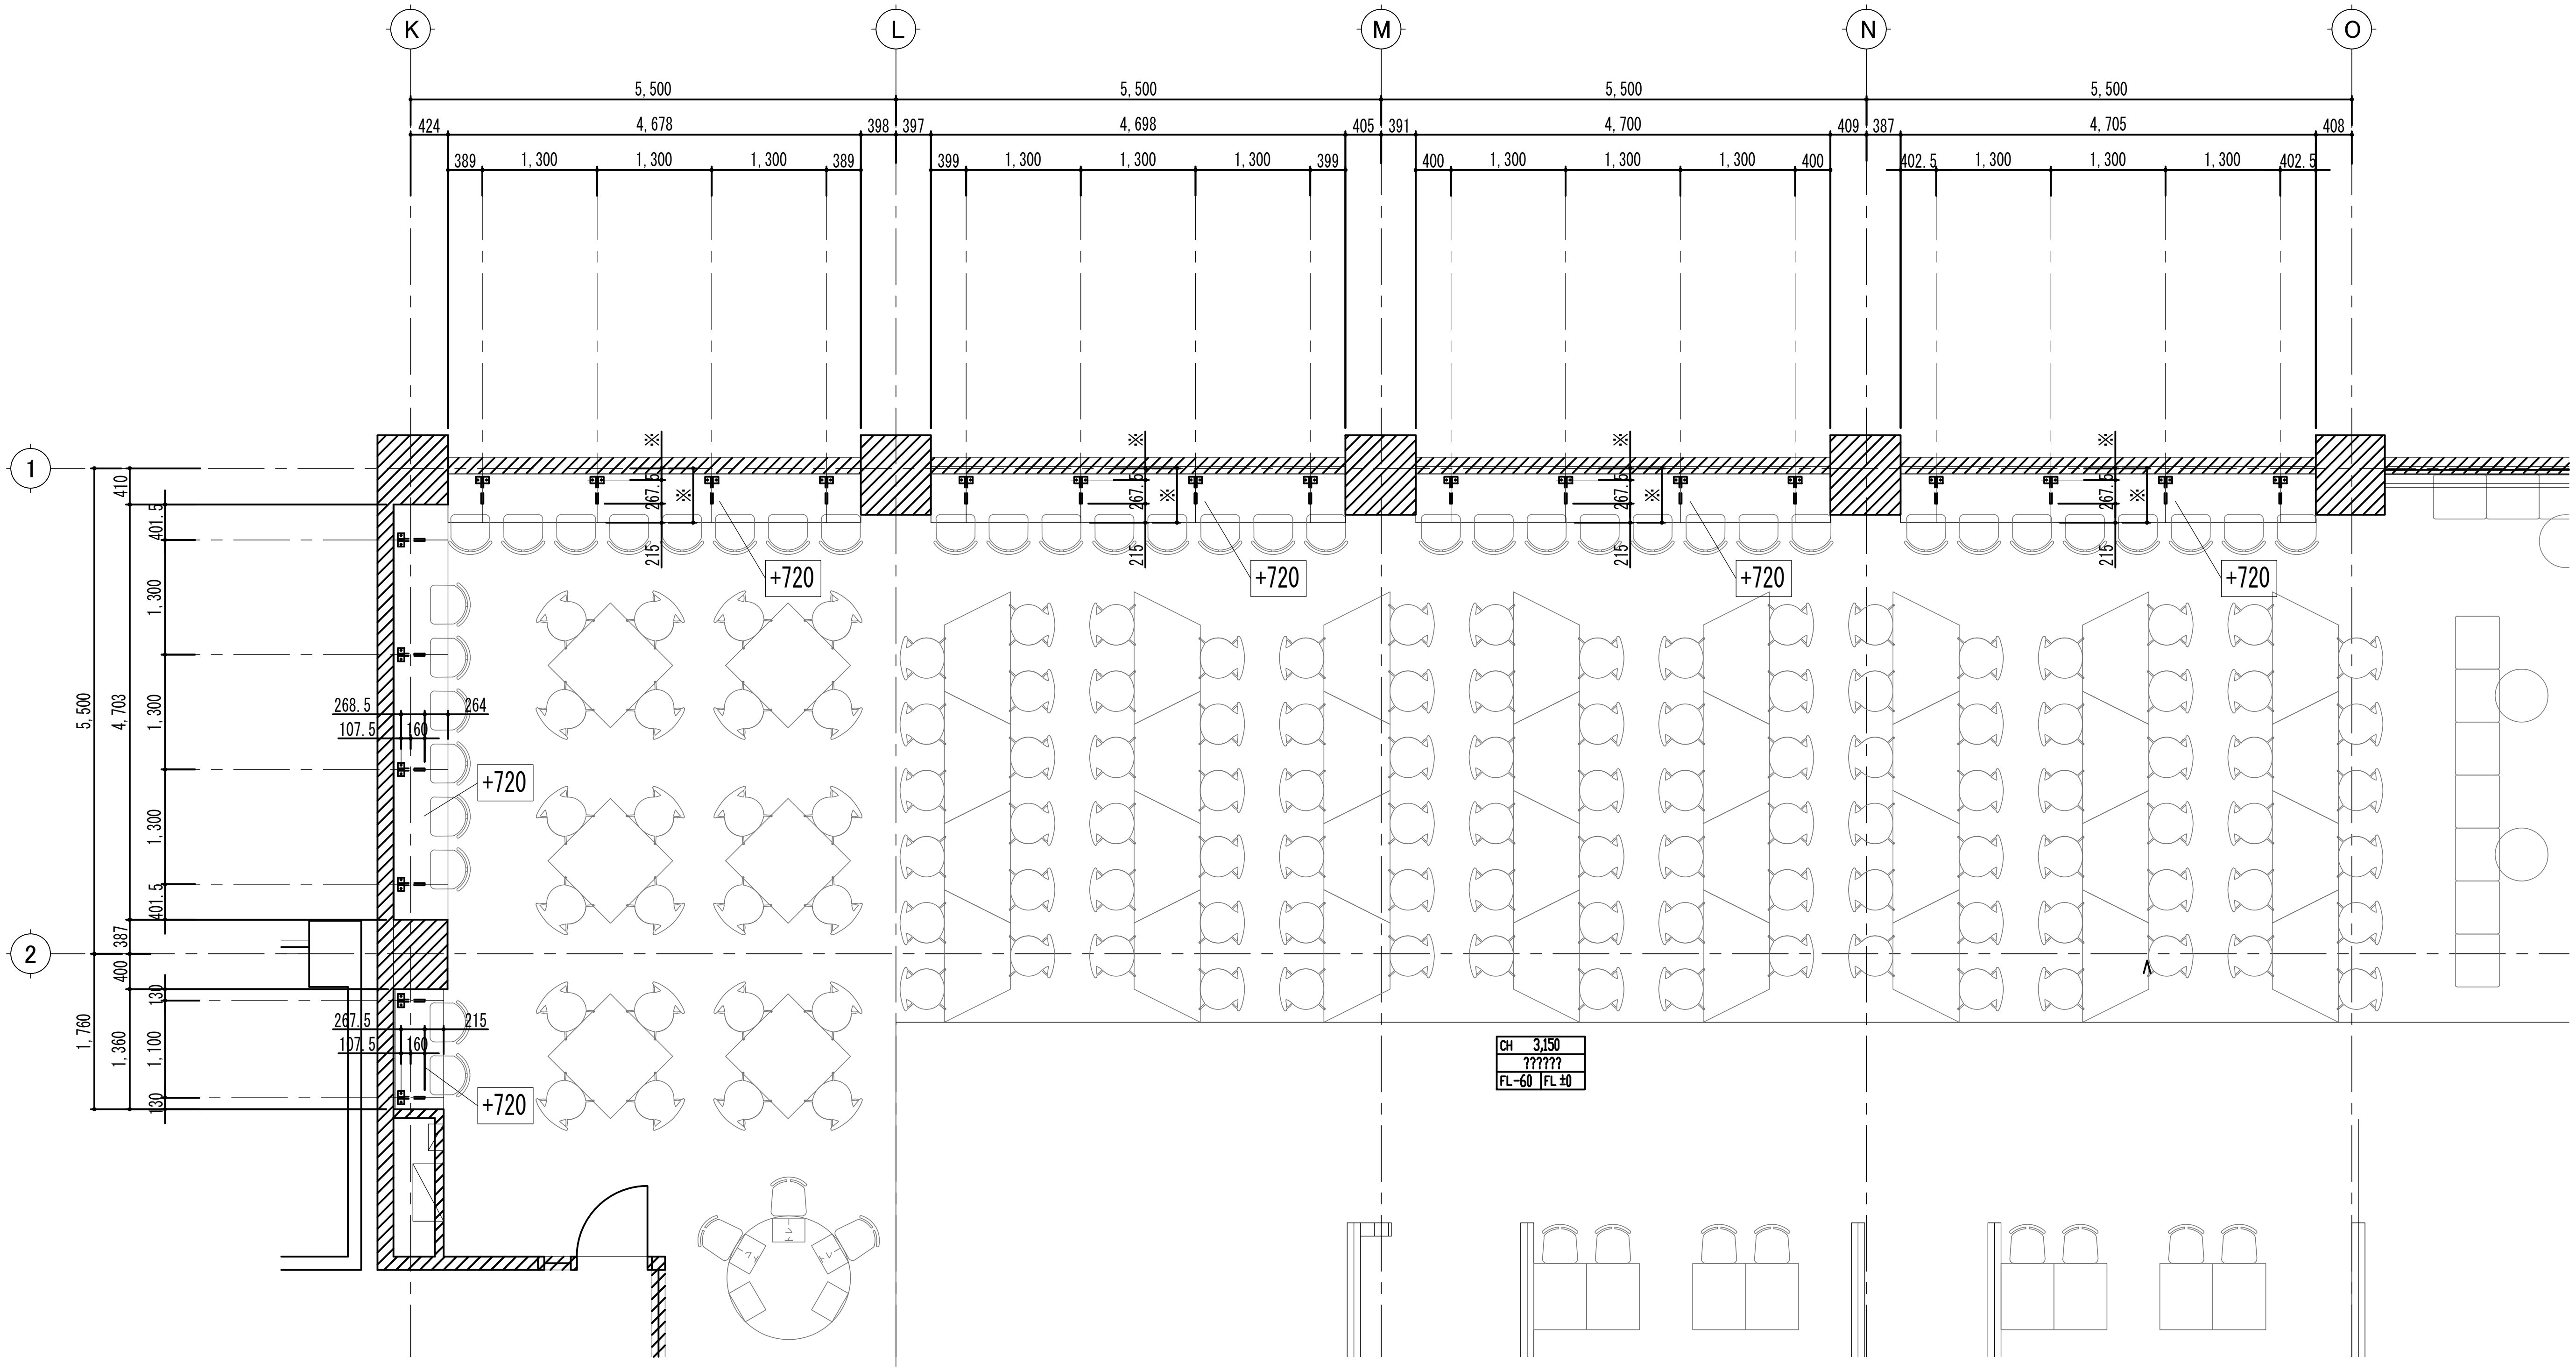

西側 窓際カウンター下地平面図1/40

参照資料名	仕上材質
	下地:錆止めマデ

三友建材株式会社

年	月	日	No.	修正内容	修正者	年	月	日	No.	修正内容	修正者
			⑩						⑤		
			⑨						④		
			⑧						③		
			⑦						②		
			⑥						①		

取極NO.

縮尺（A1用紙） S=1/40

初図日 2026 年 11 月 02 日

現場名	椙山女学園/星が丘キャンパス 大学会館食堂リニューアル工事
内容	東側・西側窓際カウンター下地 NO. 01

部長	課長	主任	製図者	現場担当	打合図 受領図
			トゥアン	榊原	2026 年 11 月 02 日

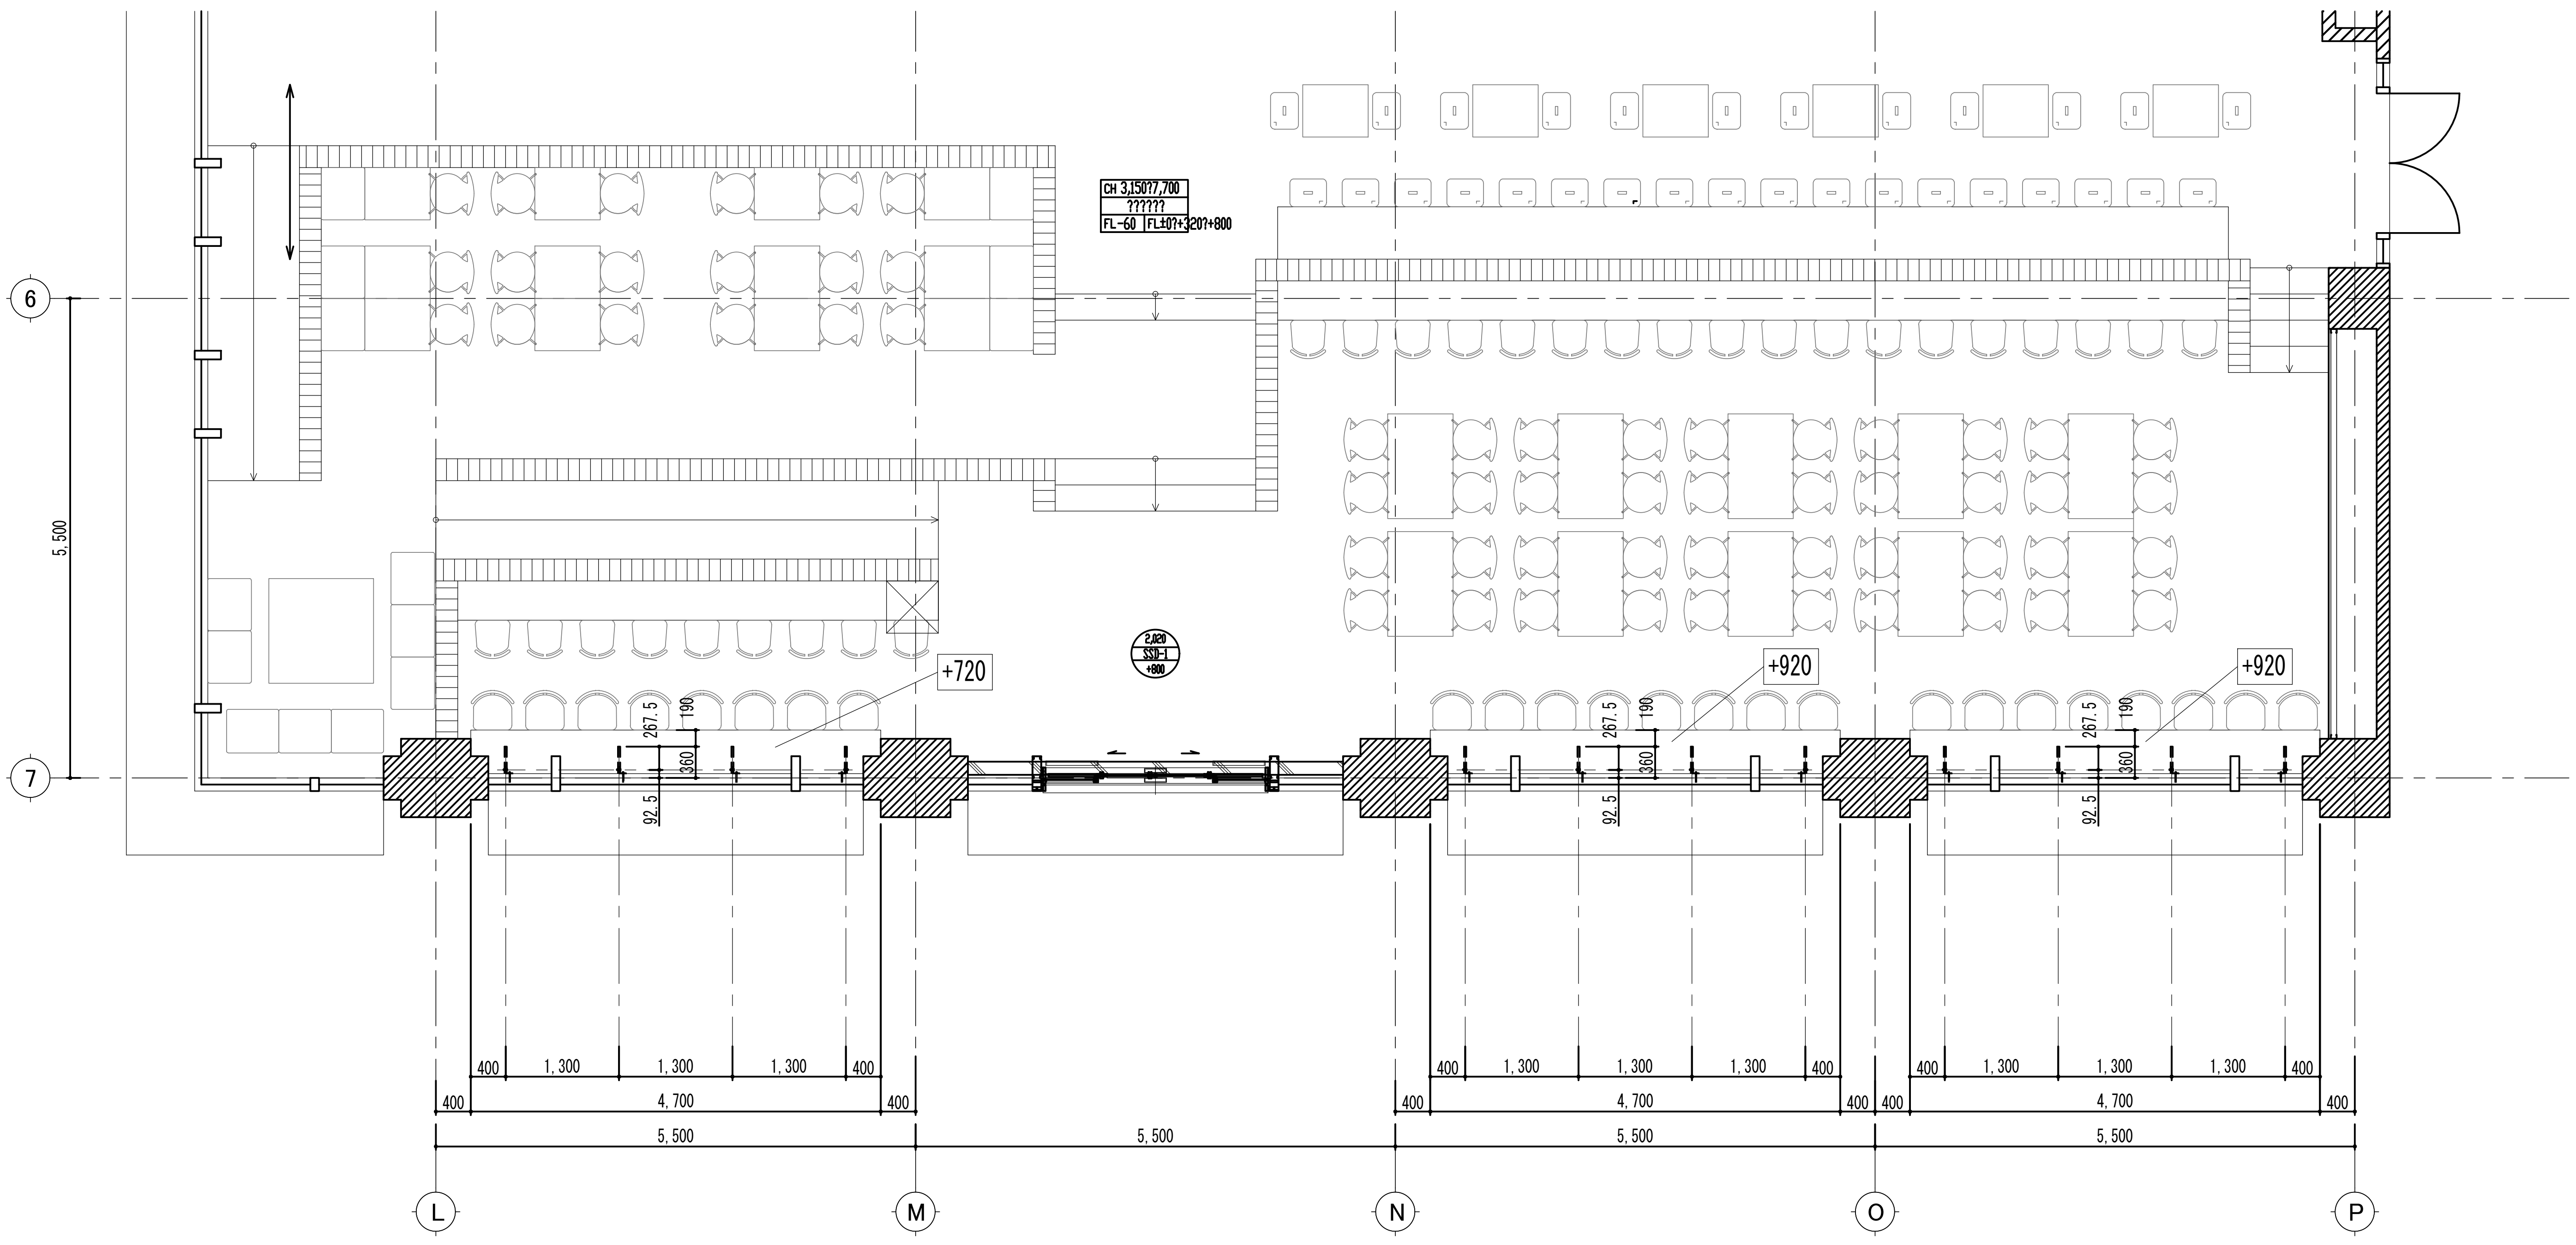

東側 窓際カウンター下地平面図1/40

参照資料名	仕上材質	
	下地:錆止めマデ	三友建材株式会社

年	月	日	No.	修 正 内 容	修正者	年	月	日	No.	修 正 内 容	修正者
			⑩						⑤		
			⑨						④		
			⑧						③		
			⑦						②		
			⑥						①		

取極NO.

縮尺（A1用紙） S=1/40

初図日 2026 年 11 月 02 日

現 場 名	相山女学園/星が丘キャンパス 大学会館食堂リニューアル工事
内 容	東側・西側窓際カウンター下地 NO. 02

部長	課長	主任	製図者	現場担当	
			トゥアン	榊原	打 合 図 受 領 図 2026 年 11 月 02 日

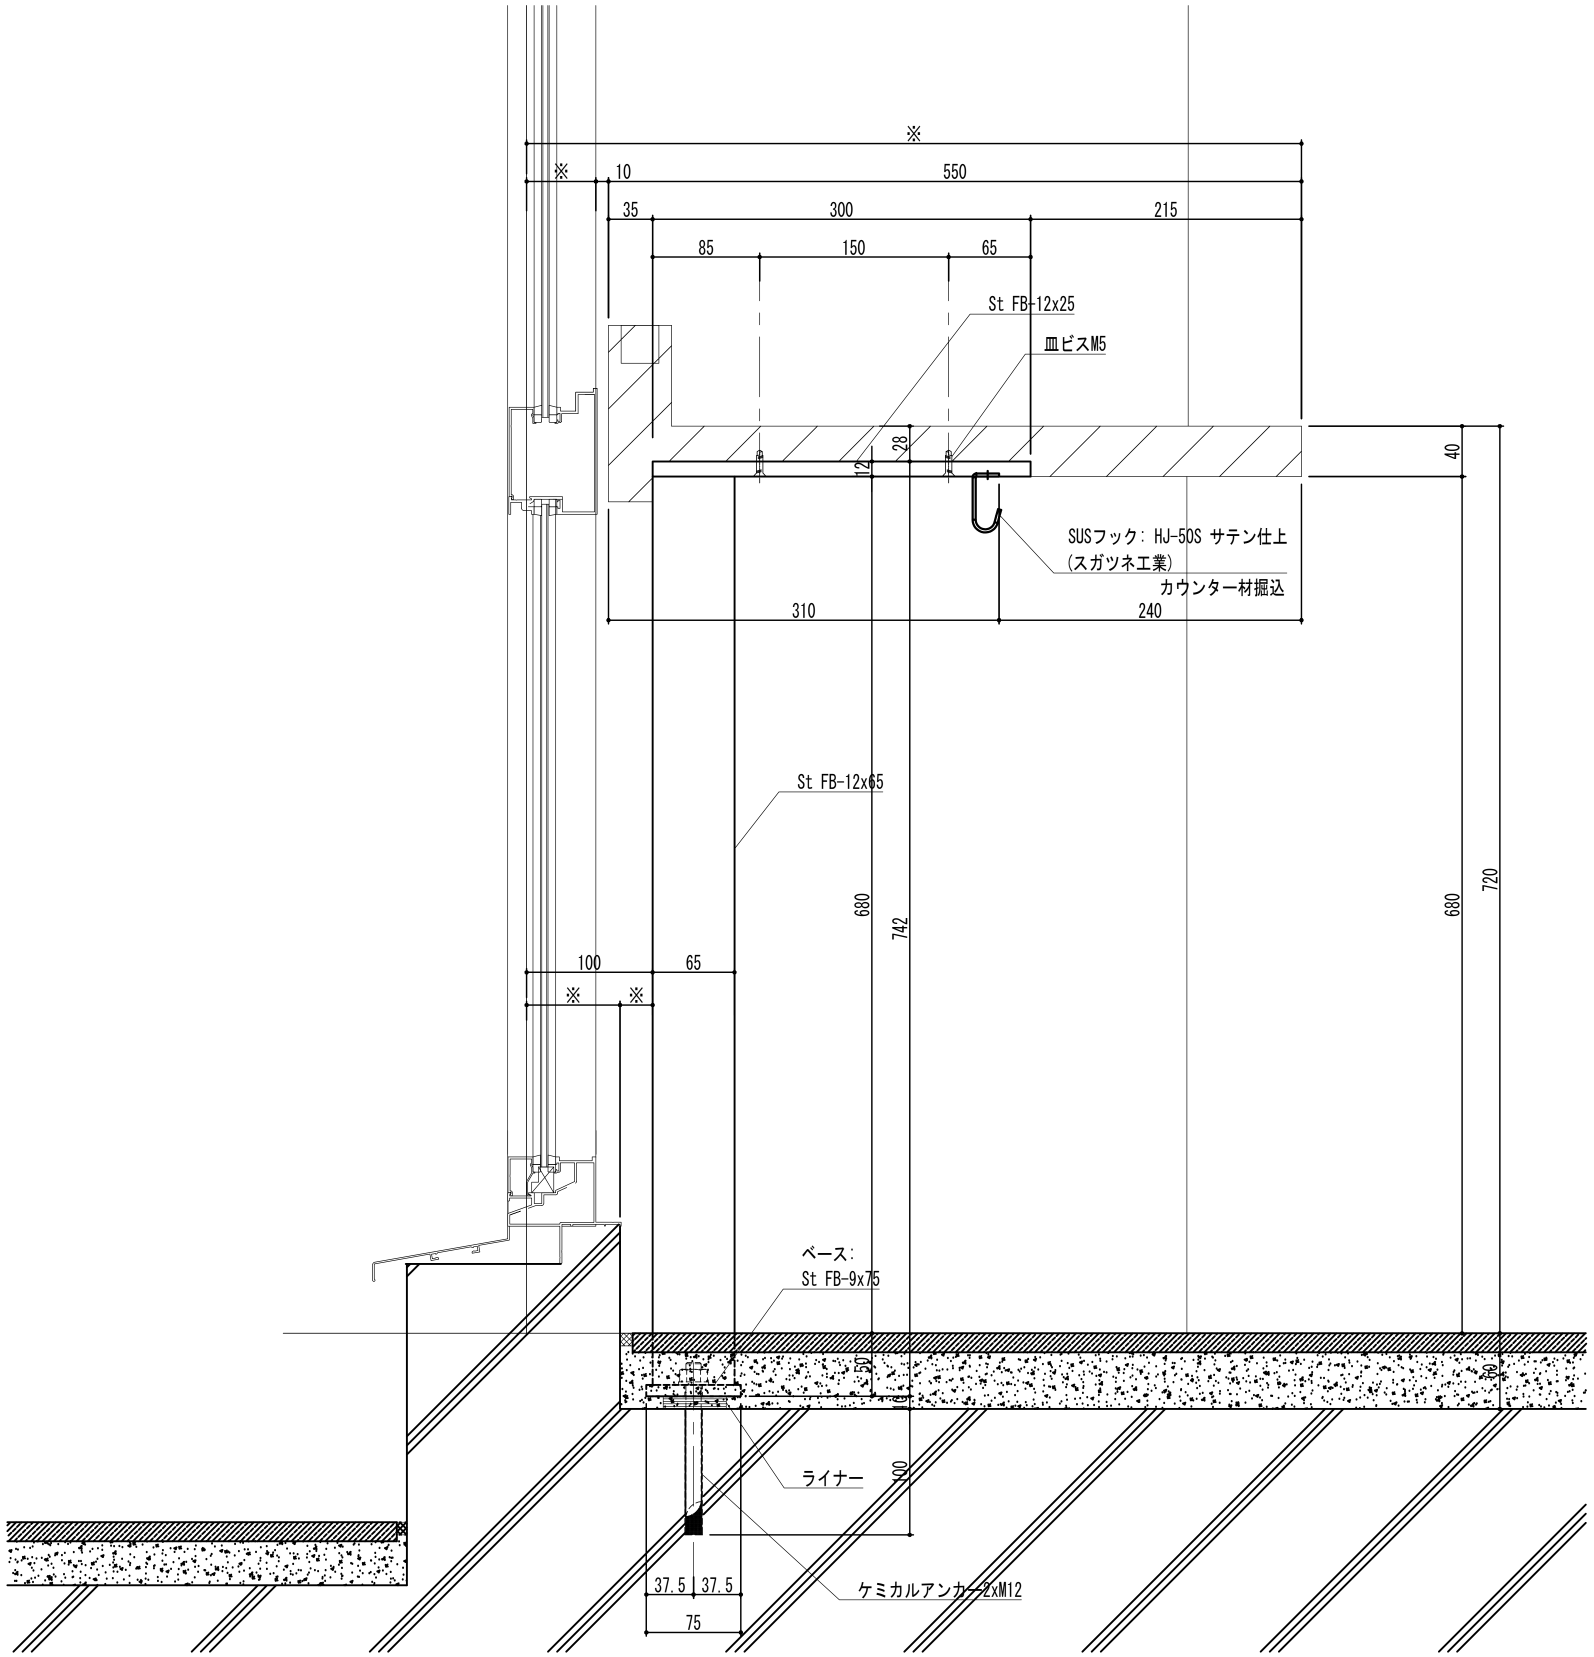

西側 窓際カウンター下地 断面図1/3

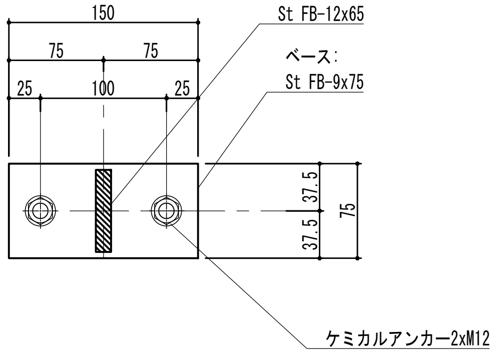

足元 断面図1/3

参照資料名	仕上材質						
	下地：錆止めマデ	三友建材株式会社					

年	月	日	No.	修　正　内　容	修正者	年	月	日	No.	修　正　内　容	修正者
			⑩						⑤		
			⑨						④		
			⑧						③		
			⑦						②		
			⑥						①		

取極NO.

縮尺（A1用紙）　S=1/3

初図日　2026 年 11 月 02 日

現場名	相山女学園/星が丘キャンパス 大学会館食堂リニューアル工事
内容	東側・西側窓際カウンター下地　NO. 03

部長	課長	主任	製図者	現場担当	打合図 受領図
			トゥアン	榊原	2026 年 11 月 02日

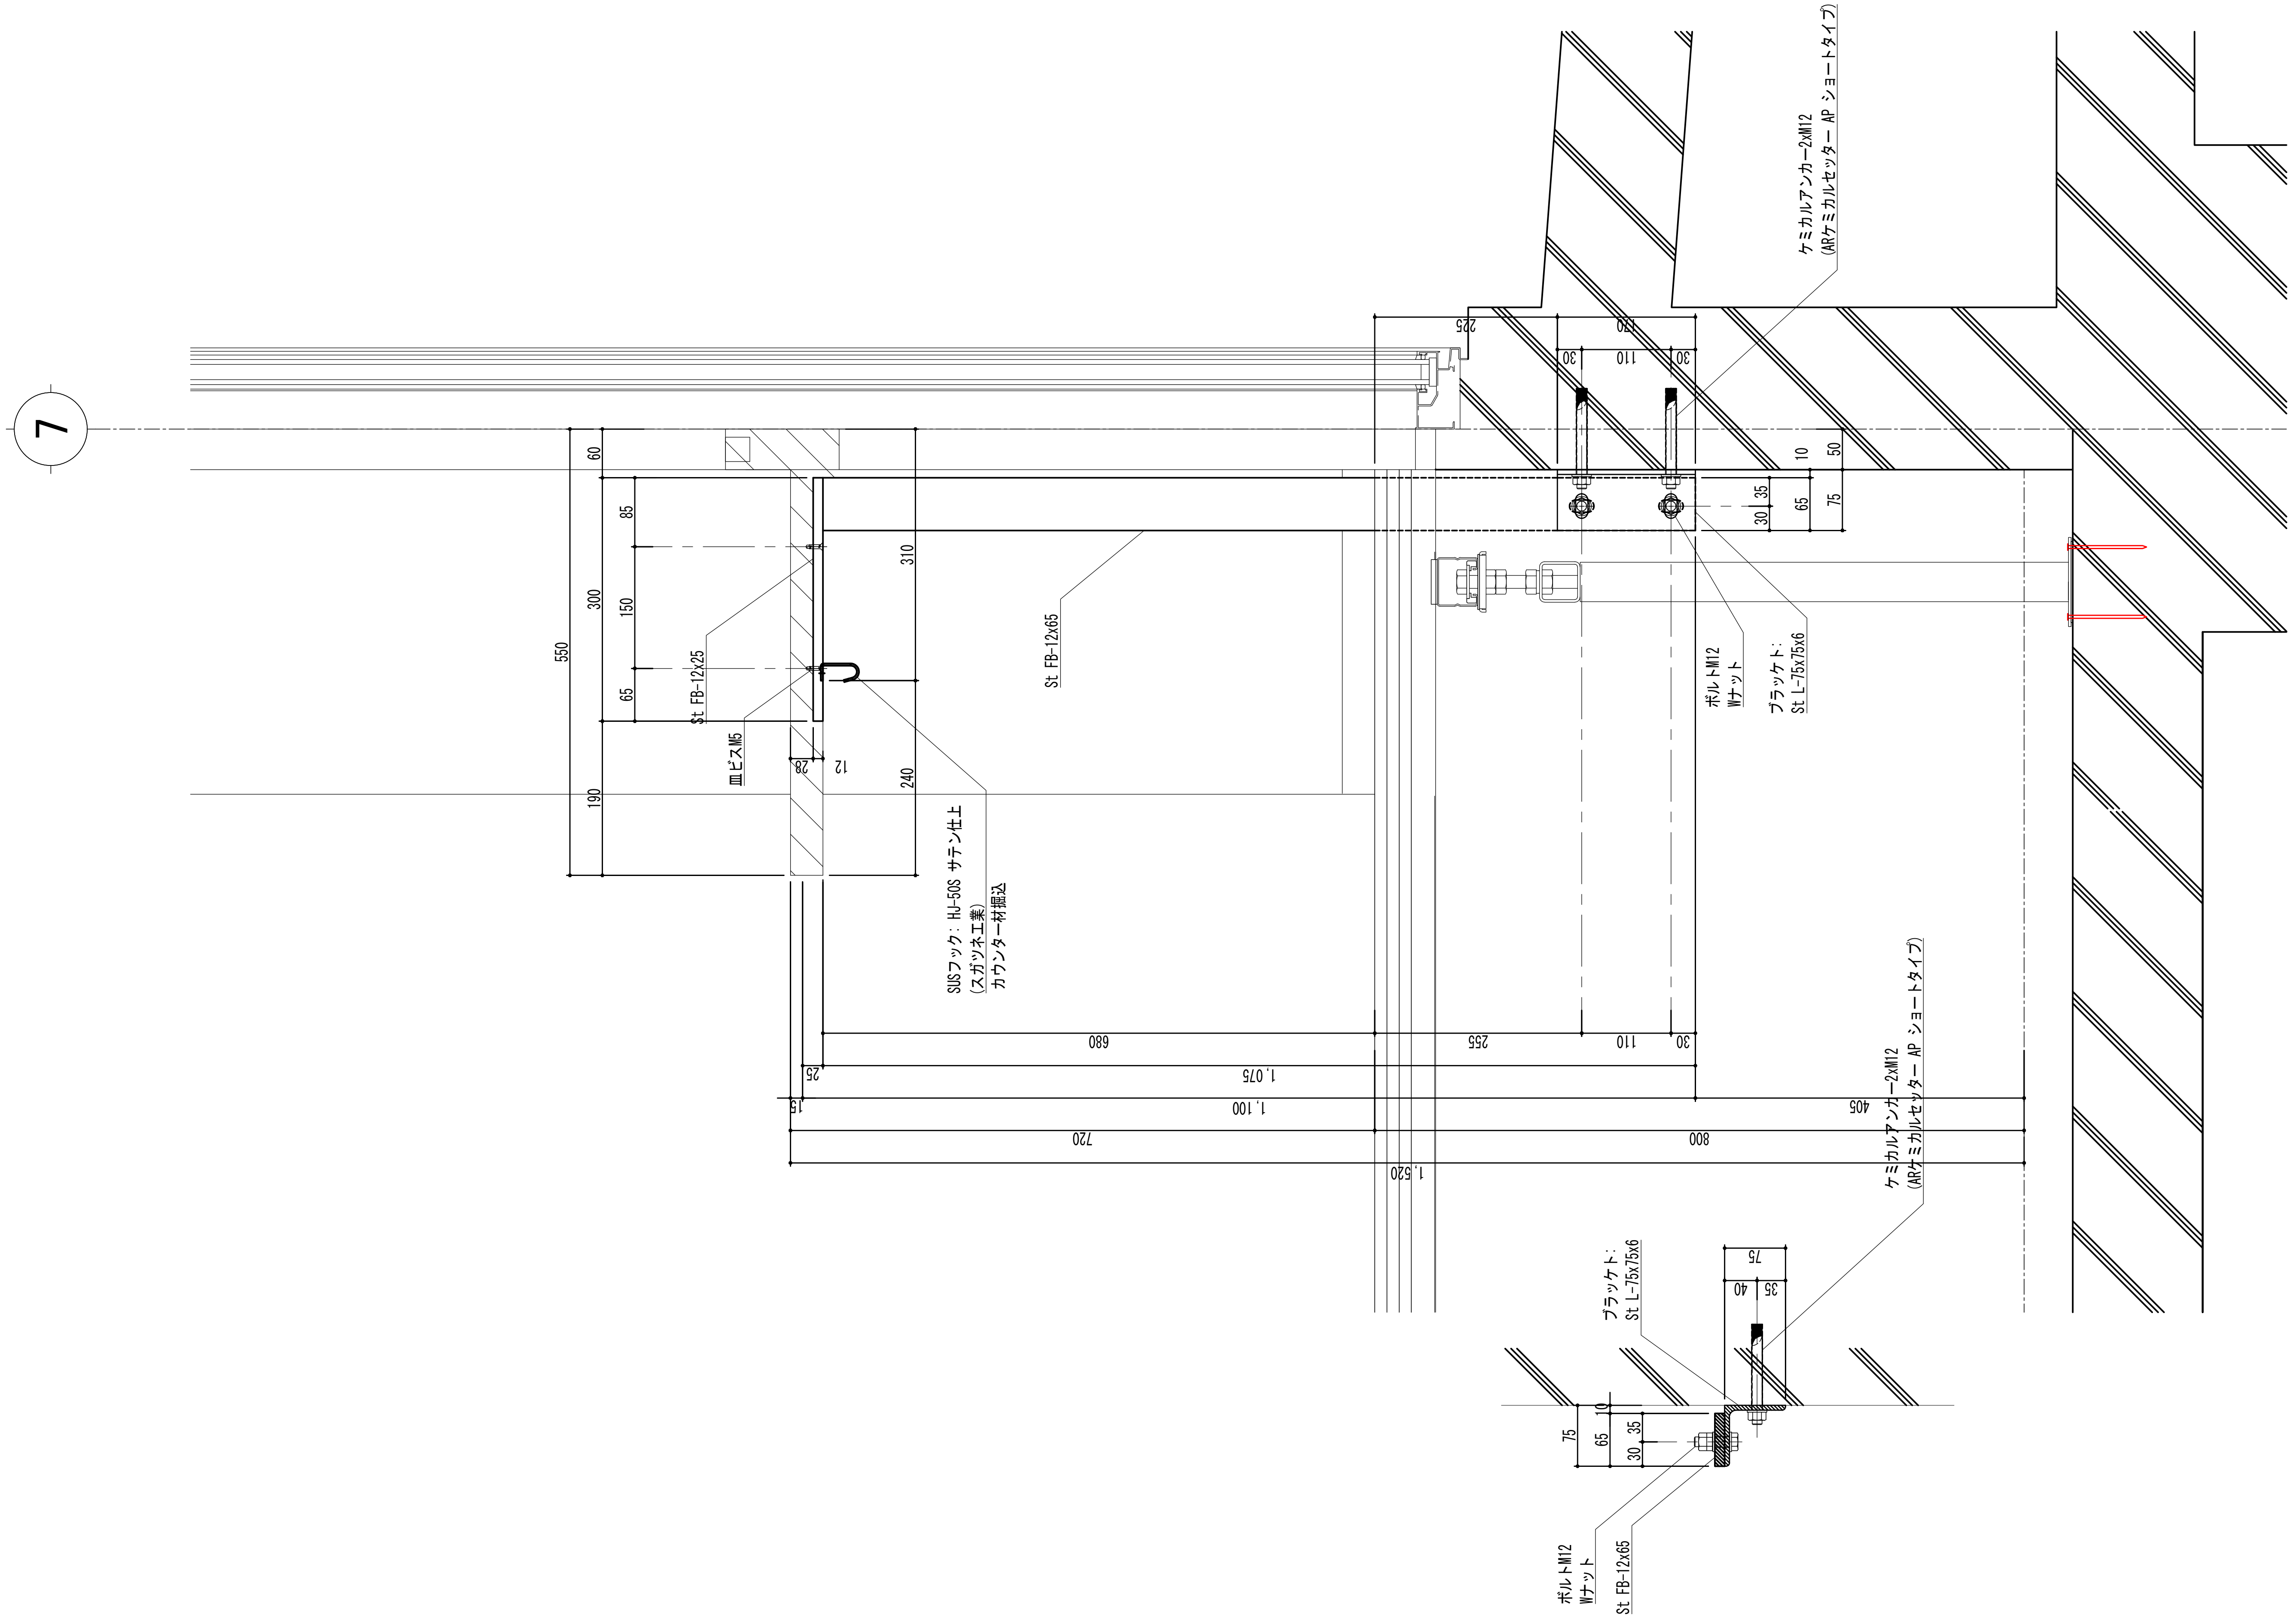

東側 窓際カウンター下地 断面図1/4

参照資料名

仕上材質

下地:錆止めマデ

三友建材株式会社

年	月	日	No.	修正内容	修正者	年	月	日	No.	修正内容	修正者
			⑩						⑤		
			⑨						④		
			⑧						③		
			⑦						②		
			⑥						①		

取極NO.

縮尺（A1用紙） S=1/4

初図日 2026年11月02日

現場名	相山女学園/星が丘キャンパス 大学会館食堂リニューアル工事
内容	東側・西側窓際カウンター下地 NO. 04

部長	課長	主任	製図者	現場担当
			トゥアン	榊原

打合図

受領図

2026年11月02日

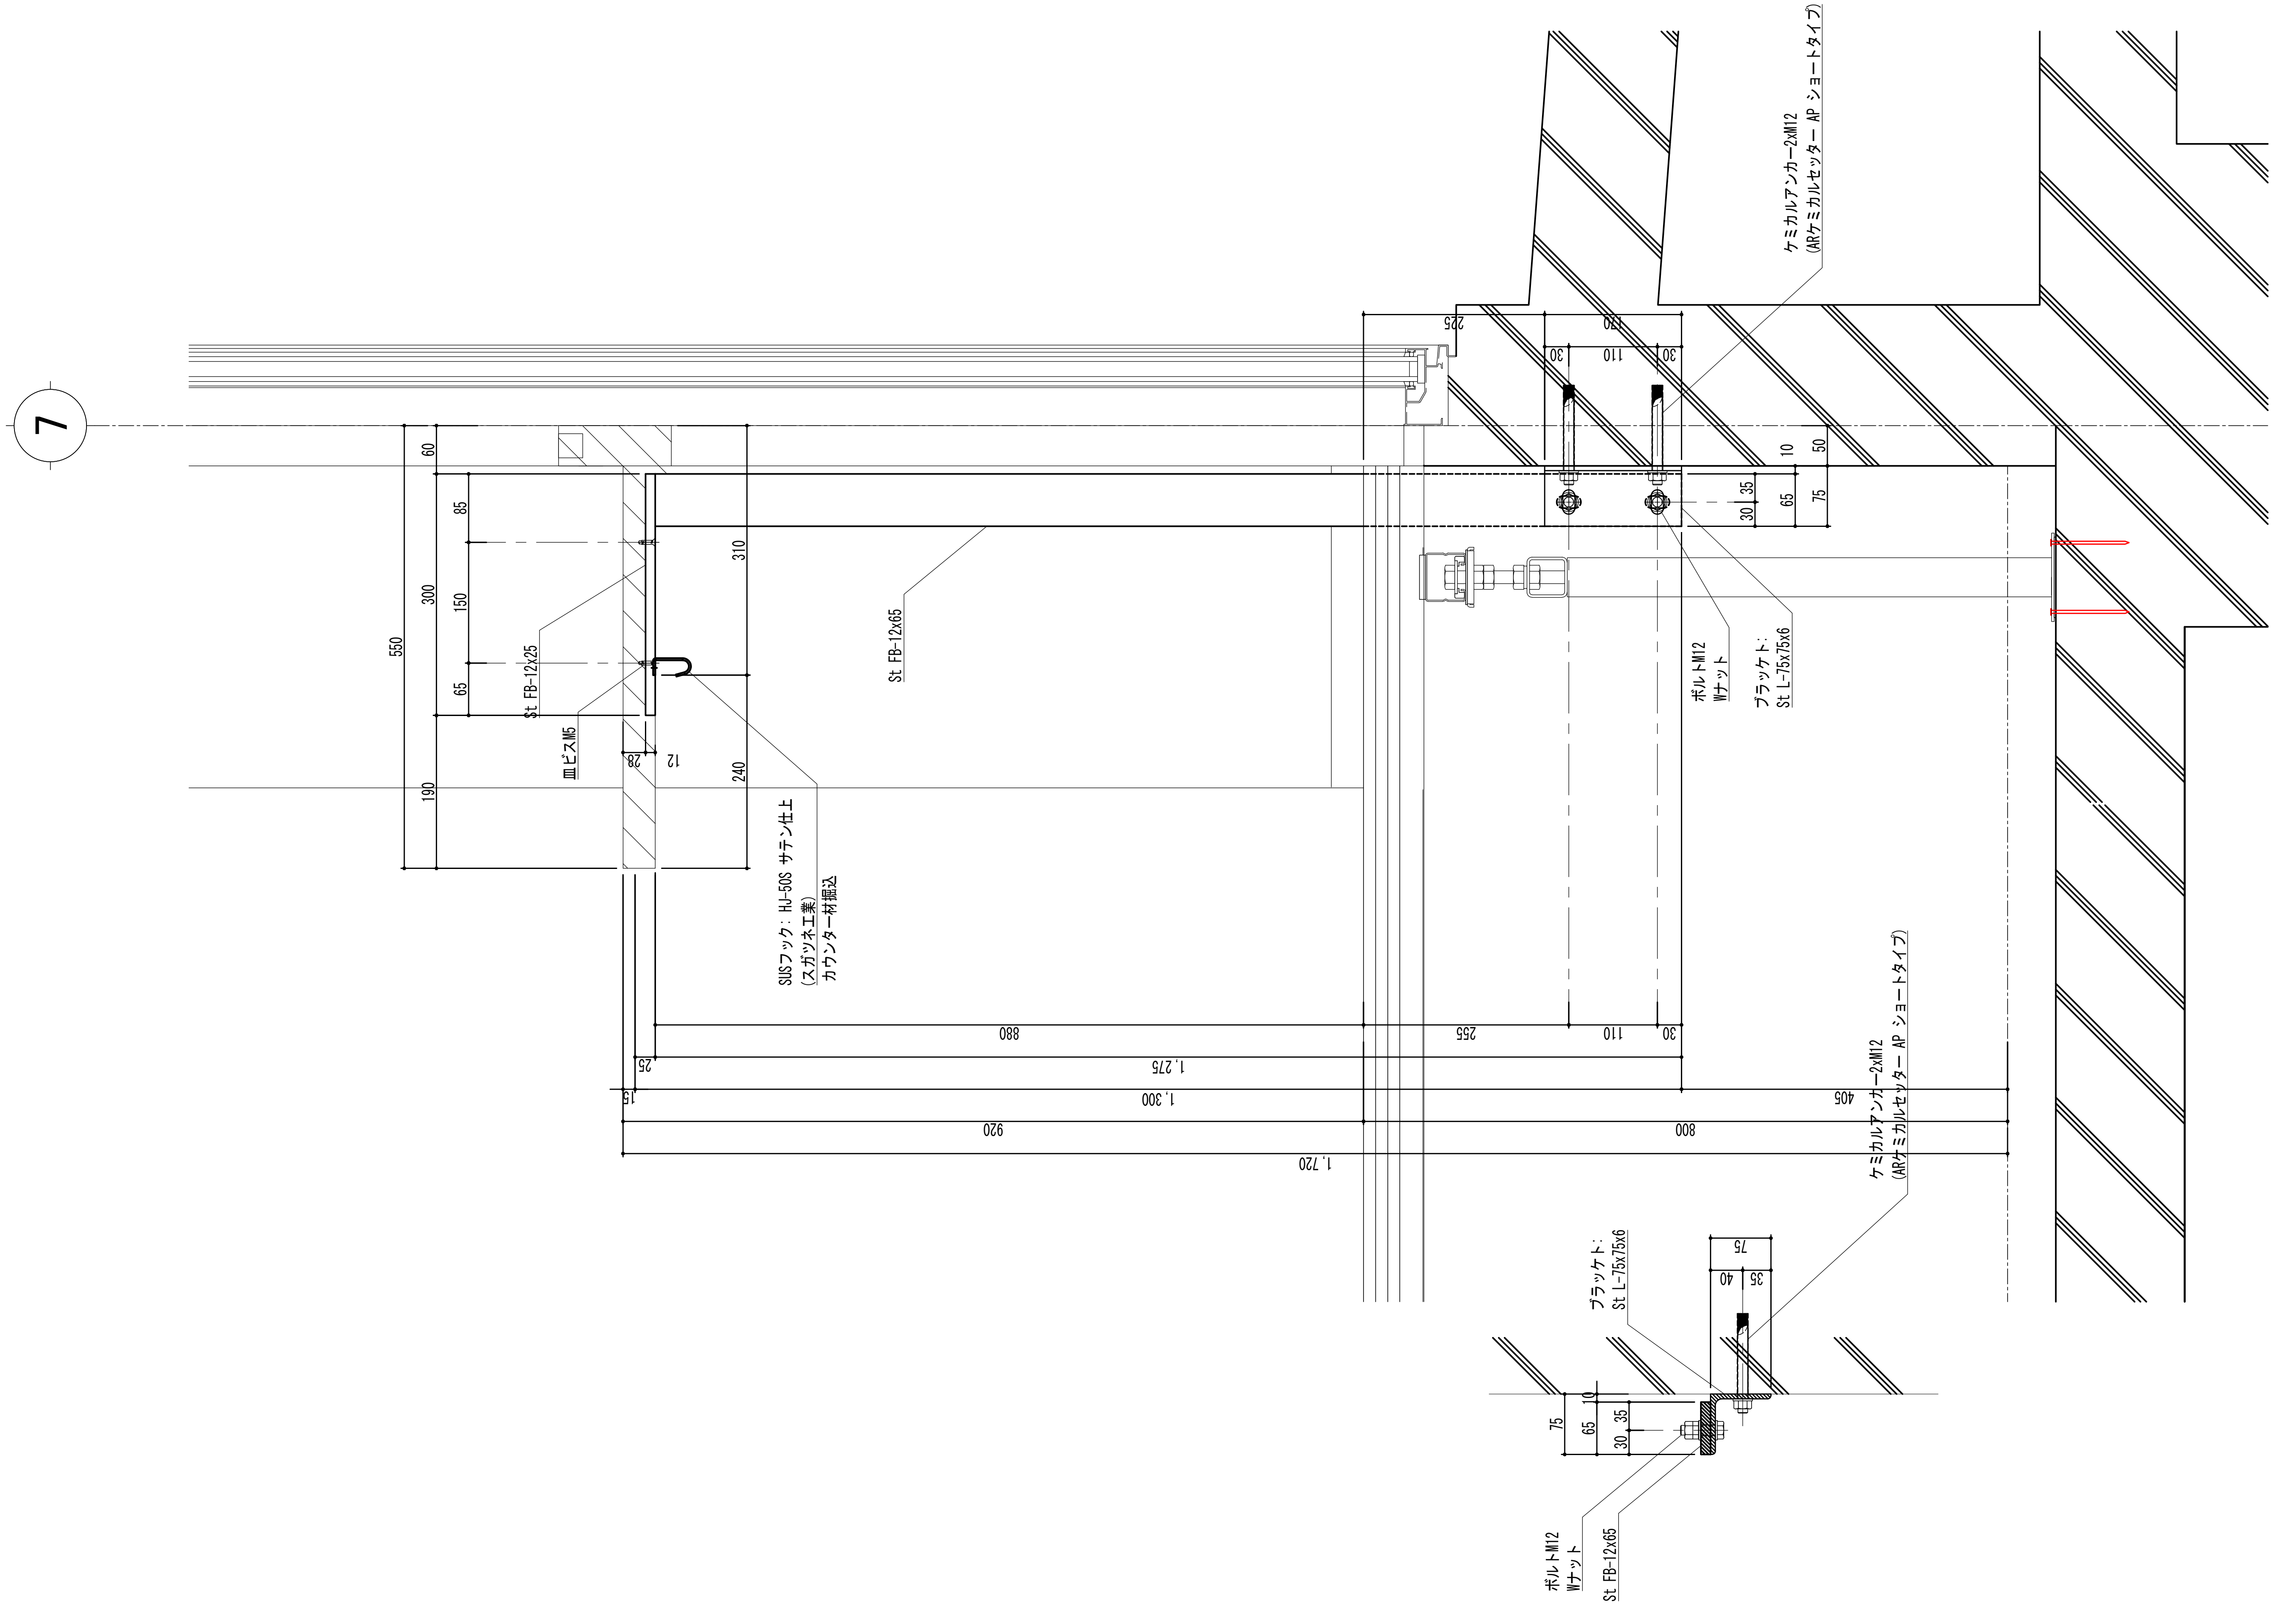

東側 窓際カウンター下地 断面図1/4

参照資料名	仕上材質
	下地:錆止めマデ

三友建材株式会社

年	月	日	No.	修 正 内 容	修正者	年	月	日	No.	修 正 内 容	修正者
			⑩						⑤		
			⑨						④		
			⑧						③		
			⑦						②		
			⑥						①		

取極NO.	
縮尺（A1用紙）	S=1/4
初図日	2026 年 11 月 02 日

現 場 名	椙山女学園/星が丘キャンパス 大学会館食堂リニューアル工事
内 容	東側・西側窓際カウンター下地 NO. 05

部長	課長	主任	製図者	現場担当	打 合 図 受 領 図
			トゥアン	榊原	2026 年 11 月 02 日